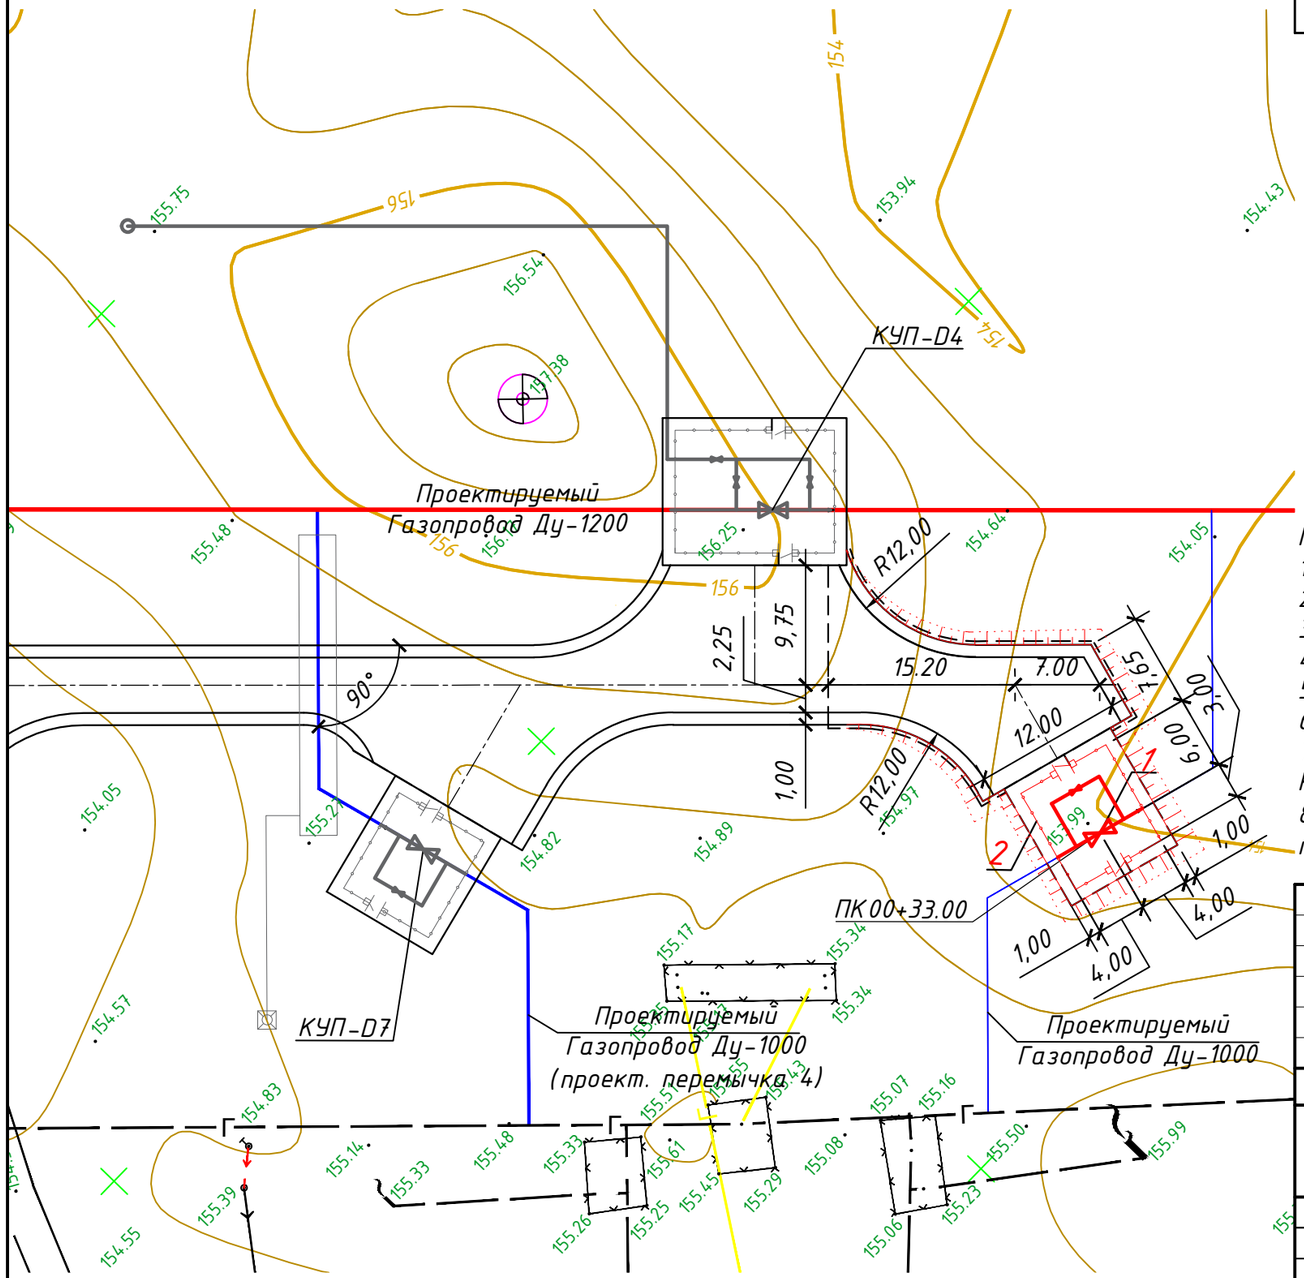


Экспликация зданий и сооружений

Номер на плане	Наименование	Примечание
1	Крановый узел Ду 1000	
2	Ограждение сетчатое	

Условные обозначения

- Ограждение
- Калитка
- Граница планировки
- Существующий газопровод
- Проектируемый газопровод ДУ-1200
- Проектируемый газопровод ДУ-1000
- Откосы насыпи
- Откосы выемки

Примечания:

При составлении настоящего чертежа были использованы :

1. Материалы топографо-геодезической съемки, предоставлены АО "O'ZLITINEFTGAZ".
2. Система координат местная. Высотные отметки даны в Балтийской системе.
3. Размеры даны в метрах.
4. Площадка кранового узла КУП-D8 привязана линейно к пикету ПК 00+33.00.
5. Данный лист смотри совместно с листами разделов PIL, PRE, ELE, STR, SYS.
6. Детальный план кранового узла см. EWE0426-MGL1-PRE-054-DRW-760203.
7. Разбивочный план кранового узла КУП-D4 см. EWE0426-MGL1-GLT-054-DRW-730102 и КУП-D7 см. EWE0426-MGL1-GLT-054-DRW-760102.
8. Защита Пересечения проектной дороги с проектной перемычкой 4 (КУП-D7) предусмотрена в техническом решении №1 в рамках авторского надзора.

Рев.	Дата	Назначение ревизии	Проверил	Утвердил
A2	07.10.2026	Выпущено для строительства		
A1	09.09.2026	Выпущено для строительства		
R1	29.07.2026	Выпущено для рассмотрения		

ЗАКАЗЧИК: UTG UZTRANSGAZ

ГЕНЕРАЛЬНЫЙ ПОДРЯДЧИК: UET UZBEKENERGOTAMIR

ПОДРЯДЧИК: PBG Pro Build Generation

ГЕНЕРАЛЬНЫЙ ПРОЕКТИРОВЩИК: EAST WEST ENGINEERING

Изм.	Кол.уч.	Лист	№ док.	Подпись	Дата	EWE0426-MGL1-GLT-054-DRW-770102-A2			
						«СТРОИТЕЛЬСТВО НОВЫХ НИТОК (УЧАСТКОВ) ГАЗОПРОВОДОВ «ГАЗЛИ - САРИМОЙ» И «АКЧАЛОК - ГАЗЛИ - НУКУС» ОБЩЕЙ ПРОТЯЖЕННОСТЬЮ НЕ МЕНЕЕ 275 км».			
ГИП		Кирпичников С.			10.2026	ГАЗОПРОВОД «ГАЗЛИ-САРИМОЙ» (54 км)	Стадия	Лист	Листов
Нач.отд.		Нигманова Н.			10.2026	Генеральный план и транспорт.	РД	1	1
Исполн.		Нигманова Н.			10.2026	КУП-D8. Разбивочный план. М 1:500	EAST WEST ENGINEERING	ООО "EAST-WEST Engineering" г. Ташкент 2026г.	
Н.контр		Кирпичников С.			10.2026				

Формат / Format A3