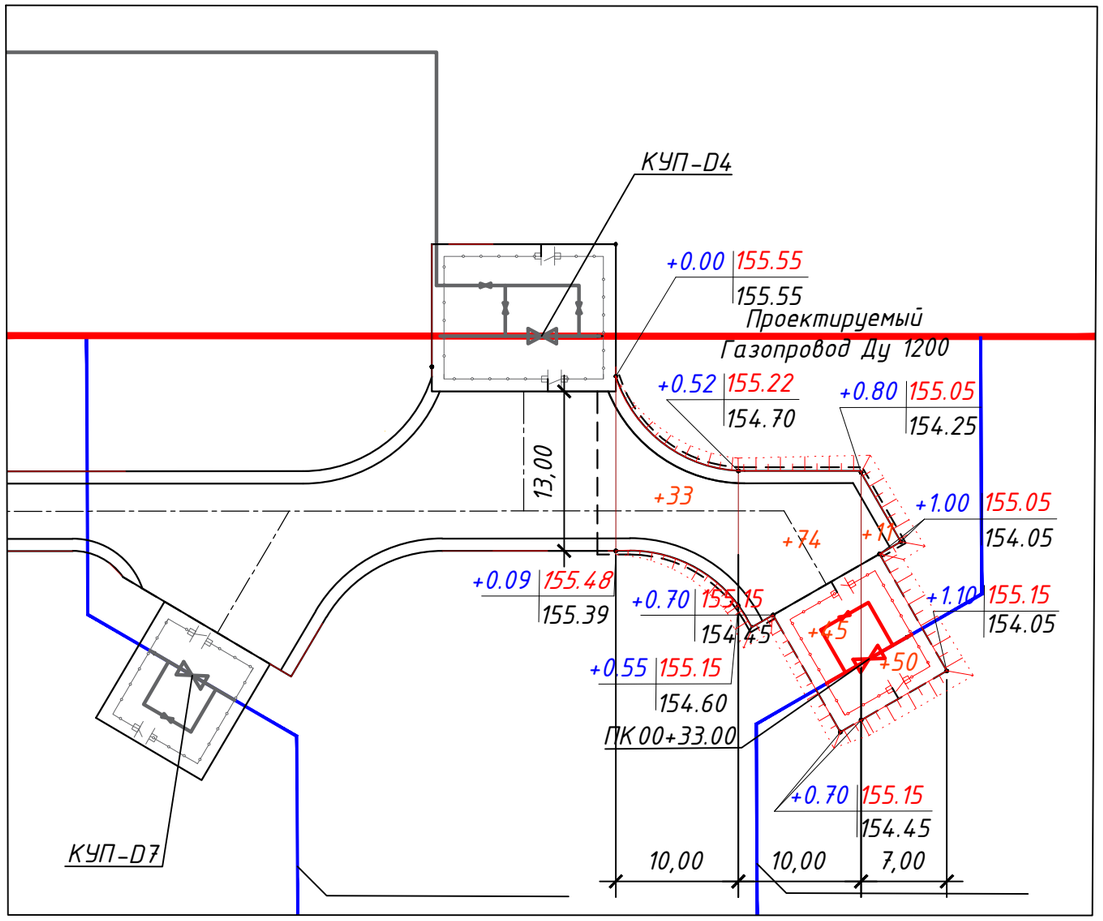



| | | | | | | |
|---|---|---|---|---|---|---|
| Итого,м3 | Насыпь (+) | +33 | +119 | +61 | Всего,м3 | +213 |
| | Выемка (-) | -- | -- | -- | | -- |

## Примечания:

При составлении настоящего чертежа были использованы :
1. Сетка картограммы привязана линейно к пикету ПК 00+33.00.
2. Сетка квадратов объёмы земляных масс разбита на ячейки размерами 10х10м.
3. Производство земляных работ вести в соответствии с требованиями КР 02.01.
4. План земляных масс кранового узла КУП-D4 и подъездной дороги см. EWE0426-MGL1-GLT-054-DRW-730104.

## Условные обозначения:

+41 — объем насыпи в м³

+0.55 | 155.15 / 154.60 — рабочая отм. | проектная отм. / отм.сущ.рельефа

— откосы насыпи

## Ведомость объемов земляных масс

| Наименование грунта | Количество, м³ | | Примечание |
|---|---|---|---|
| | Насыпь (+) | Выемка (-) | |
| 1. Грунт планировки территории | 213 | -- | |
| 2. Вытесненный грунт, в т.ч. при устройстве: | | | |
| а) автодорожных покрытий | | 70 | |
| б) покрытий площадок | | 9 | |
| в) плодородной почвы на участках насыпи | | | |
| г) плодородной почвы на участках выемки | | | |
| 3. Замена растительного грунта на участках насыпи | | | |
| 4. Грунт для устройства откосов насыпи | 40 | | |
| 5. Грунт для устройства откосов выемки | | | |
| 6. Поправка на уплотнение | 25.3 | | |
| Всего пригодного грунта | 278.3 | 79 | |
| 7. Недостаток пригодного грунта | | 199.3 | |
| 8. Плодородный грунт, всего в т.ч.: | | 97 | |
| а) Используемый для озеленения территории | | | |
| б) Избыток плодородного грунта | 97 | | |
| (рекультивация земель) | | | |
| 9. Итого перерабатываемого грунта | 375.3 | 375.3 | |

* С учетом плодородного грунта.
** В карьере. Общая площадь картограммы = 325 м2

| Рев. | Дата | Назначение ревизии | Проверил | Утвердил |
|---|---|---|---|---|
| A1 | 09.09.2026 | Выпущено для строительства | | |
| R1 | 29.07.2026 | Выпущено для рассмотрения | | |

ЗАКАЗЧИК: UTG UZBEKNEFTEGAZ | ГЕНЕРАЛЬНЫЙ ПОДРЯДЧИК: UET UZBEKENERGOTAMIR | ПОДРЯДЧИК: PBG Pro Build Generation | ГЕНЕРАЛЬНЫЙ ПРОЕКТИРОВЩИК: EAST WEST ENGINEERING

| Изм. | Кол.уч. | Лист | №док. | Подпись | Дата |
|---|---|---|---|---|---|
| ГИП | | Схабицкий А. | | | 07.2026 |
| Нач.отд. | | Нигманова Н. | | | 07.2026 |
| Исполн. | | Нигманова Н. | | | 07.2026 |
| Н.контр | | Схабицкий А. | | | 07.2026 |

EWE0426-MGL1-GLT-054-DRW-770104-A1

«СТРОИТЕЛЬСТВО НОВЫХ НИТОК (УЧАСТКОВ) ГАЗОПРОВОДОВ «ГАЗЛИ - САРИМОЙ» И «АКЧАЛОК - ГАЗЛИ - НУКУС» ОБЩЕЙ ПРОТЯЖЕННОСТЬЮ НЕ МЕНЕЕ 275 км».

ГАЗОПРОВОД «ГАЗЛИ-САРИМОЙ» (54 км)

Генеральный план и транспорт.

| Стадия | Лист | Листов |
|---|---|---|
| РД | 1 | 1 |

КУП-D8.
План земляных масс М 1:500

ООО "EAST-WEST Engineering"
г. Ташкент 2026г.

Взам. инв.№ | Подпись и дата | Инв. № подл

Формат / Format A3