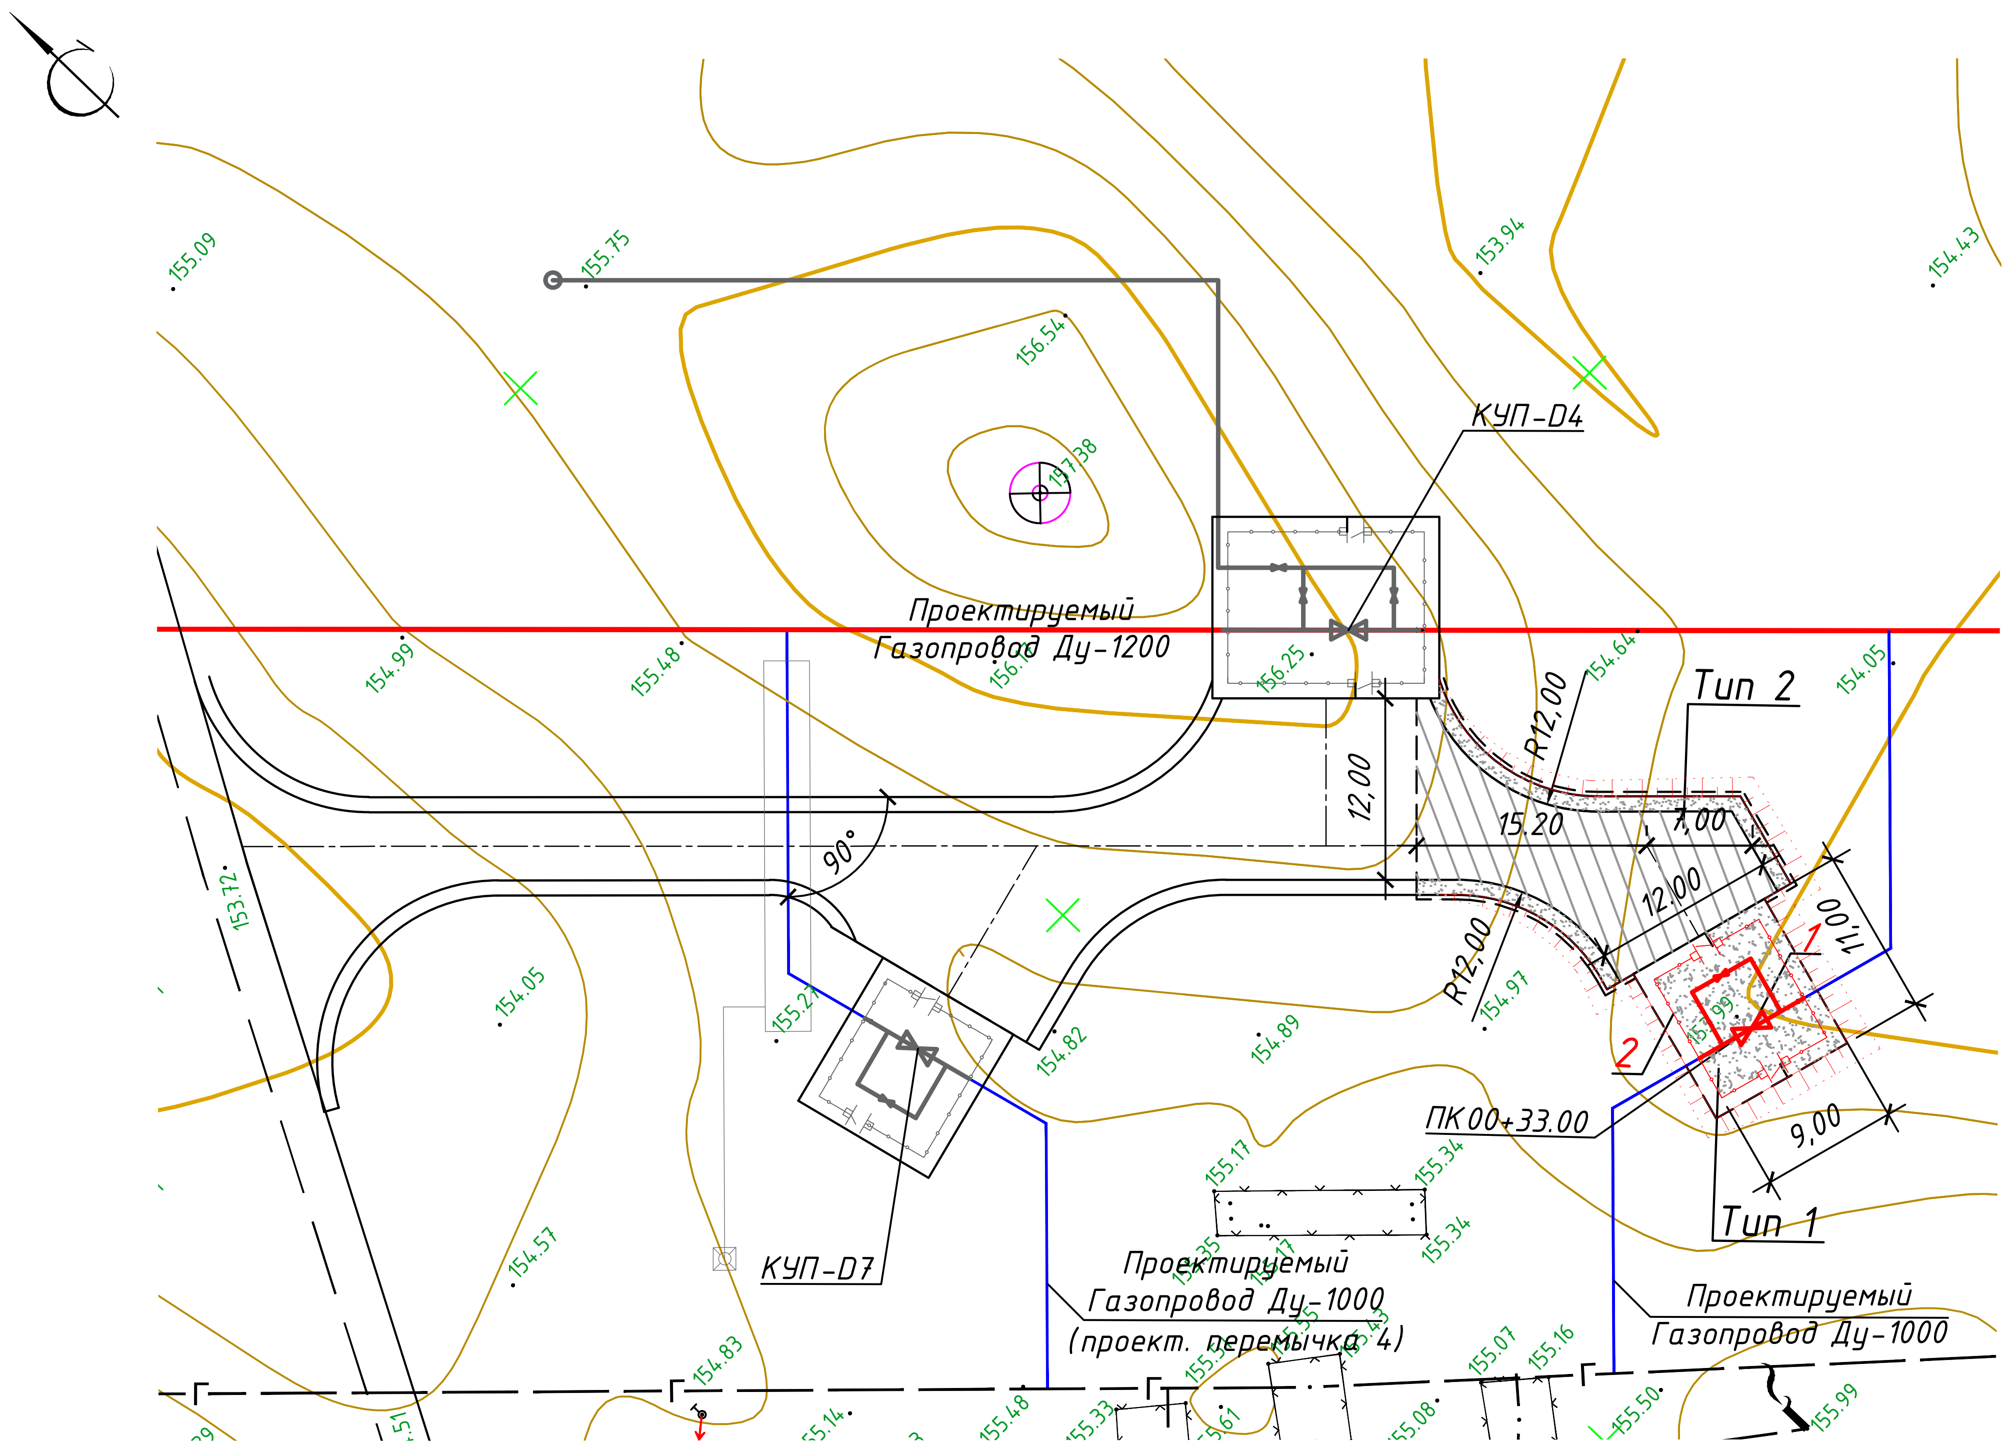

Тип 1

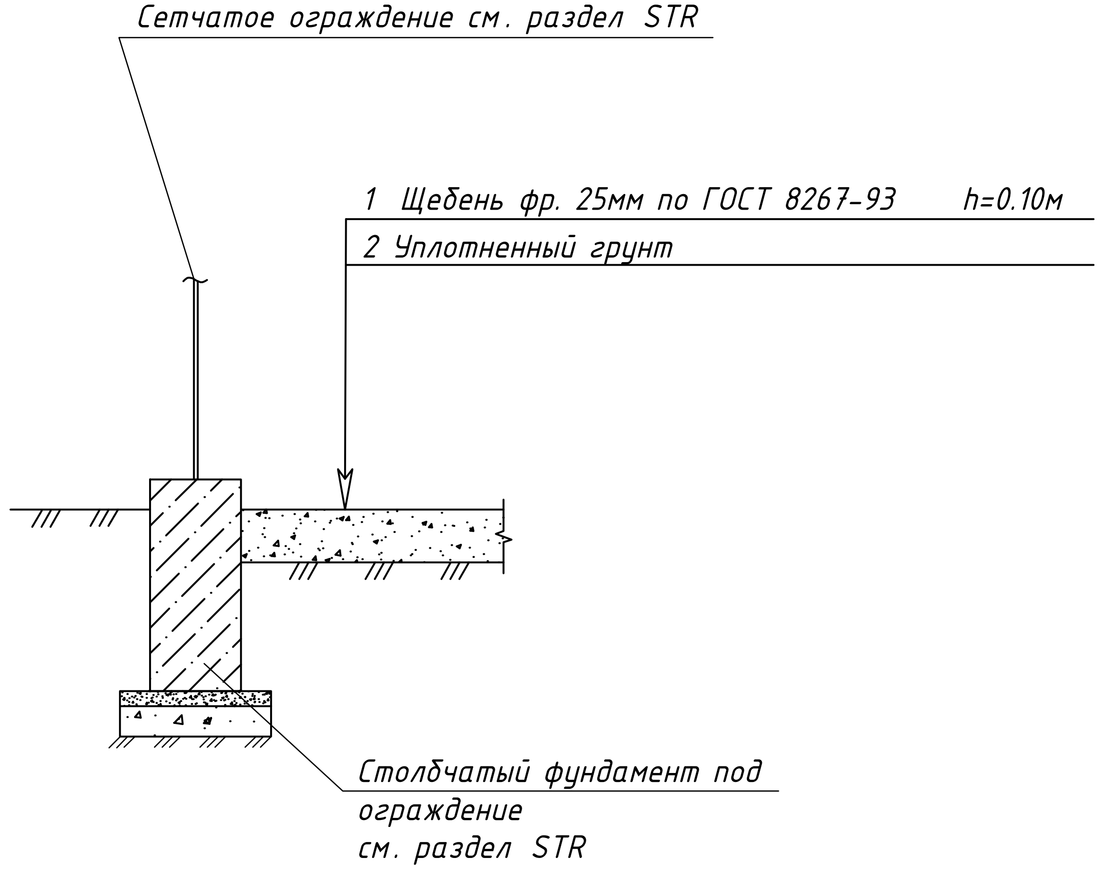
Сетчатое ограждение см. раздел STR
1 Щебень фр. 25мм по ГОСТ 8267-93 h=0.10м
2 Уплотненный грунт
Столбчатый фундамент под ограждение см. раздел STR

Экспликация зданий и сооружений

Номер на плане	Наименование	Примечание
1	Крановый узел Ду 1000	
2	Ограждение сетчатое	

Ведомость тротуаров, дорожек и площадок

Тип	Обозначение	Наименование		Ед. изм.	Примечание
Покрытие площадки					
1	▨	Покрытие из щебня по ГОСТ 8267-93,	h=0.10	м²	90
Покрытие проездов					
2	▨	Покрытие из щебеночно-песчаной смеси по ГОСТ 25607-2009 смесь С1 Основание из гравийно-песчаной смеси по ГОСТ 25607-2009 смесь С3	h=0,15 м h=0,15 м	м²	190.0
		Укрепление обочин из ГПС ГОСТ 25607-2009 смесь С4	h=0,15 м	м²	45.0

Тип 2

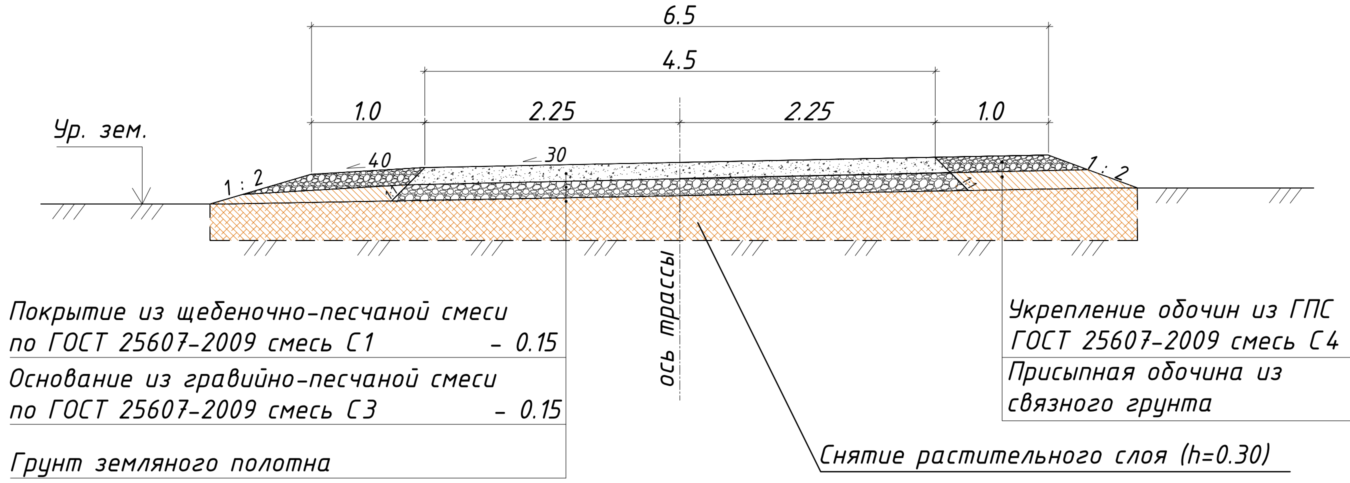
6.5
4.5
1.0
2.25
2.25
1.0
Ур. зем.
1 : 2
40
30
1 : 2
ось трассы
Покрытие из щебеночно-песчаной смеси по ГОСТ 25607-2009 смесь С1 - 0.15
Основание из гравийно-песчаной смеси по ГОСТ 25607-2009 смесь С3 - 0.15
Грунт земляного полотна
Снятие растительного слоя (h=0.30)
Укрепление обочин из ГПС ГОСТ 25607-2009 смесь С4 - 0.15
Присыпная обочина из связного грунта - 0.15

Примечания:

При составлении настоящего чертежа были использованы :

1. Материалы топографо-геодезической съемки, предоставлены АО "O'ZLITINEFTGAZ".
2. Система координат местная. Высотные отметки даны в Балтийской системе.
3. Размеры даны в метрах.
4. Площадка кранового узла КУП-D8 привязана линейно к пикету ПК 00+33.00.
5. Данный лист смотри совместно с листами разделов PIL, PRE, ELE, STR, SYS.
6. Детальный план кранового узла см. EWE0426-MGL1-PRE-054-DRW-760203.
7. План благоустройства территории кранового узла КУП-D4 см. EWE0426-MGL1-GLT-054-DRW-730103 и КУП-D7 см. EWE0426-MGL1-GLT-054-DRW-760103.
8. Защита Пересечения проектной дороги с проектной перемычкой 4 (КУП-D7) предусмотрена в техническом решении №1 в рамках авторского надзора.

Взам. инв. №

Подпись и дата

Инв.№ подл.

Рев.	Дата	Назначение ревизии	Проверил	Утвердил
A2	07.10.2026	Выпущено для строительства		
A1	09.09.2026	Выпущено для строительства		
R1	29.07.2026	Выпущено для рассмотрения		

ЗАКАЗЧИК: UTG UZTRANSGAZ

ГЕНЕРАЛЬНЫЙ ПОДРЯДЧИК: UET UZBEKENERGOTAMIR

ПОДРЯДЧИК: PBG Pro Build Generation

ГЕНЕРАЛЬНЫЙ ПРОЕКТИРОВЩИК: EAST WEST ENGINEERING

EWE0426-MGL1-GLT-054-DRW-770106-A2

«СТРОИТЕЛЬСТВО НОВЫХ НИТОК (УЧАСТКОВ) ГАЗОПРОВОДОВ «ГАЗЛИ - САРИМОЙ» И «АКЧАЛОК - ГАЗЛИ - НУКУС» ОБЩЕЙ ПРОТЯЖЕННОСТЬЮ НЕ МЕНЕЕ 275 км».

Изм.	Кол.уч.	Лист	№ док.	Подпись	Дата
ГИП		Кирпичников С.			10.2026
Нач.отд.		Нигманова Н.			10.2026
Исполн.		Нигманова Н.			10.2026
Н.контр		Кирпичников С.			10.2026

ГАЗОПРОВОД «ГАЗЛИ-САРИМОЙ» (54 км)

Генеральный план и транспорт.

Стадия	Лист	Листов
РД	1	1

КУП-D8.
План благоустройства
территории М 1:500

EAST WEST ENGINEERING
ООО "EAST-WEST Engineering"
г. Ташкент 2026 г.

Формат / Format A4x3