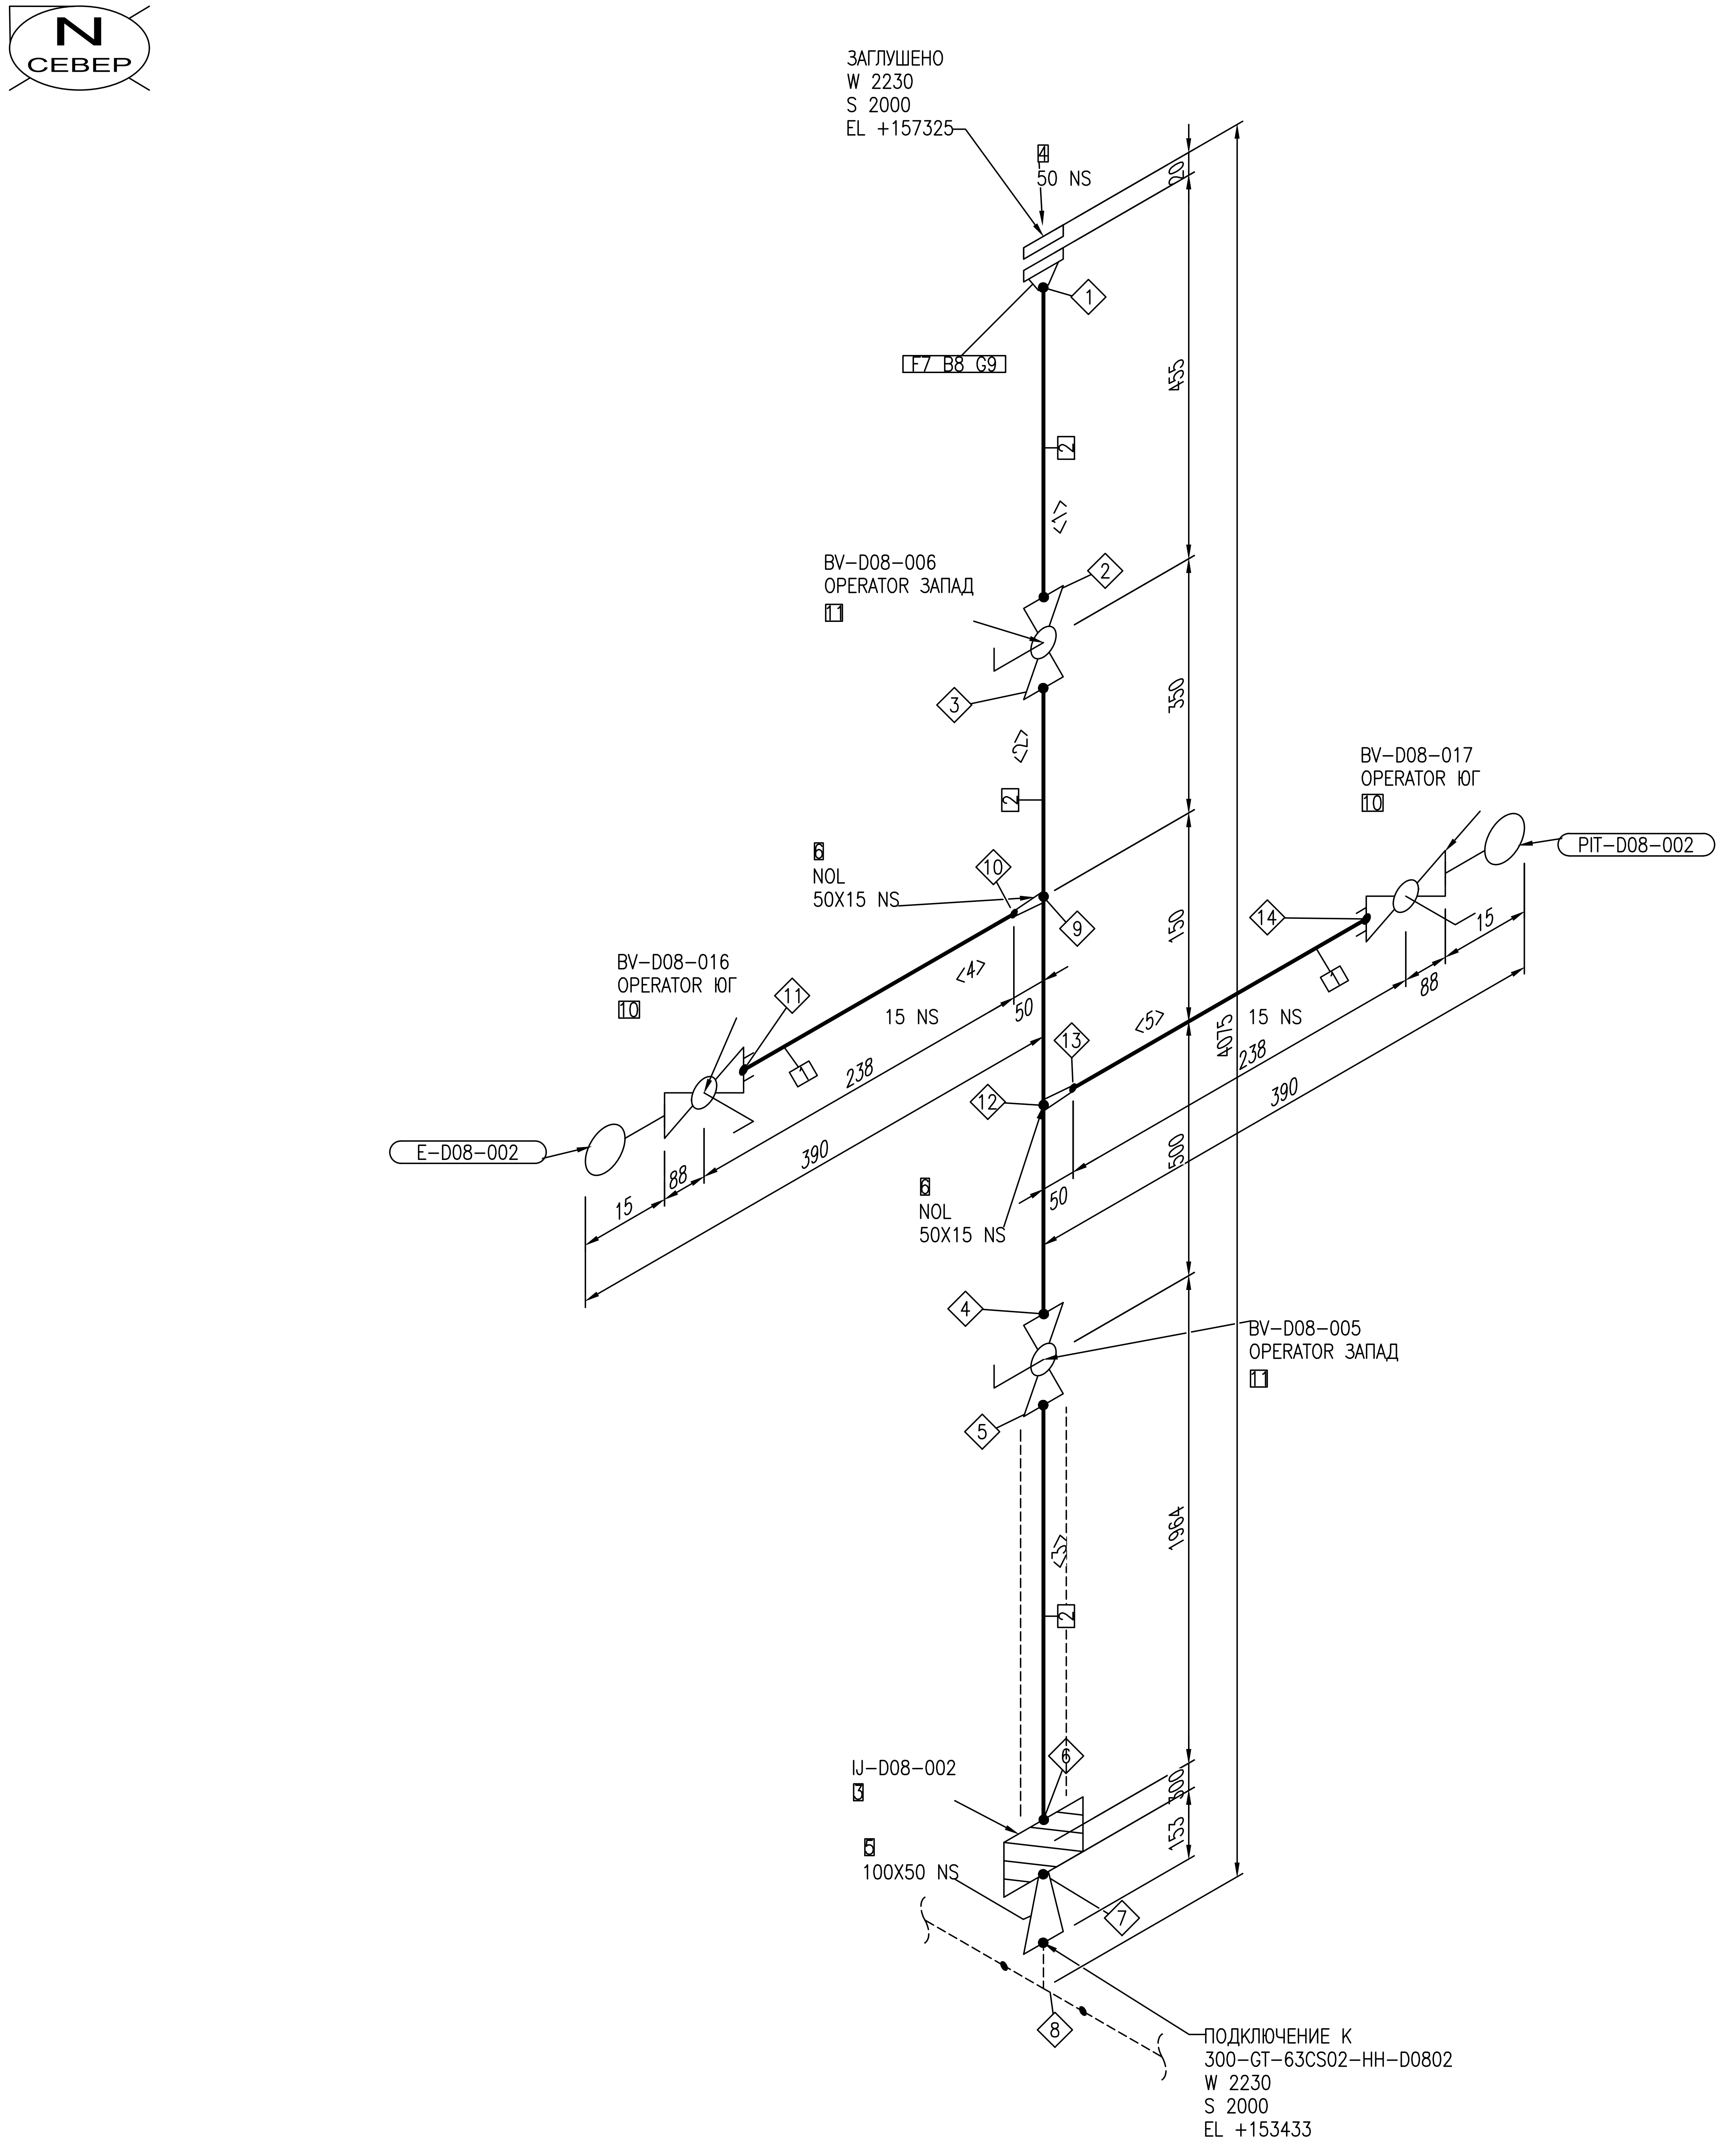

## ПЕРЕЧЕНЬ СВАРНЫХ ШВОВ

| № | DN | ТИП |
|---|---|---|
| 1 | 50 | BUTTWELD |
| 2 | 50 | BUTTWELD |
| 3 | 50 | BUTTWELD |
| 4 | 50 | BUTTWELD |
| 5 | 50 | BUTTWELD |
| 6 | 50 | BUTTWELD |
| 7 | 50 | BUTTWELD |
| 8 | 100 | BUTTWELD |
| 9 | 50 | TAPWELD |
| 10 | 15 | WELD |
| 11 | 15 | SOCKETWELD |
| 12 | 50 | TAPWELD |
| 13 | 15 | WELD |
| 14 | 15 | SOCKETWELD |

## ПЕРЕЧЕНЬ ТРУБНЫХ КАТУШЕК

| № | DN | ДЛИНА |
|---|---|---|
| 1 | 50 | 273ММ |
| 2 | 50 | 770ММ |
| 3 | 50 | 1549ММ |
| 4 | 15 | 150ММ |
| 5 | 15 | 150ММ |

## СПЕЦИФИКАЦИЯ ИЗДЕЛИЙ И МАТЕРИАЛОВ

| ПОЗ. | НАИМЕНОВАНИЕ | СТАНДАРТ | КОЛ. | ПРИМЕЧАНИЕ |
|---|---|---|---|---|
| 1 | Трубы стальные бесшовные холоднодеформированные Ст20, 22Х3 | ГОСТ 8734–75/ ГОСТ 8733–74 | 0.3М | |
| 2 | Трубы стальные бесшовные горячедеформированные Ст20, 57Х4 | ГОСТ 8732–78/ ГОСТ 8731–74 | 2.6М | |
| 3 | Изолирующее соединение приварное, 6.3 МПа, 57Х4 | EWE0426–MGL1–PRE–054–DSH –610135 | 1 | |
| 4 | Заглушка фланцевая стальная АТК 24.200.02–90, исполнение 4, 6.3 МПа, Ст20, DN50 | АТК 24.200.02–90 | 1 | |
| 5 | Переход ПШК I 114(5К48)Х57(4К42)–5,5(6,9)–0.75–30, сталь 09Г2С | ТУ 1469–017–38948552–2015 | 1 | |
| 6 | Штуцер приварной ШУсТ–1–50–22Х3.0–6,3–20–2 | ТУ 3600–010–88626180–2012 | 2 | |
| 7 | Фланец стальной приварной встык, тип 11, исполнение J, ряд 1, 6.3 МПа, Ст20, 57Х4 | ГОСТ 33259–2015 | 1 | |
| 8 | Крепежный комплект 2–1–М20х110, шпильки Ст35, шайбы Ст20, гайки Ст25, для DN50 | ОСТ 26–2040–96 | 4 | |
| 9 | Прокладка овального сечения, линзовая стальная, тип 1, Сталь 08КП, 6.3 МПа, DN50 | ГОСТ 34655–2020 | 1 | |
| 10 | Кран шаровой DN15 PN–6,3 МПа с ручным приводом, приварной х резьбовой, 1/2" NPT F, надземный | EWE0426–MGL1–PRE–054–DSH –610125 | 2 | |
| 11 | Кран шаровой DN50 PN–6,3 МПа с ручным приводом,приварной, надземный | EWE0426–MGL1–PRE–054–DSH –610125 | 2 | |

| Трубопровод | ДАННЫЕ ПО ТРУБОПРОВОДУ | | |
|---|---|---|---|
| 50-GT-63CS02-HH-D0804 | Расчетные параметры | Температура | -26,9...+85 °С |
| | | Давление | 6,3 MPa |
| | Рабочие параметры | Температура | -20...+40 °С |
| | | Давление | 5,5 MPa |
| | Параметры испытания | Тип | Гидравлическое |
| Ссылочные чертежи No | | Давление | 6,9 MPa |
| EWE0426-MGL1-PRE-054-SCM-610110 | Изоляция | Тип | НН |
| | | Толщина | mm |
| | Катодная защита | Да или Нет | Да |

| Рев. | Дата | Назначение ревизии | Проверил | Утвердил |
|---|---|---|---|---|
| A1 | 07.09.2026 | Утверждено для строительства | | |
| R1 | 22.06.2026 | Выпущено для рассмотрения | | |

ЗАКАЗЧИК: UTG UZTRANSGAZ

ГЕНЕРАЛЬНЫЙ ПОДРЯДЧИК: UET UZBEKENERGOTAMIR

ПОДРЯДЧИК: PBG Pro Build Generation

ГЕНЕРАЛЬНЫЙ ПРОЕКТИРОВЩИК: EAST WEST ENGINEERING

# EWE0426-MGL1-PRE-054-ISO-770605-A1

«СТРОИТЕЛЬСТВО НОВЫХ НИТОК (УЧАСТКОВ) ГАЗОПРОВОДОВ «ГАЗЛИ - САРИМОЙ» И «АКЧАЛОК - ГАЗЛИ - НУКУС» ОБЩЕЙ ПРОТЯЖЕННОСТЬЮ НЕ МЕНЕЕ 275 КМ».

| Изм. | Кол.уч. | Лист | №док. | Подпись | Дата |
|---|---|---|---|---|---|
| ГИП | | Кирпичников С. | | | 09.2026 |
| Нач.отд. | | Рябинин А. | | | 09.2026 |
| Исполн. | | Таштимуров Р. | | | 09.2026 |
| | | | | | |
| | | | | | |
| Н.контр | | Кирпичников С. | | | 09.2026 |

ГАЗОПРОВОД «ГАЗЛИ-САРИМОЙ» (54 КМ)
Линейный крановый узел DN1000 КУП-D8

| Стадия | Лист | Листов |
|---|---|---|
| РД | 1 | 1 |

Изометрический чертеж трубопровода
50-GT-63CS02-HH-D0804

ООО "EAST-WEST Engineering"
г. Ташкент 2026г.

Взам. инв. №
Подпись и дата
Инв.№ подл.

Формат А2 594х420