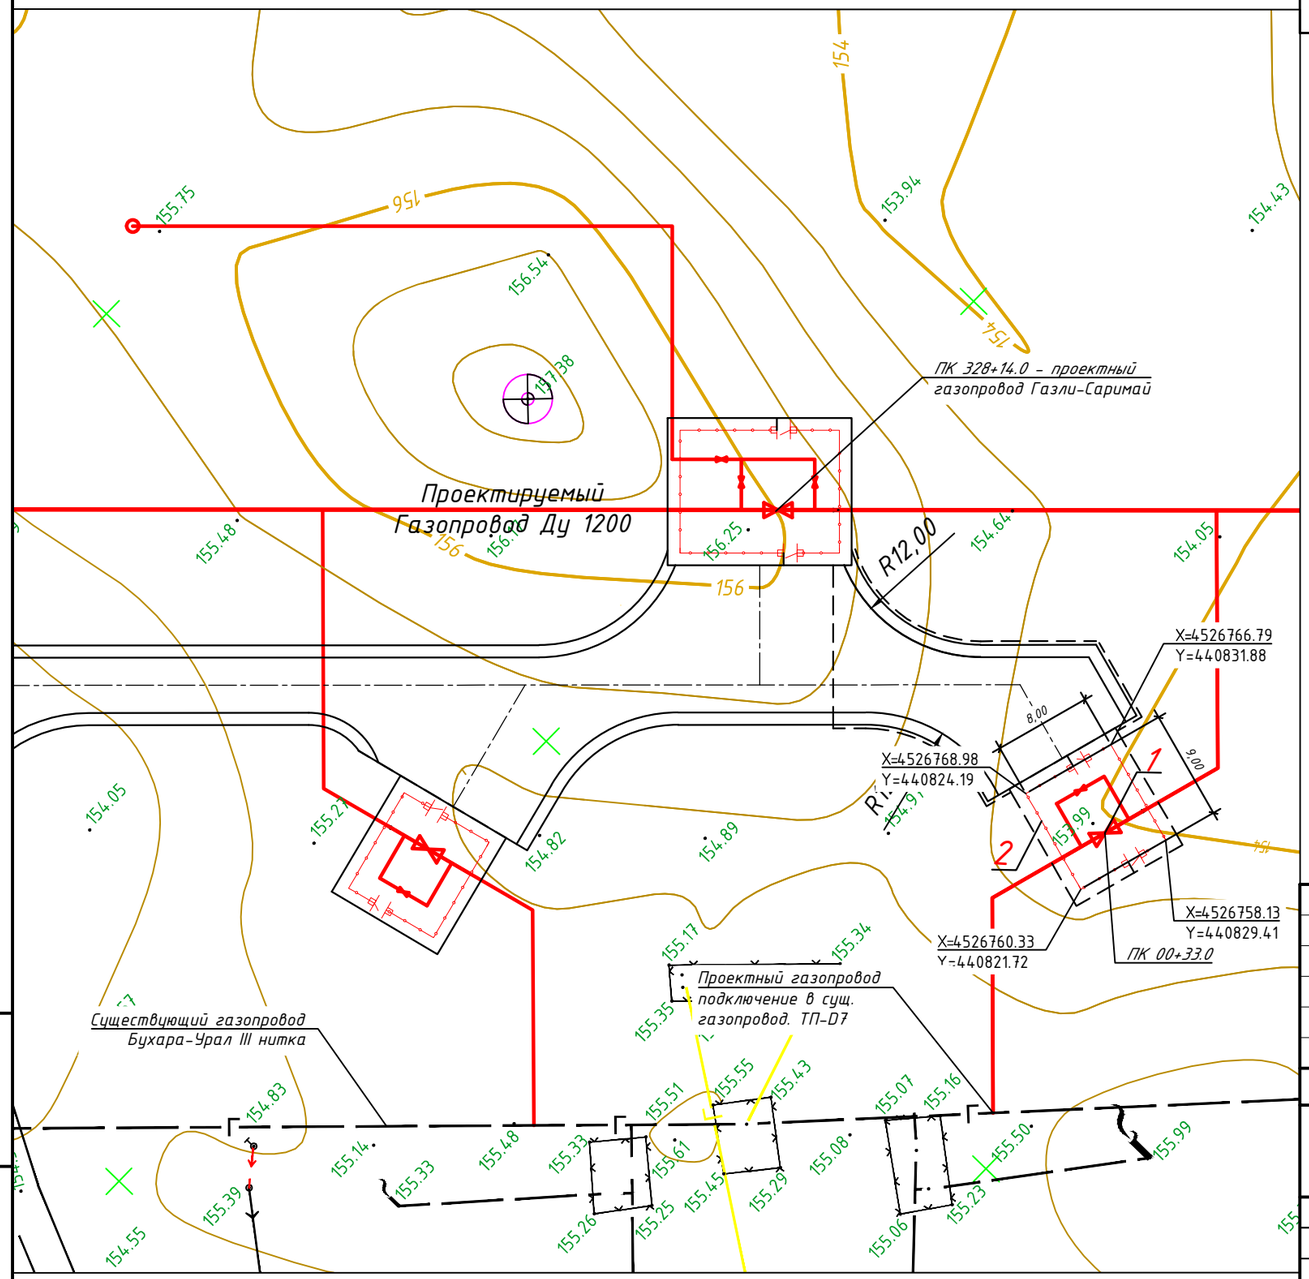


Экспликация зданий и сооружений

Номер на плане	Наименование	Примечание
1	Крановый узел Ду 1000	
2	Ограждение сетчатое	

Условные обозначения

- Ограждение
- Калитка
- Граница планировки
- Существующий газопровод
- Проектируемый газопровод ДУ-1200, ДУ-1000

Примечание:

1. Материалы топографо-геодезической съемки, предоставлены АО "O'ZLITINEFTGAZ";
2. Система координат см. раздел ГП. Высотные отметки даны в Балтийской системе;
3. Координаты ограждения даны в геометрической системе;
4. Кран XV-D08-001 установлен на ПК 0+33.0 проектного газопровода;
5. Детальный план кранового узла см. EWE0426-MGL1-PRE-054-DRW-770203;

Рев.	Дата	Назначение ревизии	Проверил	Утвердил
A1	07.08.2026	Утверждено для строительства		
R1	08.07.2026	Выпущено для рассмотрения		

ЗАКАЗЧИК: UTG UZTRANSGAZ

ГЕНЕРАЛЬНЫЙ ПОДРЯДЧИК: UET UZBEKENERGOTAMIR

ПОДРЯДЧИК: PBG Pro Build Generation

ГЕНЕРАЛЬНЫЙ ПРОЕКТИРОВЩИК: EAST WEST ENGINEERING

Изм.	Кол.уч.	Лист	№док.	Подпись	Дата
ГИП		Схабицкий А.			08.2026
Нач.отд.		Рябинин А.			08.2026
Исполн.		Юлдашев И.			08.2026
Н.контр		Схабицкий А.			08.2026

EWE0426-MGL1-PRE-054-PLA-770202-A1

«СТРОИТЕЛЬСТВО НОВЫХ НИТОК (УЧАСТКОВ) ГАЗОПРОВОДОВ «ГАЗЛИ – САРИМОЙ» И «АКЧАЛОК – ГАЗЛИ – НУКУС» ОБЩЕЙ ПРОТЯЖЕННОСТЬЮ НЕ МЕНЕЕ 275 КМ».

ГАЗОПРОВОД «ГАЗЛИ-САРИМОЙ» (54 КМ)

Стадия	Лист	Листов
РД		1

КУП-D8. Ситуационный план. М 1:500.

EAST WEST ENGINEERING

ООО "EAST-WEST Engineering"
г. Ташкент 2026г.

Взам. инв. №

Подпись и дата

Инв.№ подл.

Формат / Format A3