


Разрез 1 – 1 м 1:20.

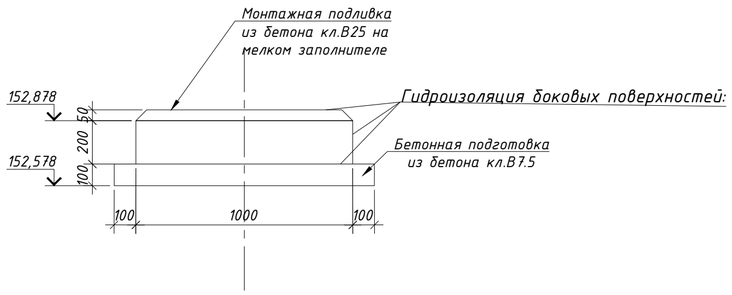


Разрез 1–1 м 1:20. (армирование)

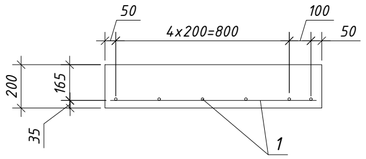

План фундамента ФОМ2 м 1:20.

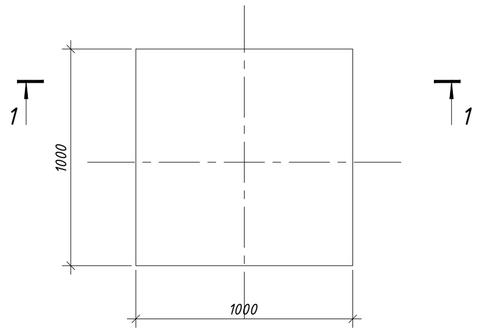

Сетка С1 м 1:20.

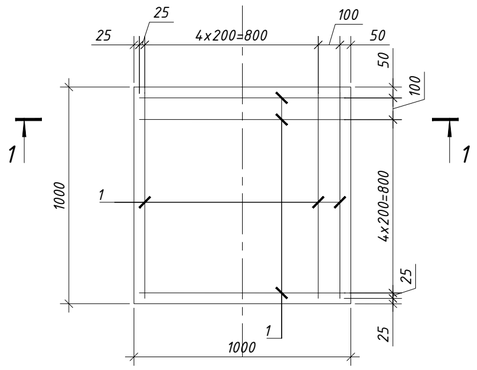

Спецификация элементов

Марка Поз.	Обозначение	Наименование	Кол.шт	Масса ед., кг	Прим.
		Фундамент ФОМ2			
		Сборные единицы			
С1	См. данный лист	Сетка С1	1		10.12
		Детали			
1	ГОСТ 34028-2016	Ф12 А500 L=950 мм	12	0.84	10.12
		Материалы			
	на подливку	Бетон на мелком заполнителе кл. В25, W6, F50			0.05 м³
		Бетон кл. В20, W6, F50			0.20 м³
	на подготовку	Бетон кл. В7.5			0.14 м³
		Гидроизоляция фундамента на площади:			3,92 м²

Гидроизоляция фундамента из двух слоев полимерного покрытия на основе лака ХВ-784 по ГОСТ 7313-2002 толщиной 25 мкм.

Примечания:

1. *Объединение арматурных стержней в плоские сетки или пространственные каркасы выполнять вязальной стальной отожженной проволокой d=0.8-1.0мм. Применение ручной электродуговой сварки не допускается.*
2. *Подливку выполнить из бетона кл. В25 на мелком заполнителе.*
3. *Расположение фундамента смотри чертёж: Схема расположения кранового узла КУП-D8.*
4. *Фундамент ФОМ2 изготовить в количестве - 1 шт.*
5. *Бетон для фундамента применять на сульфатостойком портландцементе.*

Ведомость расхода стали, кг

Марка элемента	Изделия арматурные					Общий расход
	Арматура класса				Всего	
	А240		А500			
	ГОСТ 34028-2016		ГОСТ 34028-2016			
	Ф8	Итого	Ф12	Итого		
Фундамент ФОМ2			10.12	10.12	10.12	10.12

А1	09.09.2026	Выпущено для строительства		
R1	28.07.2026	Выпущено для рассмотрения		
Рев	Дата	Назначение ревизии	Проверил	Утвердил

ЗАКАЗЧИК: UTG UZTRANSGAZ

ГЕНЕРАЛЬНЫЙ ПОДРЯДЧИК: UET UZBEKENERGOTAMIR

ПОДРЯДЧИК: PBG Pro Build Generation

ГЕНЕРАЛЬНЫЙ ПРОЕКТИРОВЩИК: EAST WEST ENGINEERING

EWE0426-MGL1-STR-054-DRW-770505-A1

«СТРОИТЕЛЬСТВО НОВЫХ НИТОК (УЧАСТКОВ) ГАЗОПРОВОДОВ «ГАЗЛИ - САРИМОЙ» И «АКЧАЛОК - ГАЗЛИ - НУКУС» ОБЩЕЙ ПРОТЯЖЕННОСТЬЮ НЕ МЕНЕЕ 275 КМ».

Изм.	Кол.уч.	Лист	№ док.	Подпись	Дата
ГИП		Кирпичников С.			09.09.26
Нач.отд.		Каршиев А.			09.09.26
Исполн.		Юлдашев Ж.			09.09.26
Н.контр		Кирпичников С.			09.09.26

ГАЗОПРОВОД "ГАЗЛИ-САРИМОЙ" (54 КМ)
Линейный крановый узел DN1000 КУП-D8

Стадия	Лист	Листов
РП	1	1

Фундамент ФОМ2

ООО "EAST-WEST Engineering"
г. Ташкент 2026г.

Взам. инв. №

Подпись и дата

Инв.№ подл.