Схема расположения сетчатого ограждения

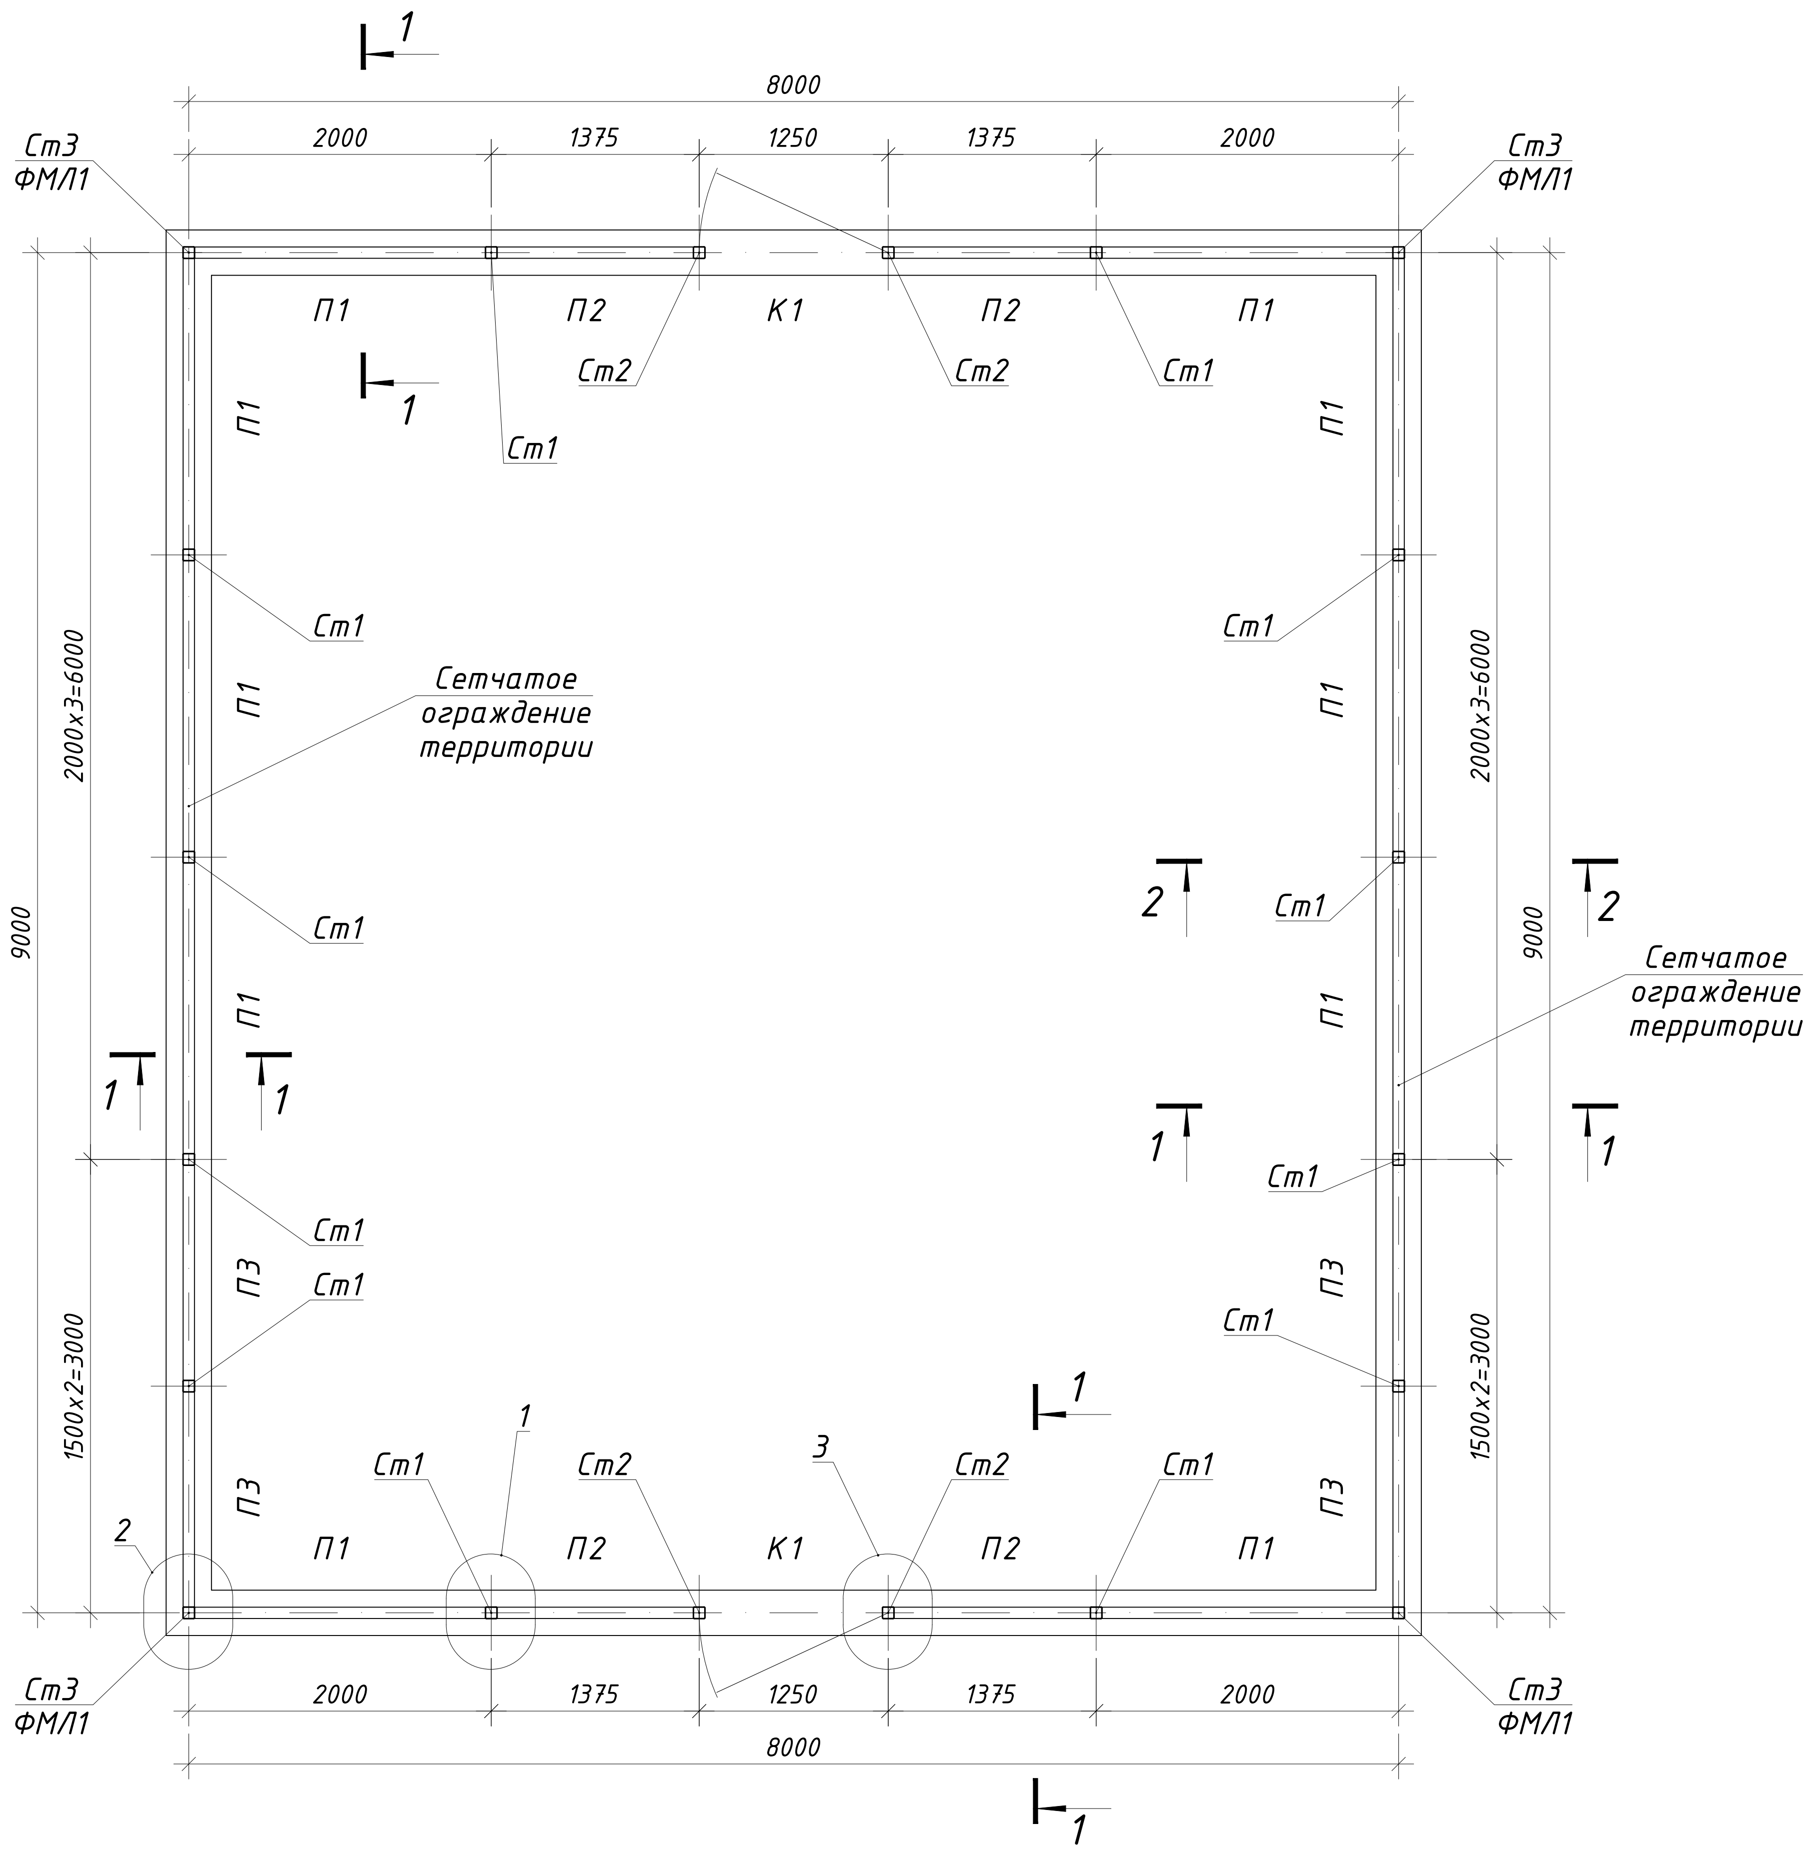

Узел 1

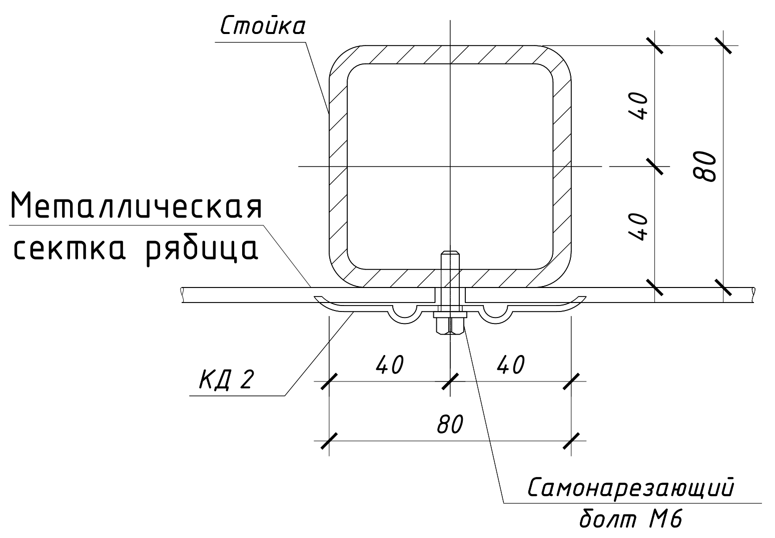

Узел 2

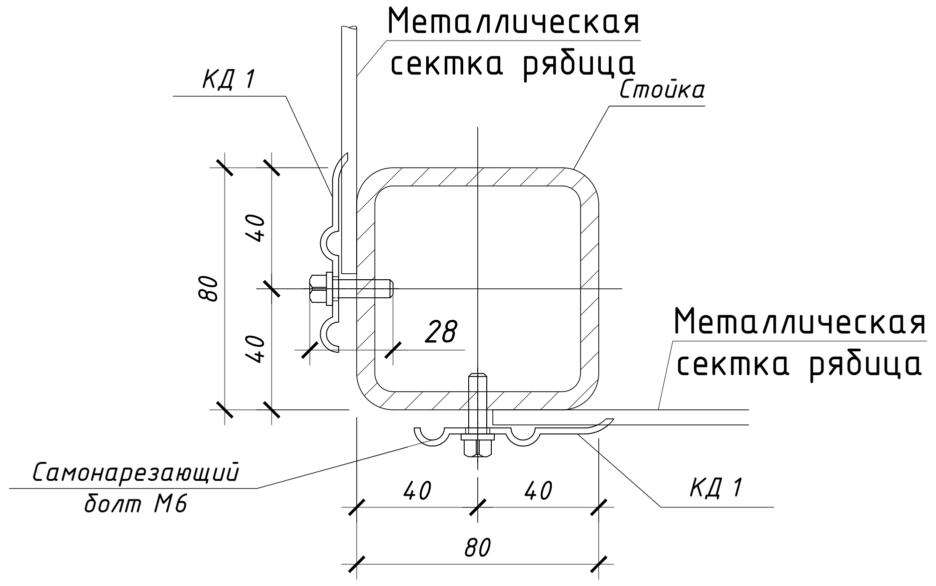

Узел 3

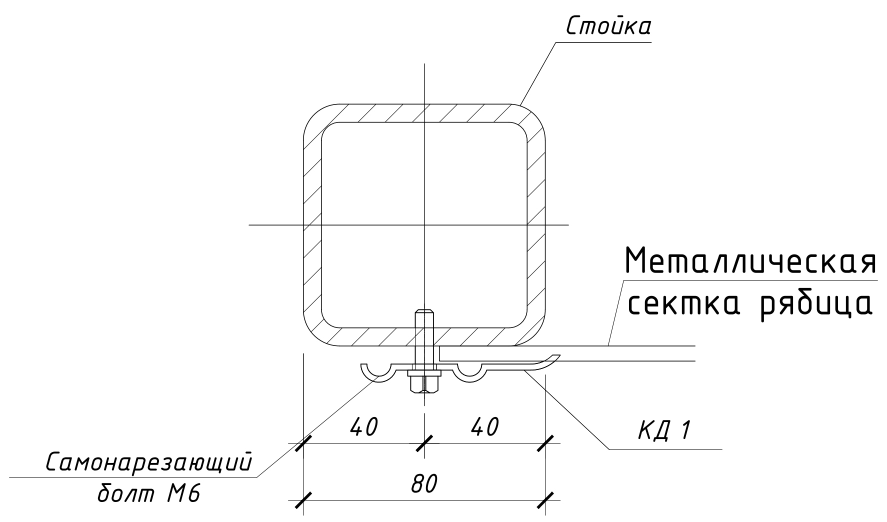

Спецификация элементов

Марка Поз.	Обозначение	Наименование	Кол. шт.	Масса ед.кг	Примеч.
		Линейный крановый узел КУП-D8			
ФМЛ1	EWE0426-MGL1-STR-054-DRW-770507	Фундамент ленточный, монолитный ФМЛ1			
Ст1	EWE0426-MGL1-STR-054-DRW-770508	Стойка ограждения Ст1	12		
Ст2	EWE0426-MGL1-STR-054-DRW-770509	Стойка ограждения Ст2	4		
Ст3	EWE0426-MGL1-STR-054-DRW-770510	Стойка ограждения Ст3	4		
П1	EWE0426-MGL1-STR-054-DRW-770511	Панель ограждения П1	10		
П2	EWE0426-MGL1-STR-054-DRW-770512	Панель ограждения П2	4		
П3	EWE0426-MGL1-STR-054-DRW-770513	Панель ограждения П3	4		
К1	EWE0426-MGL1-STR-054-DRW-770514	Калитка К1	2		
КД1	EWE0426-MGL1-STR-054-DRW-770515	Крепежная деталь КД1	24		
КД2	EWE0426-MGL1-STR-054-DRW-770515	Крепежная деталь КД2	24		

Примечания:

1. Данный чертёж читать совместно с ленточным фундаментом ФМЛ1.
2. Изготовить общее количество узлов:
   - узел 1 - 12 шт.
   - узел 2 - 4 шт.
   - узел 3 - 4 шт.
3. Сечения 1 - 1, 2 - 2 смотреть на л. -DRW-770507

Рев	Дата	Назначение ревизии	Проверил	Утвердил
A1	09.09.2026	Выпущено для строительство		
R1	28.07.2026	Выпущено для рассмотрения		

ЗАКАЗЧИК: UTG UZTRANSGAZ «TRANSGAZINJINIRING»
ГЕНЕРАЛЬНЫЙ ПОДРЯДЧИК: UET UZBEKENERGOTAMIR
ПОДРЯДЧИК: PBG Pro Build Generation
ГЕНЕРАЛЬНЫЙ ПРОЕКТИРОВЩИК: EAST WEST ENGINEERING

EWE0426-MGL1-STR-054-DRW-770506-A1

«СТРОИТЕЛЬСТВО НОВЫХ НИТОК (УЧАСТКОВ) ГАЗОПРОВОДОВ «ГАЗЛИ - САРИМОЙ» И «АКЧАЛОК - ГАЗЛИ - НУКУС» ОБЩЕЙ ПРОТЯЖЕННОСТЬЮ НЕ МЕНЕЕ 275 КМ».

Изм.	Кол.уч.	Лист	№ док.	Подпись	Дата
ГИП		Кирпичников С.			09.09.26
Нач.отд.		Каршиев А.			09.09.26
Исполн.		Юлдашев Ж.			09.09.26
Н.контр		Кирпичников С.			09.09.26

ГАЗОПРОВОД "ГАЗЛИ-САРИМОЙ" (54 КМ)
Линейный крановый узел DN1000 КУП-D8

Стадия	Лист	Листов
РП	1	1

Схема расположения сетчатого ограждения

ООО "EAST-WEST Engineering"
г. Ташкент 2026г.

Формат / Format A2

Взам. инв. №
Подпись и дата
Инв.№ подл.