

2 - 2
(опалубочный чертеж)

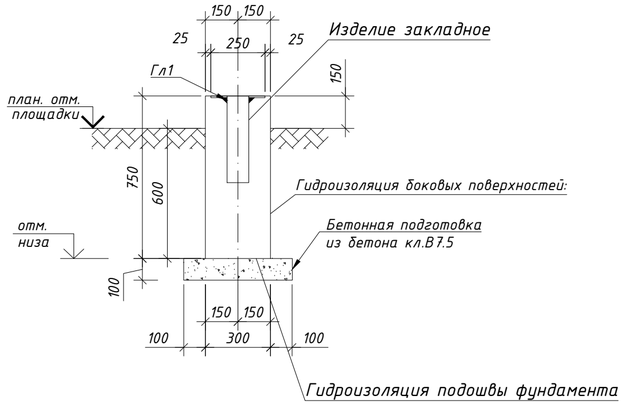

1 - 1
(армирование)

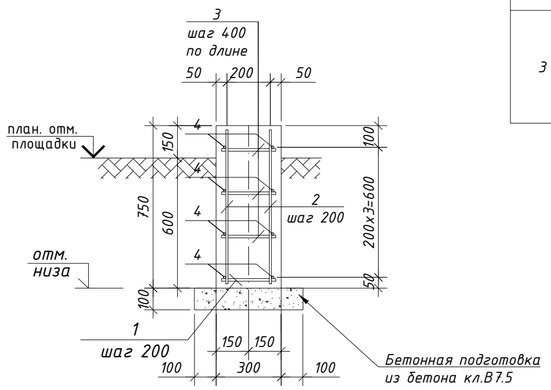


Ведомость деталей

Поз.	Эскиз
3	220; 100; 100; L=420


Спецификация элементов

Марка Поз.	Обозначение	Наименование	Кол.шт	Масса ед., кг	Прим.
		Фундамент ФМЛ1			
		Сборные единицы			
Гл-1		Гильза Гл-1	20	9.014	180.280
		Детали			
1	ГОСТ 34028-2016	Ф12 А500 L=250 мм	170	0.22	37.71
2	ГОСТ 34028-2016	Ф12 А500 L=710 мм	340	0.63	214.21
3	ГОСТ 34028-2016	Ф8 А240 L=420 мм	270	0.17	44.72
4	ГОСТ 34028-2016	Ф8 А240 L=281600 мм		111.23	
		Гильза Гл-1			на 1 шт.
5	ГОСТ 30245-2003	Профиль 100х100х4, L=396	1	4,77	4.770
6	ГОСТ 19903-90*	Лист 4х100х100	1	0,314	0.314
7	ГОСТ 19903-90*	Лист 8х250х250	1	3,93	3.930
		Материалы			
		Бетон кл. В15, W6, F50			7.65 м³
	на подготовку	Бетон кл. В7.5			1.70 м³
		Гидроизоляция фундамента на площади:			64.6 м²

Гильза Гл-1 м 1:10.

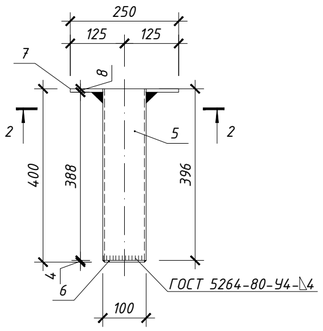

Разрез 2-2
м 1:10.

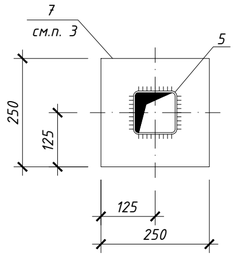

Ведомость расхода стали, кг

Марка элемента	Изделия арматурные					Изделия закладные						Общий расход
	Арматура класса				Всего	Прокат стали					Всего	
	А240		А500			С245						
	ГОСТ 34028-2016		ГОСТ 34028-2016			ГОСТ 19903-90*			ГОСТ 30245-2003			
	Ф8	Итого	Ф12	Итого		t=4	t=8	Итого	□ 100х 100х4	Итого		
Фундамент ФМЛ1	155,95	155,95	251,92	251,92	407,87	6,28	78.60	84,88	95.40	95.40	180,28	588,15

Примечания:
1. Данный чертёж читать совместно с л. EWE0426-MGL1-STR-054-DRW-770506
2. Объединение арматурных стержней в плоские сетки или пространственные каркасы выполнять вязальной стальной отожженной проволокой d=0.8-1.0мм. Применение ручной электродуговой сварки не допускается.
3. Поз.7 предназначена для крепления стойки ограждения на сварке.

Гидроизоляция фундамента из двух слоев полимерного покрытия на основе лака ХП-734 по ГОСТ 52165-2003 толщиной 25 мкм.

Рев	Дата	Назначение ревизии	Проверил	Утвердил
A1	09.09.2026	Выпущено для строительства		
R1	28.07.2026	Выпущено для рассмотрения		

ЗАКАЗЧИК: UTG UZTRANSGAZ | ГЕНЕРАЛЬНЫЙ ПОДРЯДЧИК: UET UZBEKENERGOTAMIR | ПОДРЯДЧИК: PBG Pro Build Generation | ГЕНЕРАЛЬНЫЙ ПРОЕКТИРОВЩИК: EAST WEST ENGINEERING

EWE0426-MGL1-STR-054-DRW-770507-A1

«СТРОИТЕЛЬСТВО НОВЫХ НИТОК (УЧАСТКОВ) ГАЗОПРОВОДОВ «ГАЗЛИ - САРИМОЙ» И «АКЧАЛОК - ГАЗЛИ - НУКУС» ОБЩЕЙ ПРОТЯЖЕННОСТЬЮ НЕ МЕНЕЕ 275 КМ».

Изм.	Кол.уч.	Лист	№ док.	Подпись	Дата			
ГИП		Кирпичников С.			09.09.26	ГАЗОПРОВОД "ГАЗЛИ-САРИМОЙ" (54 КМ) Линейный крановый узел DN1000 КУП-D8	Стадия	Лист	Листов
Нач.отд.		Каршиев А.			09.09.26		РП	1	1
Исполн.		Юлдашев Ж.			09.09.26				
Н.контр		Кирпичников С.			09.09.26	Ленточный фундамент ФМЛ1	EAST WEST ENGINEERING	ООО "EAST-WEST Engineering" г. Ташкент 2026г.	

Взам. инв. № | Подпись и дата | Инв.№ подл.

Формат / Format A2