Стойка ограждения Ст3

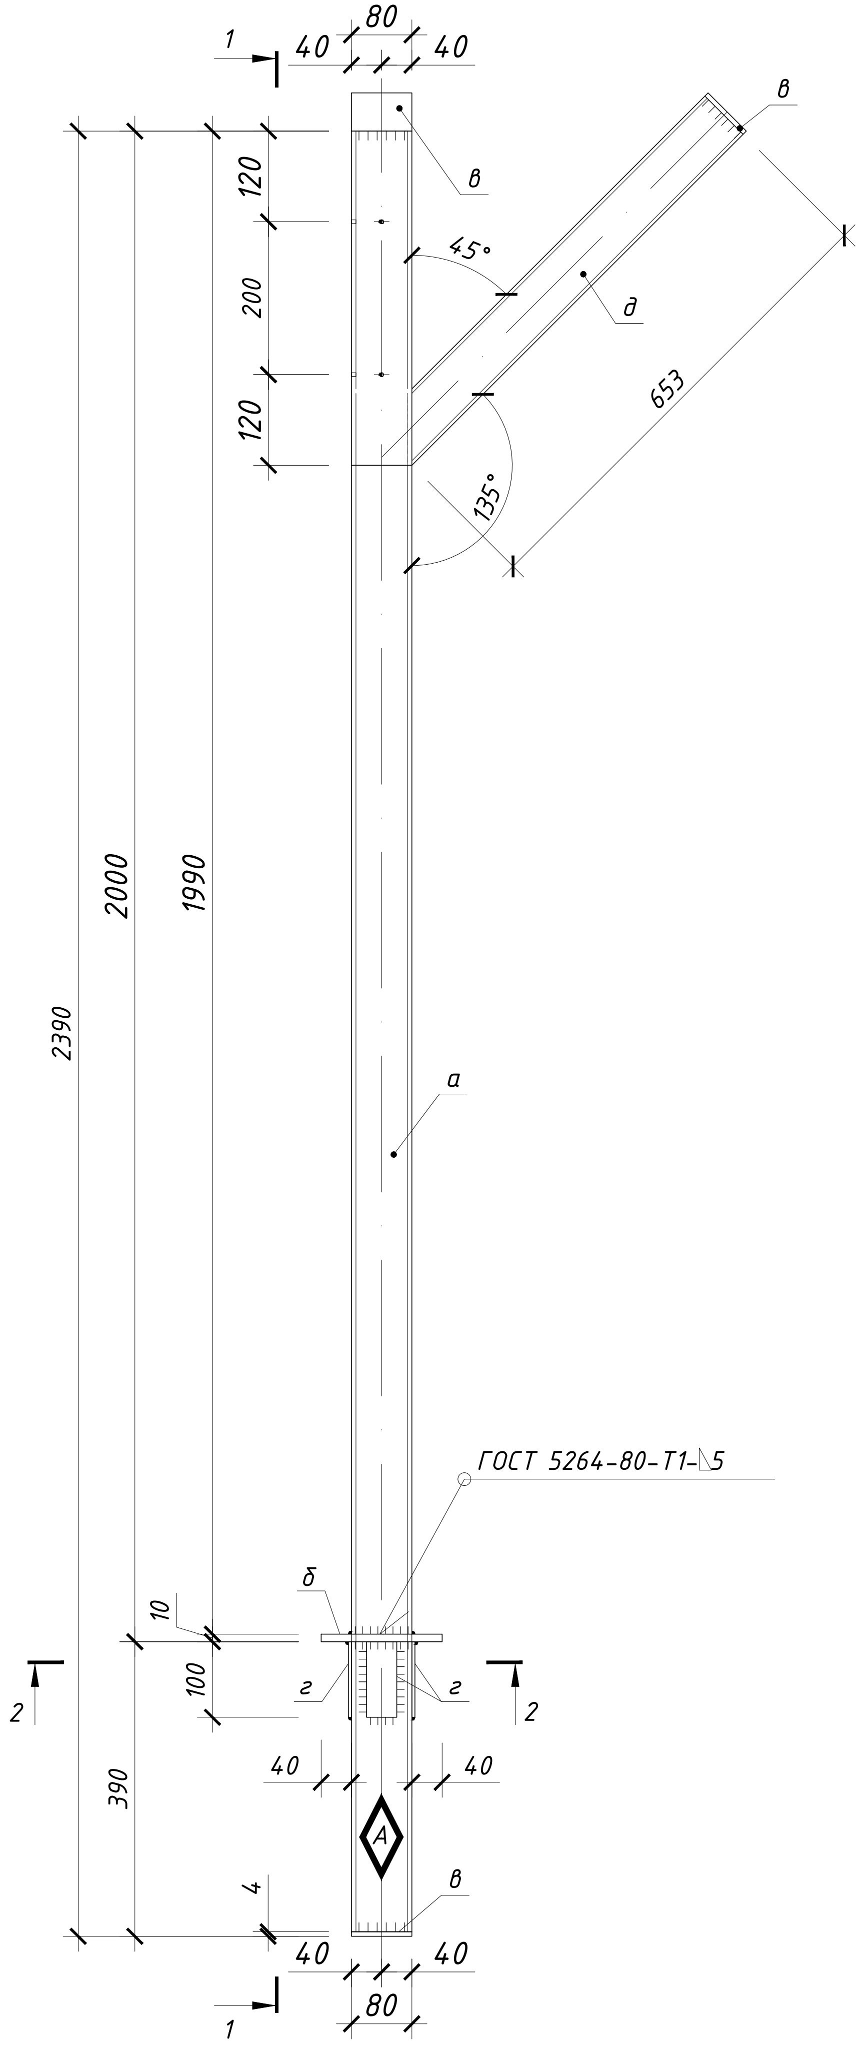
1
40
80
40
в
120
200
120
45°
д
653
135°
2390
2000
1990
а
ГОСТ 5264-80-Т1-◺5
б
10
100
г
г
2
2
390
40
40
A
в
4
40
40
80
1

1-1

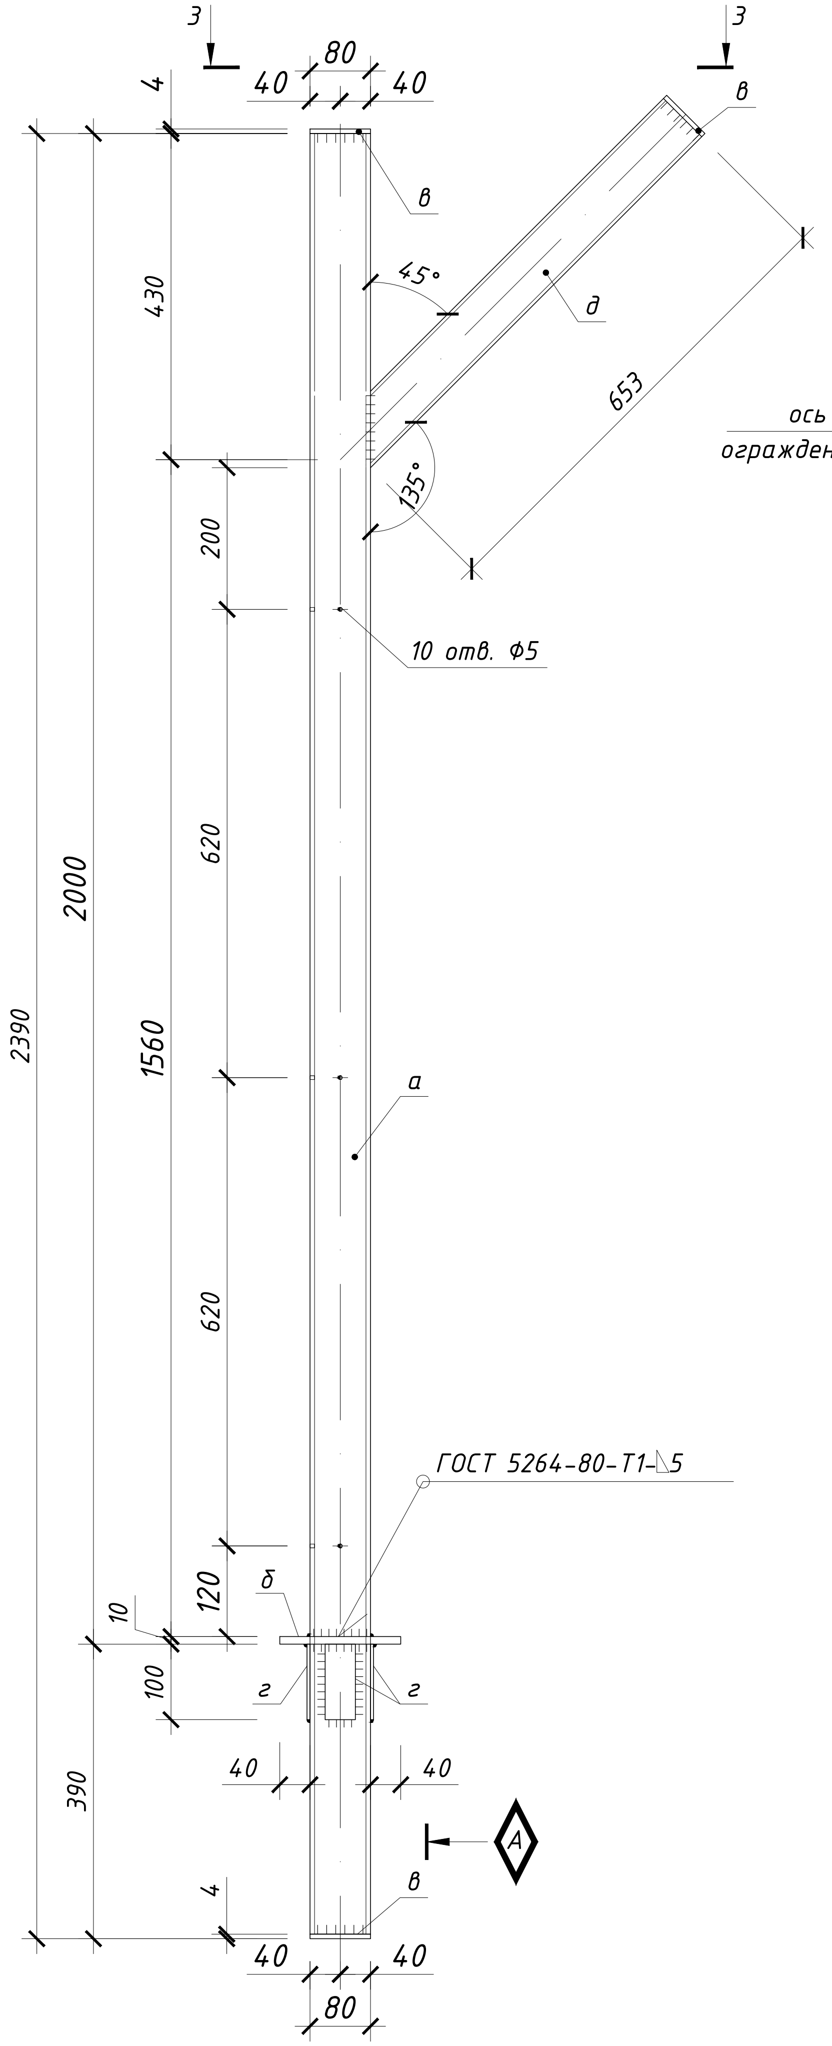
3
3
4
40
80
40
в
в
45°
д
653
135°
430
200
10 отв. Φ5
2000
2390
620
1560
а
620
ГОСТ 5264-80-Т1-◺5
120
10
б
100
г
г
390
40
40
A
4
в
40
40
80

2-2

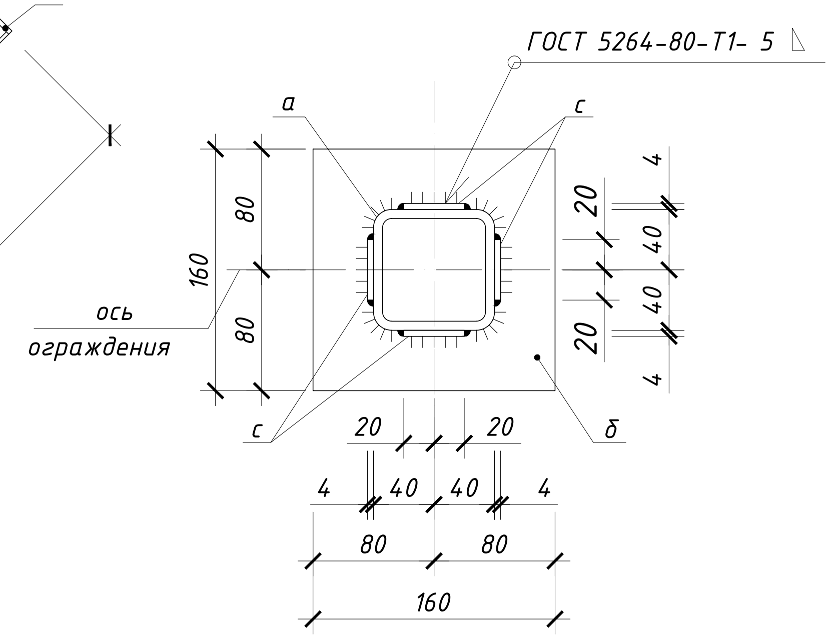
ГОСТ 5264-80-Т1- 5 ◺
а
с
80
160
80
ось ограждения
20
4
40
40
20
4
с
б
20
20
4
40
40
4
80
80
160

Позиция "б"

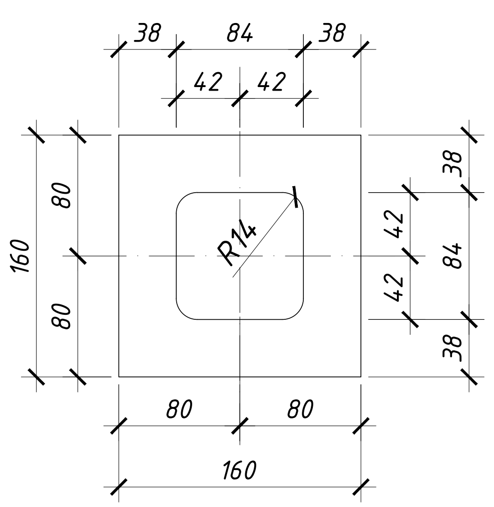
38
84
38
42
42
80
160
80
R14
38
42
84
42
38
80
80
160

3-3

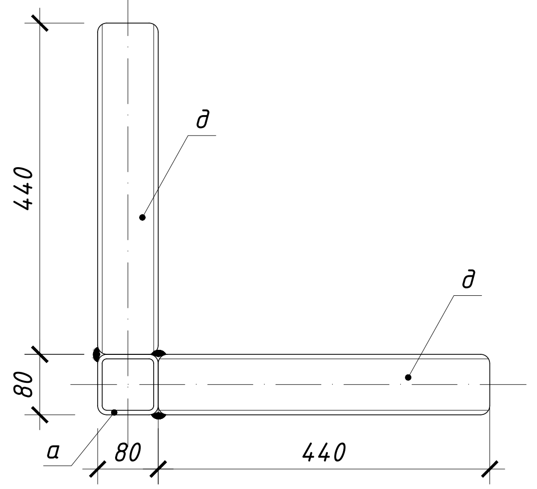
440
д
д
80
а
80
440

Деталь-1 срезки подкоса (поз. д)

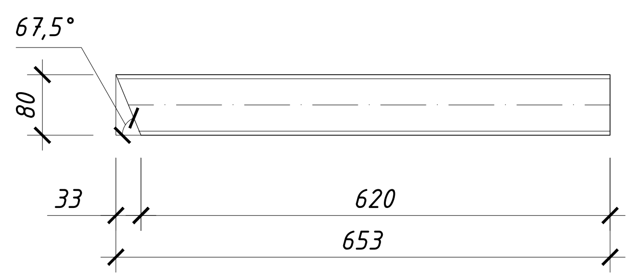
67,5°
80
33
620
653

Спецификация элементов на одну марку

Марка поз.	Обозначение	Наименование	Кол. шт.	Масса ед.кг	Примечание
Ст3		Стойка ограждения Ст-3		37.95	вес на 1 стойку
а		Гн.пр 80x80x4 ГОСТ 30245-2003 / С255-ГК ГОСТ 27772-2015 L=2390мм	1	22.3	22.3
б		Лист Б-ПН-10x160x160 ГОСТ 19903-2015 / С245-ГК ГОСТ 27772-2015	1	2,01	2,01
в		Лист Б-ПН-4x80x80 ГОСТ 19903-2015 / С245-ГК ГОСТ 27772-2015	4	0,20	0,8
г		Лист Б-ПН-4x40x124 ГОСТ 19903-2015 / С245-ГК ГОСТ 27772-2015	4	0,16	0,64
д		Гн.пр 80x80x4 ГОСТ 30245-2003 / С255-ГК ГОСТ 27772-2015 L=653мм	2	6.10	12.20
		Материалы:			
		Окраска металлоконструкций масляной краской за 2 раза			1,31м²

Примечания:
1. Сварку вести электродами Э42А ГОСТ 9467-75.
2. Конструкция должна быть покрыта масляной краской за 2 раза по грунтовке.
3. Элемент "г" следует приварить к "а" в первую очередь.
4. Деталь-1 - деталь срезки подкоса (поз. д)
5. Крепления стойки смотри лист Фундамента ФМЛ1.

◊A - Знак ориентации. Нанести несмываемой краской!

● Отверстие для болта
◈ Болт постоянный, нормальной точности
♦ Болт временный, нормальной точности
ıııııııııı Сварной шов заводской
××××× Сварной шов монтажный

Рев	Дата	Назначение ревизии	Проверил	Утвердил
A1	09.09.2026	Выпущено для строительства		
R1	28.07.2026	Выпущено для рассмотрения		

ЗАКАЗЧИК:
ГЕНЕРАЛЬНЫЙ ПОДРЯДЧИК:
ПОДРЯДЧИК:
ГЕНЕРАЛЬНЫЙ ПРОЕКТИРОВЩИК:

EWE0426-MGL1-STR-054-DRW-770510-A1

«СТРОИТЕЛЬСТВО НОВЫХ НИТОК (УЧАСТКОВ) ГАЗОПРОВОДОВ «ГАЗЛИ - САРИМОЙ» И «АКЧАЛОК - ГАЗЛИ - НУКУС» ОБЩЕЙ ПРОТЯЖЕННОСТЬЮ НЕ МЕНЕЕ 275 КМ».

Изм.	Кол.уч.	Лист	№ док.	Подпись	Дата
ГИП		Кирпичников С.			09.09.26
Нач.отд.		Каршиев А.			09.09.26
Исполн.		Юлдашев Ж.			09.09.26
Н.контр		Кирпичников С.			09.09.26

ГАЗОПРОВОД "ГАЗЛИ-САРИМОЙ" (54 КМ)
Линейный крановый узел DN1000 КУП-D8

Стадия	Лист	Листов
РП	1	1

Стойка ограждения Ст3.

ООО "EAST-WEST Engineering"
г. Ташкент 2026г.

Взам. инв. №
Подпись и дата
Инв.№ подл.

Формат / Format A4X3