Панель ограждения П2 м 1:25.

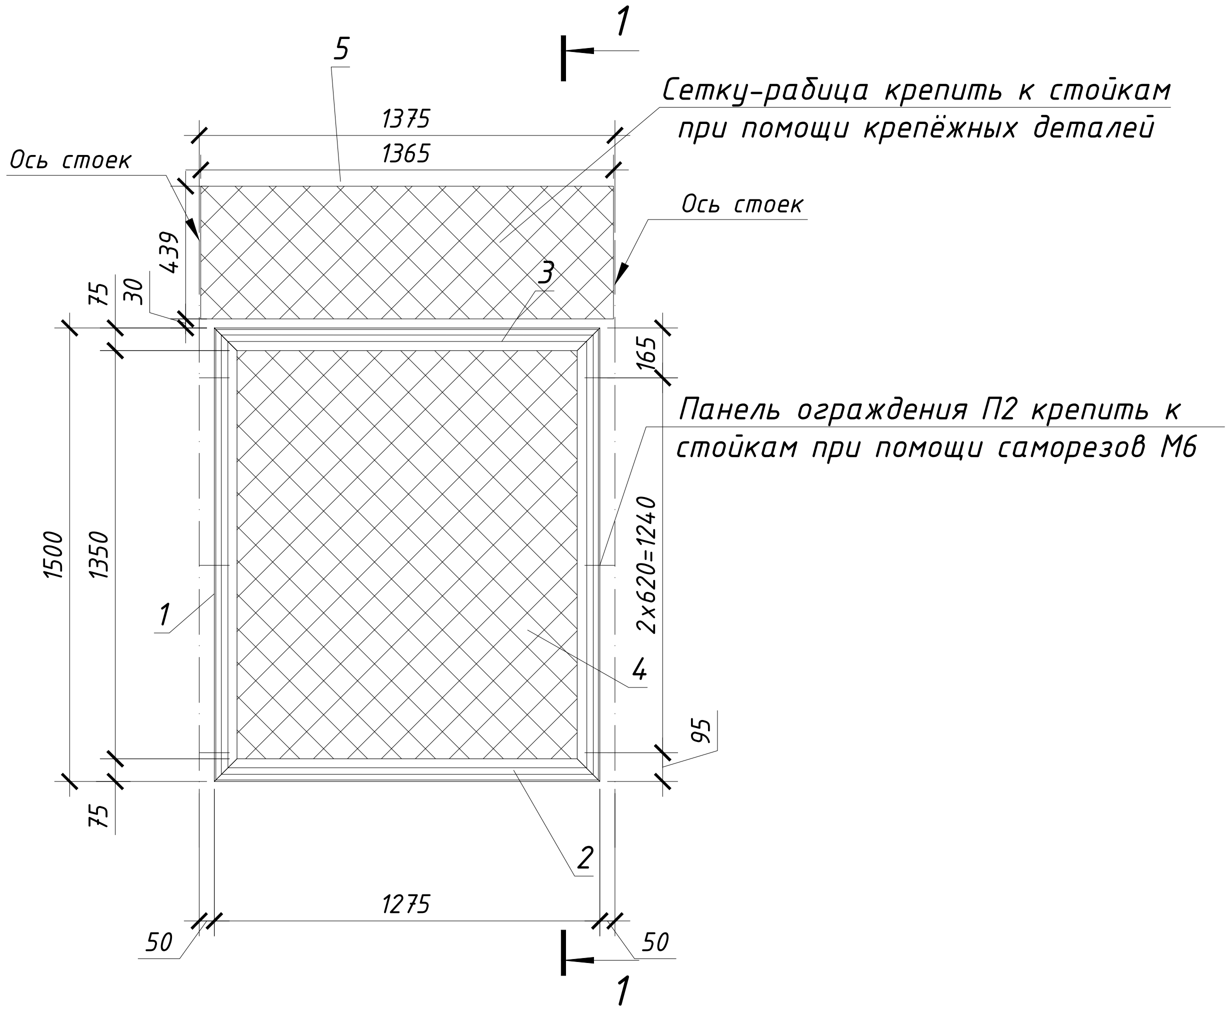

Сетку-рабица крепить к стойкам при помощи крепёжных деталей

Панель ограждения П2 крепить к стойкам при помощи саморезов М6

Разрез 1-1 м 1:50.

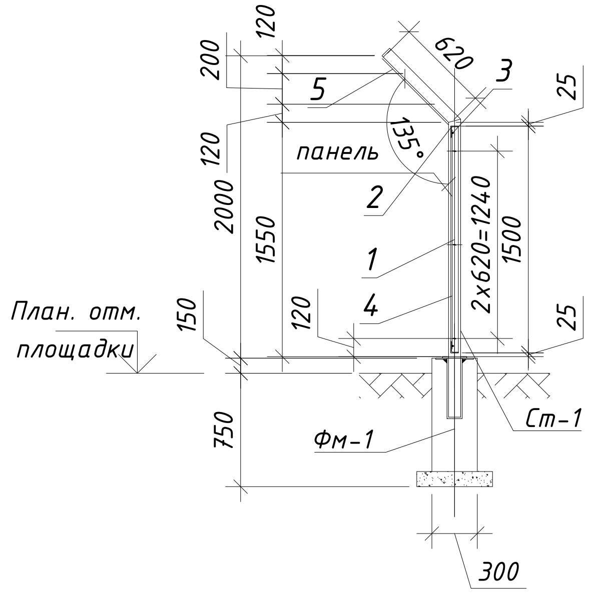

Спецификация расхода материалов

Марка Поз.	Обозначение	Наименование	Кол. шт.	Масса ед.кг.	Примечание
П-2		Панель ограждения П2		34,10	вес на 1 шт.
1	ГОСТ 8510-93, Сталь С235	L75x50x5 L=1500	2	7.19	14.37
2	ГОСТ 8510-93, Сталь С235	L75x50x5 L=1275	2	6.11	12.22
3	ГОСТ 34028-2016	Арматура Φ6.0 А240 Lобщ=5180	1	0.222 кг/м.п	1.15
4	ГОСТ 5336-80*	Сетка рабица №50-3.0,размером			
		1230 x 1450мм; S=1.78м2	1	2,42 кг/м2	4.31
5	ГОСТ 5336-80*	Сетка рабица №50-3.0,размером			
		620 x 1365мм; S=0.85м2	1	2,42 кг/м2	2.05
		Материалы:			
		Окраска металлоконструкций масляной краской за 2 раза			1,40м²

Примечания:

1. Сварку вести электродами Э42А ГОСТ9467-75.
2. Конструкция должна быть покрыта масляной краской за 2 раза по грунтовке.

А1	09.09.2026	Выпущено для строительства		
R1	28.07.2026	Выпущено для рассмотрения		
Рев	Дата	Назначение ревизии	Проверил	Утвердил

ЗАКАЗЧИК: UTG UZTRANSGAZ «TRANSGAZINJINIRING»

ГЕНЕРАЛЬНЫЙ ПОДРЯДЧИК: UET UZBEKENERGOTAMIR

ПОДРЯДЧИК: PBG Pro Build Generation

ГЕНЕРАЛЬНЫЙ ПРОЕКТИРОВЩИК: EAST WEST ENGINEERING

EWE0426-MGL1-STR-054-DRW-770512-A1

«СТРОИТЕЛЬСТВО НОВЫХ НИТОК (УЧАСТКОВ) ГАЗОПРОВОДОВ «ГАЗЛИ - САРИМОЙ» И «АКЧАЛОК - ГАЗЛИ - НУКУС» ОБЩЕЙ ПРОТЯЖЕННОСТЬЮ НЕ МЕНЕЕ 275 КМ».

Изм.	Кол.уч.	Лист	№ док.	Подпись	Дата
ГИП		Кирпичников С.			09.09.26
Нач.отд.		Каршиев А.			09.09.26
Исполн.		Юлдашев Ж.			09.09.26
Н.контр		Кирпичников С.			09.09.26

ГАЗОПРОВОД "ГАЗЛИ-САРИМОЙ" (54 КМ)
Линейный крановый узел DN1000 КУП-D8

Стадия	Лист	Листов
РП	1	1

Панель ограждения П2

EAST WEST ENGINEERING

ООО "EAST-WEST Engineering"
г. Ташкент 2026г.

Формат / Format A3

Взам. инв. №

Подпись и дата

Инв.№ подл.