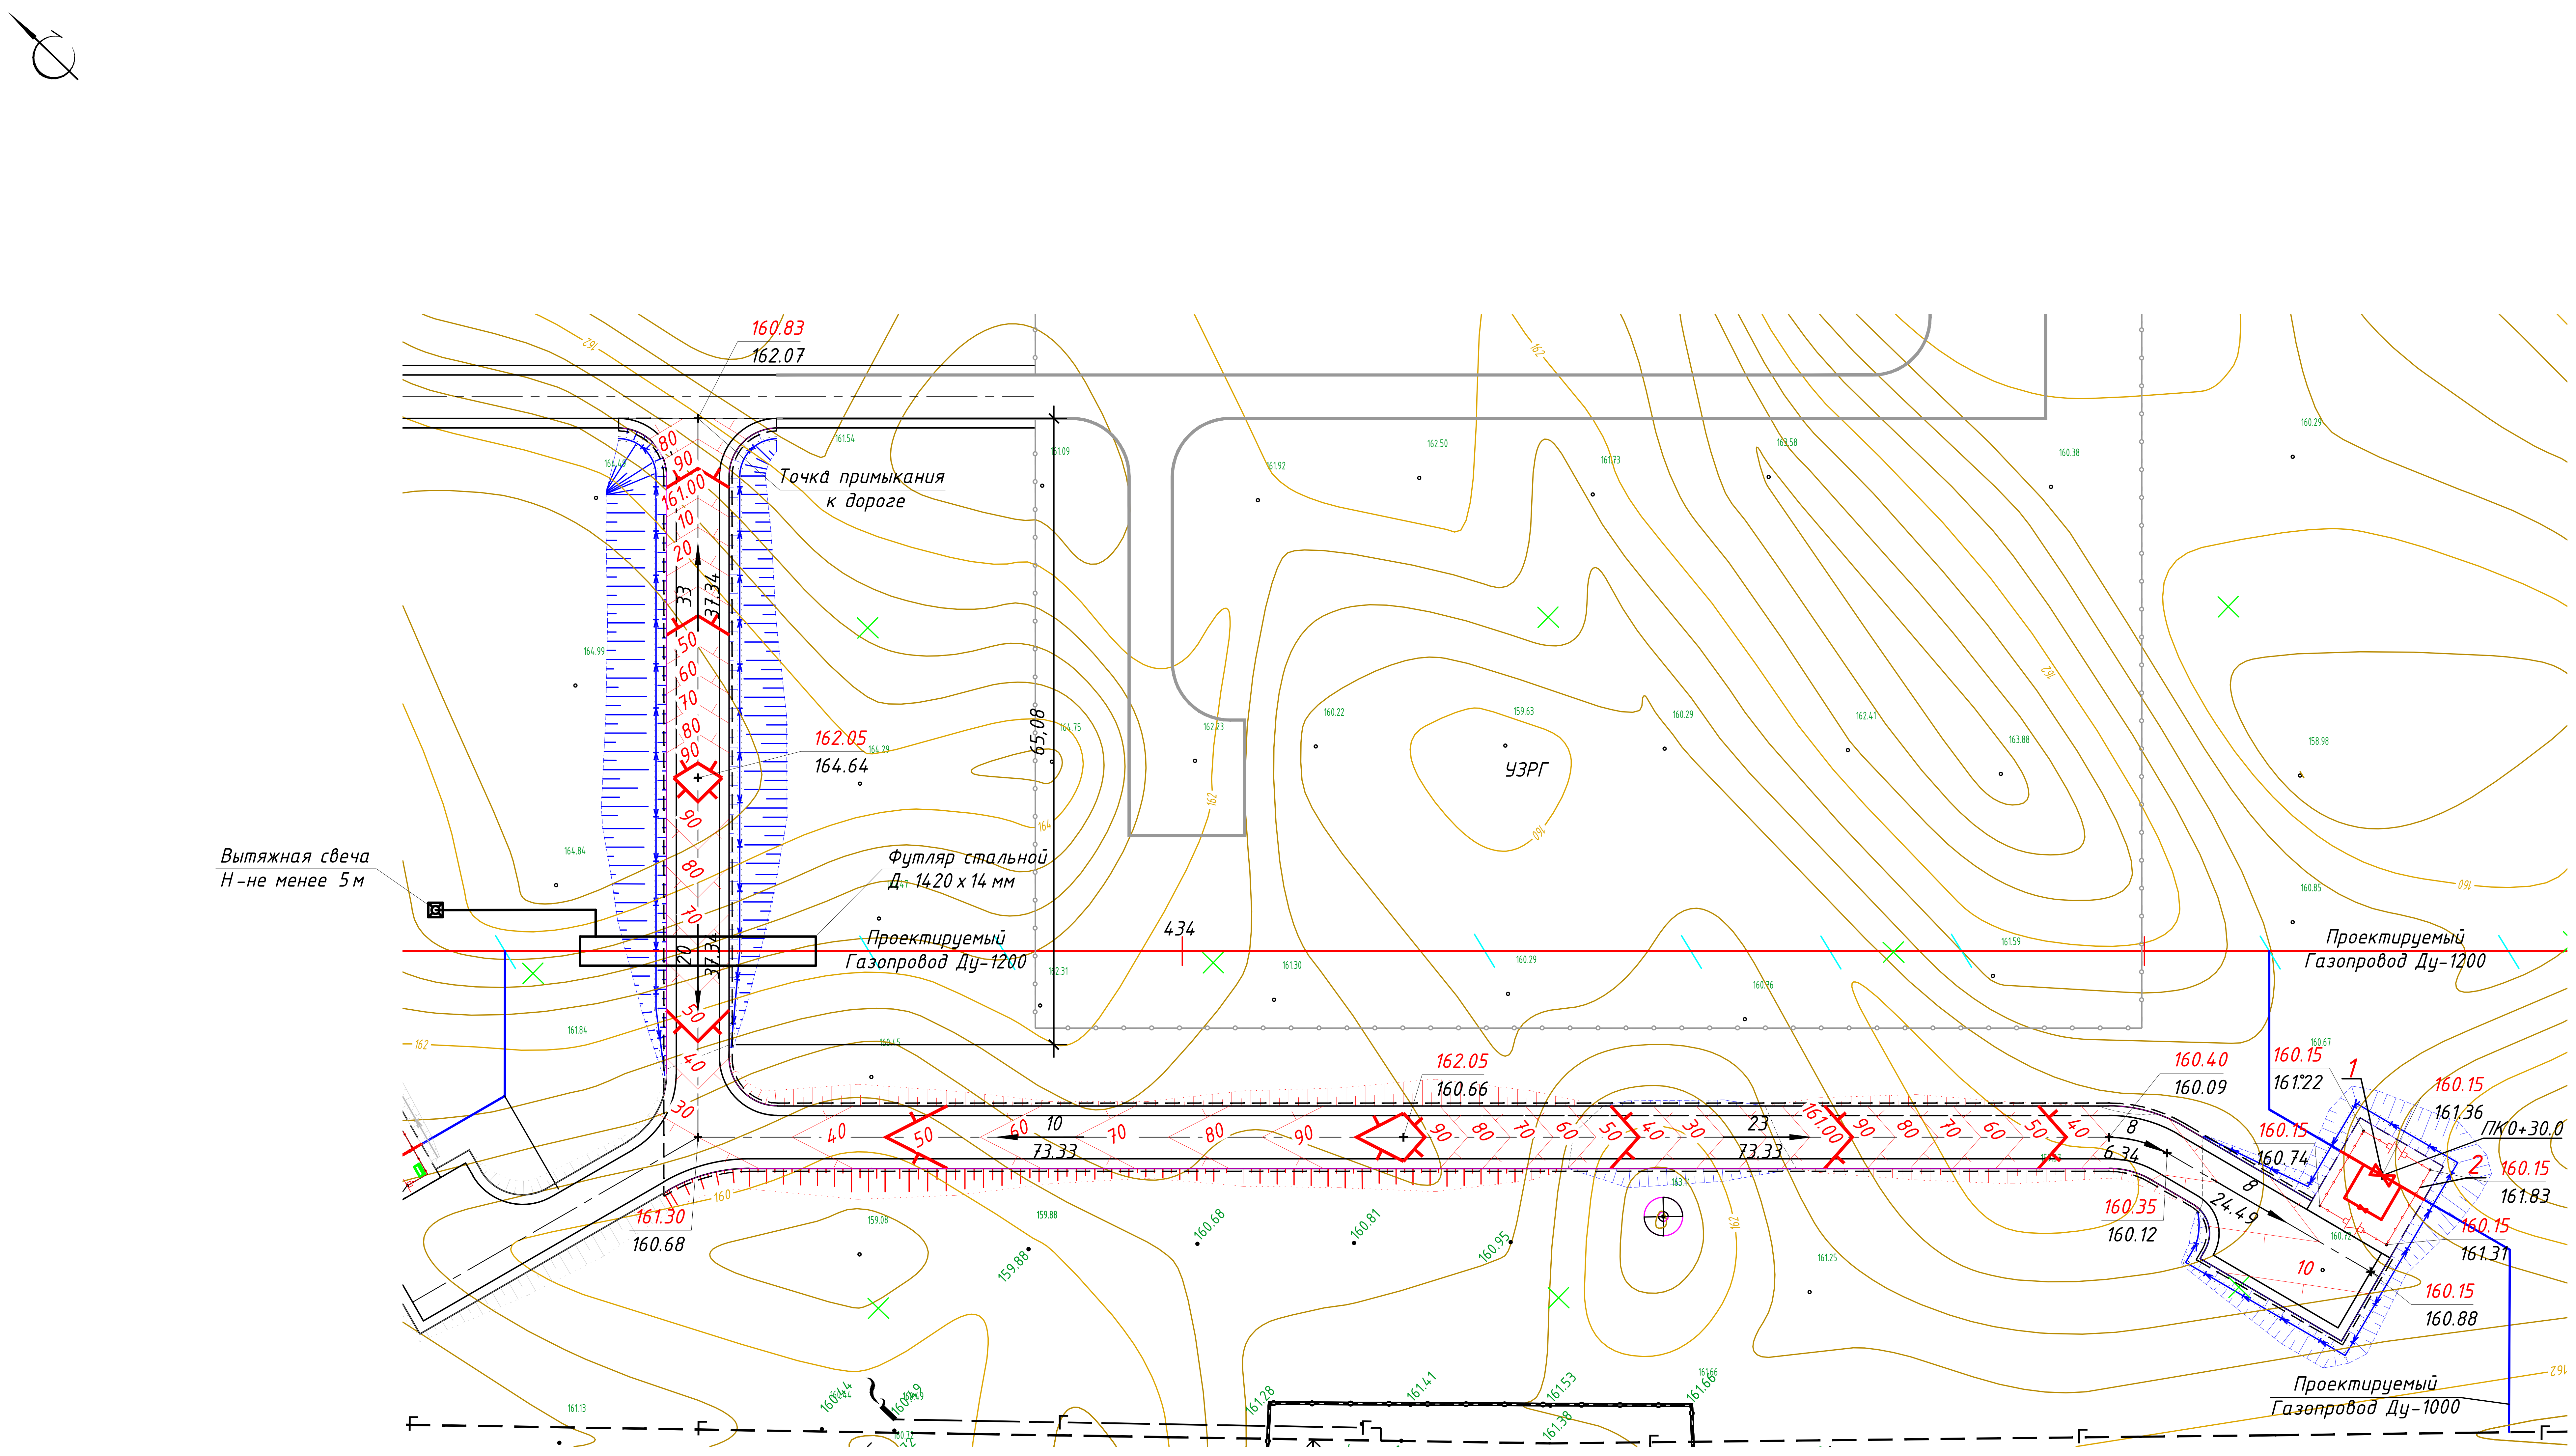

Экспликация зданий и сооружений

Номер на плане	Наименование	Примечание
1	Крановый узел Ду 1000	
2	Ограждение сетчатое	

Условные обозначения

	Ограждение
	Калитка
	Граница планировки
	Существующий газопровод
	Проектируемый газопровод ДУ-1200
	Проектируемый газопровод ДУ-1000
160.15 161.22	Проектная отметка Существующая отметка
10	Проектные красные горизонтали
	Откосы насыпи
	Откосы выемки
	Водоотводная канава

Примечания:

При составлении настоящего чертежа были использованы :
1. Материалы топографо-геодезической съемки, предоставлены АО "O'ZLITINEFTGAZ".
2. Система координат местная. Высотные отметки даны в Балтийской системе.
3. Размеры даны в метрах.
4. Площадка кранового узла КУП-D10 привязана линейно к пикету ПК 0+30.0.
5. Данный лист смотри совместно с листами разделов PIL, PRE, ELE, STR, SYS.
6. Детальный план кранового узла см. EWE0426-MGL1-PRE-054-DRW-790203.
7. Защита Пересечения проектной дороги с проектным газопроводом предусмотрена в техническом решении №2 в рамках авторского надзора.

Рев.	Дата	Назначение ревизии	Проверил	Утвердил
A2	07.10.2026	Выпущено для строительства		
A1	10.09.2026	Выпущено для строительства		
R1	28.07.2026	Выпущено для рассмотрения		

ЗАКАЗЧИК: UTG UZTRANSGAZ
ГЕНЕРАЛЬНЫЙ ПОДРЯДЧИК: UET UZBEKENERGOTAMIR
ПОДРЯДЧИК: PBG Pro Build Generation
ГЕНЕРАЛЬНЫЙ ПРОЕКТИРОВЩИК: EAST WEST ENGINEERING

EWE0426-MGL1-GLT-054-DRW-790103-A2

«СТРОИТЕЛЬСТВО НОВЫХ НИТОК (УЧАСТКОВ) ГАЗОПРОВОДОВ «ГАЗЛИ - САРИМОЙ» И «АКЧАЛОК - ГАЗЛИ - НУКУС» ОБЩЕЙ ПРОТЯЖЕННОСТЬЮ НЕ МЕНЕЕ 275 км».

Изм.	Кол.уч.	Лист	№ док.	Подпись	Дата
ГИП		Кирпичников С.			10.2026
Нач.отд.		Нигманова Н.			10.2026
Исполн.		Горлова О.			10.2026
Н.контр		Кирпичников С.			10.2026

ГАЗОПРОВОД «ГАЗЛИ-САРИМОЙ» (54 км)

Генеральный план и транспорт.

Стадия	Лист	Листов
РД	1	1

КУП-D10.
План организации рельефа
М 1:500

ООО "EAST-WEST Engineering"
г. Ташкент 2026г.

Формат / Format A3x3

Взам. инв. №
Подпись и дата
Инв.№ подл.