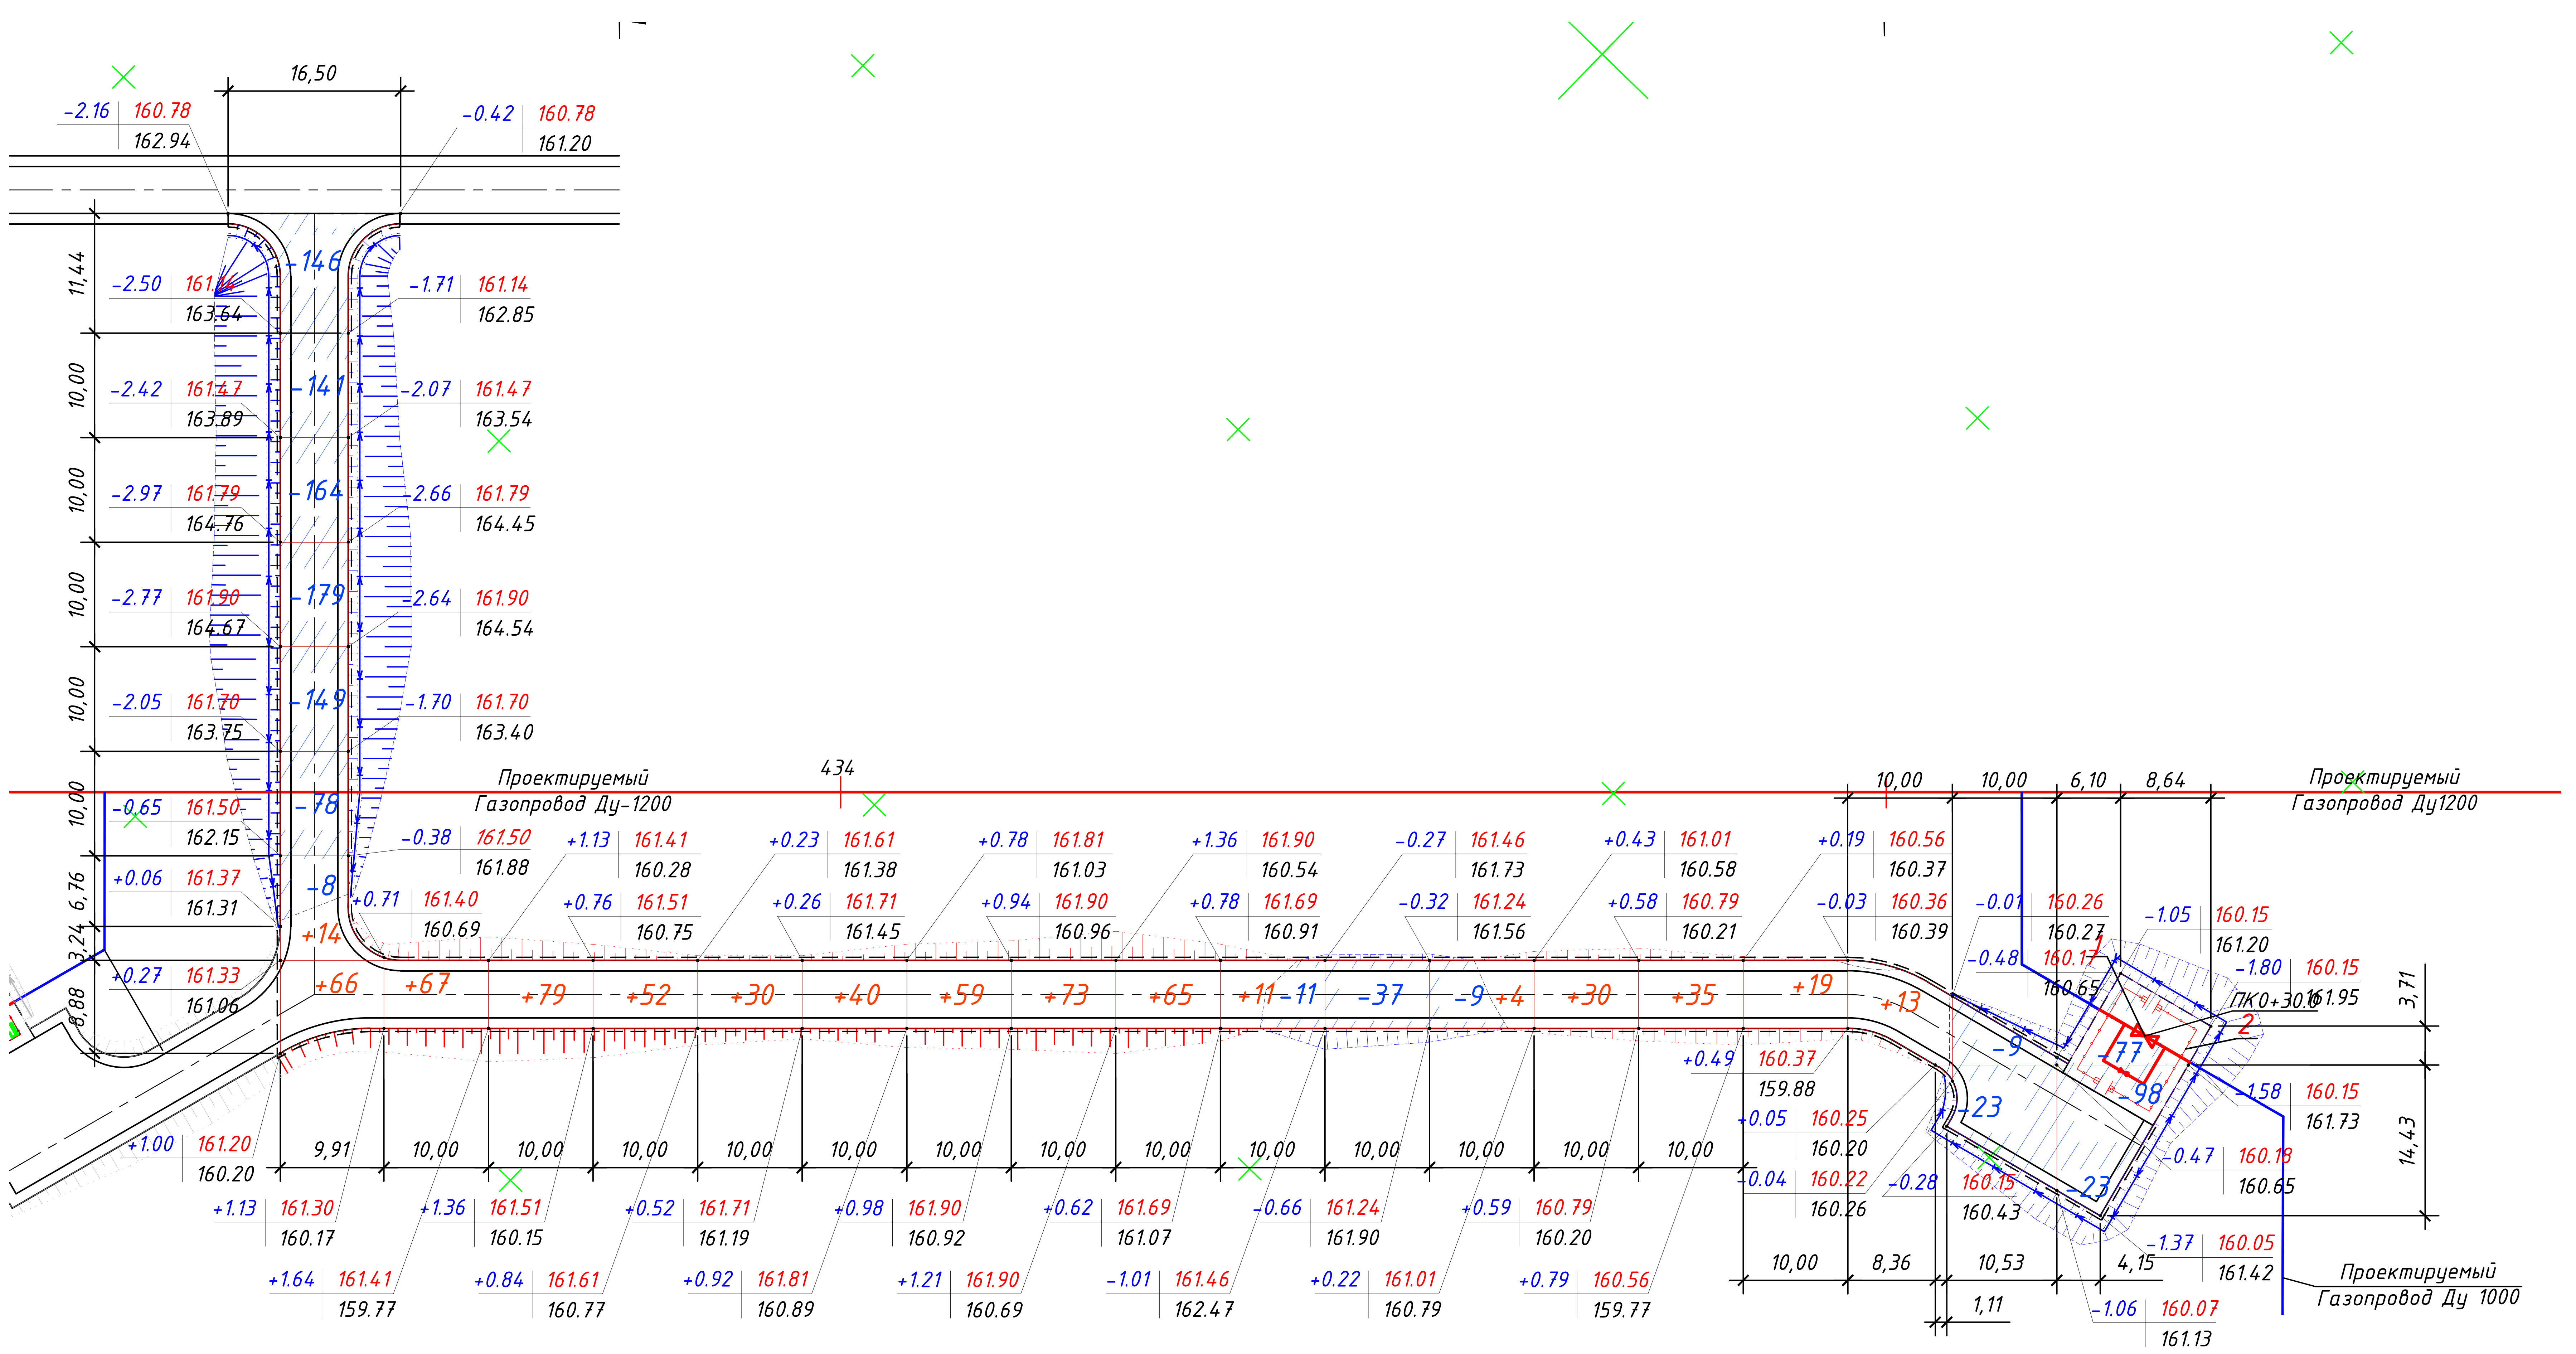

Ведомость объемов земляных масс

Наименование грунта	Количество, м^3		Примечание
	Насыпь (+)	Выемка (–)	
1. Грунт планировки территории	657	1151	
2. Вытесненный грунт, в т.ч. при устройстве:			
а) автодорожных покрытий		541	
б) покрытий площадок		9.5	
в) водоотводной канавы		84	
г) плодородной почвы на участках насыпи			
д) плодородной почвы на участках выемки			
3. Замена растительного грунта на участках насыпи			
4. Грунт для устройства откосов насыпи	80		
5. Грунт для устройства откосов выемки		280	
6. Поправка на уплотнение	74		
Всего пригодного грунта	811	2060.5	
7. Избыток пригодного грунта	1249.5*		
8. Плодородный грунт, всего в т.ч.:		557.1	
а) Используемый для озеленения территории			
б) Избыток плодородного грунта	557.1		
(рекультивация земель)			
9. Итого перерабатываемого грунта	2617.6	2617.6	

* С учетом плодородного грунта.

** В карьере.

Общая площадь картограммы = 1857 м2

Условные обозначения

+67	объем насыпи в м^3
-146	объем выемки в м^3
+0.47 160.18 / 160.65	рабочая отм. | проектная отм. / отм.сущ.рельефа
┬┬┬┬┬	Откосы насыпи
┴┴┴┴┴	Откосы выемки

Итого,м3	Насыпь (+)	+80	+67	+79	+52	+30	+40	+59	+73	+65	+11	--	+4	+30	+35	+19	+13	--	--	Всего,м3	+657
	Выемка (-)	-864	-1	--	--	--	--	--	--	--	-11	-37	-9	--	--	--	--	-35	-194		-1151

Общая площадь насыпи = 949 м2
Общая площадь выемки = 902 м2
Общая площадь 0-области = 6 м2
Общая площадь картограммы = 1857 м2

Примечания:

При составлении настоящего чертежа были использованы :
1. Сетка картограммы привязана линейно к пикету ПК0+30.0.
2. Сетка квадратов объёмы земляных масс разбита на ячейки размерами 10х10м.
3. Производство земляных работ вести в соответствии с требованиями ҚР 02.01.

Рев.	Дата	Назначение ревизии	Проверил	Утвердил
А1	10.09.2026	Выпущено для строительства		
R1	28.07.2026	Выпущено для рассмотрения		

ЗАКАЗЧИК: UTG UZTRANSGAZ
ГЕНЕРАЛЬНЫЙ ПОДРЯДЧИК: UET UZBEKENERGOTAMIR
ПОДРЯДЧИК: PBG Pro Build Generation
ГЕНЕРАЛЬНЫЙ ПРОЕКТИРОВЩИК: EAST WEST ENGINEERING

EWE0426-MGL1-GLT-054-DRW-790104-A1

«СТРОИТЕЛЬСТВО НОВЫХ НИТОК (УЧАСТКОВ) ГАЗОПРОВОДОВ «ГАЗЛИ - САРИМОЙ» И «АКЧАЛОК - ГАЗЛИ - НУКУС» ОБЩЕЙ ПРОТЯЖЕННОСТЬЮ НЕ МЕНЕЕ 275 км».

Изм.	Кол.уч.	Лист	№док.	Подпись	Дата
ГИП		Схабицкий А.			09.2026
Нач.отд.		Нигманова Н.			09.2026
Исполн.		Горлова О.			09.2026
Н.контр		Схабицкий А.			09.2026

ГАЗОПРОВОД «ГАЗЛИ-САРИМОЙ» (54 км)
Генеральный план и транспорт.

Стадия	Лист	Листов
РД	1	1

КУП-D10.
План земляных масс
М 1:500

EAST WEST ENGINEERING
ООО "EAST-WEST Engineering"
г. Ташкент 2026г.

Взам. инв. №
Подпись и дата
Инв.№ подл.

Формат / Format A3x3