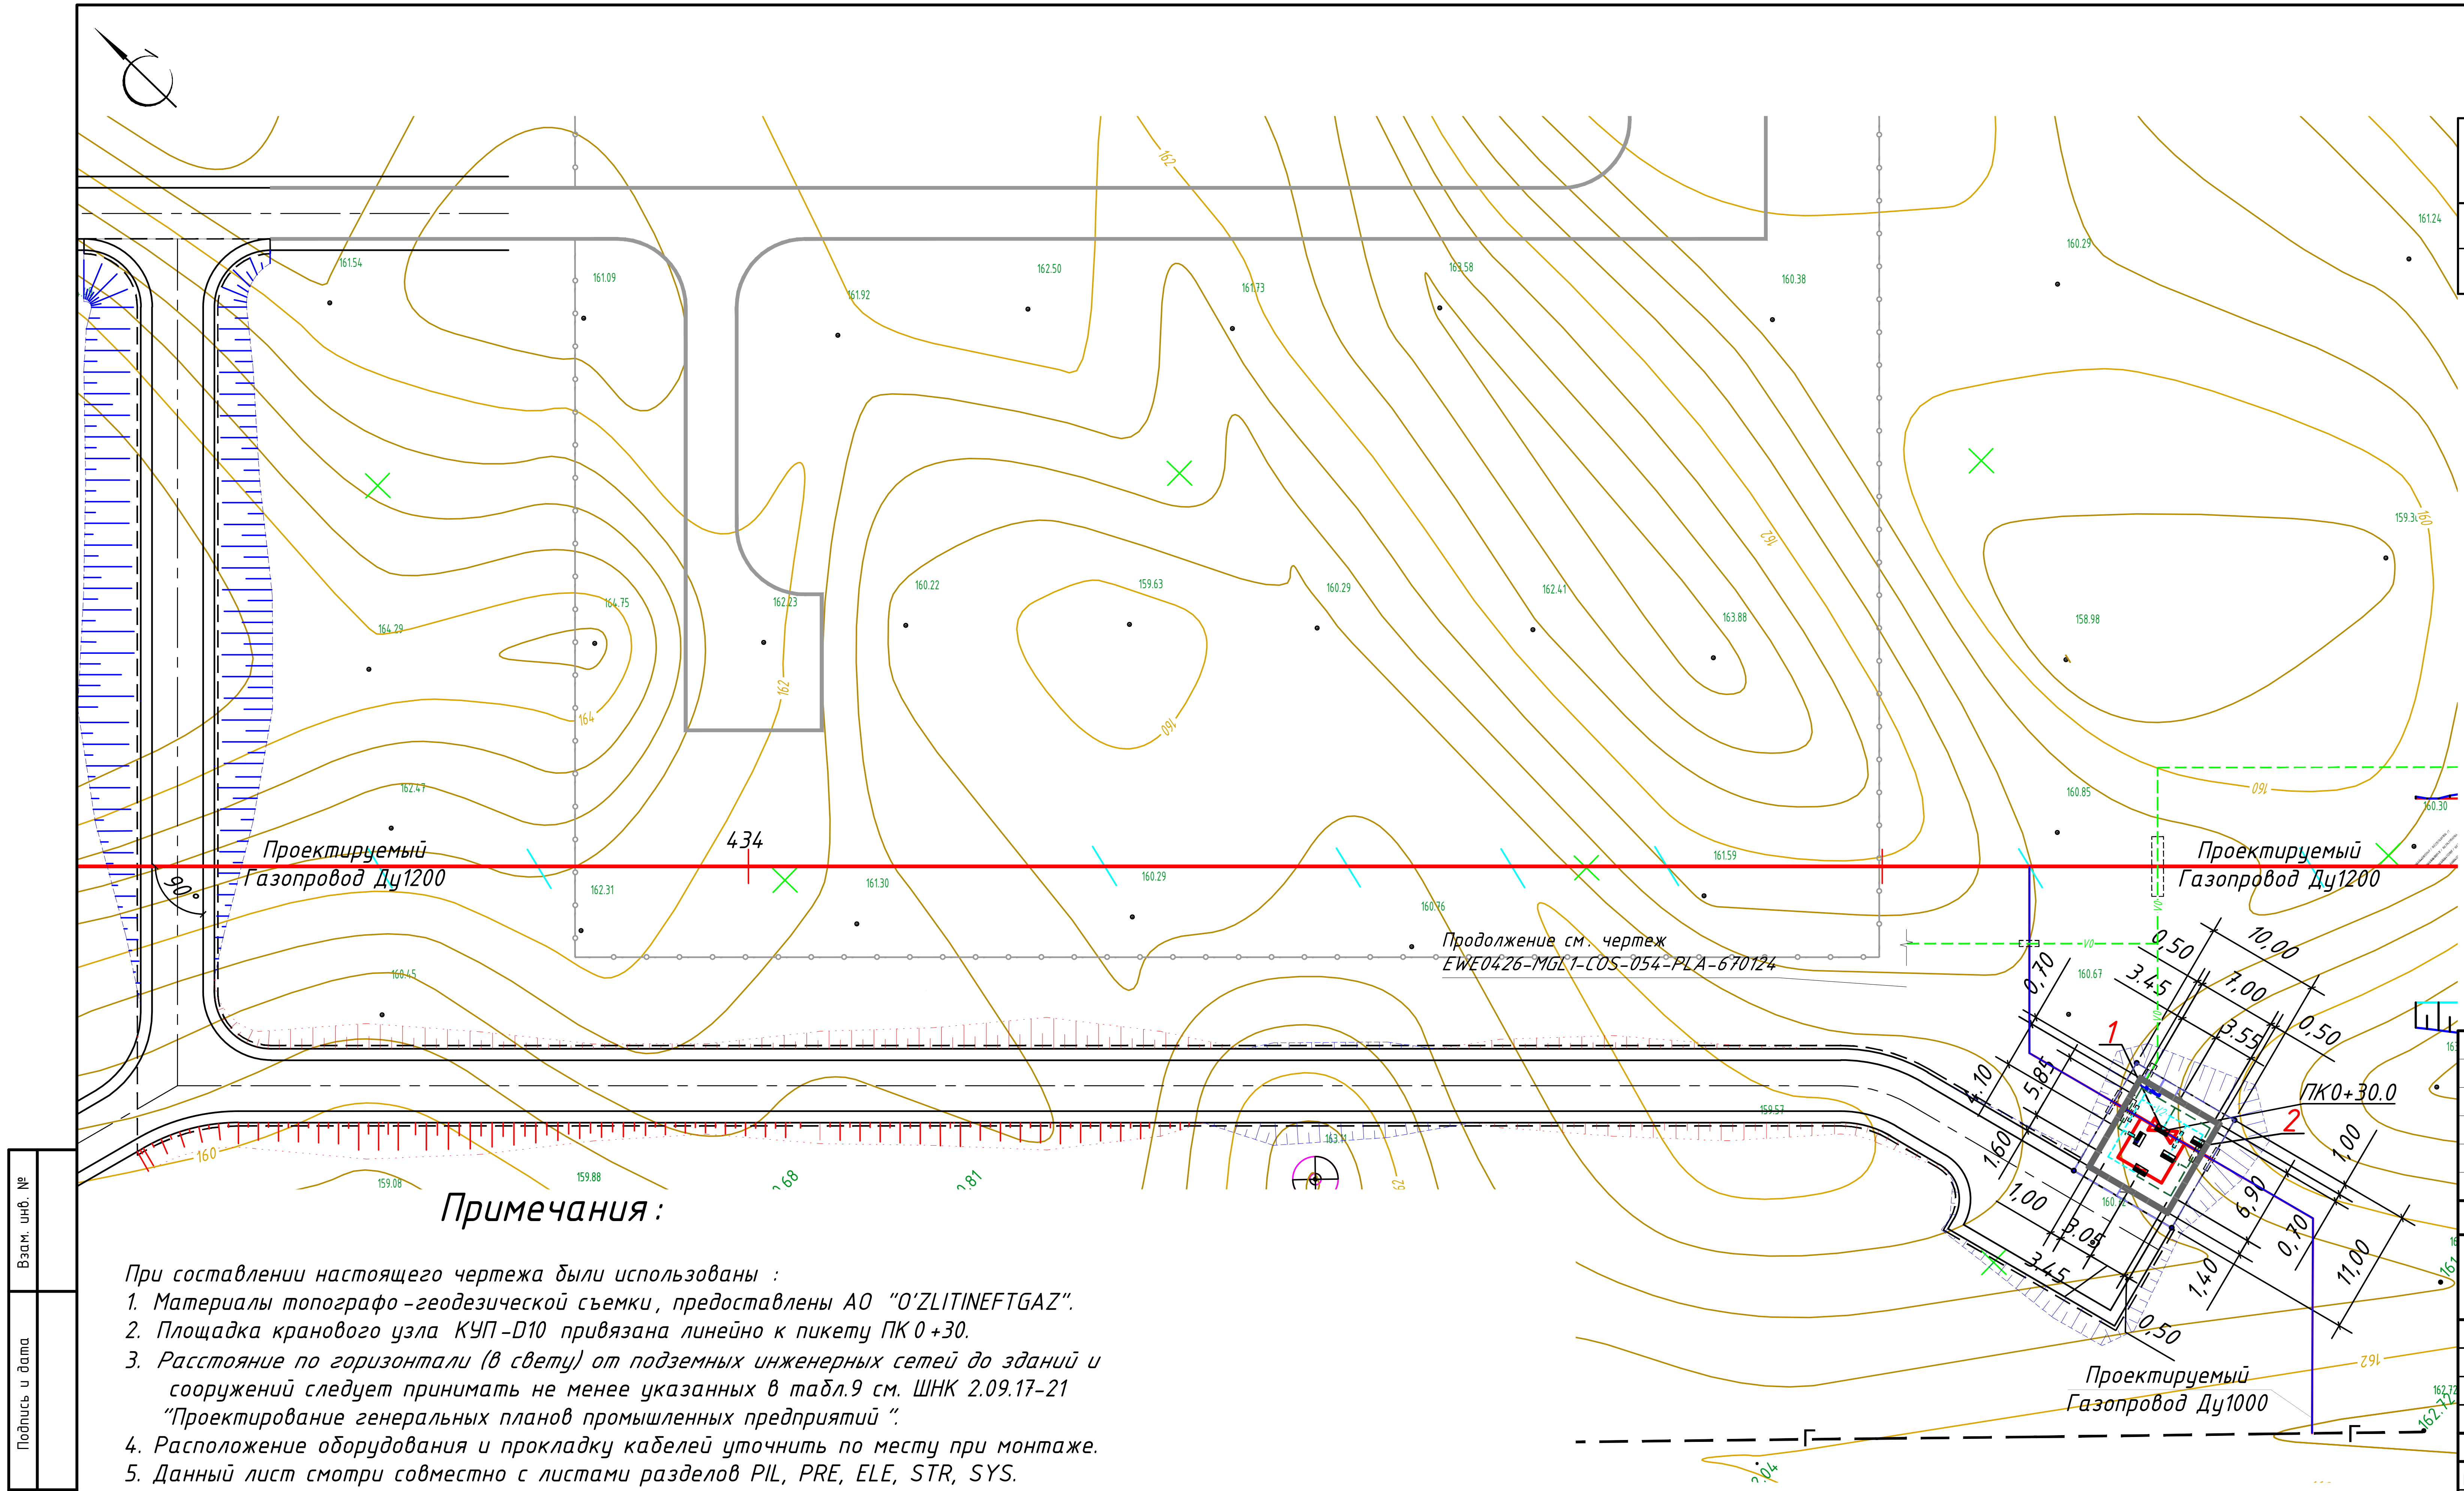

434
Проектируемый Газопровод Ду1200
Проектируемый Газопровод Ду1200
Продолжение см. чертеж EWE0426-MGL1-COS-054-PLA-670124
ПК0+30.0
1
2
10,00
7,00
0,50
3,45
3,55
0,50
0,70
4,10
5,85
1,60
1,00
3,05
3,45
0,50
1,40
0,70
6,90
1,00
11,00
Проектируемый Газопровод Ду1000
160
162

Экспликация зданий и сооружений

Номер на плане	Наименование	Примечание
1	Крановый узел Ду 1000	
2	Ограждение сетчатое	

Условные обозначения

—г—г—	Существующий газопровод
—	Проектируемый газопровод ДУ-1200
—	Проектируемый газопровод ДУ-1000
●	Вертикальный заземлитель Ф 16
– – –	Полоса заземления 4х40
– – –	Гибкий провод
⬚	Стальная труба
▭	Шкаф телемеханики (ШТМ)
▬	Датчики давления
– –V2– –	Проектный кабель КИПиА в траншее
– –V2– –	Проектный кабель КИПиА в ПНД трубе
– –V0– –	Проектируемый волоконно-оптический кабель в траншее
– –V0– –	Проектируемый волоконно-оптический кабель в трубе

Примечания:

При составлении настоящего чертежа были использованы :

1. Материалы топографо-геодезической съемки, предоставлены АО "O'ZLITINEFTGAZ".
2. Площадка кранового узла КУП-D10 привязана линейно к пикету ПК 0+30.
3. Расстояние по горизонтали (в свету) от подземных инженерных сетей до зданий и сооружений следует принимать не менее указанных в табл.9 см. ШНК 2.09.17-21 "Проектирование генеральных планов промышленных предприятий ".
4. Расположение оборудования и прокладку кабелей уточнить по месту при монтаже.
5. Данный лист смотри совместно с листами разделов PIL, PRE, ELE, STR, SYS.
6. Детальный план кранового узла см. EWE0426-MGL1-PRE-054-DRW-790203.
7. Детальный план сетей КИПиА см. EWE0426-MGL1-SYS-054-PLA-790306.
8. Детальный план сетей заземления см. EWE0426-MGL1-ELE-054-DRW-790402.
9. Детальный план ограждения см. EWE0426-MGL1-STR-054-DRW-790507.
6. Защита Пересечения проектной дороги с проектным газопроводом предусмотрена в техническом решении №2 в рамках авторского надзора.

Взам. инв. №
Подпись и дата
Инв.№ подл.

Рев.	Дата	Назначение ревизии	Проверил	Утвердил
A1	23.09.2026	Выпущено для строительства		
R1	07.08.2026	Выпущено для рассмотрения		

ЗАКАЗЧИК: UTG UZTRANSGAZ
ГЕНЕРАЛЬНЫЙ ПОДРЯДЧИК: UET UZBEKENERGOTAMIR
ПОДРЯДЧИК: PBG Pro Build Generation
ГЕНЕРАЛЬНЫЙ ПРОЕКТИРОВЩИК: EAST WEST ENGINEERING

EWE0426-MGL1-GLT-054-DRW-790105-A1

«СТРОИТЕЛЬСТВО НОВЫХ НИТОК (УЧАСТКОВ) ГАЗОПРОВОДОВ «ГАЗЛИ – САРИМОЙ» И «АКЧАЛОК – ГАЗЛИ – НУКУС» ОБЩЕЙ ПРОТЯЖЕННОСТЬЮ НЕ МЕНЕЕ 275 КМ».

Изм.	Кол.уч.	Лист	№док.	Подпись	Дата
ГИП		Схабицкий А.			09.2026
Нач.отд.		Нигманова Н.			09.2026
Исполн.		Горлова О.			09.2026
Н.контр		Схабицкий А.			09.2026

ГАЗОПРОВОД «ГАЗЛИ-САРИМОЙ» (54 КМ)
Генеральный план

Стадия	Лист	Листов
РД		1

КУП-D10.
Сводный план инженерных сетей
М 1:500

EAST WEST ENGINEERING
ООО "EAST-WEST Engineering"
г. Ташкент 2026г.

Формат / Format ####