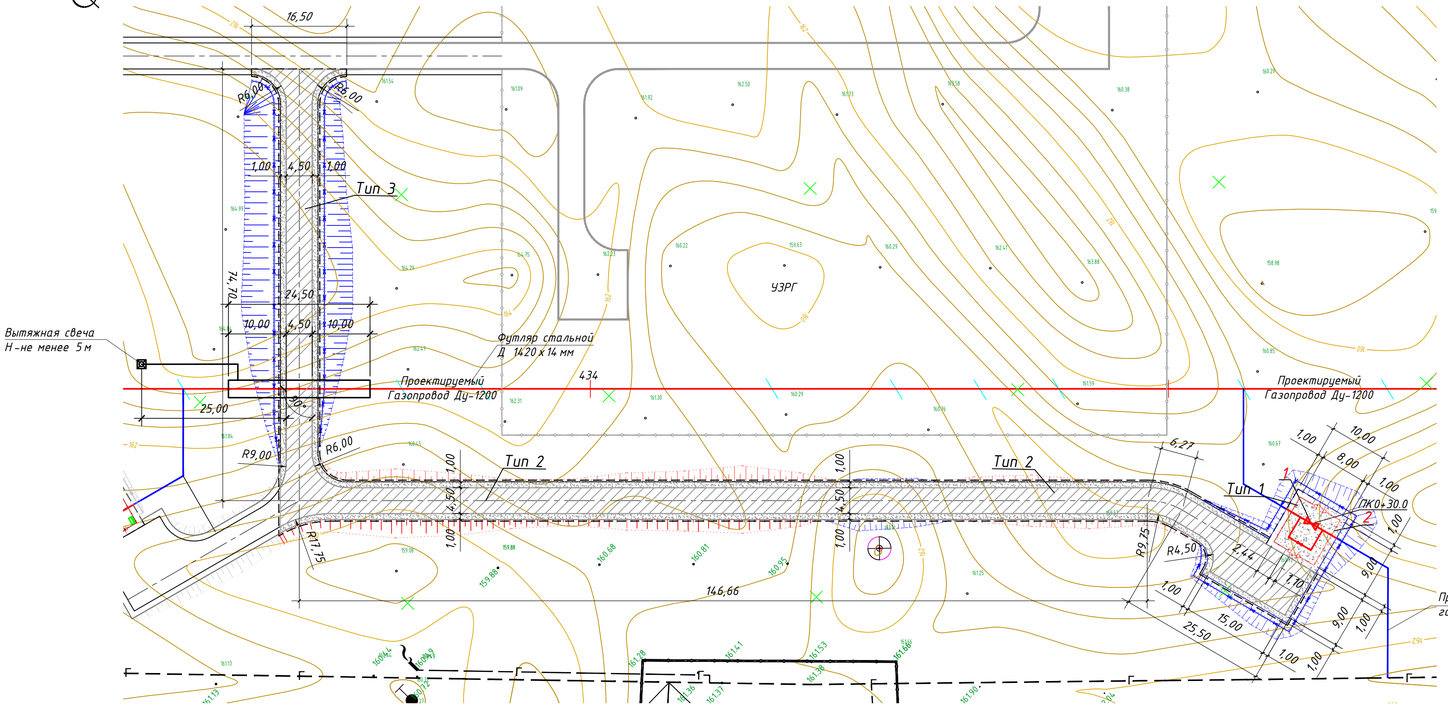


Экспликация зданий и сооружений

Номер на плане	Наименование	Примечание
1	Крановый узел Ду 1000	
2	Ограждение сетчатое	

Ведомость тротуаров, дорожек и площадок

Тип	Обозначение	Наименование	Ед. изм.	Примечание
		Покрытие площадки		
1		Покрытие из щебня по ГОСТ 8267-93, h=0.10	м²	95
		Покрытие проездов		
3		Покрытие из щебеночно-песчаной смеси по ГОСТ 25607-2009 смесь С 1 h=0,15 м Основание из гравийно-песчаной смеси по ГОСТ 25607-2009 смесь С 3 h=0,15 м Укрепление обочин из ГПС ГОСТ 25607-2009 смесь С 4 h=0,15 м	м²	1242.0 506.0


Спецификация элемента пересечения проектного газопровода проектной подъездной дорогой

Поз.	Обозначение	Наименование	Ед. изм.	Кол. шт.	Примечание
1	ГОСТ 10704-91	Труба 1420х14 с заводской изоляцией трехслойной усиленного типа по ТУ1394-015-05757848-2011/Д ГОСТ 10706-76	м	24.5	L тр.= шир.дороги+по 10м в каждую сторону
2	ТУ 1469-001-53597015-01	Опорно-направляющие кольца ПМТД тип1 1220х1420 ТУ 1469-001-53597015-01	шт	7	шаг расстановки 6м+3шт
3	ТУ 2531-002-53597015-12	"Манжета ПМТД 1220х1420 Н ТУ 2531-002-53597015-12" в комплекте с замковой пластиной, вулканизирующим слоем, праймером	шт	2	на концах кожуха
4	ГОСТ 10704-91	Труба 57х3 ГОСТ 10704-91, без изоляции/ ДГОСТ 10705-80	м	25	для отвода к вытяжной свече от кожуха на расстоянии 25 м от дробки дороги
5	ТП 402-021-1-12.000.МГ	Вытяжная свеча	шт	1	


Примечания:

При составлении настоящего чертежа были использованы :
1. Материалы топографо-геодезической съемки, предоставлены АО "O'ZLITINEFTGAZ".
2. Система координат местная. Высотные отметки даны в Балтийской системе.
3. Размеры даны в метрах.
4. Площадка кранового узла КУП-D10 привязана линейно к пикету ПК 0 +30.0.
5. Данный лист смотри совместно с листами разделов PIL, PRE, ELE, STR, SYS.
6. Детальный план кранового узла см. EWE0426-MGL1-PRE-054-DRW-790203.
7. Защита Пересечения проектной дороги с проектным газопроводом предусмотрена в техническом решении №2 в рамках авторского надзора.


Тип 1

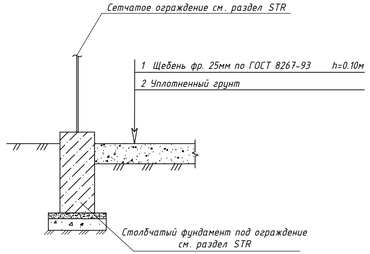

Тип 2

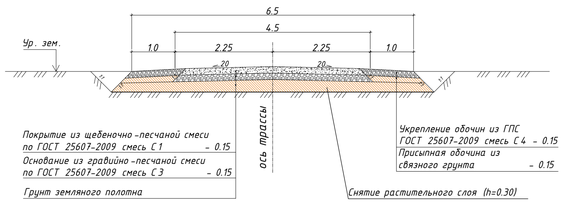

Тип 3

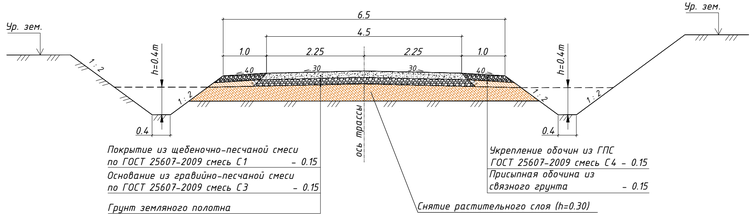

Рев.	Дата	Назначение ревизии	Проверил	Утвердил
A2	07.10.2026	Выпущено для строительства		
A1	10.09.2026	Выпущено для строительства		
R1	28.07.2026	Выпущено для рассмотрения		

ЗАКАЗЧИК: UTG INTERNATIONAL | ГЕНЕРАЛЬНЫЙ ПОДРЯДЧИК: UET | ПОДРЯДЧИК: PBC | ГЕНЕРАЛЬНЫЙ ПРОЕКТИРОВЩИК: EAST WEST ENGINEERING

Изм.	Кол.уч.	Лист	№док.	Подпись	Дата		
ГИП			Кирпичников С.		10.2026	EWE0426-MGL1-GLT-054-DRW-790106-A2	
Нач.отд.			Нигманова Н.		10.2026	«СТРОИТЕЛЬСТВО НОВЫХ НИТОК (УЧАСТКОВ) ГАЗОПРОВОДОВ «ГАЗЛИ – САРИМОЙ» И «АКЧАЛОК – ГАЗЛИ – НУКУС» ОБЩЕЙ ПРОТЯЖЕННОСТЬЮ НЕ МЕНЕЕ 275 КМ».	
Исполн.			Горлова О.		10.2026	ГАЗОПРОВОД «ГАЗЛИ–САРИМОЙ» (54 км).	Стадия: Р.Д. / Лист: 1 / Листов: 1
Н.контр			Кирпичников С.		10.2026	Генеральный план и транспорт. КУП-D10. План благоустройства территории М 1:500	ООО "EAST-WEST Engineering" г. Ташкент 2026 г.

Взам. инв. №

Подпись и дата

Инв.№ подл.

Формат / Format A3x3