План / Plan
М (1:50)

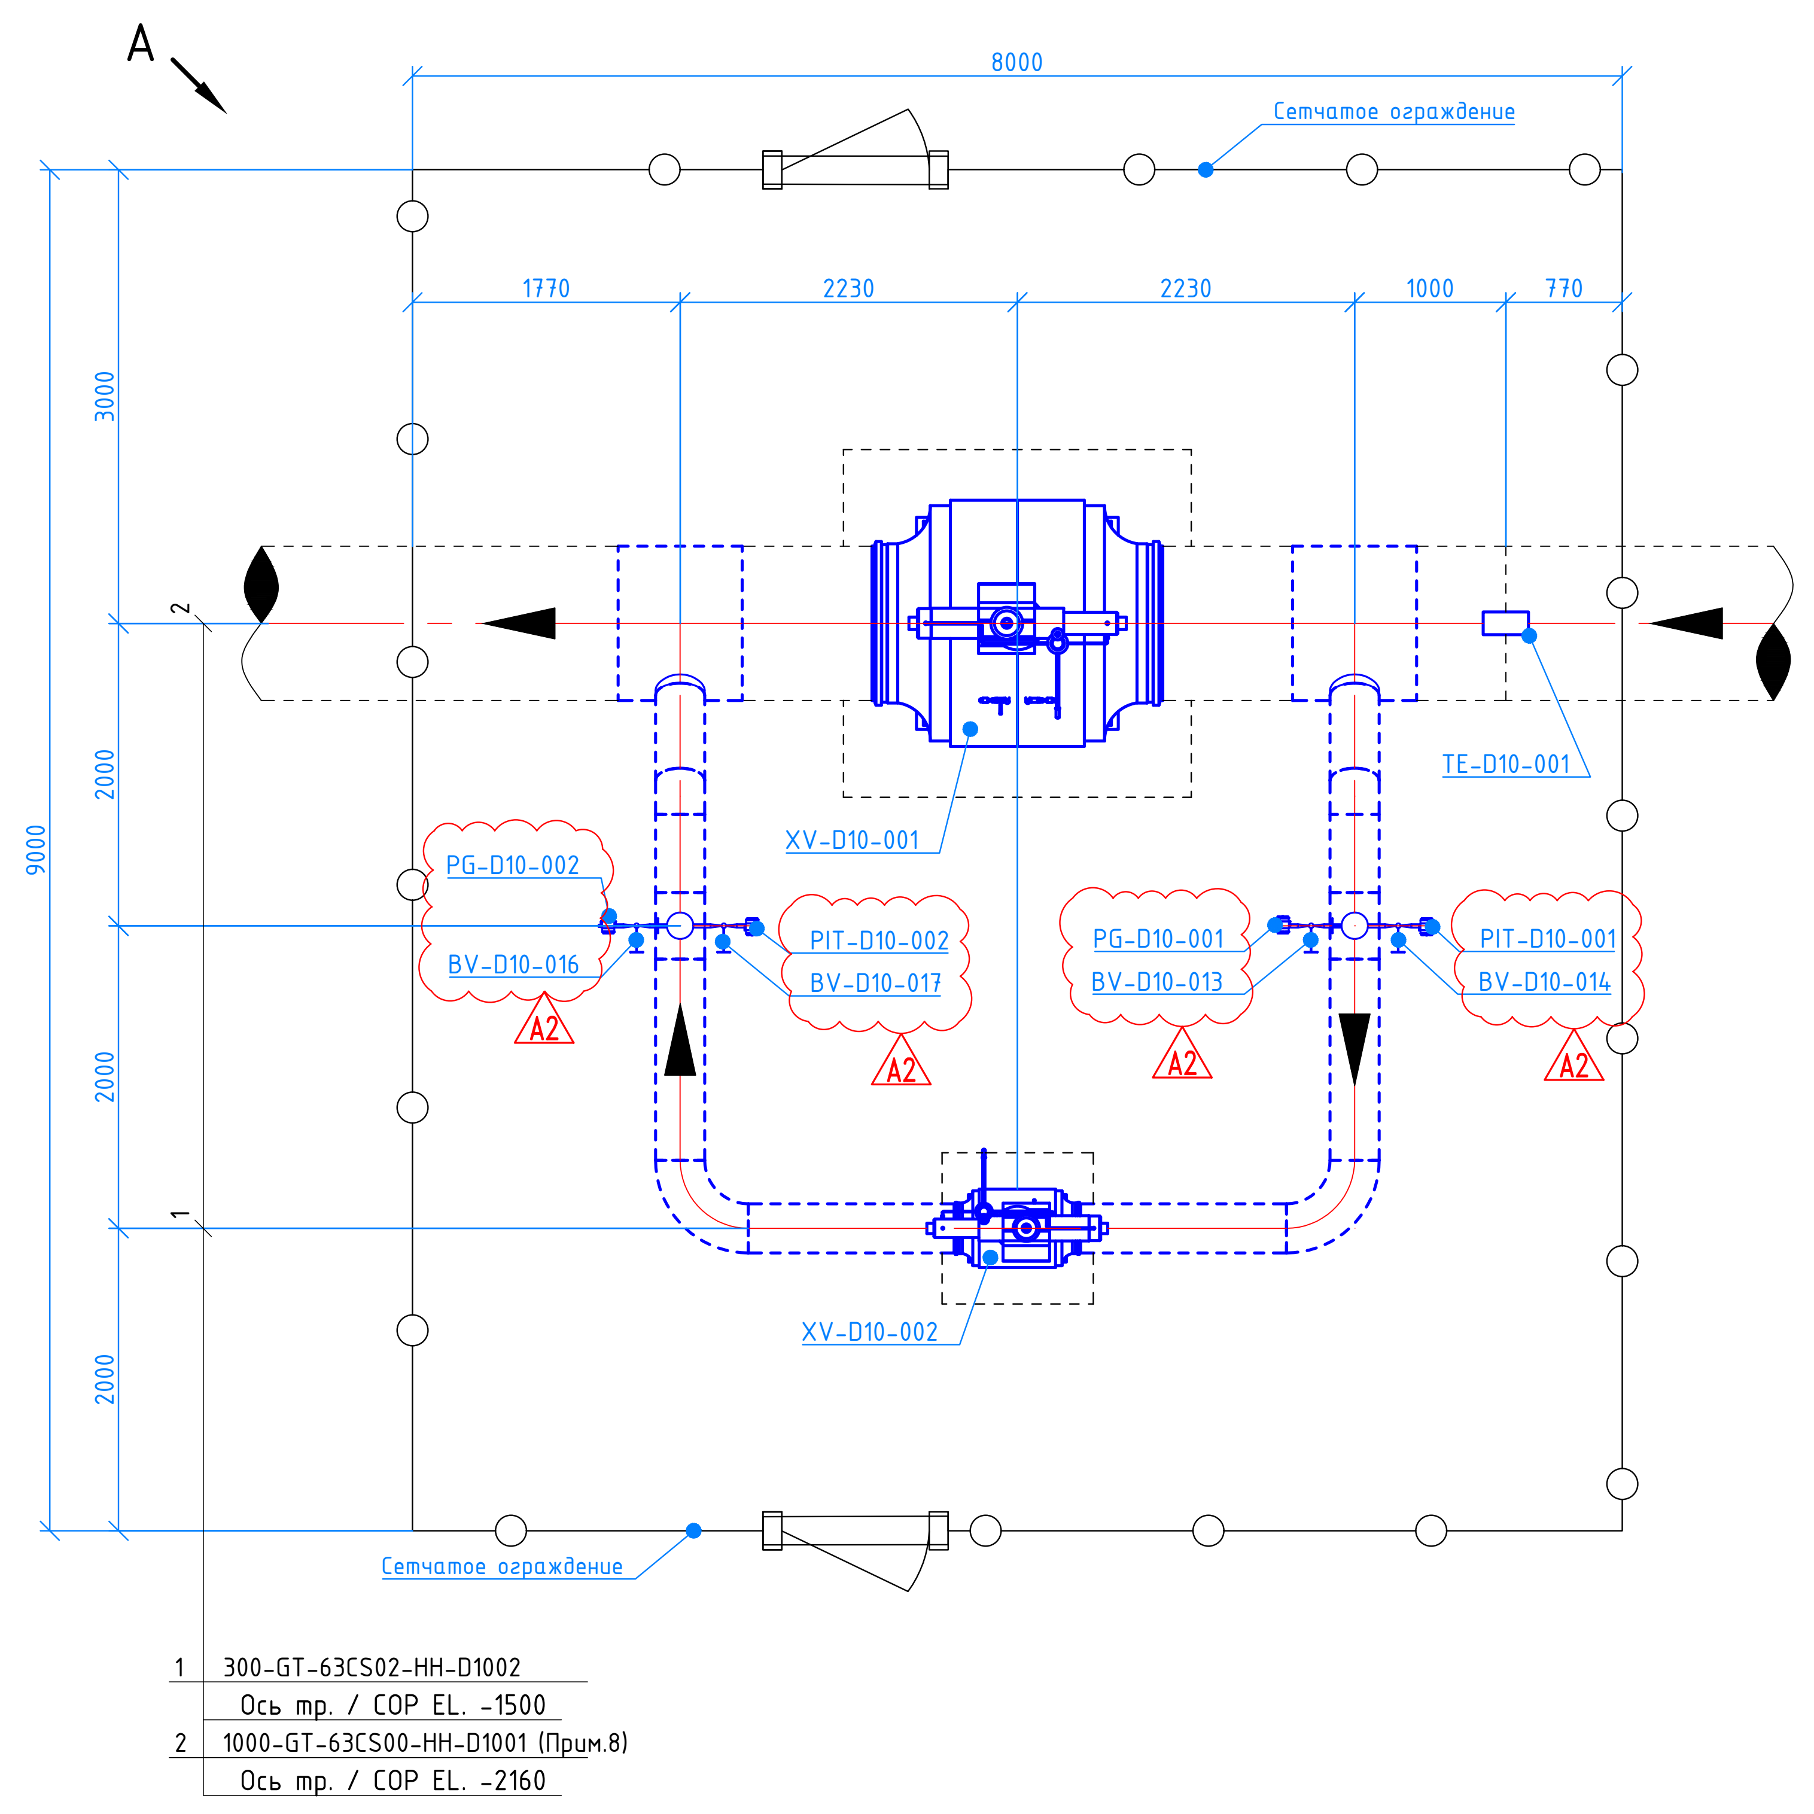
A
8000
Сетчатое ограждение
1770
2230
2230
1000
770
3000
2000
2000
2000
9000
2
1
XV-D10-001
TE-D10-001
PG-D10-002
BV-D10-016
PIT-D10-002
BV-D10-017
PG-D10-001
BV-D10-013
PIT-D10-001
BV-D10-014
A2
A2
A2
A2
XV-D10-002
Сетчатое ограждение
1 300-GT-63CS02-HH-D1002
Ось тр. / COP EL. -1500
2 1000-GT-63CS00-HH-D1001 (Прим.8)
Ось тр. / COP EL. -2160

Изометрический вид "A"
М (1:50)

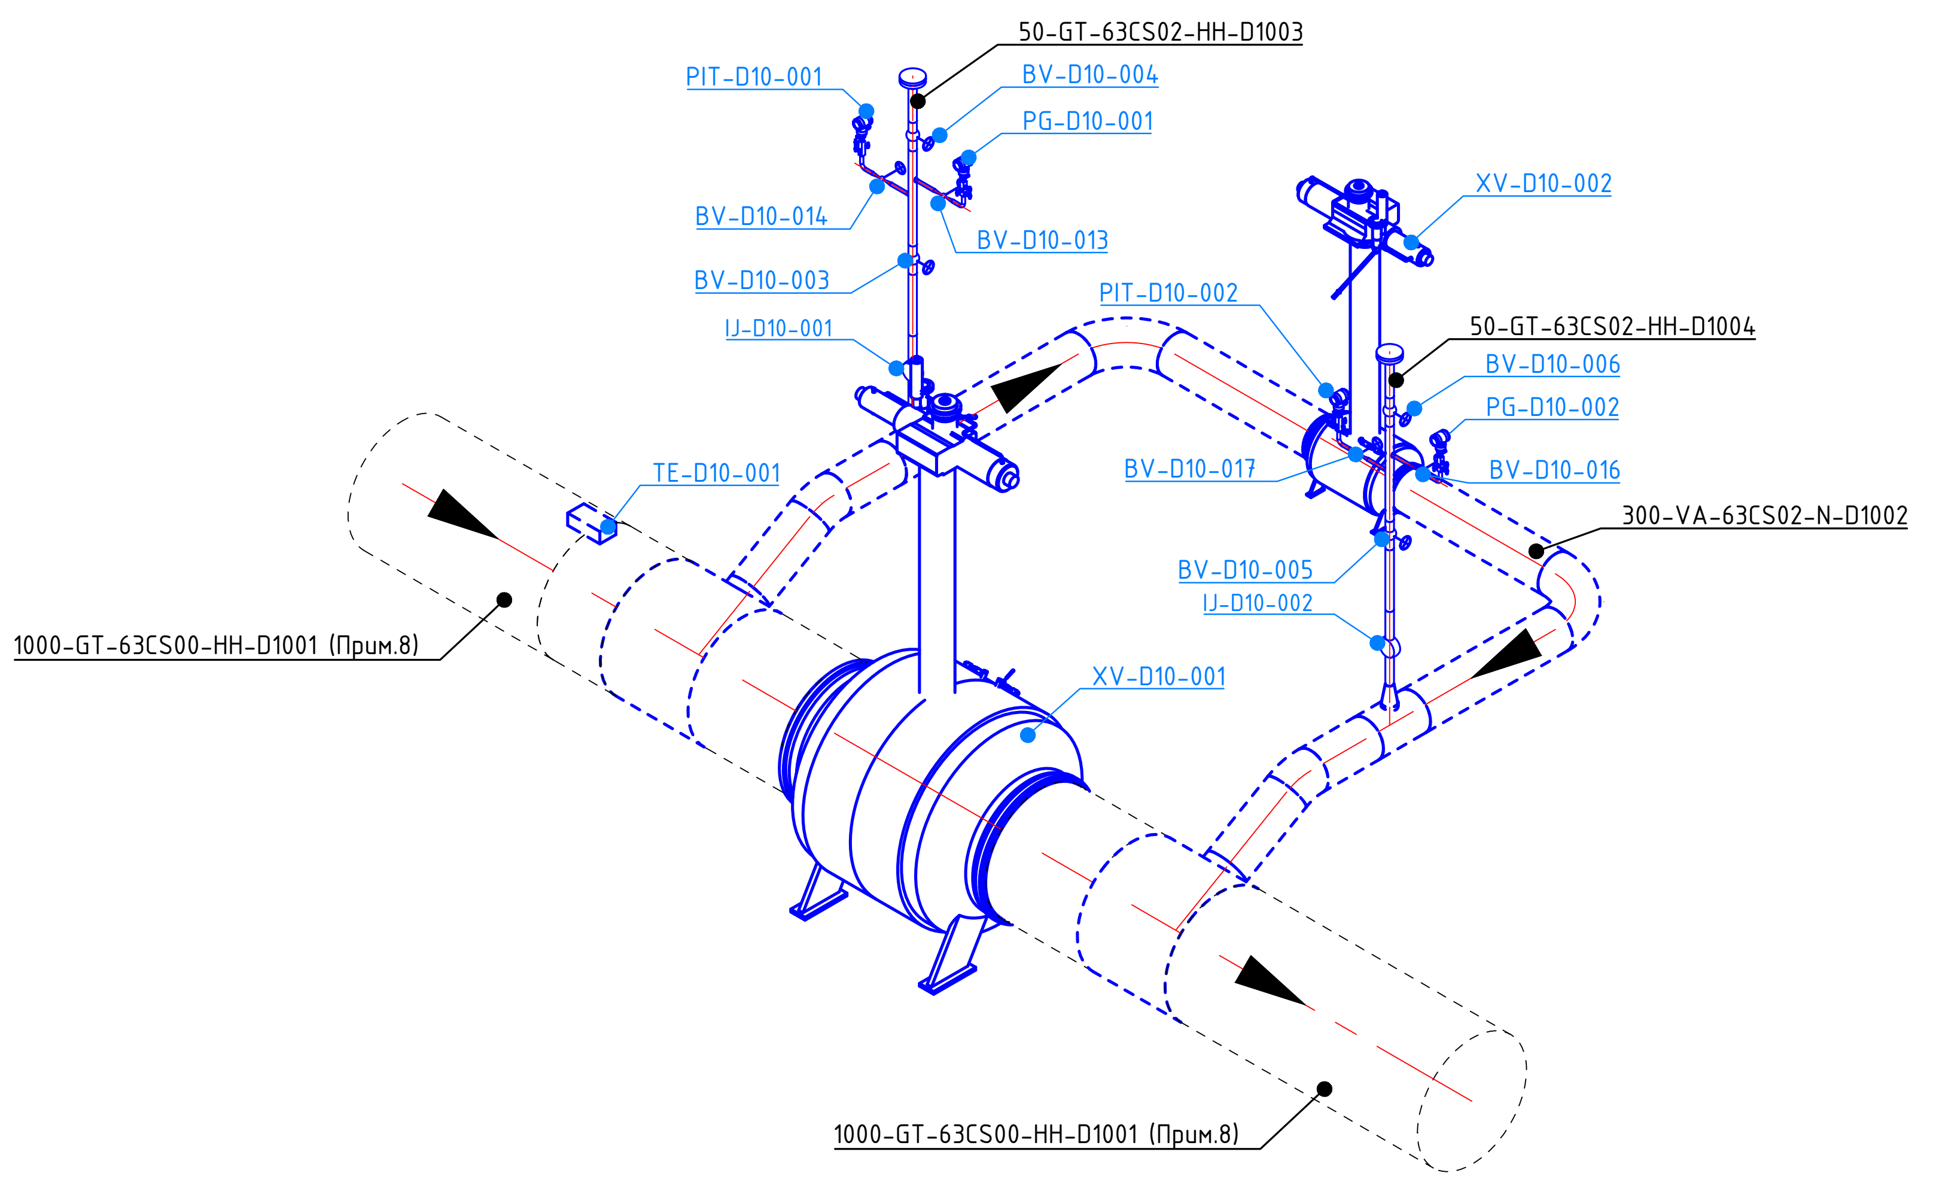
50-GT-63CS02-HH-D1003
PIT-D10-001
BV-D10-004
PG-D10-001
BV-D10-014
BV-D10-013
BV-D10-003
IJ-D10-001
XV-D10-002
PIT-D10-002
50-GT-63CS02-HH-D1004
BV-D10-006
PG-D10-002
TE-D10-001
BV-D10-017
BV-D10-016
300-VA-63CS02-N-D1002
BV-D10-005
IJ-D10-002
1000-GT-63CS00-HH-D1001 (Прим.8)
XV-D10-001
1000-GT-63CS00-HH-D1001 (Прим.8)

Разрез / Section 1-1
М (1:50)

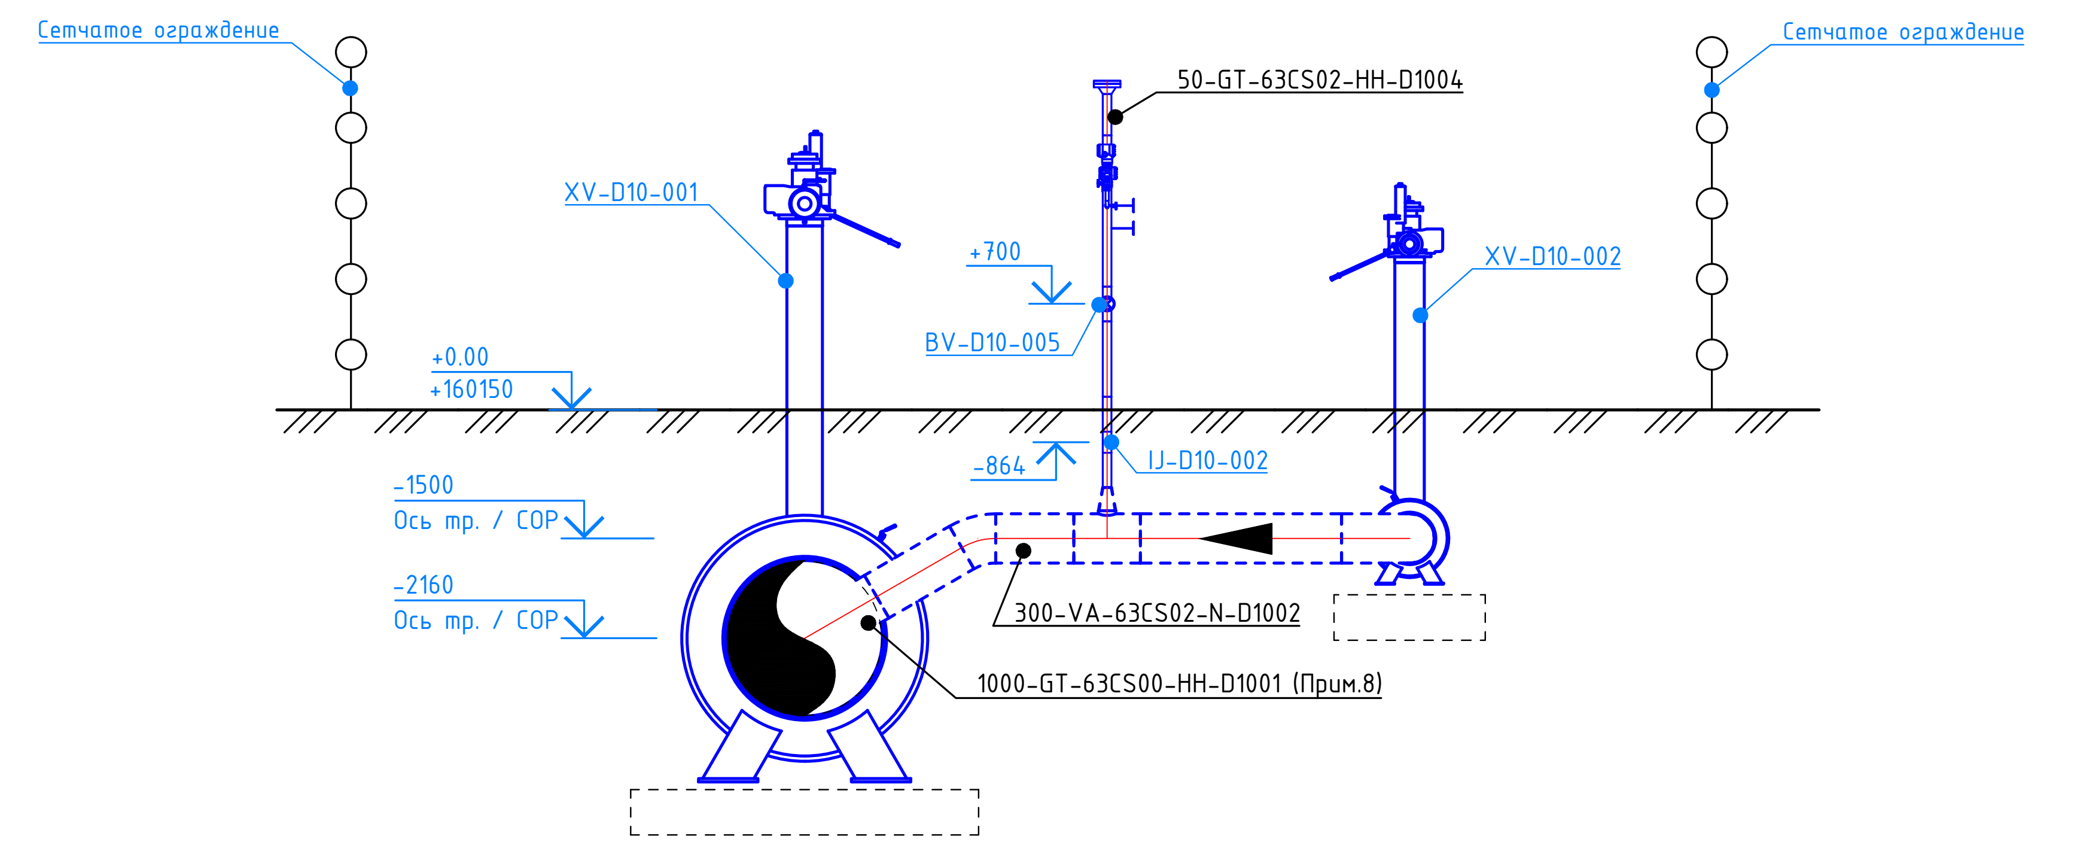
Сетчатое ограждение
Сетчатое ограждение
50-GT-63CS02-HH-D1004
XV-D10-001
+700
XV-D10-002
BV-D10-005
+0.00
+160150
-864
IJ-D10-002
-1500
Ось тр. / COP
-2160
Ось тр. / COP
300-VA-63CS02-N-D1002
1000-GT-63CS00-HH-D1001 (Прим.8)

Разрез / Section 2-2
М (1:50)

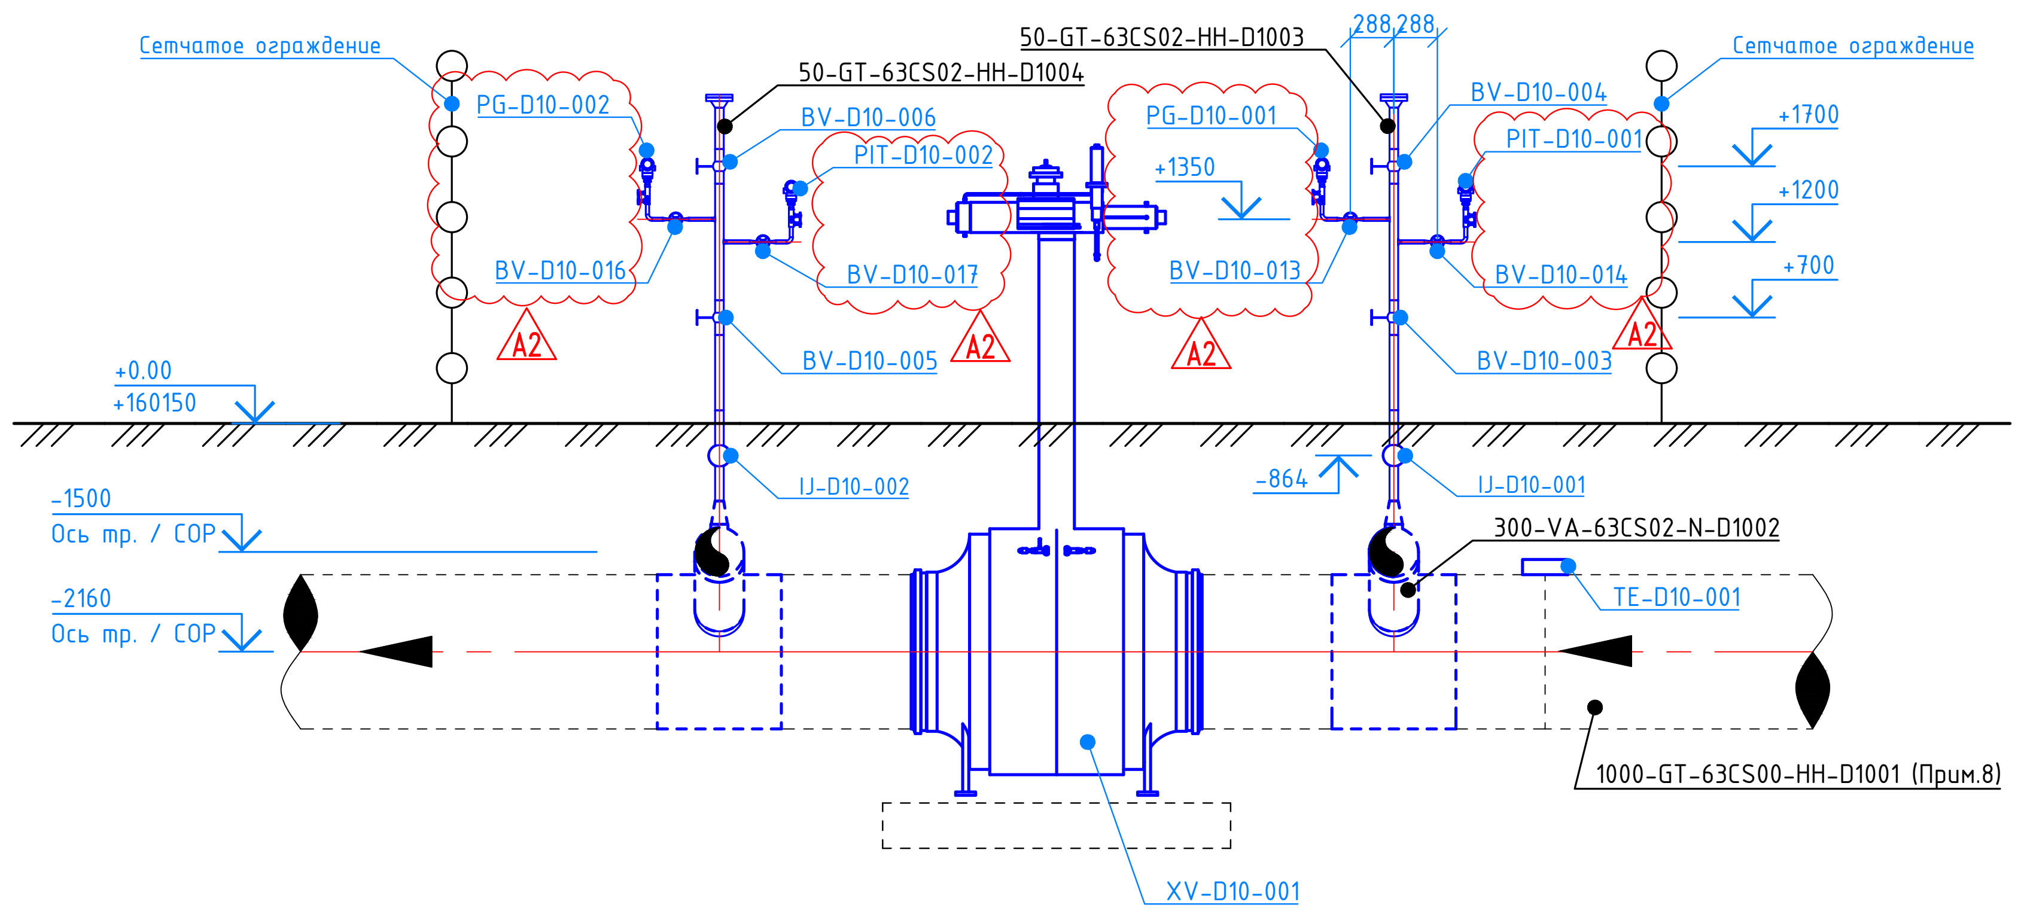
Сетчатое ограждение
PG-D10-002
50-GT-63CS02-HH-D1004
BV-D10-006
PIT-D10-002
50-GT-63CS02-HH-D1003
288
288
PG-D10-001
+1350
BV-D10-004
PIT-D10-001
Сетчатое ограждение
+1700
+1200
+700
BV-D10-016
BV-D10-017
BV-D10-013
BV-D10-014
A2
A2
A2
A2
BV-D10-005
BV-D10-003
+0.00
+160150
IJ-D10-002
-864
IJ-D10-001
-1500
Ось тр. / COP
-2160
Ось тр. / COP
300-VA-63CS02-N-D1002
TE-D10-001
1000-GT-63CS00-HH-D1001 (Прим.8)
XV-D10-001

ПРИМЕЧАНИЯ

1. Общие данные см. EWE0426-MGL1-PRE-054-COM-790201;
2. * - Размеры для справок;
3. ** - Размеры уточнить по месту;
4. Кран XV-D10-001 расположен на пикете ПК 0+30 перемычки №7 Ду1000;
5. Размеры фитингов - по ГОСТ. Все размеры указаны в миллиметрах;
6. Высотные отметки уточнить по месту;
7. Данный чертеж составлен на основе EWE0426-MGL1-PIL-054-COM-660201;
8. Труба учтена в линейной части проекта;
9. Привязка к пикетажу указана в EWE0426-MGL1-PRE-054-PLA-790202;
10. Фундаменты под опоры, шаровой кран XV-D10-001, продувочную свечу см. EWE0426-MGL1-STR-054-COM-790501;
11. Детальную информацию по трубопроводам см. изометрические чертежи;
12. На схеме указано основное направление потока газа, согласно схеме PFD, см. EWE0426-MGL1-PRE-054-PFD-610101. В процессе эксплуатации поток может быть направлен в обратном направлении.

Условные обозначения:

N - нет изоляции
HH - гидроизоляция от почвенной коррозии

Рев	Дата	Назначение ревизии	Проверил	Утвердил
A2	28.08.2026	Утверждено для строительства		
A1	24.07.2026	Утверждено для строительства		
R1	19.06.2026	Выпущено для рассмотрения		

ЗАКАЗЧИК:
ГЕНЕРАЛЬНЫЙ ПОДРЯДЧИК:
ПОДРЯДЧИК:
ГЕНЕРАЛЬНЫЙ ПРОЕКТИРОВЩИК:

EWE0426-MGL1-PRE-054-DRW-790203-A2

«СТРОИТЕЛЬСТВО НОВЫХ НИТОК (УЧАСТКОВ) ГАЗОПРОВОДОВ «ГАЗЛИ - САРИМОЙ» И «АКЧАЛОК - ГАЗЛИ - НУКУС» ОБЩЕЙ ПРОТЯЖЕННОСТЬЮ НЕ МЕНЕЕ 275 КМ».

Изм.	Кол.уч.	Лист	№ док.	Подпись	Дата
ГИП		Схабицкий А.			08.2026
Нач.отд.		Рябинин А.			08.2026
Исполн.		Таштимуров Р.			08.2026
Н.контр		Схабицкий А.			08.2026

ГАЗОПРОВОД «ГАЗЛИ-САРИМОЙ» (54 КМ). Линейный крановый узел DN1000 КУП-D10.

Стадия	Лист	Листов
РП	1	1

КУП-D10. План. Разрезы. Виды.
М 1:50

ООО "EAST-WEST Engineering"
г. Ташкент 2026г.

Взам. инв. №
Подпись и дата
Инв.№ подл.

Формат / Format A1