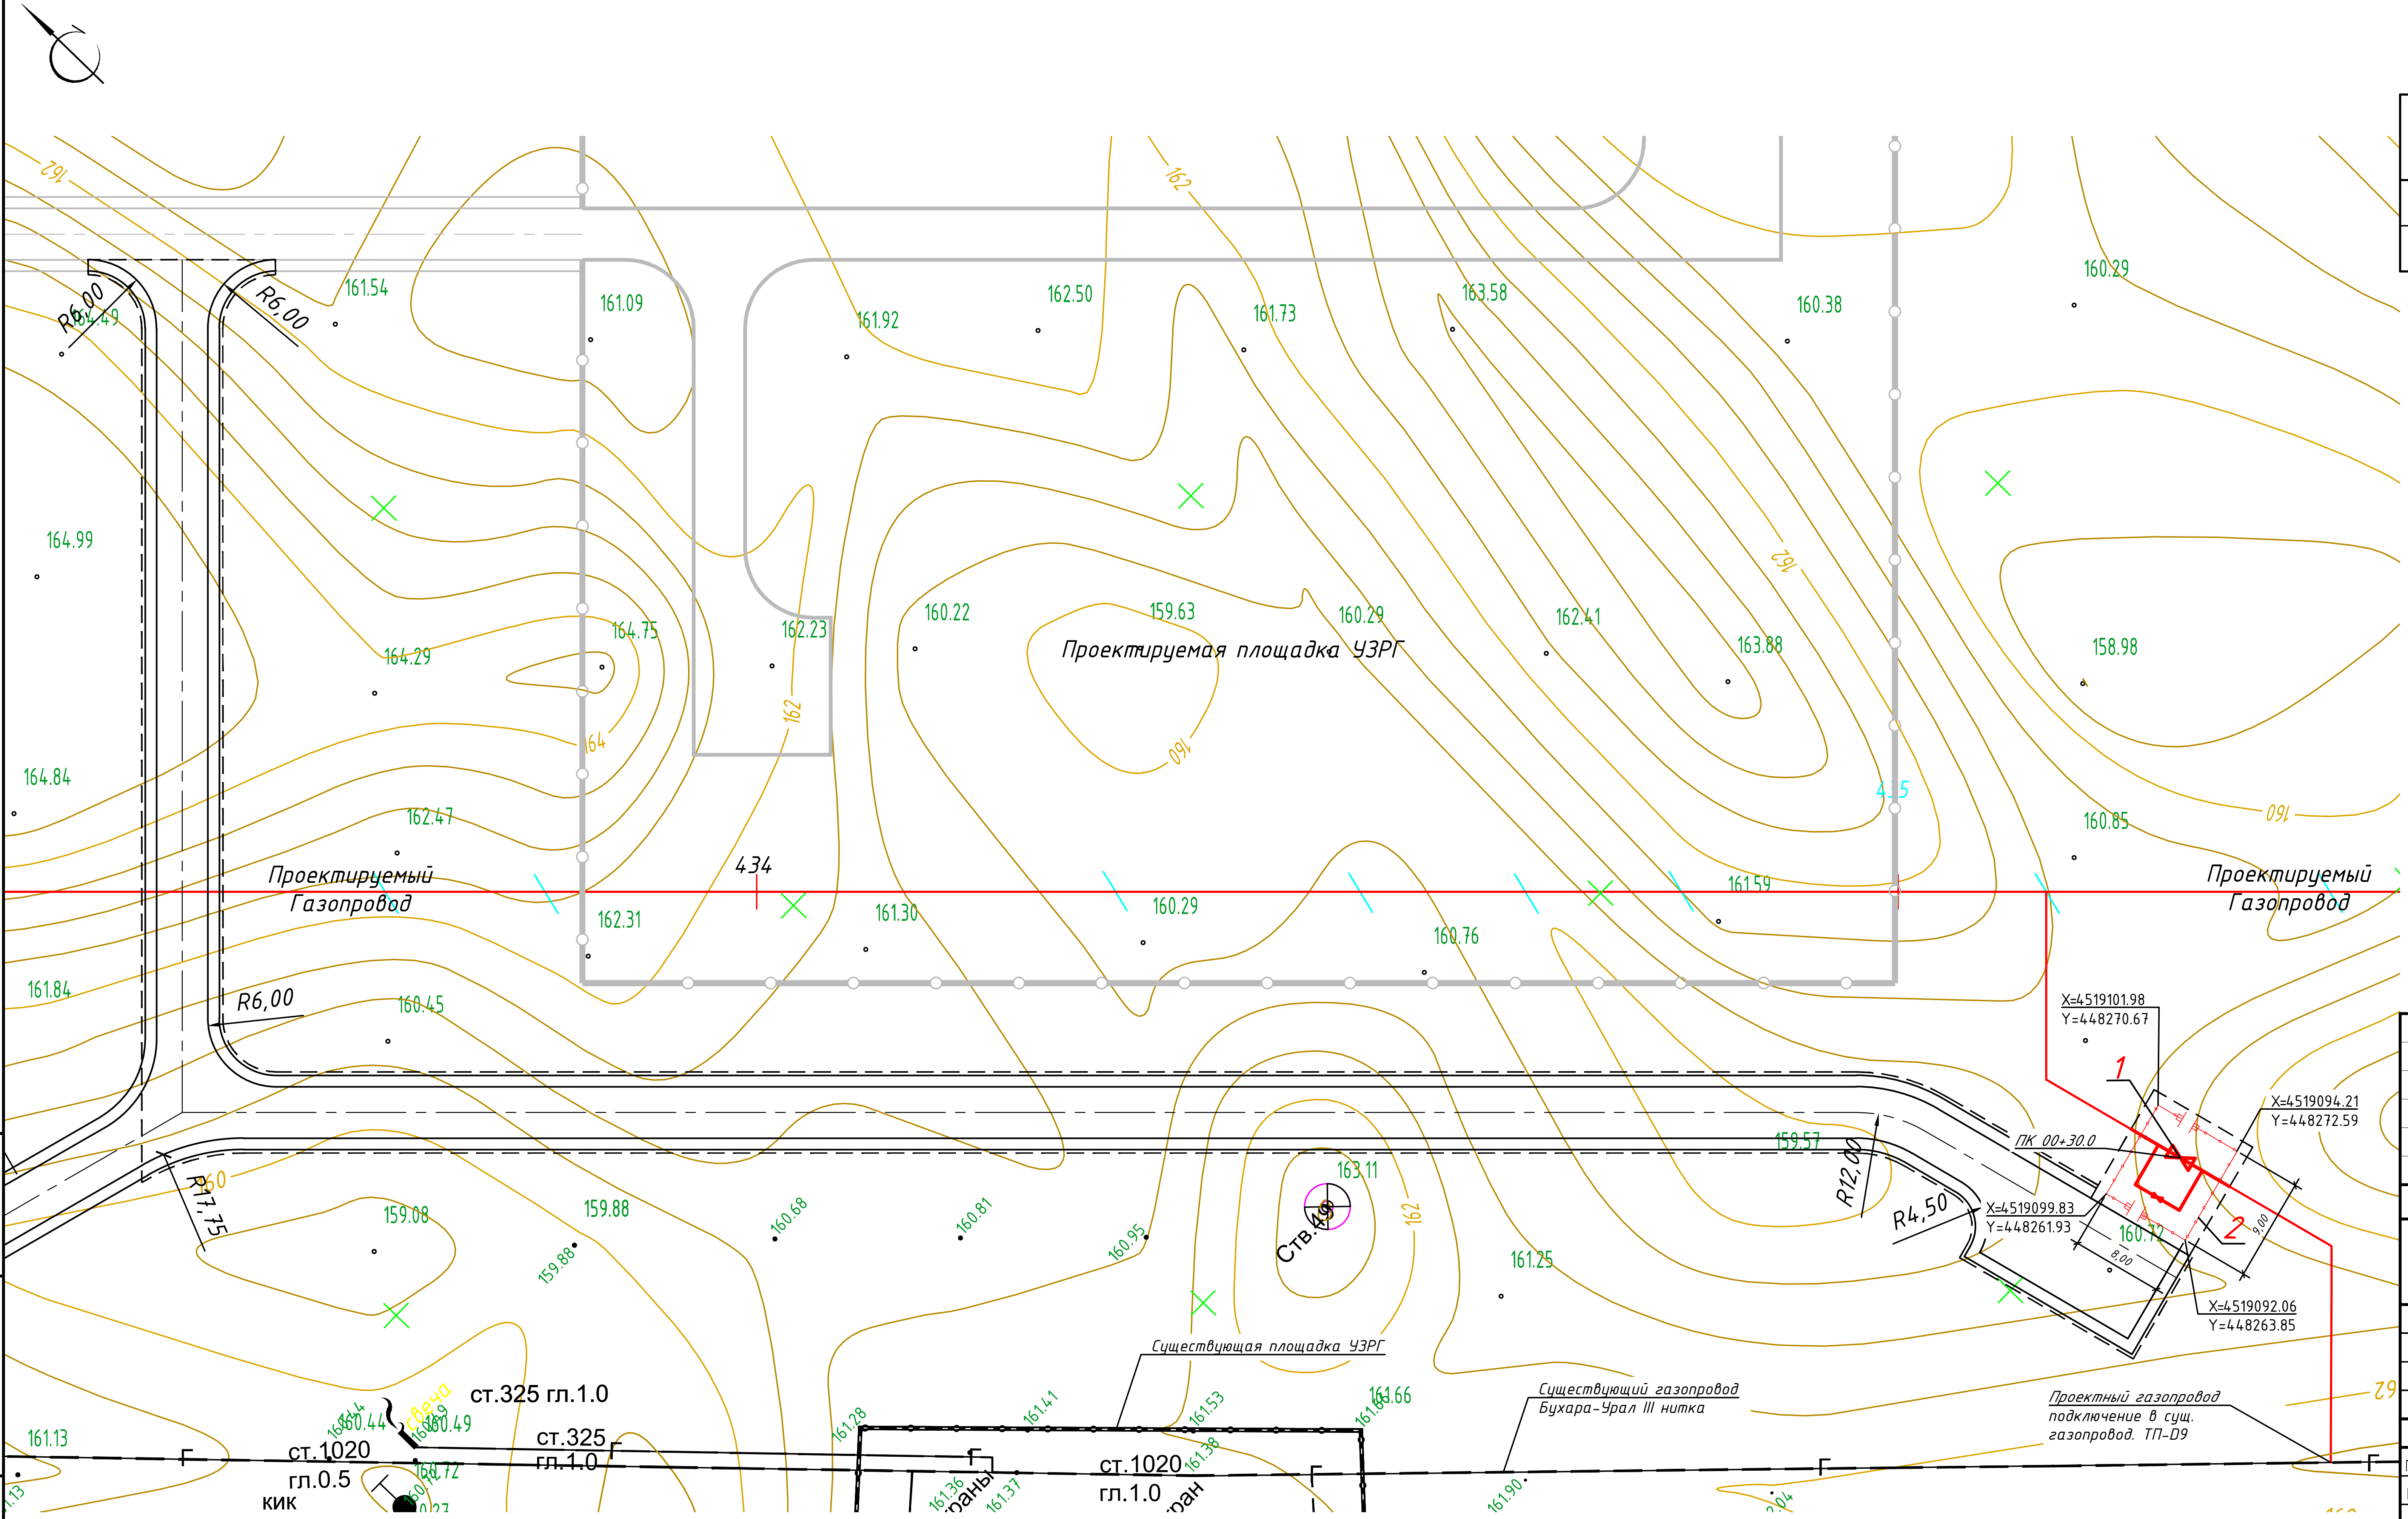
Проектируемая площадка УЗРГ
Проектируемый газопровод
Проектируемый газопровод
434
R6,00
R6,00
R6,00
R17,75
R12,00
R4,50
ПК 00+30.0
1
2
X=4519101.98
Y=448270.67
X=4519094.21
Y=448272.59
X=4519099.83
Y=448261.93
X=4519092.06
Y=448263.85
8,00
9,00
Ств.49
Существующая площадка УЗРГ
Существующий газопровод
Бухара-Урал III нитка
Проектный газопровод
подключение в сущ.
газопровод. ТП-D9
ст.325 гл.1.0
ст.325
гл.1.0
ст.1020
гл.0.5
КИК
ст.1020
гл.1.0
свеча
161.54
161.09
161.92
162.50
161.73
163.58
160.38
160.29
164.99
164.75
162.23
160.22
159.63
160.29
162.41
163.88
158.98
164.29
164.84
162.47
162.31
161.30
160.29
160.76
161.59
160.85
161.84
160.45
159.57
160.72
159.08
159.88
159.88
160.68
160.81
160.95
163.11
161.25
161.13
160.44
160.49
161.28
161.41
161.53
161.66
161.38
161.36
161.37
161.90
162
164
160

Экспликация зданий и сооружений

Номер на плане	Наименование	Примечание
1	Крановый узел Ду 1000	
2	Ограждение сетчатое	

Условные обозначения

—●—●—	Ограждение
⊣⊢	Калитка
– – – – –	Граница планировки
—г—г—	Существующий газопровод
———	Проектируемый газопровод ДУ-1200, ДУ-1000

Примечание:

1. Материалы топографо-геодезической съемки, предоставлены АО "O'ZLITINEFTGAZ";
2. Система координат см. раздел ГП. Высотные отметки даны в Балтийской системе;
3. Координаты ограждения даны в геометрической системе;
4. Кран XV-D10-001 установлен на ПК 0+30.0 проектного газопровода;
5. Детальный план кранового узла см. EWE0426-MGL1-PRE-054-DRW-790203;

Рев.	Дата	Назначение ревизии	Проверил	Утвердил
A1	07.08.2026	Утверждено для строительства		
R1	28.07.2026	Выпущено для рассмотрения		

ЗАКАЗЧИК: UTG UZTRANSGAZ
ГЕНЕРАЛЬНЫЙ ПОДРЯДЧИК: UET UZBEKENERGOTAMIR
ПОДРЯДЧИК: PBG Pro Build Generation
ГЕНЕРАЛЬНЫЙ ПРОЕКТИРОВЩИК: EAST WEST ENGINEERING

EWE0426-MGL1-PRE-054-PLA-790202-A1

«СТРОИТЕЛЬСТВО НОВЫХ НИТОК (УЧАСТКОВ) ГАЗОПРОВОДОВ «ГАЗЛИ – САРИМОЙ» И «АКЧАЛОК – ГАЗЛИ – НУКУС» ОБЩЕЙ ПРОТЯЖЕННОСТЬЮ НЕ МЕНЕЕ 275 КМ».

Изм.	Кол.уч.	Лист	№док.	Подпись	Дата
ГИП		Схабицкий А.			07.2026
Нач.отд.		Рябинин А.			07.2026
Исполн.		Юлдашев И.			07.2026
Н.контр		Схабицкий А.			07.2026

ГАЗОПРОВОД «ГАЗЛИ-САРИМОЙ» (54 КМ)

Стадия	Лист	Листов
РД		1

КУП-D10. Ситуационный план. М 1:500.

EAST WEST ENGINEERING
ООО "EAST-WEST Engineering"
г. Ташкент 2026г.

Взам. инв. №
Подпись и дата
Инв.№ подл.

Формат / Format A4X3