

1 – 1 м 1:25.

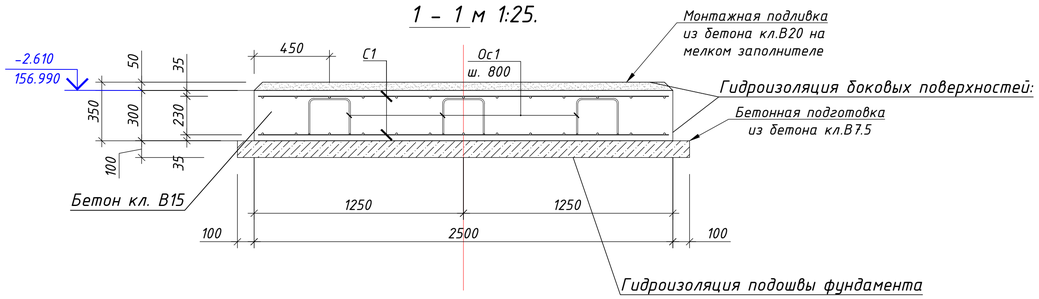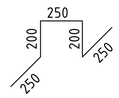

Ведомость деталей

Поз.	Эскиз
Ос1	

Размеры хомутов даны по центру стержня.

Спецификация элементов

Марка Поз.	Обозначение	Наименование	Кол.шт	Масса ед., кг	Прим.
		Фундамент Фом-1			
		Сборные единицы			
С1	См. данный лист	Сетка С1	2		153.87
		Детали			
Ос1	ГОСТ 34028-2016	Ф8 А240 L=1150 мм	9	0.45	4.08
		Сетка С1			
а1	ГОСТ 34028-2016	Ф14 А500 L=2450 мм	26	2.96	76.94
		Материалы			
	на подливку	Бетон кл. В20, W6, F50			0.30 м³
		Бетон кл. В15, W6, F50			1.88 м³
	на подготовку	Бетон кл. В7.5			0.73м³
		Гидроизоляция фундамента на площади:			16,55 м²

Фундамент Фом-1

Сетка С1

Примечания:

1. *Объединение арматурных стержней в плоские сетки или пространственные каркасы выполнять вязальной стальной отожженной проволокой d=0.8-1.0мм. Применение ручной электродуговой сварки не допускается.*
2. *Подливку выполнить из бетона кл. В20 на мелком заполнителе.*
3. *Фундамент Фом-1 разработан под шаровой кран. Бетонирование выполнять после получения оборудования и сверки с паспортными данными.*
4. *Фиксаторы для крепления двух сеток марки Ос-1 устанавливать в шахматном порядке.*
5. *Расположение фундамента смотри чертёж: Схема расположения кранового узла КУП-D10.*
6. *Фундаментов Фом-1 изготовить в количестве - 1шт.*
7. *Бетон для фундамента применять на сульфатостойком портландцементе.*

Гидроизоляция фундамента из двух слоев полимерного покрытия на основе лака ХП-734 по ГОСТ 52165-2003 толщиной 25 мкм.

Ведомость расхода стали, кг

Марка элемента	Изделия арматурные					Общий расход
	Арматура класса				Всего	
	А240		А500			
	ГОСТ 34028-2016		ГОСТ 34028-2016			
	Ф8	Итого	Ф14	Итого		
Фундамент Фом1	4.08	4.08	153.87	153.87	157.95	157.95

Рев	Дата	Назначение ревизии	Проверил	Утвердил
А1	09.09.2026	Выпущено для строительства		
R1	31.07.2026	Выпущено для рассмотрения		

ЗАКАЗЧИК: UTG UZTRANSGAZ | ГЕНЕРАЛЬНЫЙ ПОДРЯДЧИК: UET UZHEKENERGOTAME | ПОДРЯДЧИК: PBG Pro Build Generation | ГЕНЕРАЛЬНЫЙ ПРОЕКТИРОВЩИК: EAST WEST ENGINEERING

Изм.	Кол.уч.	Лист	№ док.	Подпись	Дата	EWE0426-MGL1-STR-054-DRW-790505-A1		
						«СТРОИТЕЛЬСТВО НОВЫХ НИТОК (УЧАСТКОВ) ГАЗОПРОВОДОВ «ГАЗЛИ - САРИМОЙ» И «АКЧАЛОК - ГАЗЛИ - НУКУС» ОБЩЕЙ ПРОТЯЖЕННОСТЬЮ НЕ МЕНЕЕ 275 КМ».		
ГИП		Кирпичников С.			09.09.26		Стадия	Лист	Листов
Нач.отд.		Каршиев А.			09.09.26	ГАЗОПРОВОД "ГАЗЛИ-САРИМОЙ" (54 КМ) Линейный крановый узел DN1000 КУП-D10	РП	1	1
Исполн.		Хабиров Х.			09.09.26				
Н.контр		Кирпичников С.			09.09.26	Фундамент Фом-1.	EAST WEST ENGINEERING	ООО "EAST-WEST Engineering" г. Ташкент 2026г.	

Взам. инв. № | Подпись и дата | Инв.№ подл.

Формат / Format A2