
Схема расположения сетчатого ограждения м 1:50.

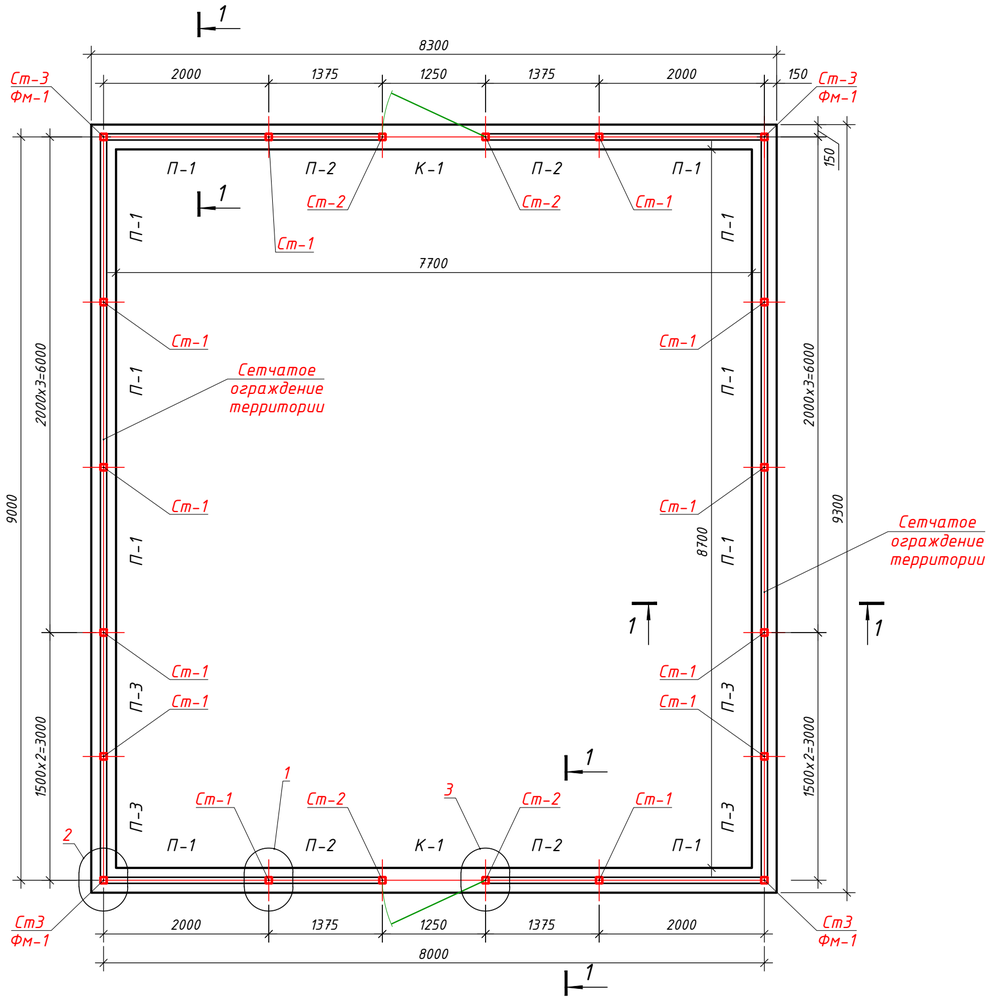


Спецификация элементов

Марка Поз.	Обозначение	Наименование	Кол. шт.	Масса ед.кг	Примеч.
		Линейный крановый узел КУП-D10			
Фм-1	EWE0426-MGL1-STR-054-DRW-790508	Фундамент ленточный, монолитный Фм-1			
Ст-1	EWE0426-MGL1-STR-054-DRW-790509	Стойка ограждения Ст1	12		
Ст-2	EWE0426-MGL1-STR-054-DRW-790510	Стойка ограждения Ст2	4		
Ст-3	EWE0426-MGL1-STR-054-DRW-790511	Стойка ограждения Ст3	4		
П-1	EWE0426-MGL1-STR-054-DRW-790512	Панель ограждения П1	10		
П-2	EWE0426-MGL1-STR-054-DRW-790513	Панель ограждения П2	4		
П-3	EWE0426-MGL1-STR-054-DRW-790514	Панель ограждения П3	4		
К-1	EWE0426-MGL1-STR-054-DRW-790515	Калитка К1	2		
КД-1	EWE0426-MGL1-STR-054-DRW-790516	Крепежная деталь КД1	24		
КД-2	EWE0426-MGL1-STR-054-DRW-790516	Крепежная деталь КД2	24		


Примечания:

1. Данный чертёж читать совместно с ленточным фундаментом Фм-1.
2. Изготовить общее количество узлов:
   - узел 1 - 12 шт.
   - узел 2 - 4 шт.
   - узел 3 - 4 шт.
3. Сечение 1 - 1 смотреть на листе - EWE0426-MGL1-STR-054-DRW-790508


Узел 1

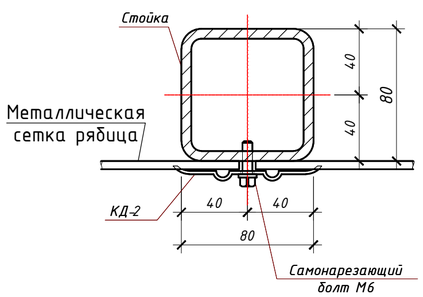

Узел 2

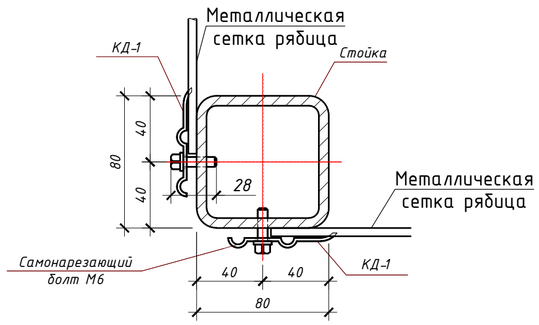

Узел 3

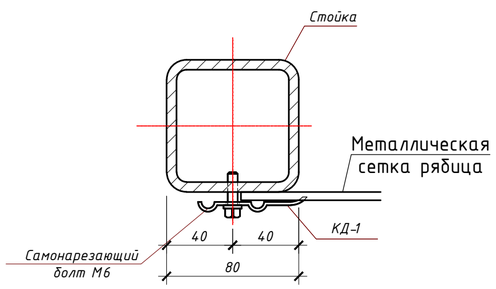

A1	09.09.2026	Выпущено для строительства		
R1	31.07.2026	Выпущено для рассмотрения		
Рев	Дата	Назначение ревизии	Проверил	Утвердил

ЗАКАЗЧИК: UTG | ГЕНЕРАЛЬНЫЙ ПОДРЯДЧИК: UET | ПОДРЯДЧИК: PBG | ГЕНЕРАЛЬНЫЙ ПРОЕКТИРОВЩИК: EAST WEST ENGINEERING

Изм.	Кол.уч.	Лист	№ док.	Подпись	Дата
ГИП		Кирпичников С.			09.09.26
Нач.отд.		Каршиев А.			09.09.26
Исполн.		Хабиров Х.			09.09.26
Н.контр		Кирпичников С.			09.09.26

EWE0426-MGL1-STR-054-DRW-790507-A1

«СТРОИТЕЛЬСТВО НОВЫХ НИТОК (УЧАСТКОВ) ГАЗОПРОВОДОВ «ГАЗЛИ - САРИМОЙ» И «АКЧАЛОК - ГАЗЛИ - НУКУС» ОБЩЕЙ ПРОТЯЖЕННОСТЬЮ НЕ МЕНЕЕ 275 КМ».

ГАЗОПРОВОД "ГАЗЛИ-САРИМОЙ" (54 КМ)
Линейный крановый узел DN1000 КУП-D10

Стадия	Лист	Листов
РП	1	1

Схема расположения сетчатого ограждения

ООО "EAST-WEST Engineering"
г. Ташкент 2026г.

Взам. инв. № | Подпись и дата | Инв.№ подл.

Формат / Format A2