

Панель ограждения П-3

м 1:25.

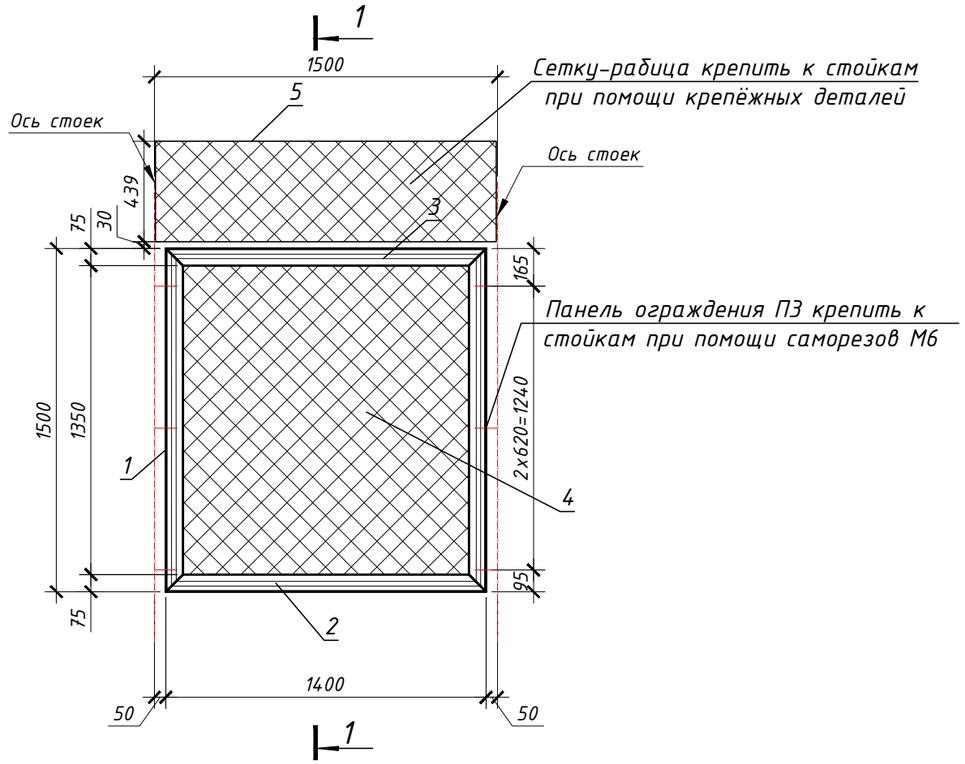

Разрез 1-1 м 1:50.

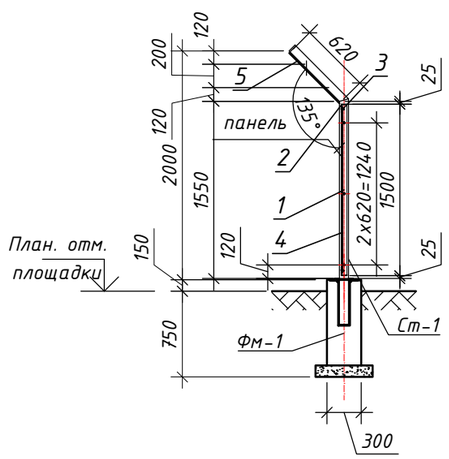

Спецификация расхода материалов

Марка Поз.	Обозначение	Наименование	Кол. шт.	Масса ед.кг.	Примечание
П-3		Панель ограждения П-3		36,07	вес на 1 шт.
1	ГОСТ 8510-86, Сталь С235	L75х50х5 L=1500	2	7.19	14.37
2	ГОСТ 8510-86, Сталь С235	L75х50х5 L=1400	2	6.71	13.41
3	ГОСТ 34028-2016	Арматура Ф6.0 А240 Lобщ=5600	1	0.222 кг/м.п	1.24
4	ГОСТ 5336-80*	Сетка рабица №50-3.0, размером			
		1450 х 1370мм; S=1.99м2	1	2,42 кг/м2	4.82
5	ГОСТ 5336-80*	Сетка рабица №50-3.0,размером			
		620 х 1490мм; S=0.92м2	1	2,42 кг/м2	2.23
		Материалы:			
		Окраска металлоконструкций масляной краской за 2 раза			1,45м²

Примечания:

1. Сварку вести электродами Э42А ГОСТ9467-75.
2. Конструкция должна быть покрыта масляной краской за 2 раза по грунтовке.

A1	09.09.2026	Выпущено для строительство		
R1	31.07.2026	Выпущено для рассмотрения		
Рев	Дата	Назначение ревизии	Проверил	Утвердил

ЗАКАЗЧИК: UTG UZBEKISTANGAZ

ГЕНЕРАЛЬНЫЙ ПОДРЯДЧИК: UET UZBEKENERGOTAMIR

ПОДРЯДЧИК: PBG Pro Build Generation

ГЕНЕРАЛЬНЫЙ ПРОЕКТИРОВЩИК: EAST WEST ENGINEERING

Изм.	Кол.уч.	Лист	№ док.	Подпись	Дата
ГИП		Кирпичников С.			09.09.26
Нач.отд.		Каршиев А.			09.09.26
Исполн.		Хабиров Х.			09.09.26
Н.контр		Кирпичников С.			09.09.26

EWE0426-MGL1-STR-054-DRW-790514-A1

«СТРОИТЕЛЬСТВО НОВЫХ НИТОК (УЧАСТКОВ) ГАЗОПРОВОДОВ «ГАЗЛИ - САРИМОЙ» И «АКЧАЛОК - ГАЗЛИ - НУКУС» ОБЩЕЙ ПРОТЯЖЕННОСТЬЮ НЕ МЕНЕЕ 275 КМ».

ГАЗОПРОВОД "ГАЗЛИ-САРИМОЙ" (54 КМ)
Линейный крановый узел DN1000 КУП-D10

Стадия	Лист	Листов
РП	1	1

Панель ограждения П-3.

EAST WEST ENGINEERING

ООО "EAST-WEST Engineering"
г. Ташкент 2026г.

Взам. инв. №

Подпись и дата

Инв.№ подл.

Формат / Format А3