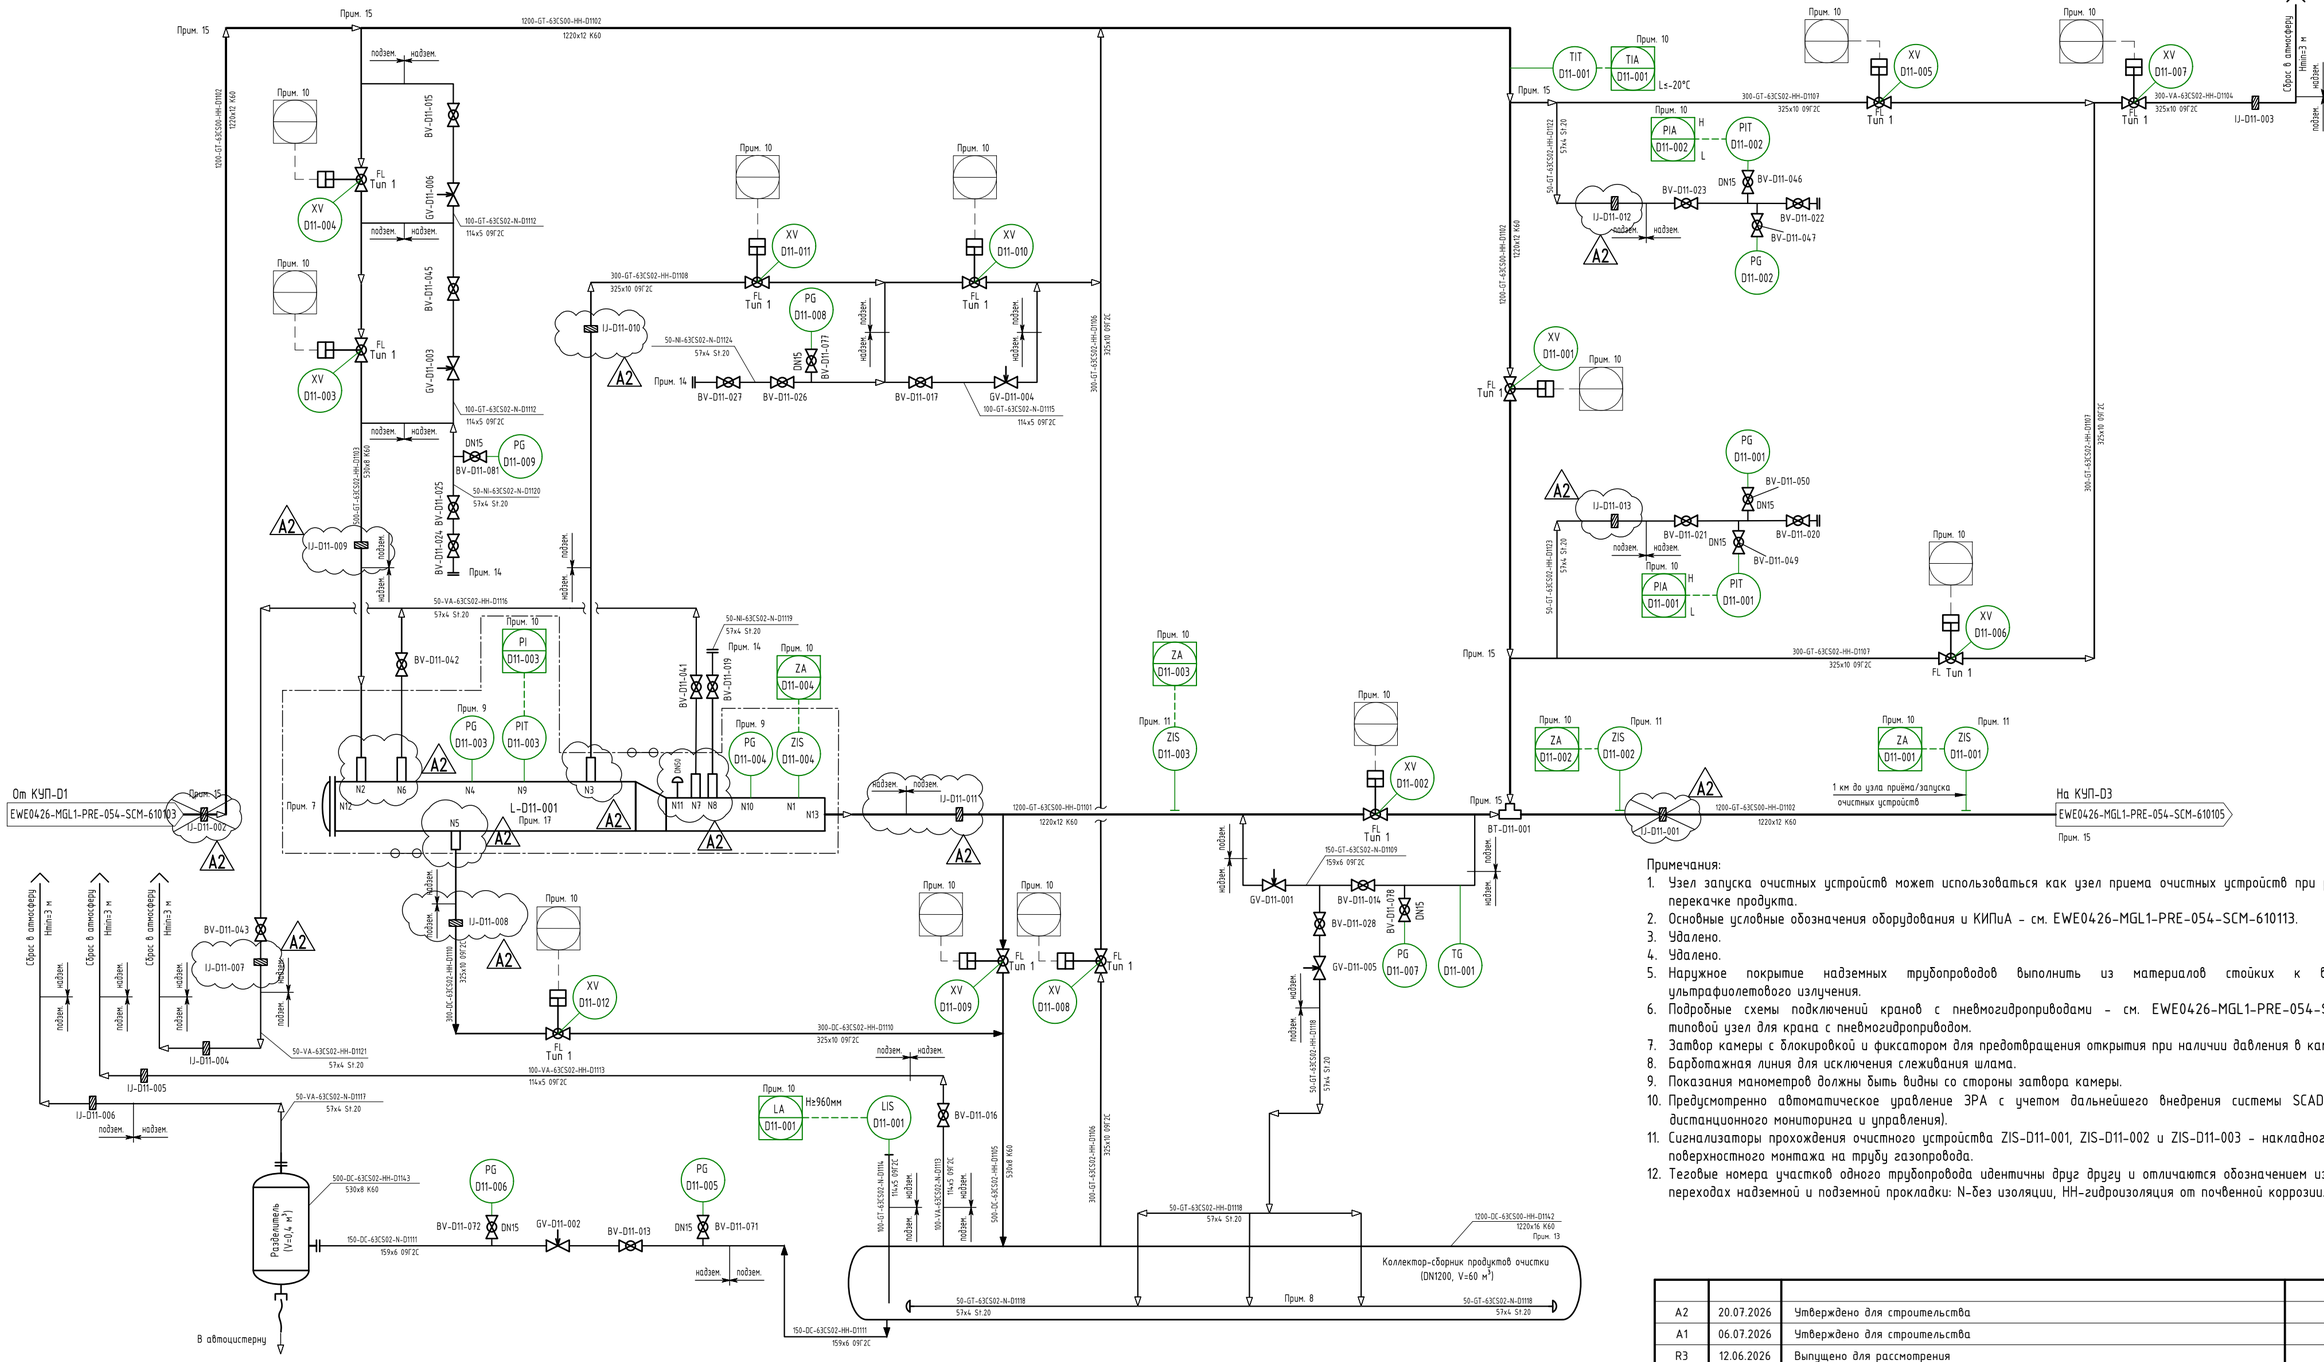


Примечания:

1. Узел запуска очистных устройств может использоваться как узел приема очистных устройств при реверсивной перекачке продукта.
2. Основные условные обозначения оборудования и КИПиА - см. EWE0426-MGL1-PRE-054-SCM-610113.
3. Удалено.
4. Удалено.
5. Наружное покрытие надземных трубопроводов выполнить из материалов стойких к воздействию ультрафиолетового излучения.
6. Подробные схемы подключений кранов с пневмогидроприводами - см. EWE0426-MGL1-PRE-054-SCM-610113, типовой узел для крана с пневмогидроприводом.
7. Затвор камеры с блокировкой и фиксатором для предотвращения открытия при наличии давления в камере.
8. Барботажная линия для исключения слеживания шлама.
9. Показания манометров должны быть видны со стороны затвора камеры.
10. Предусмотренно автоматическое управление ЗРА с учетом дальнейшего внедрения системы SCADA (система дистанционного мониторинга и управления).
11. Сигнализаторы прохождения очистного устройства ZIS-D11-001, ZIS-D11-002 и ZIS-D11-003 - накладного типа для поверхностного монтажа на трубу газопровода.
12. Теговые номера участков одного трубопровода идентичны друг другу и отличаются обозначением изоляции при переходах надземной и подземной прокладки: N-без изоляции, HH-гидроизоляция от почвенной коррозии.
13. Толщина трубы DN 1200 для изготовления коллектора-сборника продуктов очистки указана для категории В.
14. В процессе эксплуатации проталкивание поршня к затвору камеры, продувку дна и передавливание жидкости из конденсатосборника выполнять с помощью инертного газа (азота) из внешнего источника.
15. На схеме указано основное направление потока газа, согласно схеме PFD, см. EWE0426-MGL1-PRE-054-PFD-610101. В процессе эксплуатации поток может быть направлен в обратном направлении.
16. Трубный аккумулятор, стояки отбора и стояки подачи импульсного газа исключены из технологической схемы в ревизии R2 в связи с применением аккумуляторов в составе привода кранов, в соответствии с решениями принятыми на совещании от 08.06.2026 г. между ООО «Probuild Generation» и проектным институтом.
17. Типы соединений штуцеров камеры изменены на приварные, в соответствии с требованием Заказчика на основании письма УП «Ургенчтрансгаз» № 45-8/4786 от 01.07.2026.
18. Тэговые номера тройников указаны только для тройников с решеткой магистрального газопровода. В местах, где тэговые номера не указаны принять как тройник без решетки.

Узел запуска очистных устройств #D11	
Номинальное давление (МПа)	6,3
Расчетная температура (°C)	-26,9...+85
Рабочее давление (МПа)	5,5
Рабочая температура (°C)	-20...+40

Рев.	Дата	Назначение ревизии	Проверил	Утвердил
A2	20.07.2026	Утверждено для строительства		
A1	06.07.2026	Утверждено для строительства		
R3	12.06.2026	Выпущено для рассмотрения		
R2	08.06.2026	Выпущено для рассмотрения		
R1	13.05.2026	Выпущено для рассмотрения		

ЗАКАЗЧИК: UTG UZTRANSGAZ
ГЕНЕРАЛЬНЫЙ ПОДРЯДЧИК: UET
ПОДРЯДЧИК: PBG Pro Build Generation
ГЕНЕРАЛЬНЫЙ ПРОЕКТИРОВЩИК: EAST WEST ENGINEERING

Изм.	Кол.уч.	Лист	№док.	Подпись	Дата
ГИП		Схабицкий А.			07.2026
Нач.отд.		Рябинин А.			07.2026
Исполн.		Юлдашев И.			07.2026
Н.контр		Схабицкий А.			07.2026

EWE0426-MGL1-PRE-054-SCM-610102-A2

«СТРОИТЕЛЬСТВО НОВЫХ НИТОК (УЧАСТКОВ) ГАЗОПРОВОДОВ «ГАЗЛИ - САРИМОЙ» И «АКЧАЛОК - ГАЗЛИ - НУКУС» ОБЩЕЙ ПРОТЯЖЕННОСТЬЮ НЕ МЕНЕЕ 275 КМ».

ГАЗОПРОВОД «ГАЗЛИ-САРИМОЙ» (54 КМ)

Стадия	Лист	Листов
РД	1	1

Узел приема/запуска очистных устройств DN1200.УЗПОУ-D11. Схема трубной обвязки и КИПиА P&ID

ООО "EAST-WEST Engineering"
г. Ташкент 2026г.

Взам. инв. №
Подпись и дата
Инв.№ подл.

Формат / Format A2