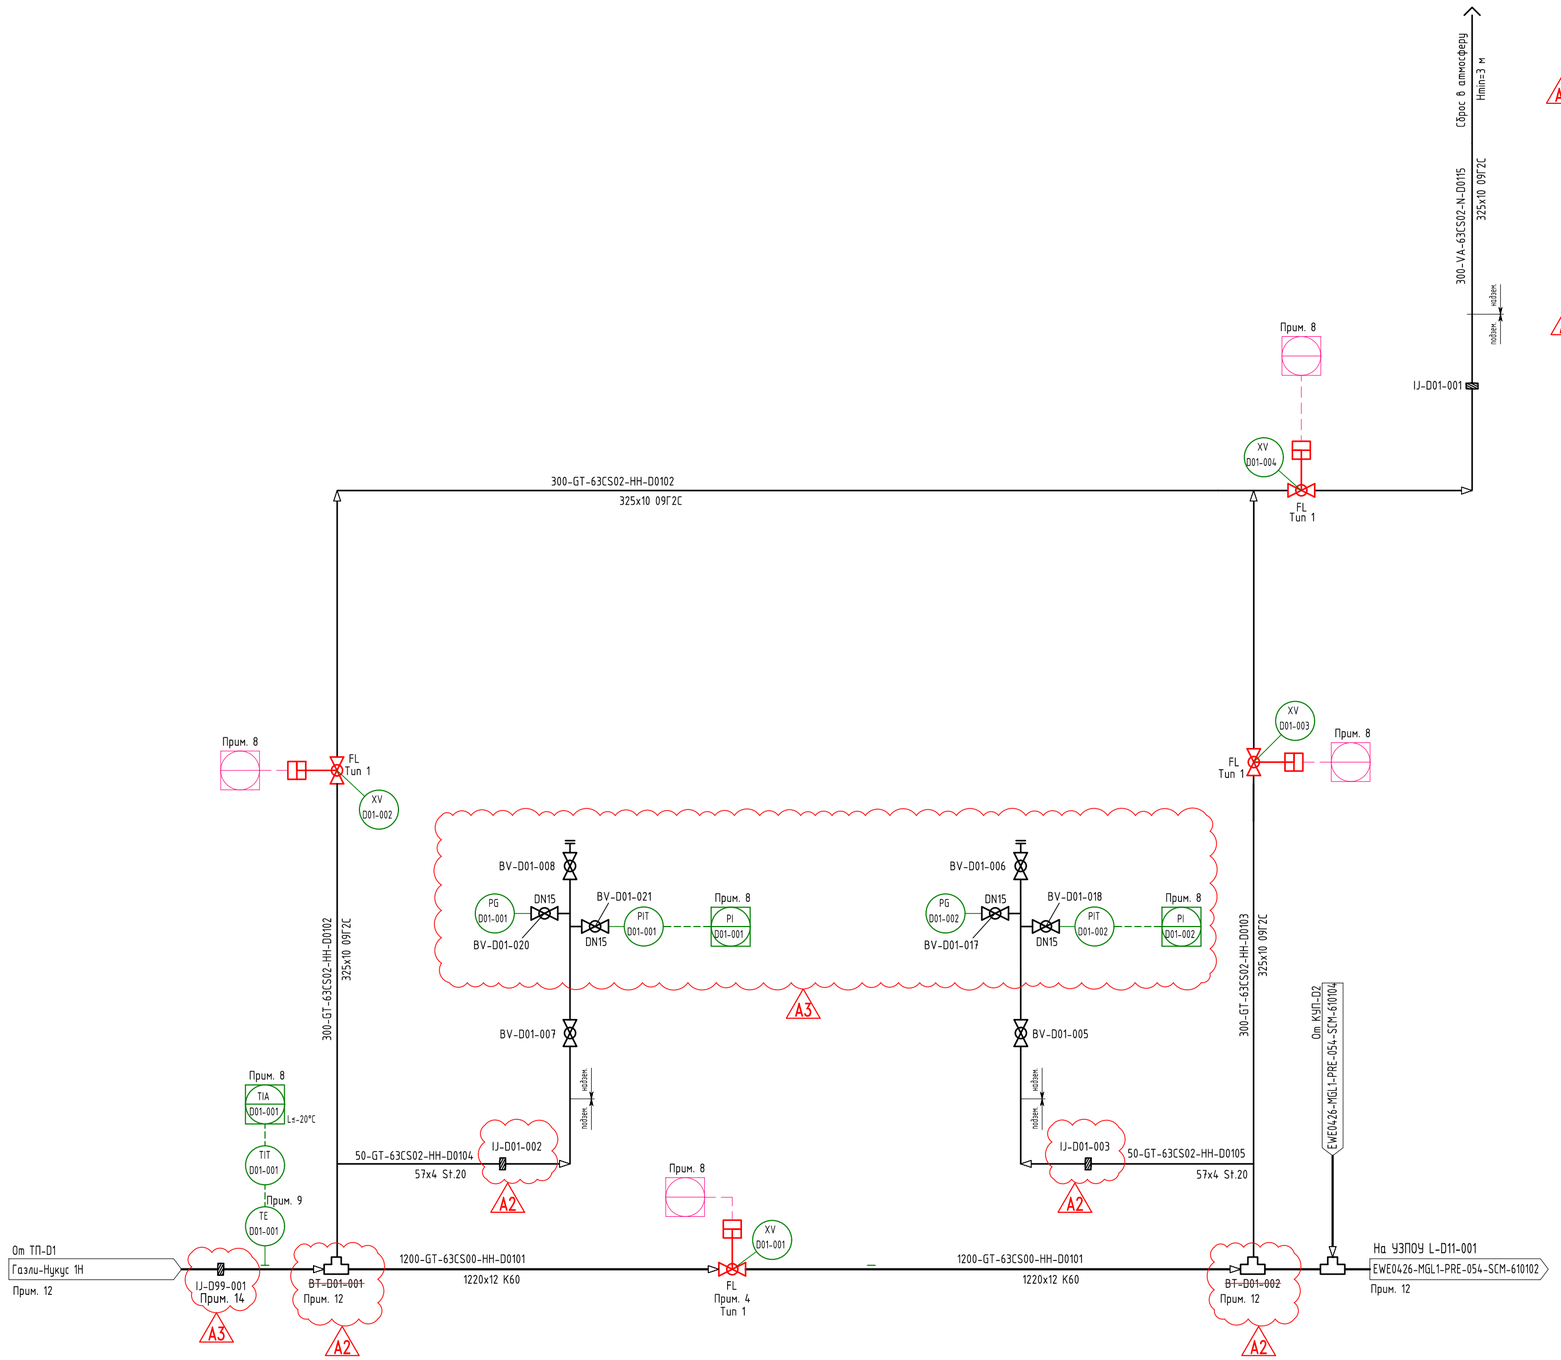


Примечания:

1. Основные условные обозначения оборудования и КИПиА – см. EWE0426-MGL1-PRE-054-PID-610113.
2. Удалено.
3. Удалено.
4. Полнопроходной шаровой кран с пневмогидроприводом, с автоматом аварийного закрытия крана.
5. Наружное покрытие надземных трубопроводов выполнить из материалов стойких к воздействию ультрафиолетового излучения.
6. Подробные схемы подключений кранов с пневмогидроприводами – см. EWE0426-MGL1-PRE-054-PID-610113, типовой узел для крана с пневмогидроприводом.
7. Тэговые номера тройников указаны только для тройников с решеткой. В местах, где тэговые номера не указаны принять как тройник без решетки. (A2)
8. Предусмотренно автоматическое управление ЗРА с учетом дальнейшего внедрения системы SCADA (система дистанционного мониторинга и управления).
9. Датчик температуры TE-D01-001 – накладного типа для поверхностного монтажа на трубу газопровода.
10. Теговые номера участков одного трубопровода идентичны друг другу и отличаются обозначением изоляции при переходах надземной и подземной прокладки: N-без изоляции, НН-гидроизоляция от почвенной коррозии.
11. Удалено.
12. На схеме указано основное направление потока газа, согласно схеме PFD, см. EWE0426-MGL1-PRE-054-PFD-610101. В процессе эксплуатации поток может быть направлен в обратном направлении.
13. Трубный аккумулятор, стояки отбора и стояки подачи импульсного газа исключены из технологической схемы в ревизии R2 и R3 в связи с применением аккумуляторов в составе привода кранов, в соответствии с решениями принятыми на совещании от 08.06.2026 г. между ООО «Probuild Generation» и проектным институтом. (A3)
14. Изолирующая вставка установлена на линейном трубопроводе, подробней см. проект ЭХЗ. (A3)

Крановый узел #D01	
Номинальное давление (МПа)	6,3
Расчетная температура (°С)	-26,9...+85
Рабочее давление (МПа)	5,5
Рабочая температура (°С)	-20...+40

Рев.	Дата	Назначение ревизии	Проверил	Утвердил
A3	10.09.2026	Утверждено для строительства		
A2	15.07.2026	Утверждено для строительства		
A1	06.07.2026	Утверждено для строительства		
R3	12.06.2026	Выпущено для рассмотрения		
R2	03.06.2026	Выпущено для рассмотрения		
R1	08.05.2026	Выпущено для рассмотрения		

ЗАКАЗЧИК: UTG ГЕНЕРАЛЬНЫЙ ПОДРЯДЧИК: UET ПОДРЯДЧИК: PBG ГЕНЕРАЛЬНЫЙ ПРОЕКТИРОВЩИК: EAST WEST ENGINEERING

Изм.	Кол.уч.	Лист	№док.	Подпись	Дата	EWE0426-MGL1-PRE-054-SCM-610103-A3		
						«СТРОИТЕЛЬСТВО НОВЫХ НИТОК (УЧАСТКОВ) ГАЗОПРОВОДОВ «ГАЗЛИ – САРИМОЙ» И «АКЧАЛОК – ГАЗЛИ – НУКУС» ОБЩЕЙ ПРОТЯЖЕННОСТЬЮ НЕ МЕНЕЕ 275 КМ».		
ГИП		Кирпичников С.			09.2026	ГАЗОПРОВОД «ГАЗЛИ-САРИМОЙ» (54 КМ)	Стадия	Лист	Листов
Нач.отд.		Рябинин А.			09.2026		РД	1	1
Исполн.		Юлдашев И.			09.2026	Линейный крановый узел DN1200 КУП-D1. Схема трубной обвязки и КИПиА. P&ID	ООО "EAST-WEST Engineering" г. Ташкент 2026г.		
Н.контр		Кирпичников С.			09.2026				

Взам. инв. №

Подпись и дата

Инв.№ подл.