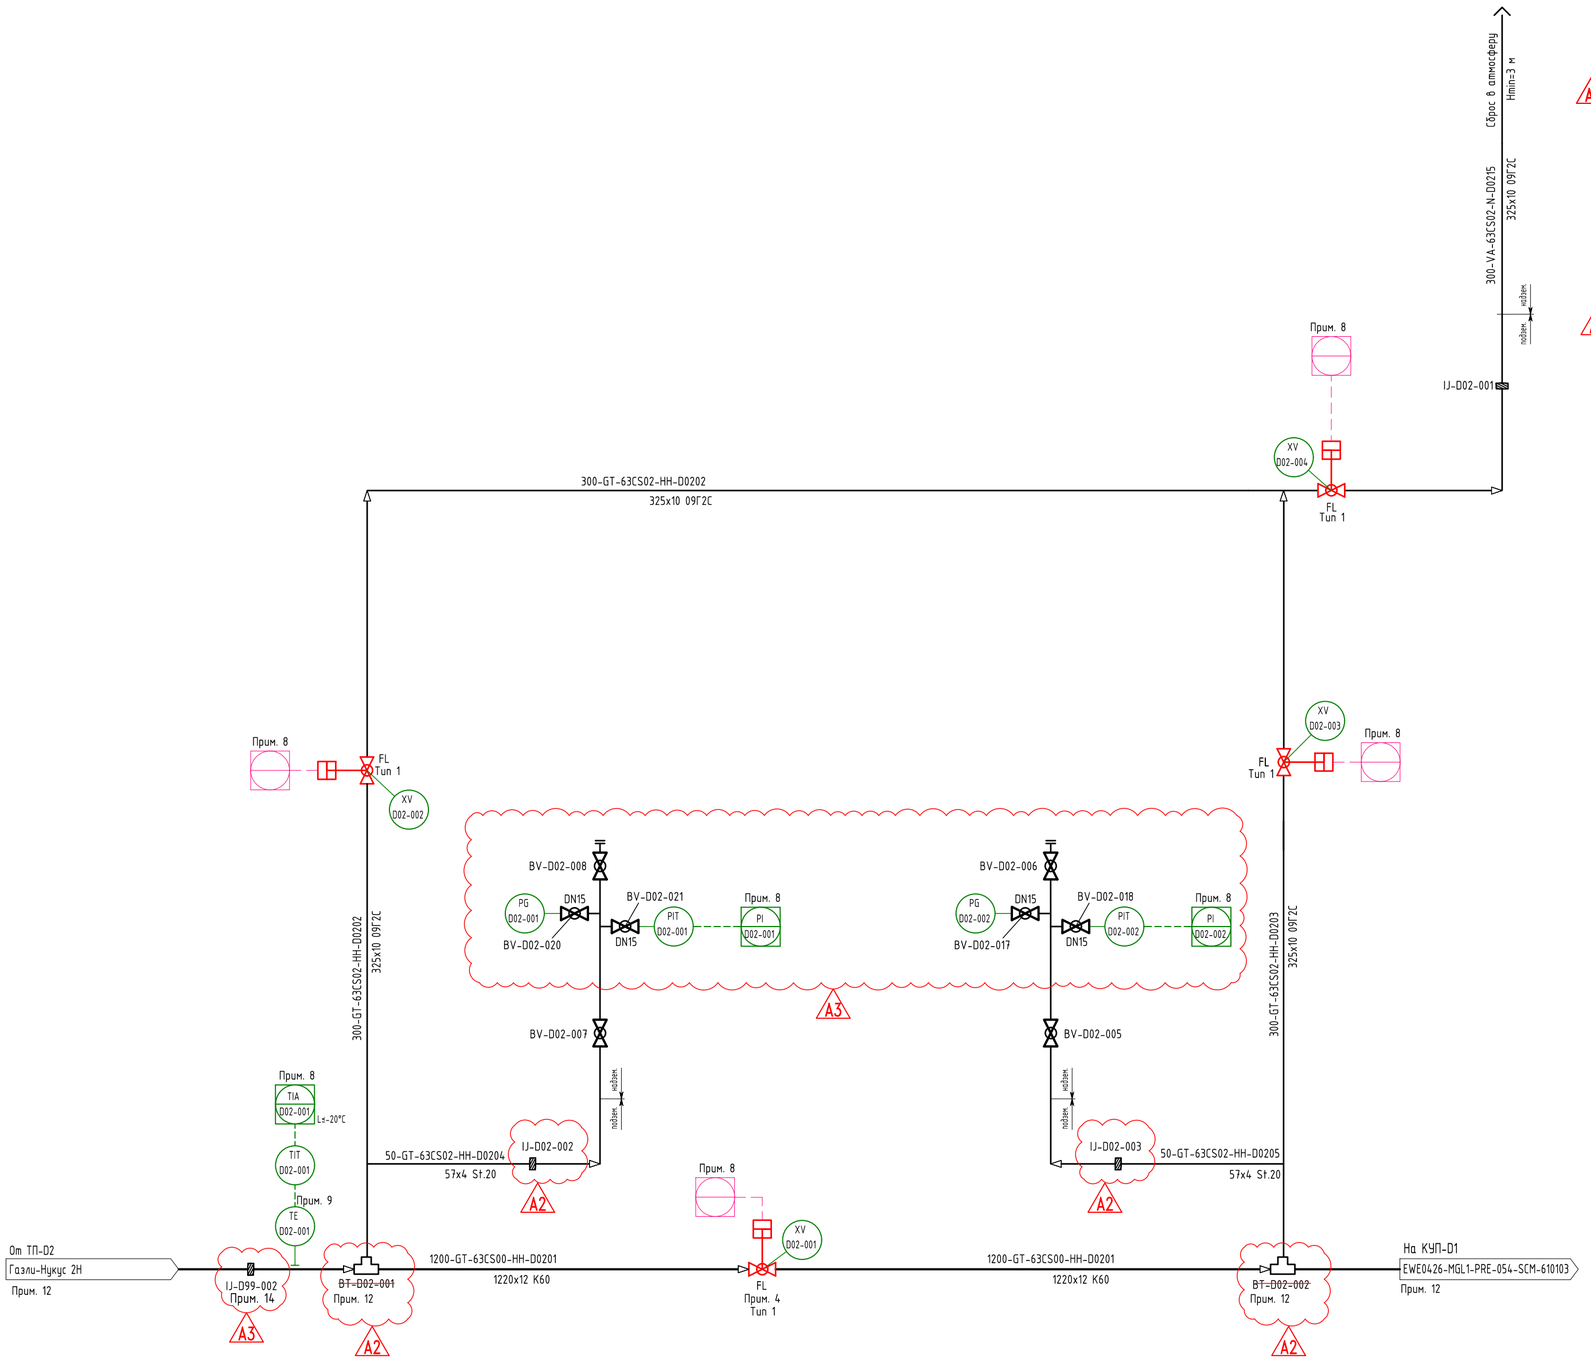



Примечания:

1. Основные условные обозначения оборудования и КИПиА – см. EWE0426-MGL1-PRE-054-PID-610113.
2. Удалено.
3. Удалено.
4. Полнопроходной шаровой кран с пневмогидроприводом, с автоматом аварийного закрытия крана.
5. Наружное покрытие надземных трубопроводов выполнить из материалов стойких к воздействию ультрафиолетового излучения.
6. Подробные схемы подключений кранов с пневмогидроприводами – см. EWE0426-MGL1-PRE-054-PID-610113, типовой узел для крана с пневмогидроприводом.
7. Тэговые номера тройников указаны только для тройников с решеткой. В местах, где тэговые номера не указаны принять как тройник без решетки. (A2)
8. Предусмотренно автоматическое управление ЗРА с учетом дальнейшего внедрения системы SCADA (система дистанционного мониторинга и управления).
9. Датчик температуры TE-D01-001 – накладного типа для поверхностного монтажа на трубу газопровода.
10. Теговые номера участков одного трубопровода идентичны друг другу и отличаются обозначением изоляции при переходах надземной и подземной прокладки: N-без изоляции, HH-гидроизоляция от почвенной коррозии.
11. Удалено.
12. На схеме указано основное направление потока газа, согласно схеме PFD, см. EWE0426-MGL1-PRE-054-PFD-610101. В процессе эксплуатации поток может быть направлен в обратном направлении.
13. Трубный аккумулятор, стояки отбора и стояки подачи импульсного газа исключены из технологической схемы в ревизии R2 и R3 в связи с применением аккумуляторов в составе привода кранов, в соответствии с решениями принятыми на совещании от 08.06.2026 г. между ООО «Probuild Generation» и проектным институтом. (A3)
14. Изолирующая вставка установлена на линейном трубопроводе, подробней см. проект ЭХЗ. (A3)

| Крановый узел #D02 | |
|---|---|
| Номинальное давление (МПа) | 6,3 |
| Расчетная температура (°C) | -26,9...+85 |
| Рабочее давление (МПа) | 5,5 |
| Рабочая температура (°C) | -20...+40 |

| Рев. | Дата | Назначение ревизии | Проверил | Утвердил |
|---|---|---|---|---|
| A3 | 10.09.2026 | Утверждено для строительства | | |
| A2 | 15.07.2026 | Утверждено для строительства | | |
| A1 | 06.07.2026 | Утверждено для строительства | | |
| R3 | 12.06.2026 | Выпущено для рассмотрения | | |
| R2 | 03.06.2026 | Выпущено для рассмотрения | | |
| R1 | 08.05.2026 | Выпущено для рассмотрения | | |

ЗАКАЗЧИК: UTG ГЕНЕРАЛЬНЫЙ ПОДРЯДЧИК: UET ПОДРЯДЧИК: PBG ГЕНЕРАЛЬНЫЙ ПРОЕКТИРОВЩИК: EAST WEST ENGINEERING

| Изм. | Кол.уч. | Лист | №док. | Подпись | Дата | EWE0426-MGL1-PRE-054-SCM-610104-A3 | | |
|---|---|---|---|---|---|---|---|---|
| | | | | | | «СТРОИТЕЛЬСТВО НОВЫХ НИТОК (УЧАСТКОВ) ГАЗОПРОВОДОВ «ГАЗЛИ – САРИМОЙ» И «АКЧАЛОК – ГАЗЛИ – НУКУС» ОБЩЕЙ ПРОТЯЖЕННОСТЬЮ НЕ МЕНЕЕ 275 КМ». | | |
| ГИП | | Кирпичников С. | | | 09.2026 | ГАЗОПРОВОД «ГАЗЛИ-САРИМОЙ» (54 КМ) | Стадия | Лист | Листов |
| Нач.отд. | | Рябинин А. | | | 09.2026 | | РД | 1 | 1 |
| Исполн. | | Юлдашев И. | | | 09.2026 | Линейный крановый узел DN1200 КУП-D2. Схема трубной обвязки и КИПиА. P&ID | ООО "EAST-WEST Engineering" г. Ташкент 2026г. | | |
| Н.контр | | Кирпичников С. | | | 09.2026 | | | | |

Взам. инв. №

Подпись и дата

Инв.№ подл.

Формат / Format A2