Примечания:

1. Основные условные обозначения оборудования и КИПиА - см. EWE0426-MGL1-PRE-054-SCM-610113.
2. Удалено.
3. Удалено.
4. Полнопроходной шаровой кран с пневмогидроприводом, с автоматом аварийного закрытия крана.
5. Наружное покрытие надземных трубопроводов выполнить из материалов стойких к воздействию ультрафиолетового излучения.
6. Подробные схемы подключений кранов с пневмогидроприводами - см. EWE0426-MGL1-PRE-054-SCM-610113, типовой узел для крана с пневмогидроприводом.
7. Тэговые номера тройников указаны только для тройников с решеткой. В местах, где тэговые номера не указаны принять как тройник без решетки.
8. Предусмотренно автоматическое уравление ЗРА с учетом дальнейшего внедрения системы SCADA (система дистанционного мониторинга и управления).
9. Датчик температуры TE-D08-001 - накладного типа для поверхностного монтажа на трубу газопровода.
10. Теговые номера участков одного трубопровода идентичны друг другу и отличаются обозначением изоляции при переходах надземной и подземной прокладки: N-без изоляции, HH-гидроизоляция от почвенной коррозии.
11. Удалено.
12. На схеме указано основное направление потока газа, согласно схеме PFD, см. EWE0426-MGL1-PRE-054-PFD-610101. В процессе эксплуатации поток может быть направлен в обратном направлении.
13. Трубный аккумулятор, стояки отбора и стояки подачи импульсного газа исключены из технологической схемы в ревизии R2 и R3 в связи с применением аккумуляторов в составе привода кранов, в соответствии с решениями принятыми на совещании от 05.06.2026 г. между ООО «Probuild Generation» и проектным институтом.
14. Изолирующая вставка установлена на линейном трубопроводе, подробней см. проект ЭХЗ.

A2 A3

Крановый узел #D08	
Номинальное давление (МПа)	6,3
Расчетная температура (°С)	-26,9...+85
Рабочее давление (МПа)	5,5
Рабочая температура (°С)	-20...+40

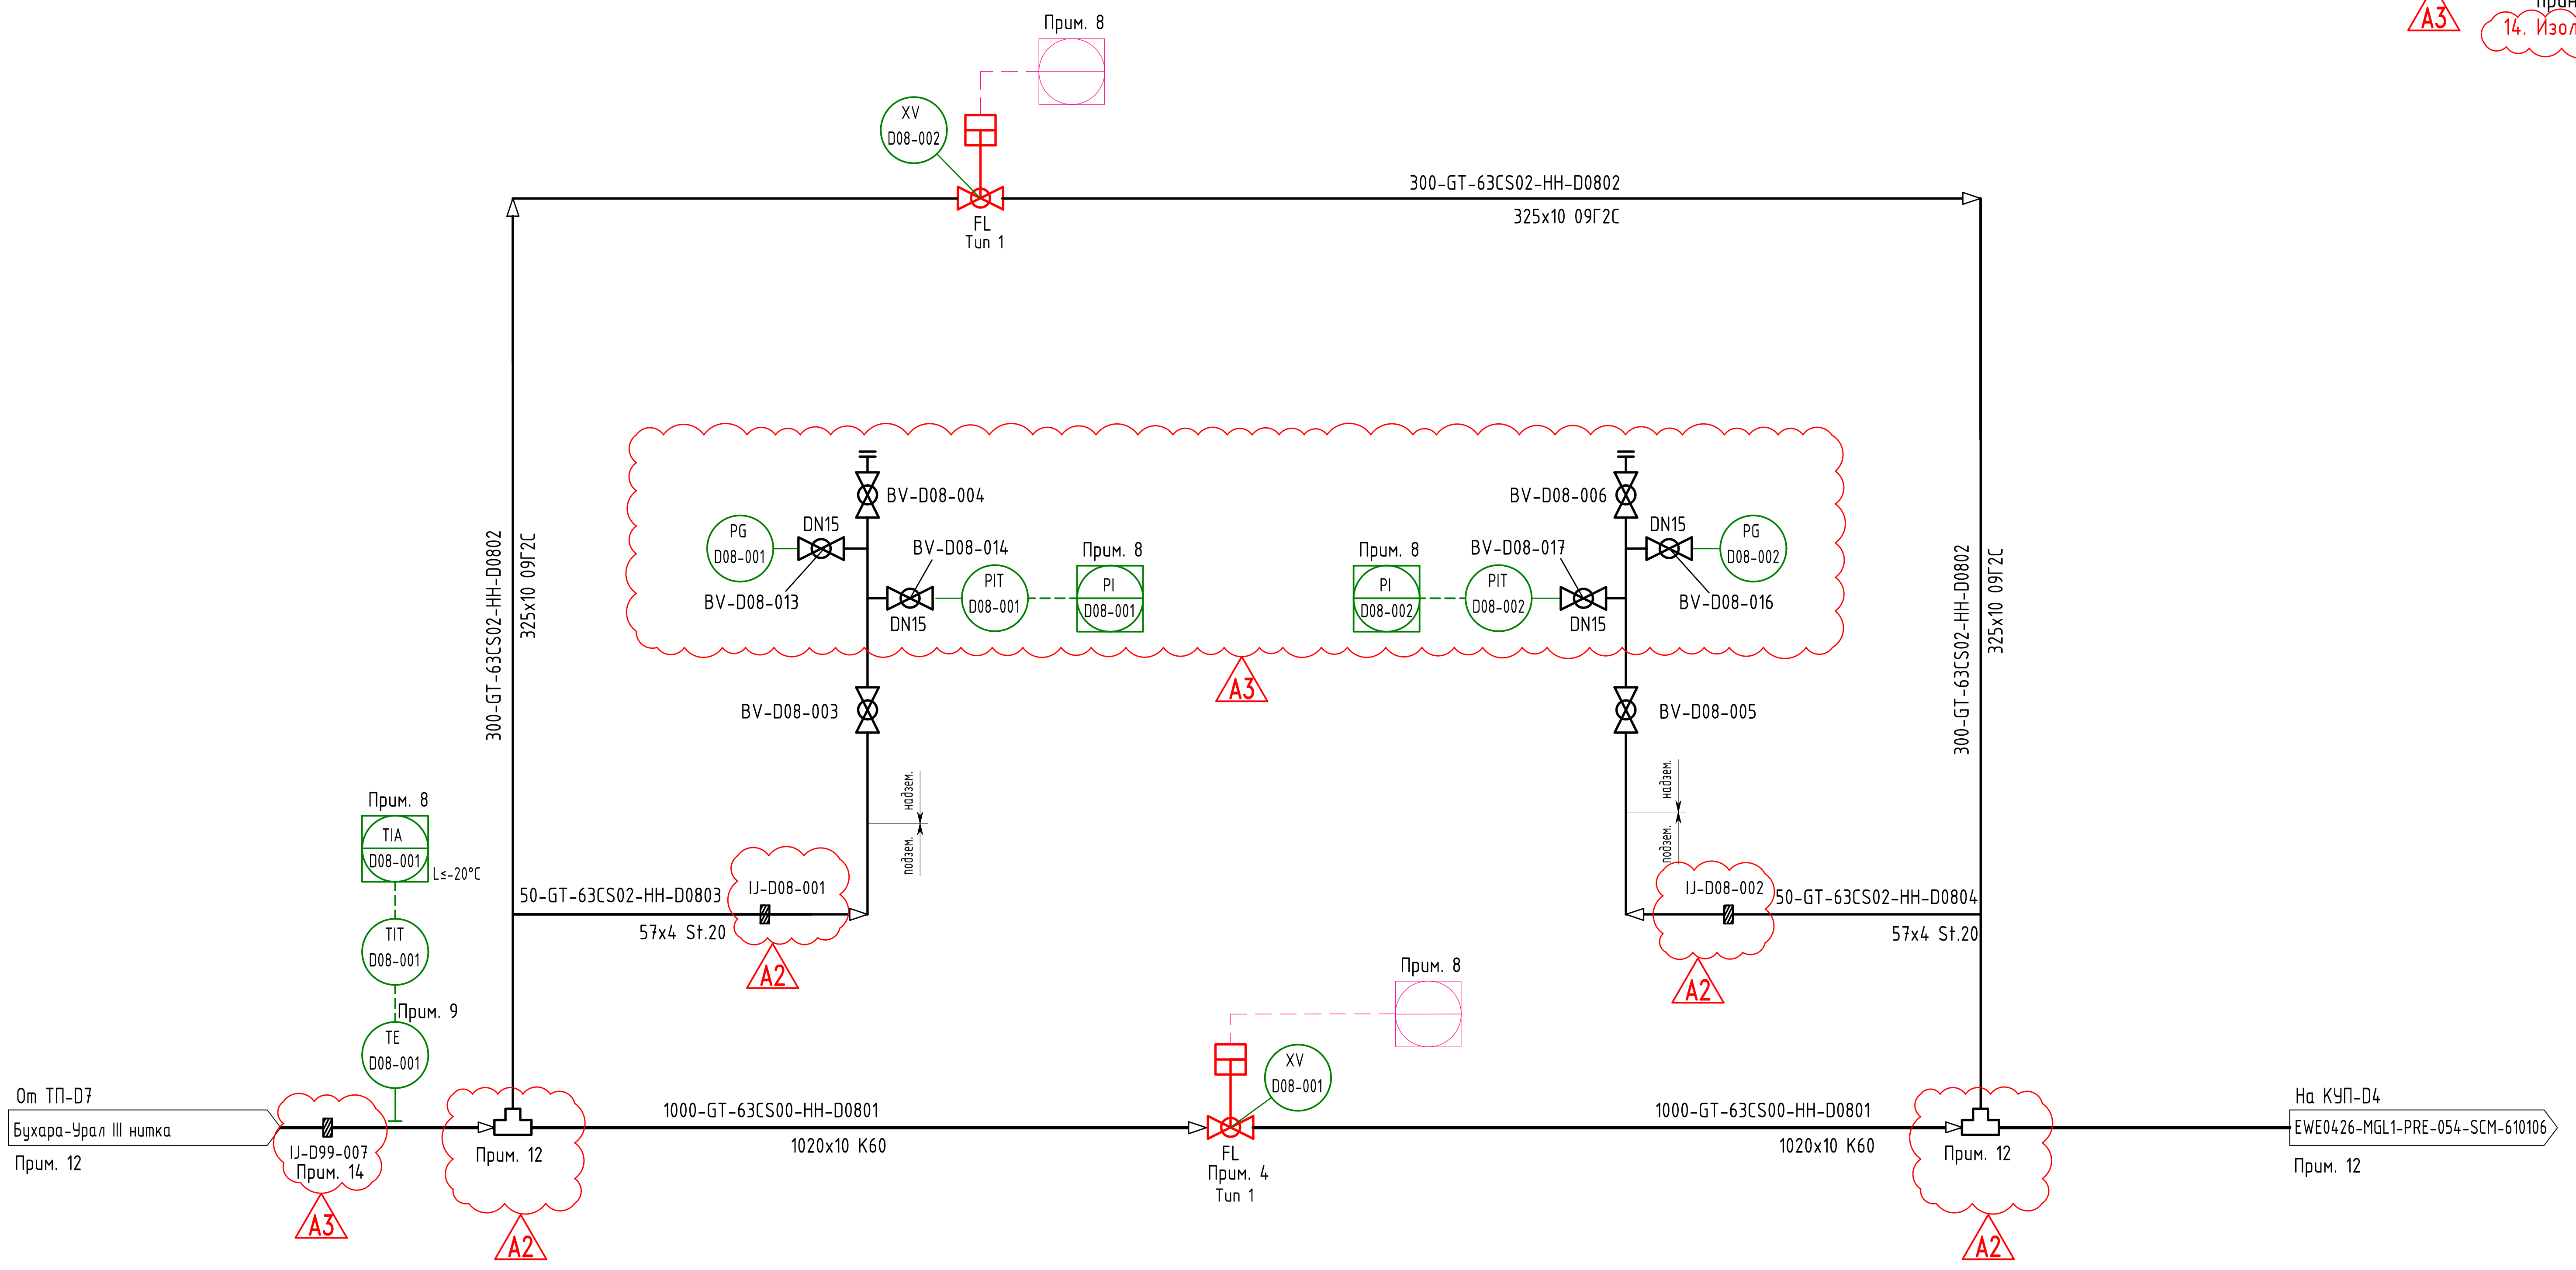
Прим. 8
XV
D08-002
FL
Тип 1
300-GT-63CS02-HH-D0802
325x10 09Г2С
300-GT-63CS02-HH-D0802
325x10 09Г2С
BV-D08-004
PG
D08-001
DN15
BV-D08-013
BV-D08-014
PIT
D08-001
Прим. 8
PI
D08-001
DN15
Прим. 8
PI
D08-002
PIT
D08-002
BV-D08-017
DN15
BV-D08-006
DN15
PG
D08-002
BV-D08-016
A3
BV-D08-003
BV-D08-005
надзем.
подзем.
Прим. 8
TIA
D08-001
L≤-20°C
TIT
D08-001
Прим. 9
TE
D08-001
50-GT-63CS02-HH-D0803
57x4 St.20
IJ-D08-001
A2
IJ-D08-002
50-GT-63CS02-HH-D0804
57x4 St.20
A2
Прим. 8
XV
D08-001
От ТП-D7
Бухара-Урал III нитка
Прим. 12
IJ-D99-007
Прим. 14
A3
Прим. 12
A2
1000-GT-63CS00-HH-D0801
1020x10 K60
FL
Прим. 4
Тип 1
1000-GT-63CS00-HH-D0801
1020x10 K60
Прим. 12
A2
На КУП-D4
EWE0426-MGL1-PRE-054-SCM-610106
Прим. 12

Рев.	Дата	Назначение ревизии	Проверил	Утвердил
A3	10.09.2026	Утверждено для строительства		
A2	14.07.2026	Утверждено для строительства		
A1	06.07.2026	Утверждено для строительства		
R3	12.06.2026	Выпущено для рассмотрения		
R2	04.06.2026	Выпущено для рассмотрения		
R1	08.05.2026	Выпущено для рассмотрения		

ЗАКАЗЧИК: UTG UZTRANSGAZ
ГЕНЕРАЛЬНЫЙ ПОДРЯДЧИК: UET UZBEKENERGOTAMIR
ПОДРЯДЧИК: PBG Pro Build Generation
ГЕНЕРАЛЬНЫЙ ПРОЕКТИРОВЩИК: EAST WEST ENGINEERING

EWE0426-MGL1-PRE-054-SCM-610110-A3

«СТРОИТЕЛЬСТВО НОВЫХ НИТОК (УЧАСТКОВ) ГАЗОПРОВОДОВ «ГАЗЛИ - САРИМОЙ» И «АКЧАЛОК - ГАЗЛИ - НУКУС» ОБЩЕЙ ПРОТЯЖЕННОСТЬЮ НЕ МЕНЕЕ 275 КМ».

Изм.	Кол.уч.	Лист	№док.	Подпись	Дата
ГИП		Кирпичников С.			09.2026
Нач.отд.		Рябинин А.			09.2026
Исполн.		Юлдашев И.			09.2026
Н.контр		Кирпичников С.			09.2026

ГАЗОПРОВОД «ГАЗЛИ-САРИМОЙ» (54 КМ)

Стадия	Лист	Листов
РД	1	1

Крановый узел DN1000 КУП-D8
Схема трубной обвязки и КИПиА. P&ID

EAST WEST ENGINEERING
ООО "EAST-WEST Engineering"
г. Ташкент 2026г.

Взам. инв. №
Подпись и дата
Инв.№ подл.

Формат / Format A2