Примечания:

1. Основные условные обозначения оборудования и КИПиА - см. EWE0426-MGL1-PRE-054-SCM-610113.
2. Удалено.
3. Удалено.
4. Полнопроходной шаровой кран с пневмогидроприводом, с автоматом аварийного закрытия крана.
5. Наружное покрытие надземных трубопроводов выполнить из материалов стойких к воздействию ультрафиолетового излучения.
6. Подробные схемы подключений кранов с пневмогидроприводами - см. EWE0426-MGL1-PRE-054-SCM-610113, типовой узел для крана с пневмогидроприводом.
7. Тэговые номера тройников указаны только для тройников с решеткой. В местах, где тэговые номера не указаны принять как тройник без решетки.
8. Предусмотренно автоматическое уравление ЗРА с учетом дальнейшего внедрения системы SCADA (система дистанционного мониторинга и управления).
9. Датчик температуры TE-D10-001 - накладного типа для поверхностного монтажа на трубу газопровода.
10. Теговые номера участков одного трубопровода идентичны друг другу и отличаются обозначением изоляции при переходах надземной и подземной прокладки: N-без изоляции, HH-гидроизоляция от почвенной коррозии.
11. Удалено.
12. На схеме указано основное направление потока газа, согласно схеме PFD, см. EWE0426-MGL1-PRE-054-PFD-610101. В процессе эксплуатации поток может быть направлен в обратном направлении.
13. Трубный аккумулятор, стояки отбора и стояки подачи импульсного газа исключены из технологической схемы в связи с применением аккумуляторов в составе привода кранов, в соответствии с решениями принятыми на совещании от 05.06.2026 г. между ООО «Probuild Generation» и проектным институтом.
14. Изолирующая вставка установлена на линейном трубопроводе, подробней см. проект ЭХЗ.

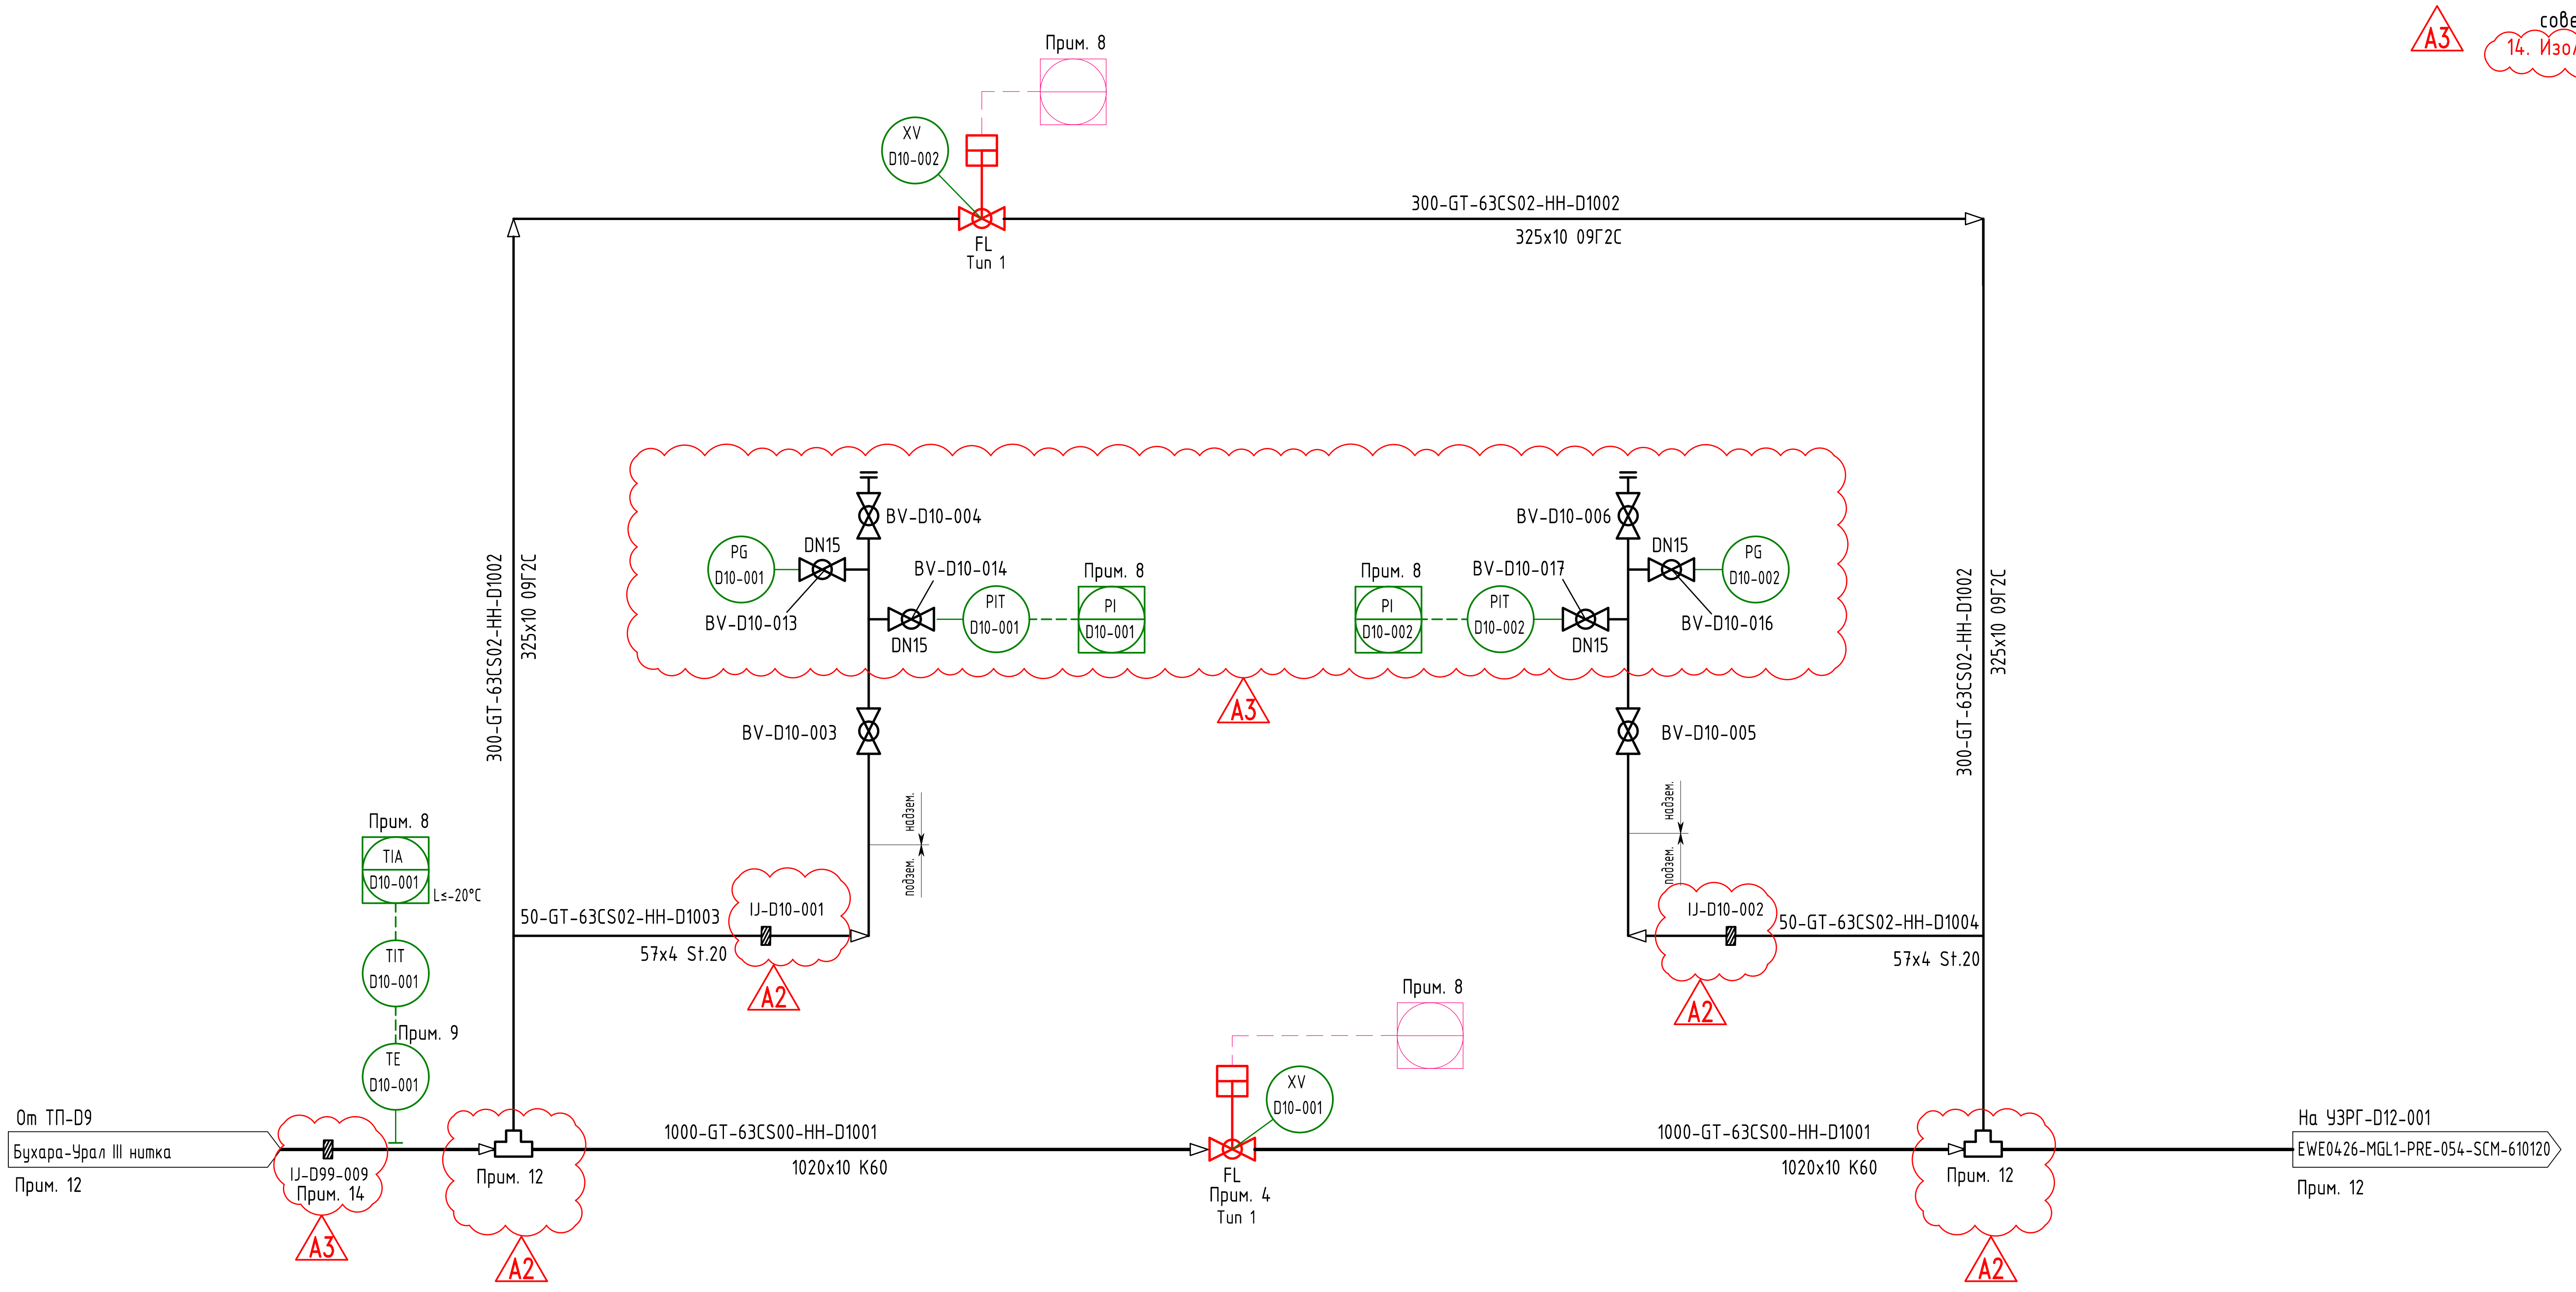

| Крановый узел #D10 | |
|---|---|
| Номинальное давление (МПа) | 6,3 |
| Расчетная температура (°C) | -26,9...+85 |
| Рабочее давление (МПа) | 5,5 |
| Рабочая температура (°C) | -20...+40 |

| Рев. | Дата | Назначение ревизии | Проверил | Утвердил |
|---|---|---|---|---|
| | | | | |
| | | | | |
| A3 | 10.09.2026 | Утверждено для строительства | | |
| A2 | 14.07.2026 | Утверждено для строительства | | |
| A1 | 06.07.2026 | Утверждено для строительства | | |
| R1 | 12.06.2026 | Выпущено для рассмотрения | | |

ЗАКАЗЧИК:
ГЕНЕРАЛЬНЫЙ ПОДРЯДЧИК:
ПОДРЯДЧИК:
ГЕНЕРАЛЬНЫЙ ПРОЕКТИРОВЩИК:

# EWE0426-MGL1-PRE-054-SCM-610112-A3

«СТРОИТЕЛЬСТВО НОВЫХ НИТОК (УЧАСТКОВ) ГАЗОПРОВОДОВ «ГАЗЛИ - САРИМОЙ» И «АКЧАЛОК - ГАЗЛИ - НУКУС» ОБЩЕЙ ПРОТЯЖЕННОСТЬЮ НЕ МЕНЕЕ 275 КМ».

| Изм. | Кол.уч. | Лист | №док. | Подпись | Дата |
|---|---|---|---|---|---|
| ГИП | | Кирпичников С. | | | 09.2026 |
| Нач.отд. | | Рябинин А. | | | 09.2026 |
| Исполн. | | Юлдашев И. | | | 09.2026 |
| Н.контр | | Кирпичников С. | | | 09.2026 |

ГАЗОПРОВОД «ГАЗЛИ-САРИМОЙ» (54 КМ)

| Стадия | Лист | Листов |
|---|---|---|
| РД | 1 | 1 |

Крановый узел DN1000 КУП-D10.
Схема трубной обвязки и КИПиА. P&ID

ООО "EAST-WEST Engineering"
г. Ташкент 2026г.

Взам. инв. №
Подпись и дата
Инв.№ подл.

Формат / Format A2