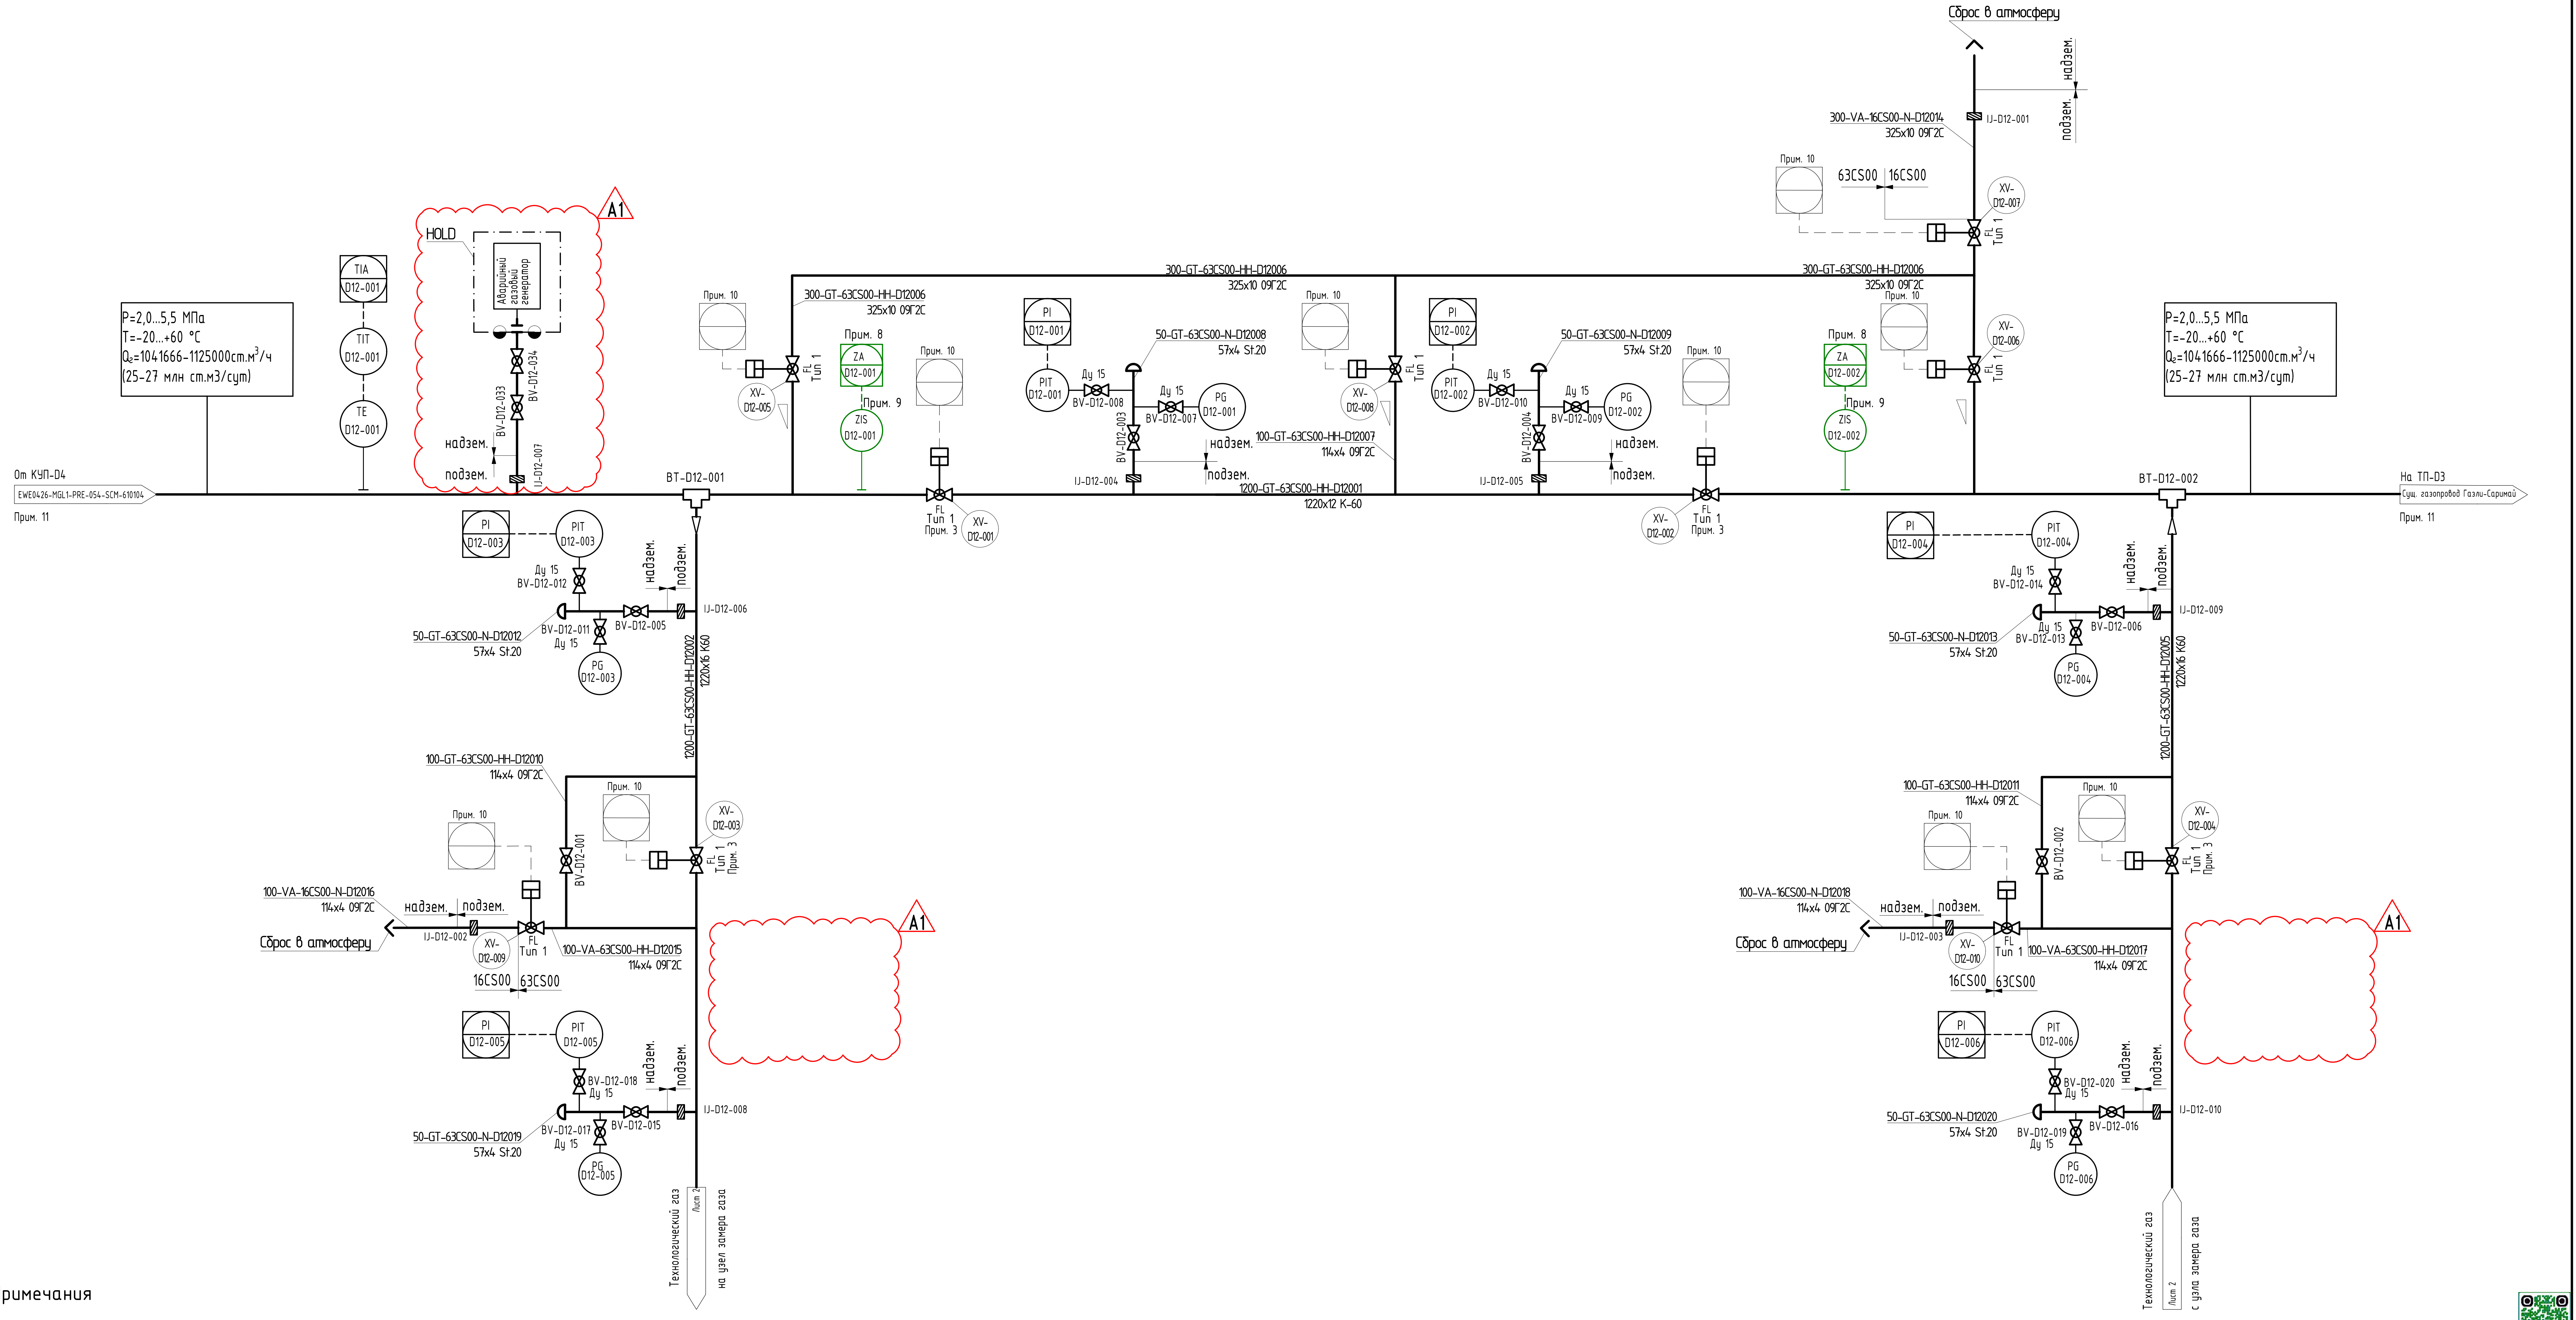
Сброс в атмосферу
надзем.
подзем.
300-VA-16CS00-N-D12014
325x10 09Г2С
IJ-D12-001
Прим. 10
63CS00 | 16CS00
XV-D12-007
FL Тип 1
300-GT-63CS00-HH-D12006
325x10 09Г2С
XV-D12-006
HOLD
Аварийный газовый генератор
BV-D12-033
BV-D12-034
IJ-D12-007
A1
TIA D12-001
TIT D12-001
TE D12-001
P=2,0...5,5 МПа
T=-20...+60 °C
Q₂=1041666-1125000ст.м³/ч
(25-27 млн ст.м3/сут)
От КУП-D4
EWE0426-MGL1-PRE-054-SCM-610104
Прим. 11
BT-D12-001
XV-D12-005
Прим. 8
ZA D12-001
Прим. 9
ZIS D12-001
XV-D12-001
Прим. 3
PI D12-001
PIT D12-001
Ду 15
BV-D12-008
BV-D12-007
PG D12-001
50-GT-63CS00-N-D12008
57x4 St.20
BV-D12-003
IJ-D12-004
XV-D12-008
100-GT-63CS00-HH-D12007
114x4 09Г2С
1200-GT-63CS00-HH-D12001
1220x12 K-60
PI D12-002
PIT D12-002
BV-D12-010
BV-D12-009
PG D12-002
50-GT-63CS00-N-D12009
57x4 St.20
BV-D12-004
IJ-D12-005
XV-D12-002
ZA D12-002
ZIS D12-002
BT-D12-002
На ТП-D3
Сущ. газопровод Газли-Саримай
PI D12-003
PIT D12-003
BV-D12-012
BV-D12-011
BV-D12-005
PG D12-003
50-GT-63CS00-N-D12012
57x4 St.20
IJ-D12-006
1200-GT-63CS00-HH-D12002
1220x16 K60
PI D12-004
PIT D12-004
BV-D12-014
BV-D12-013
BV-D12-006
PG D12-004
50-GT-63CS00-N-D12013
57x4 St.20
IJ-D12-009
1200-GT-63CS00-HH-D12005
1220x16 K60
100-GT-63CS00-HH-D12010
114x4 09Г2С
BV-D12-001
XV-D12-003
100-VA-16CS00-N-D12016
114x4 09Г2С
IJ-D12-002
XV-D12-009
16CS00 | 63CS00
100-VA-63CS00-HH-D12015
114x4 09Г2С
PI D12-005
PIT D12-005
BV-D12-018
BV-D12-017
BV-D12-015
PG D12-005
50-GT-63CS00-N-D12019
57x4 St.20
IJ-D12-008
Технологический газ
Лист 3
на узел замера газа
100-GT-63CS00-HH-D12011
114x4 09Г2С
BV-D12-002
XV-D12-004
100-VA-16CS00-N-D12018
114x4 09Г2С
IJ-D12-003
XV-D12-010
100-VA-63CS00-HH-D12017
114x4 09Г2С
PI D12-006
PIT D12-006
BV-D12-020
BV-D12-019
BV-D12-016
PG D12-006
50-GT-63CS00-N-D12020
57x4 St.20
IJ-D12-010
Технологический газ
Лист 2
с узла замера газа

Примечания

1. Основные условные обозначения оборудования и КИПиА - см. EWE0426-MGL1-PRE-054-PID-610113.
2. Подробные схемы подключений кранов с пневмогидроприводами - см. EWE0426-MGL1-PRE-054-PID-610113, типовой узел для крана с пневмогидроприводом.
3. Полнопроходной шаровой кран с пневмогидроприводом, с автоматом аварийного закрытия крана.
4. На узле замера расхода газа УЗРГ-D12-001 предусмотрены 4 рабочих и 1 резервная измерительные линии. Количество линий, задействованных для замера (от 1 до 4) будет зависеть от фактического расхода газа. Нижний предел измерений прибора учёта газа, обеспечивающий нормированную погрешность измерений при стандартных условиях составляет Qmin = 2,0 млн. м3/сут (83333 м3/час).
5. Предусмотреть реверсивное движение газа.
6. Выдержать прямолинейные участки расстоянием не менее 10 диаметров до и после измерительной диафрагмы. Длины съёмных участков будут определяться изготовителем замерных устройств.
7. Предусмотреть фланцевые катушки для демонтажа расходомерных устройств при проведении испытания трубопроводов под давлением.
8. Теговые номера участков одного трубопровода идентичны друг другу и отличаются обозначением изоляции при переходах надземной и подземной прокладки: N-без изоляции, HH-гидроизоляция от почвенной коррозии.
9. Сигнализаторы прохождения очистного устройства ZIS-D12-001 и ZIS-D12-002, Датчик температуры TE-D12-001 - накладного типа для поверхностного монтажа на трубу газопровода.
10. Предусмотренно автоматическое уравление ЗРА с учетом дальнейшего внедрения системы SCADA (система дистанционного мониторинга и управления)
11. На схеме указано основное направление потока газа, согласно схеме PFD, см. EWE0426-MGL1-PRE-054-PFD-610101. В процессе эксплуатации поток может быть направлен в обратном направлении.
12. Ресивер импульсного газа, стояки отбора и стояки подачи импульсного газа исключены из технологической схемы связи с применением аккумуляторов в составе привода кранов, в соответствии с решениями принятыми на совещании от 05.06.2026 г. между ~~ООО «Probuild Generation» и проектным институтом.~~
13. Ручной отбор проб выполняется в помещении блока аналитического оборудования.
14. Пробоотборные зонды и их узлы подключения входят в поставку блока аналитического оборудования. Отсекающая арматура на пробоотборных линиях предусмотрена в конструкции пробоотборных зондов.

A1

Взам. инв. №
Подпись и дата
Инв.№ подл.

| Рев. | Дата | Назначение ревизии | Проверил | Утвердил |
|---|---|---|---|---|
| A1 | 31.07.2026 | Утверждено для строительства | | |
| R2 | 16.07.2026 | Выпущено для рассмотрения | | |
| R1 | 26.06.2026 | Выпущено для рассмотрения | | |

ЗАКАЗЧИК: UTG UZTRANSGAZ
ГЕНЕРАЛЬНЫЙ ПОДРЯДЧИК: UET UZBEKENERGOTAMIR
ПОДРЯДЧИК: PBG Pro Build Generation
ГЕНЕРАЛЬНЫЙ ПРОЕКТИРОВЩИК: EAST WEST ENGINEERING

EWE0426-MGL1-PRE-054-SCM-610120-A1

«СТРОИТЕЛЬСТВО НОВЫХ НИТОК (УЧАСТКОВ) ГАЗОПРОВОДОВ «ГАЗЛИ - САРИМОЙ» И «АКЧАЛОК - ГАЗЛИ - НУКУС» ОБЩЕЙ ПРОТЯЖЕННОСТЬЮ НЕ МЕНЕЕ 275 КМ».

| Изм. | Кол.уч. | Лист | №док. | Подпись | Дата |
|---|---|---|---|---|---|
| ГИП | | Схабицкий А. | | | 07.2026 |
| Нач.отд. | | Рябинин А. | | | 07.2026 |
| Исполн. | | Юлдашев И. | | | 07.2026 |
| Н.контр | | Схабицкий А. | | | 07.2026 |

ГАЗОПРОВОД «ГАЗЛИ-САРИМОЙ» (54 КМ)

| Стадия | Лист | Листов |
|---|---|---|
| РД | 1 | 3 |

Узел замера расхода газа УЗРГ-D12-001.
Схема трубной обвязки и КИПиА. P&ID

EAST WEST ENGINEERING
ООО "EAST-WEST Engineering"
г. Ташкент 2026г.

Формат / Format A2

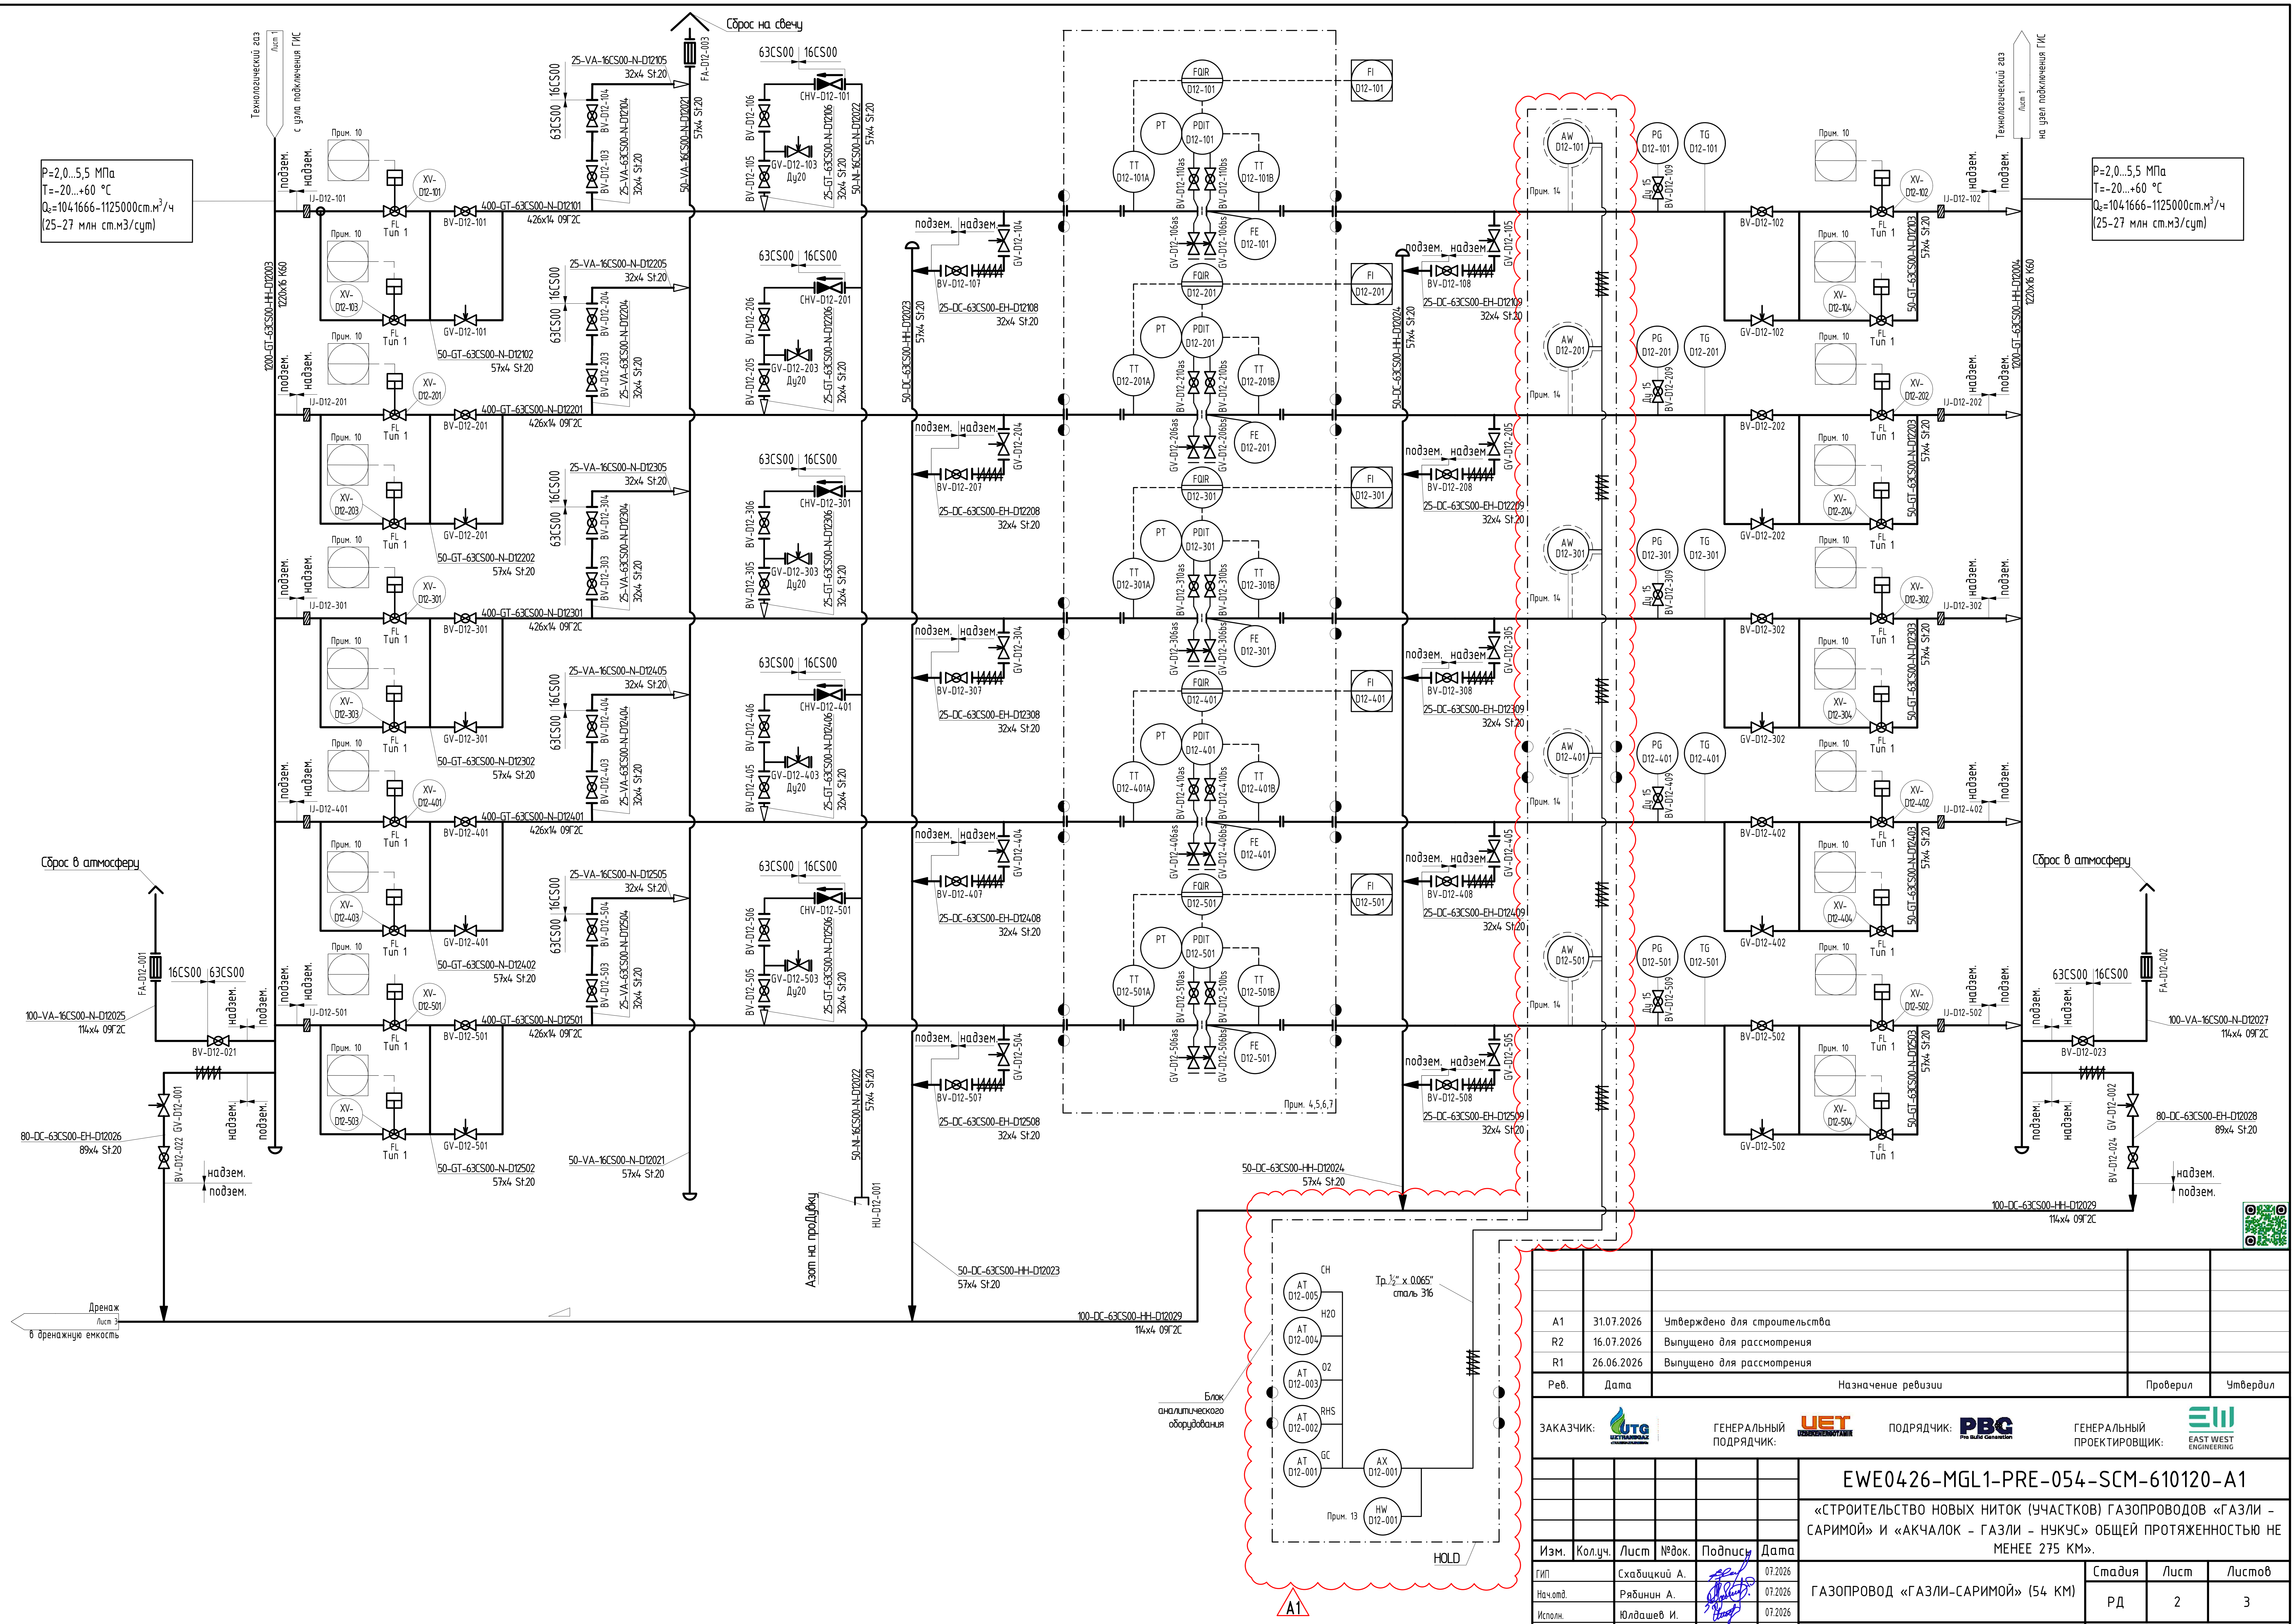
Технологический газ
Лист 1
с узла подключения ГИС
P=2,0...5,5 МПа
T=-20...+60 °C
$Q_г$=1041666-1125000ст.м$^3$/ч
(25-27 млн ст.м3/сут)
1200-GT-63CS00-HH-D12003
1220х16 К60
подзем.
надзем.
IJ-D12-101
Прим. 10
XV-D12-101
FL
Тип 1
BV-D12-101
400-GT-63CS00-N-D12101
426х14 09Г2С
XV-D12-103
GV-D12-101
50-GT-63CS00-N-D12102
57х4 St.20
IJ-D12-201
XV-D12-201
BV-D12-201
400-GT-63CS00-N-D12201
426х14 09Г2С
XV-D12-203
GV-D12-201
50-GT-63CS00-N-D12202
57х4 St.20
IJ-D12-301
XV-D12-301
BV-D12-301
400-GT-63CS00-N-D12301
426х14 09Г2С
XV-D12-303
GV-D12-301
50-GT-63CS00-N-D12302
57х4 St.20
IJ-D12-401
XV-D12-401
BV-D12-401
400-GT-63CS00-N-D12401
426х14 09Г2С
XV-D12-403
GV-D12-401
50-GT-63CS00-N-D12402
57х4 St.20
IJ-D12-501
XV-D12-501
BV-D12-501
400-GT-63CS00-N-D12501
426х14 09Г2С
XV-D12-503
GV-D12-501
50-GT-63CS00-N-D12502
57х4 St.20
Сброс в атмосферу
FA-D12-001
16CS00
63CS00
100-VA-16CS00-N-D12025
114х4 09Г2С
BV-D12-021
GV-D12-001
80-DC-63CS00-EH-D12026
89х4 St.20
BV-D12-022
Дренаж
Лист 3
в дренажную емкость
Сброс на свечу
FA-D12-003
50-VA-16CS00-N-D12021
57х4 St.20
25-VA-16CS00-N-D12105
32х4 St.20
63CS00
16CS00
BV-D12-104
BV-D12-103
25-VA-63CS00-N-D12104
32х4 St.20
25-VA-16CS00-N-D12205
BV-D12-204
BV-D12-203
25-VA-63CS00-N-D12204
25-VA-16CS00-N-D12305
BV-D12-304
BV-D12-303
25-VA-63CS00-N-D12304
25-VA-16CS00-N-D12405
BV-D12-404
BV-D12-403
25-VA-63CS00-N-D12404
25-VA-16CS00-N-D12505
BV-D12-504
BV-D12-503
25-VA-63CS00-N-D12504
CHV-D12-101
BV-D12-106
BV-D12-105
GV-D12-103
Ду20
25-GT-63CS00-N-D12106
32х4 St.20
50-NI-16CS00-N-D12022
57х4 St.20
CHV-D12-201
BV-D12-206
BV-D12-205
GV-D12-203
25-GT-63CS00-N-D12206
CHV-D12-301
BV-D12-306
BV-D12-305
GV-D12-303
25-GT-63CS00-N-D12306
CHV-D12-401
BV-D12-406
BV-D12-405
GV-D12-403
25-GT-63CS00-N-D12406
CHV-D12-501
BV-D12-506
BV-D12-505
GV-D12-503
25-GT-63CS00-N-D12506
HU-D12-001
Азот на продувку
50-DC-63CS00-HH-D12023
57х4 St.20
GV-D12-104
BV-D12-107
25-DC-63CS00-EH-D12108
32х4 St.20
GV-D12-204
BV-D12-207
25-DC-63CS00-EH-D12208
GV-D12-304
BV-D12-307
25-DC-63CS00-EH-D12308
GV-D12-404
BV-D12-407
25-DC-63CS00-EH-D12408
GV-D12-504
BV-D12-507
25-DC-63CS00-EH-D12508
FQIR D12-101
FI D12-101
PT
PDIT D12-101
TT D12-101A
TT D12-101B
BV-D12-110as
BV-D12-110bs
GV-D12-106as
GV-D12-106bs
FE D12-101
FQIR D12-201
FI D12-201
PDIT D12-201
TT D12-201A
TT D12-201B
BV-D12-210as
BV-D12-210bs
GV-D12-206as
GV-D12-206bs
FE D12-201
FQIR D12-301
FI D12-301
PDIT D12-301
TT D12-301A
TT D12-301B
BV-D12-310as
BV-D12-310bs
GV-D12-306as
GV-D12-306bs
FE D12-301
FQIR D12-401
FI D12-401
PDIT D12-401
TT D12-401A
TT D12-401B
BV-D12-410as
BV-D12-410bs
GV-D12-406as
GV-D12-406bs
FE D12-401
FQIR D12-501
FI D12-501
PDIT D12-501
TT D12-501A
TT D12-501B
BV-D12-510as
BV-D12-510bs
GV-D12-506as
GV-D12-506bs
FE D12-501
Прим. 4,5,6,7
50-DC-63CS00-HH-D12024
57х4 St.20
GV-D12-105
BV-D12-108
25-DC-63CS00-EH-D12109
GV-D12-205
BV-D12-208
25-DC-63CS00-EH-D12209
GV-D12-305
BV-D12-308
25-DC-63CS00-EH-D12309
GV-D12-405
BV-D12-408
25-DC-63CS00-EH-D12409
GV-D12-505
BV-D12-508
25-DC-63CS00-EH-D12509
AW D12-101
AW D12-201
AW D12-301
AW D12-401
AW D12-501
Прим. 14
PG D12-101
TG D12-101
Ду 15
BV-D12-109
PG D12-201
TG D12-201
BV-D12-209
PG D12-301
TG D12-301
BV-D12-309
PG D12-401
TG D12-401
BV-D12-409
PG D12-501
TG D12-501
BV-D12-509
BV-D12-102
GV-D12-102
XV-D12-102
XV-D12-104
IJ-D12-102
50-GT-63CS00-N-D12103
BV-D12-202
GV-D12-202
XV-D12-202
XV-D12-204
IJ-D12-202
50-GT-63CS00-N-D12203
BV-D12-302
GV-D12-302
XV-D12-302
XV-D12-304
IJ-D12-302
50-GT-63CS00-N-D12303
BV-D12-402
GV-D12-402
XV-D12-402
XV-D12-404
IJ-D12-402
50-GT-63CS00-N-D12403
BV-D12-502
GV-D12-502
XV-D12-502
XV-D12-504
IJ-D12-502
50-GT-63CS00-N-D12503
Технологический газ
Лист 1
на узел подключения ГИС
1200-GT-63CS00-HH-D12004
1220х16 К60
FA-D12-002
100-VA-16CS00-N-D12027
114х4 09Г2С
BV-D12-023
GV-D12-002
BV-D12-024
80-DC-63CS00-EH-D12028
89х4 St.20
100-DC-63CS00-HH-D12029
114х4 09Г2С
Блок аналитического оборудования
AT D12-005
CH
AT D12-004
H2O
AT D12-003
O2
AT D12-002
RHS
AT D12-001
GC
AX D12-001
HW D12-001
Прим. 13
Тр.½" х 0.065"
сталь 316
HOLD
A1

| | | | | |
|---|---|---|---|---|
| A1 | 31.07.2026 | Утверждено для строительства | | |
| R2 | 16.07.2026 | Выпущено для рассмотрения | | |
| R1 | 26.06.2026 | Выпущено для рассмотрения | | |
| Рев. | Дата | Назначение ревизии | Проверил | Утвердил |

ЗАКАЗЧИК: UTG UZTRANSGAZ
ГЕНЕРАЛЬНЫЙ ПОДРЯДЧИК: UET UZBEKENERGOTAMIR
ПОДРЯДЧИК: PBG Pro Build Generation
ГЕНЕРАЛЬНЫЙ ПРОЕКТИРОВЩИК: EAST WEST ENGINEERING

## EWE0426-MGL1-PRE-054-SCM-610120-A1

«СТРОИТЕЛЬСТВО НОВЫХ НИТОК (УЧАСТКОВ) ГАЗОПРОВОДОВ «ГАЗЛИ – САРИМОЙ» И «АКЧАЛОК – ГАЗЛИ – НУКУС» ОБЩЕЙ ПРОТЯЖЕННОСТЬЮ НЕ МЕНЕЕ 275 КМ».

| Изм. | Кол.уч. | Лист | №док. | Подпись | Дата |
|---|---|---|---|---|---|
| ГИП | | Схабицкий А. | | | 07.2026 |
| Нач.отд. | | Рябинин А. | | | 07.2026 |
| Исполн. | | Юлдашев И. | | | 07.2026 |
| | | | | | |
| | | | | | |
| Н.контр | | Схабицкий А. | | | 07.2026 |

ГАЗОПРОВОД «ГАЗЛИ-САРИМОЙ» (54 КМ)

| Стадия | Лист | Листов |
|---|---|---|
| РД | 2 | 3 |

Узел замера расхода газа УЗРГ-D12-001.
Схема трубной обвязки и КИПиА. P&ID

ООО "EAST-WEST Engineering"
г. Ташкент 2026г.

Взам. инв. №
Подпись и дата
Инв.№ подл.

Формат / Format A2

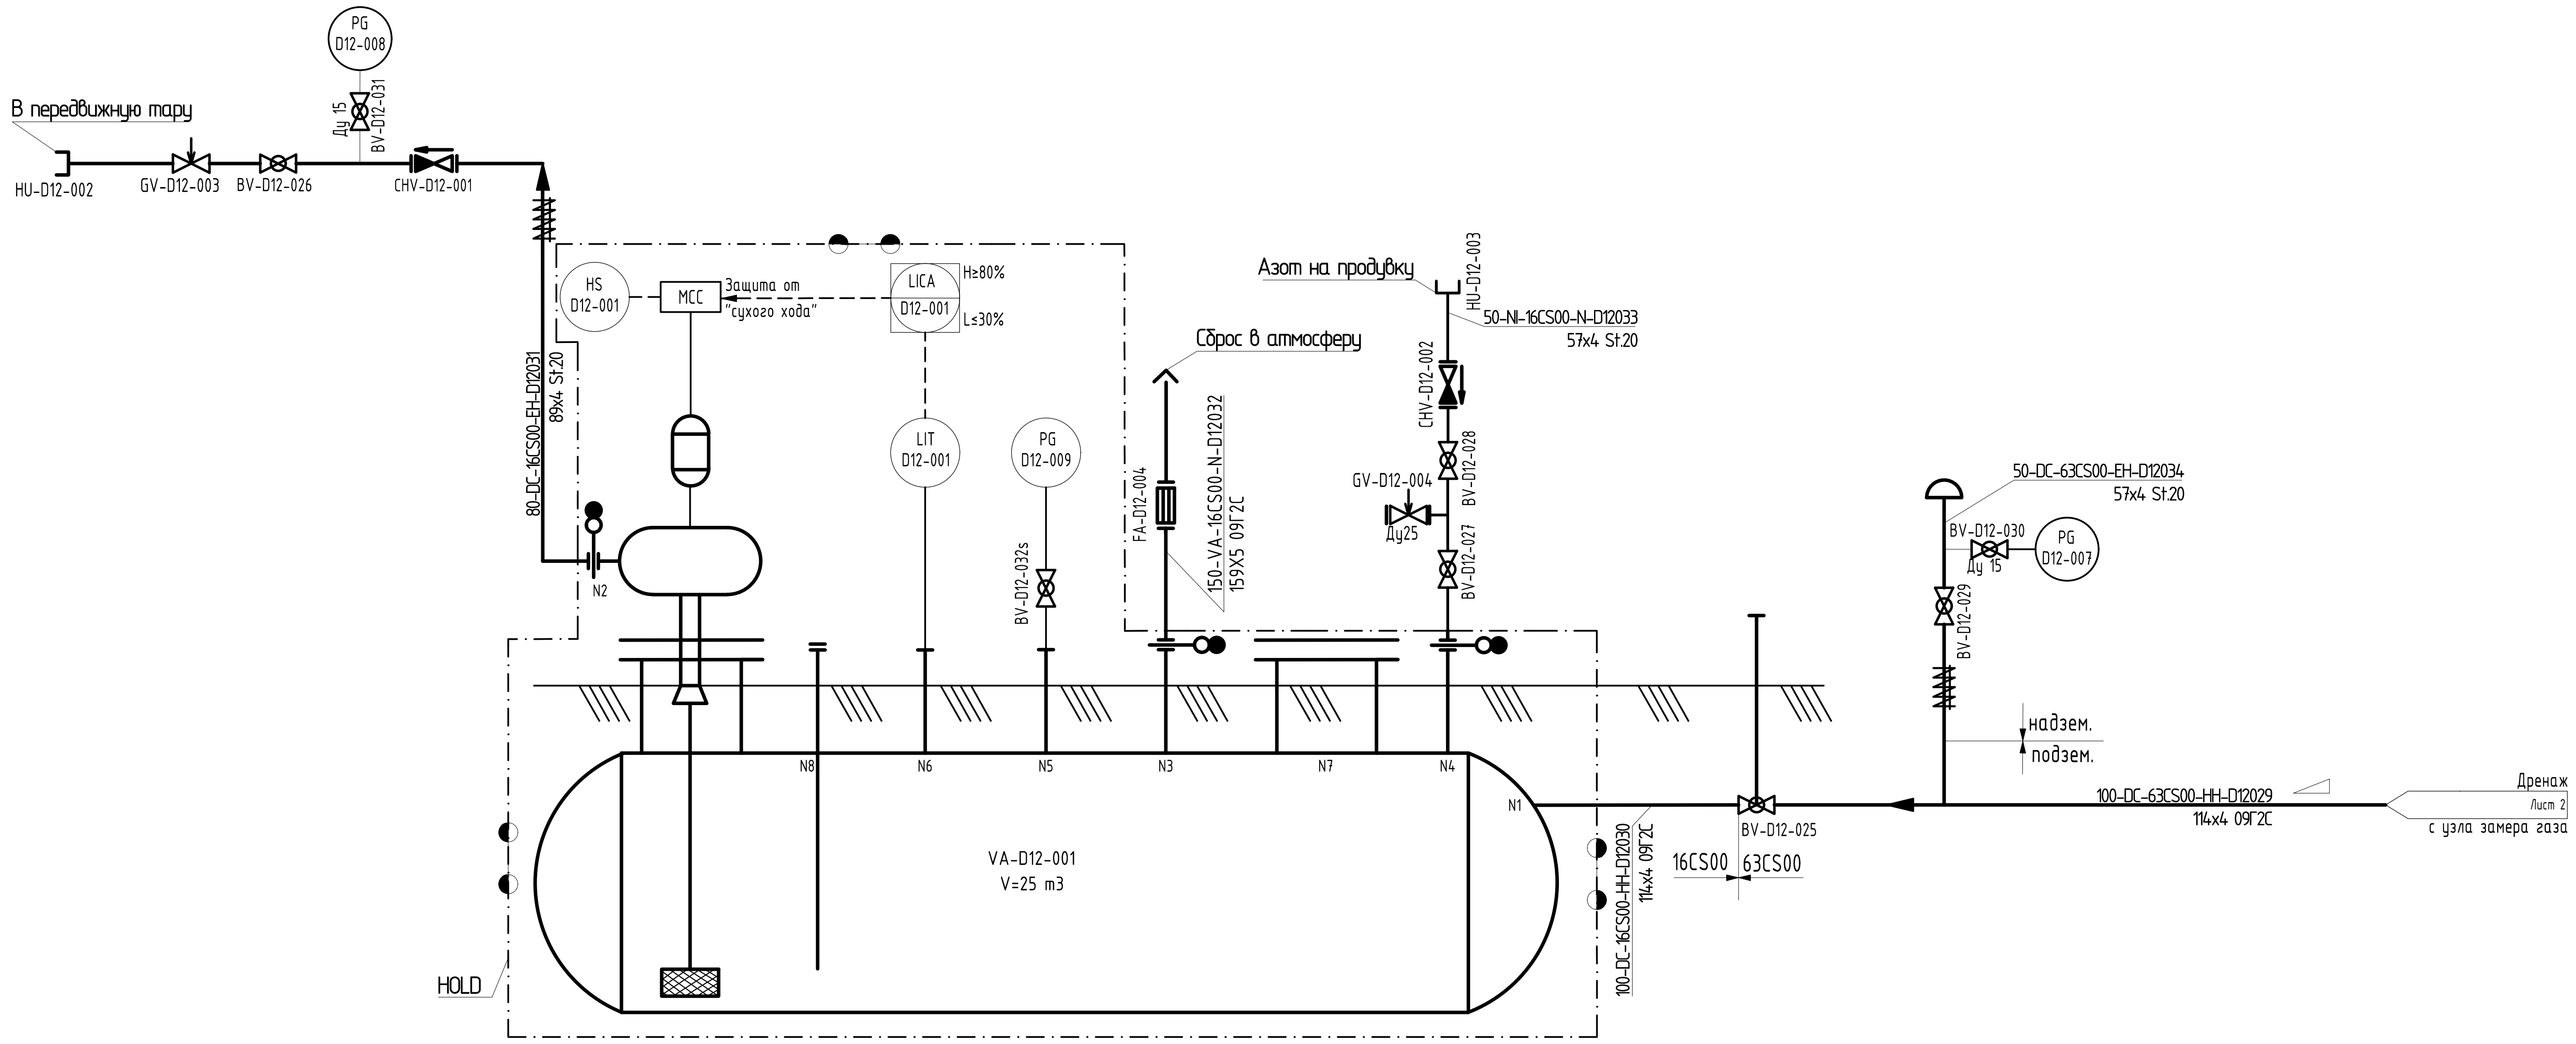
PG
D12-008
Ду 15
BV-D12-031
В передвижную тару
HU-D12-002
GV-D12-003
BV-D12-026
CHV-D12-001
80-DC-16CS00-EH-D12031
89x4 St.20
HS
D12-001
MCC
Защита от
"сухого хода"
LICA
D12-001
H≥80%
L≤30%
LIT
D12-001
PG
D12-009
BV-D12-032s
N2
N8
N6
N5
N3
N7
N4
N1
VA-D12-001
V=25 m3
HOLD
FA-D12-004
Сброс в атмосферу
150-VA-16CS00-N-D12032
159X5 09Г2С
Азот на продувку
HU-D12-003
50-NI-16CS00-N-D12033
57x4 St.20
CHV-D12-002
GV-D12-004
Ду25
BV-D12-028
BV-D12-027
100-DC-16CS00-HH-D12030
114x4 09Г2С
16CS00
63CS00
BV-D12-025
50-DC-63CS00-EH-D12034
57x4 St.20
BV-D12-030
Ду 15
PG
D12-007
BV-D12-029
надзем.
подзем.
100-DC-63CS00-HH-D12029
114x4 09Г2С
Дренаж
Лист 2
с узла замера газа

| | | | | |
|---|---|---|---|---|
| | | | | |
| | | | | |
| | | | | |
| A1 | 31.07.2026 | Утверждено для строительства | | |
| R2 | 16.07.2026 | Выпущено для рассмотрения | | |
| R1 | 26.06.2026 | Выпущено для рассмотрения | | |
| Рев. | Дата | Назначение ревизии | Проверил | Утвердил |

ЗАКАЗЧИК: UTG UZTRANSGAZ

ГЕНЕРАЛЬНЫЙ ПОДРЯДЧИК: UET UZBEKENERGOTAMIR

ПОДРЯДЧИК: PBG Pro Build Generation

ГЕНЕРАЛЬНЫЙ ПРОЕКТИРОВЩИК: EAST WEST ENGINEERING

EWE0426-MGL1-PRE-054-SCM-610120-A1

«СТРОИТЕЛЬСТВО НОВЫХ НИТОК (УЧАСТКОВ) ГАЗОПРОВОДОВ «ГАЗЛИ - САРИМОЙ» И «АКЧАЛОК - ГАЗЛИ - НУКУС» ОБЩЕЙ ПРОТЯЖЕННОСТЬЮ НЕ МЕНЕЕ 275 КМ».

| Изм. | Кол.уч. | Лист | №док. | Подпись | Дата |
|---|---|---|---|---|---|
| ГИП | | Схабицкий А. | | | 07.2026 |
| Нач.отд. | | Рябинин А. | | | 07.2026 |
| Исполн. | | Юлдашев И. | | | 07.2026 |
| | | | | | |
| | | | | | |
| Н.контр | | Схабицкий А. | | | 07.2026 |

ГАЗОПРОВОД «ГАЗЛИ-САРИМОЙ» (54 КМ)

| Стадия | Лист | Листов |
|---|---|---|
| РД | 3 | 3 |

Узел замера расхода газа УЗРГ-D12-001.
Схема трубной обвязки и КИПиА. P&ID

EAST WEST ENGINEERING

ООО "EAST-WEST Engineering"
г. Ташкент 2026г.

Формат / Format A2

Взам. инв. №

Подпись и дата

Инв.№ подл.