

План (1:500)

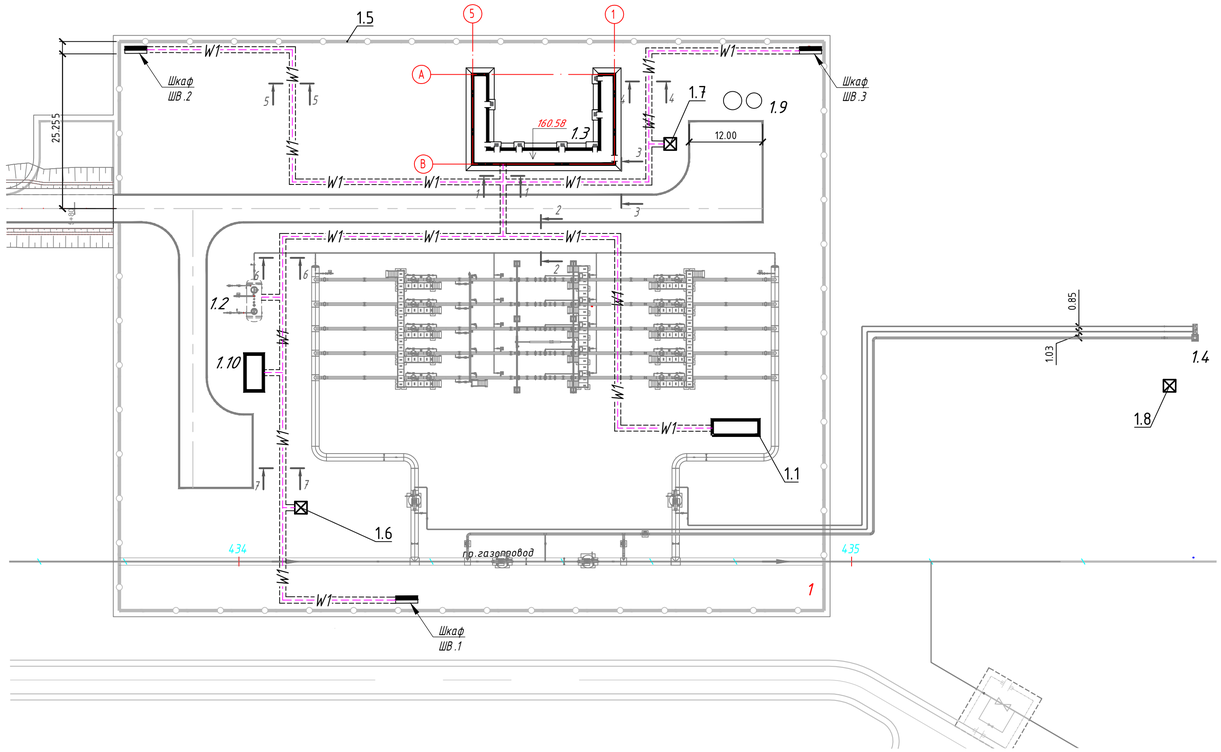


Экспликация зданий и сооружений

Номер на плане	Наименование	Примечание
	Площадка УЗРГ	
1.1	Блок качества газа	
1.2	Площадка дренажной емкости V=25м3	
1.3	Операторная	
1.4	Продувочные свечи	
1.5	Сетчатое ограждение с воротами шир.4.5 м	
1.6	Прожекторная мачта ПМЖ-22.8	
1.7	Прожекторная мачта ПМЖ-22.8	
1.8	Молниеотвод МЖ-24.3	
1.9	Выгреб	
1.10	ГПЭС	


1-1(1:20)

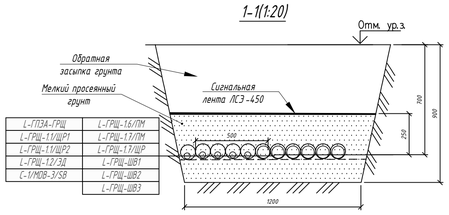


2-2(1:20)

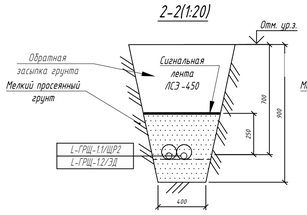


3-3(1:20)

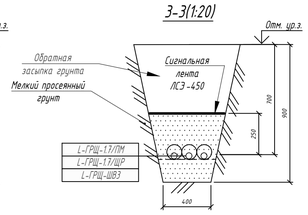


4-4(1:20)

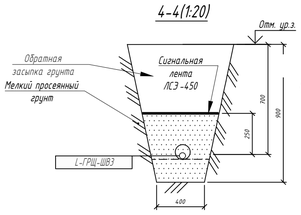


5-5(1:20)

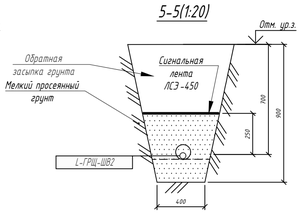

6-6(1:20)

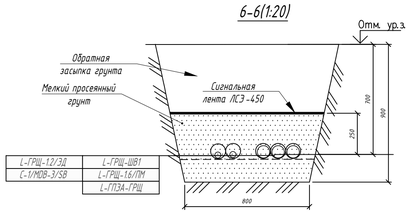

7-7(1:20)

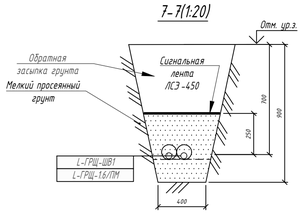

Условные обозначения

- кабель до 1 кВ, проложенный в ПНД трубе в траншее

1-1 - разрез

Процедура нумерации кабелей							
Пример нумерации кабеля: L-10/РЗНН.1-3.6.1/НКУ.1-(A,B)							
L	-	10/РЗНН.1	-	3.6.1/НКУ	-	1	(A,B)
ТИП КАБЕЛЯ: Н - выше 1 кВ; L - ниже 1 кВ; С - контрольный; DC - кабель постоянного тока		ТАГОВЫЙ НОМЕР НАЧАЛА КАБЕЛЯ (ИСТОЧНИК): здание 10 по экспликации/ ЩИТ РЗНН секция 1		ТАГОВЫЙ НОМЕР КОНЦА КАБЕЛЯ (ПОТРЕБИТЕЛЬ): с сооружение 3.6.1 по экспликации/ Потребитель ГПА. Щит НКУ		ПОРЯДКОВЫЙ НОМЕР ВВОДА (или питающей секции)	КОЛИЧЕСТВО ПАРАЛЕЛЬНЫХ КАБЕЛЕЙ (если больше 1го кабеля): A,B - 2 параллельных кабеля

Примечания:

1. При прокладке кабельных линий в земле, расстояние от кабеля до трубопровода должно быть не менее:
   - 1 м - при параллельной прокладке;
   - от 0,250 м - при пересечениях в стесненных условиях.
2. В месте пересечения кабельной траншеи с водоотводным лотком, кабель в трубе проложить на отметке 0,5 м ниже конструкции лотка.
3. В местах пересечения кабельных траншей с автомобильными дорогами, кабель проложить в трубе на глубине не менее 1 м. Протяженность прокладки в трубах принять равной ширине пересекаемого участка дороги плюс по 2 м с каждой стороны.
4. Прокладку труб с каблем в земле выполнить на глубине не менее 700 мм. На расстоянии 250 мм над трубами с каблем проложить сигнальную ленту "Осторожно кабель". Сигнальная лента должна выступать за крайние кабели не менее, чем на 50 мм.
5. Подготовку траншей выполнить согласно КМК 3.05.06-97.

Рев.	Дата	Назначение ревизии	Проверил	Утвердил
R1	12.08.2026	Выпущено для рассмотрения		

ЗАКАЗЧИК: UTG METHANOL | ГЕНЕРАЛЬНЫЙ ПОДРЯДЧИК: UET | ПОДРЯДЧИК: PBG | ГЕНЕРАЛЬНЫЙ ПРОЕКТИРОВЩИК: EAST WEST ENGINEERING

EWE0426-MGL1-ELE-054-DRW-801503-R1

«СТРОИТЕЛЬСТВО НОВЫХ НИТОК (УЧАСТКОВ) ГАЗОПРОВОДОВ «ГАЗЛИ – САРИМОЙ» И «АКЧАЛОК – ГАЗЛИ – НУКУС» ОБЩЕЙ ПРОТЯЖЕННОСТЬЮ НЕ МЕНЕЕ 275 КМ».

Изм.	Кол. уч.	Лист.	№док.	Подп.	Дата
ГИП		Скабицкий А.			08.2026
Нач.отд.		Гимранов Т.			08.2026
Исполн.		Пац В.			08.2026
Н. контр.		Скабицкий А.			08.2026

ГАЗОПРОВОД «ГАЗЛИ-САРИМОЙ» (54 КМ)
Площадка УЗРГ.
Внутриплощадочные коммуникации

Наружные электрические сети. План. Разрезы

Стадия	Лист	Листов
РП	1	1

ООО "EAST-WEST Engineering"
г. Ташкент 2026г.

Формат А1

Взам. инв. №

Подп. и дата

Инв. № подл.