
План (1:500)

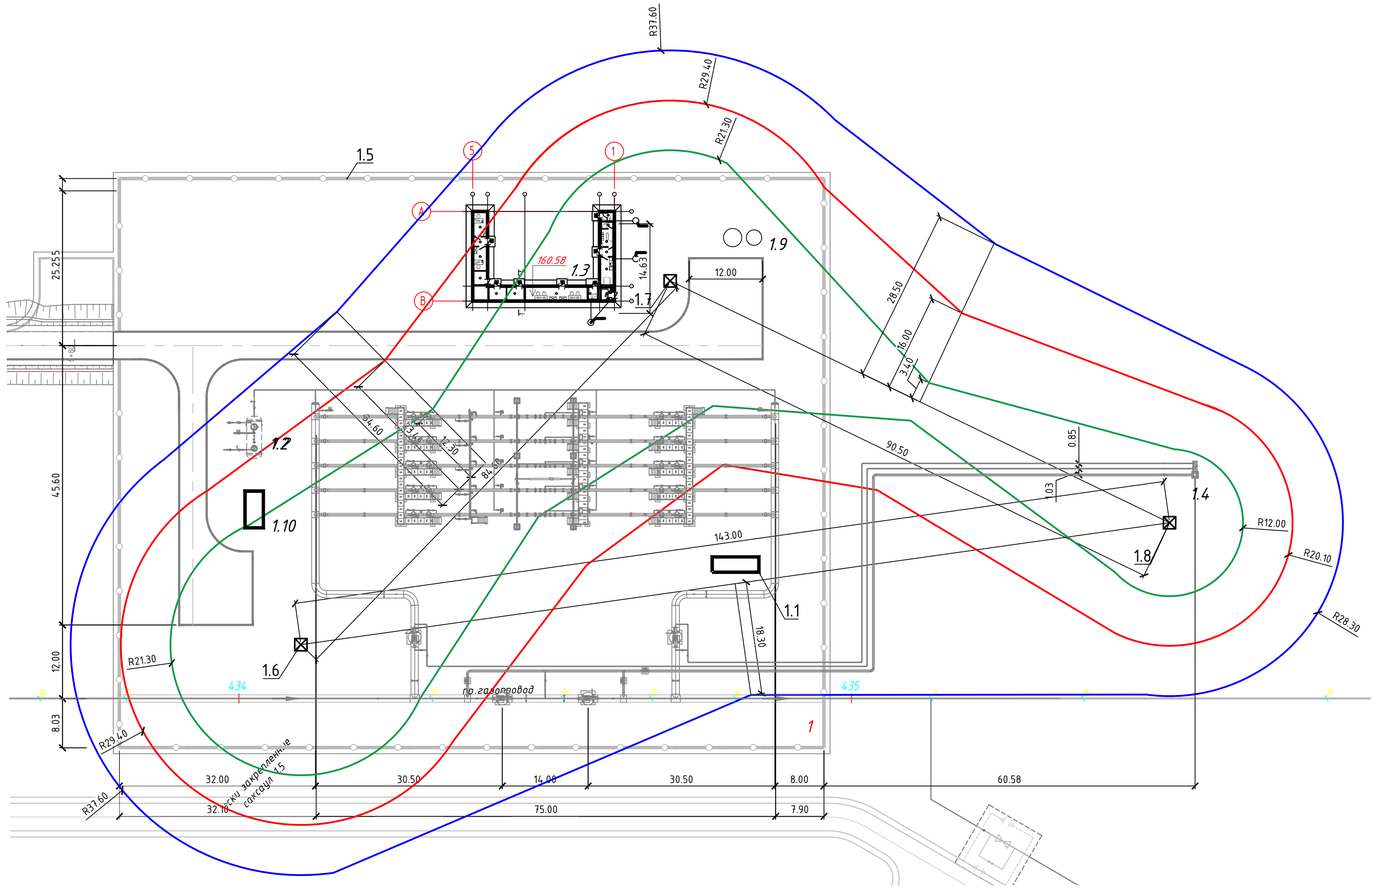


Экспликация зданий и сооружений

Номер на плане	Наименование	Примечание
	Площадка УЗРГ	
1.1	Блок качества газа	
1.2	Площадка дренажной емкости V=25м3	
1.3	Операторная	
1.4	Продувочные свечи	
1.5	Сетчатое ограждение с воротами шир.4.5 м	
1.6	Прожекторная мачта ПМЖ-22.8	
1.7	Прожекторная мачта ПМЖ-22.8	
1.8	Молниеотвод МЖ-24.3	
1.9	Выгреб	
1.10	ГПЭС	

1-й молниеотвод		2-й молниеотвод	L	h1	h2	hx	Rx1	Rx2	Rcx
Для высоты защищаемых объектов не более 10 м.									
ПМ 1.6	-	ПМ 1.7	84,6	30,5	30,5	5,0	37,6	37,6	34,6
ПМ 1.6	-	ПМ 1.7	84,6	30,5	30,5	10,0	29,4	29,4	23,4
ПМ 1.6	-	ПМ 1.7	84,6	30,5	30,5	15,0	21,3	21,3	12,3
ПМ 1.7	-	ПМ 1.8	90,5	30,5	24,3	5,0	37,6	28,3	28,5
ПМ 1.7	-	ПМ 1.8	90,5	30,5	24,3	10,0	29,4	20,1	16,0
ПМ 1.7	-	ПМ 1.8	90,5	30,5	24,3	15,0	21,3	12,0	3,4
ПМ 1.6	-	ПМ 1.8	14,3	30,5	24,3	5,0	37,6	28,3	18,3

Зона защиты двойного стержневого молниеотвода

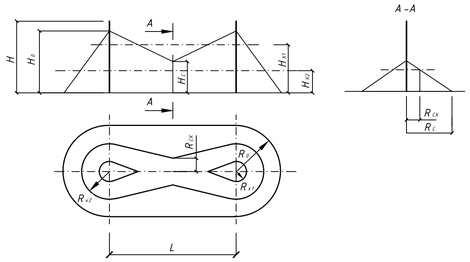

Условные обозначения

- зона молниезащиты на высоте 5 м
- зона молниезащиты на высоте 10 м
- зона молниезащиты на высоте 15 м

Примечания

1. Размеры зон молниезащиты построены в соответствии с РД 34.21.122-87 для зоны Б и II категории молниезащиты.
2. Высота проектируемого прожекторной мачты ПМ 1.6, ПМ 1.7 (типа ПМЖ-22,8) составляет 30,5 м, высота молниеприемника ПМ 1.8 составляет 24,3 м.
3. Материалы заземлителей молниеотводов учтены на чертеже заземления.
4. Класс взрывоопасной зоны согласно ПУЭ - В-Iг.
5. Координаты прожекторных мачт с молниеотводами - согласно разбивочного плана.

R1	03.08.2026	Выпущено для рассмотрения		
Рев.	Дата	Назначение ревизии	Проверил	Утвердил

ЗАКАЗЧИК: | ГЕНЕРАЛЬНЫЙ ПОДРЯДЧИК: | ПОДРЯДЧИК: | ГЕНЕРАЛЬНЫЙ ПРОЕКТИРОВЩИК: EAST WEST ENGINEERING

EWE0426-MGL1-ELE-054-DRW-801504-R1

«СТРОИТЕЛЬСТВО НОВЫХ НИТОК (УЧАСТКОВ) ГАЗОПРОВОДОВ «ГАЗЛИ – САРИМОЙ» И «АКЧАЛОК – ГАЗЛИ – НУКУС» ОБЩЕЙ ПРОТЯЖЕННОСТЬЮ НЕ МЕНЕЕ 275 КМ».

Изм.	Кол. уч.	Лист.	№док.	Подп.	Дата
ГИП		Скабицкий А.			08.2026
Нач.отд.		Гимранов Т.			08.2026
Исполн.		Пац В.			08.2026
Н. контр.		Скабицкий А.			08.2026

ГАЗОПРОВОД «ГАЗЛИ-САРИМОЙ» (54 КМ)
Площадка УЗРГ.
Внутриплощадочные коммуникации

Стадия	Лист	Листов
РП	1	1

Молниезащита. План.

ООО "EAST-WEST Engineering"
г. Ташкент 2026г.

Формат А1

Взам. инв. №
Подп. и дата
Инв. № подл.