
План (1:500)

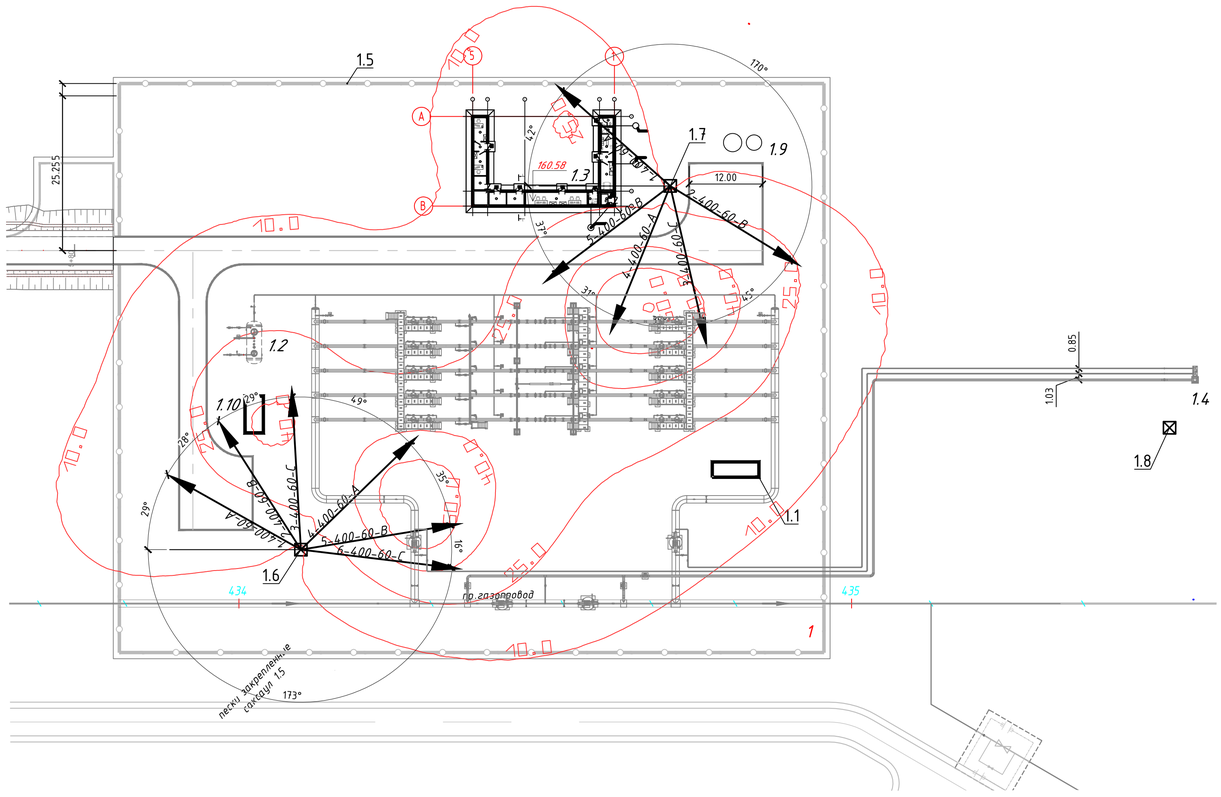


Экспликация зданий и сооружений

Номер на плане	Наименование	Примечание
	Площадка УЗРГ	
1.1	Блок качества газа	
1.2	Площадка дренажной емкости V=25м3	
1.3	Операторная	
1.4	Продувочные свечи	
1.5	Сетчатое ограждение с воротами шир.4.5 м	
1.6	Прожекторная мачта ПМЖ-22.8	
1.7	Прожекторная мачта ПМЖ-22.8	
1.8	Молниеотвод МЖ-24.3	
1.9	Выгреб	
1.10	ГПЭС	


СПЕЦИФИКАЦИЯ МАТЕРИАЛОВ ОСВЕЩЕНИЯ

Поз	Наименование	Тип, размер	Параметры, ГОСТ, ТУ	К-во 1 мачту		Количество, всего	Масса ед., кг	Единица измерения
				ПМ1.6	ПМ1.7			
1	Светильник общепромышленный модульный, со светодиодным источником света 230 В, 50 Гц, 400 Вт, IP66, крепление на скобе, с фотометрической кривой 60°, со световым потоком 40000 Лм	-	ТУ 3461-015-00213569-2010	6	5	11	10,0	компл.
2	Кабельный ввод	ВК-Н-ВЭЛ 3-М 20	ПИНЮ.687153.002 ТУ IP66	3	3	6	0,15	шт.
3	Кабель силовой бронированный 3х4	ВБбШВнг(А)-LS	ТУ 16.К01-37-2003	95	95	190	0,534	м
4	Кабель 3х2,5-660	ВВГнг	ТУ 16.К01-37-2003	10	10	20	0,144	м
5	Металлорукав негерметичный	РЗ-Ц-Х-20	ТУ 4833-019-29124208-00	10	10	20	0,3	м
6	Скоба	К 14.2 У 1		10	10	20	0,035	шт.
7	Коробка соединительная общепромышленная на 3 ввода	КС12-32-УХЛ1	ТУ 3434-001-00213569-2005	3	3	6	1,5	шт.
8	Короб кабельный	СП (50х25) УТ 1.5 L=2 м		21	21	42	3,5	шт.
9	Ящик силовой с выключателем врубным и предохранителями	ЯРВ-20-31 УХЛ1	100 А, 380 В, IP54, Iн п.в.=31,5 А	1	1	2	9,2	компл.
10	Полоса для крепления щита	4х40, L=0,5 м		2	2	4	0,63	шт.
11	Труба	32х3,2	ГОСТ 3262-75	2	2	4	3,09	м


Схема сети освещения

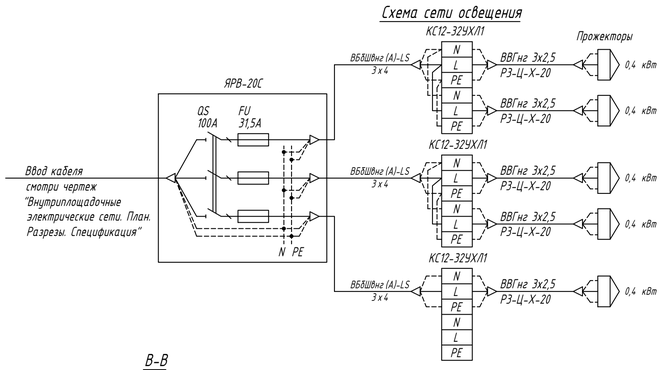

Б

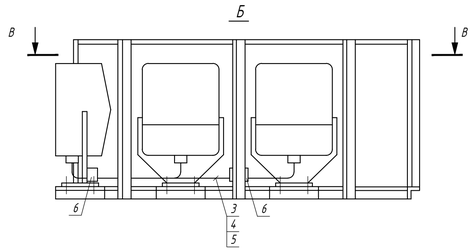

В-В

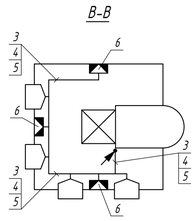


Условные обозначения

- Прожекторная мачта №16 с 4-ю прожекторами установленными на отм. +23,400.


1-400-30-А - Номер прожектора-мощность прожектора-угол наклона относительно горизонта-фаза сети к которой подключается прожектор

+10.0 - Изолинии освещенности, люкс.

А

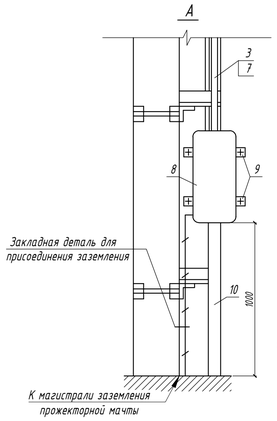

ПМЖ-22,8 (ПМ 1.6, ПМ 1.7)

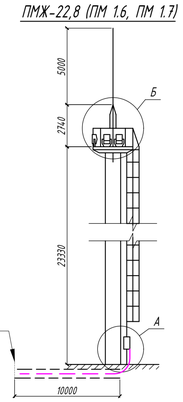

Примечания:

1. Условные обозначения по ГОСТ 21.607-2014.
2. Нормируемая освещенность для площадочных проездов и проходов принята 4 Лк согласно СНК 2.01.05-98.
3. Наружное освещение площадки узла замера газа выполнено прожекторами со светодиодными источниками света мощностью 400 Вт, расположенными на 2- х прожекторных мачтах типа ПМЖ (серия 3.407.9-172). Координаты прожекторных мачт согласно разбивочного плана.
4. Питающие кабели прожекторов предусмотерны на чертеже "Наружные электрические сети. План. Спецификация".
5. Заземление прожекторных мачт и материалы предусмотрены на чертеже "Заземление. План. Спецификация".
6. Кабель питания прожекторных мачт проложить на протяжении 10 метров около молниеотвода, в трубе по траншее согласно ПУЕ п.4.2.132.
7. Прожекторы подключить так, что бы распределить нагрузку равномерно по фазам. Кабель между щитком и клеммной коробкой на вертикальном участке (по всей высоте) защитить коробом СП (50х25) от наведения потенциала при прохождении тока молнии, а также для механической защиты.
8. Прожекторы и клеммные коробки на отм. +23,500 заземляятся при помощи PE жилы питающего кабеля.
9. Расчет освещенности выполнен в программном комплексе Dialux с применением технических данных от завода-изготовителя

Изм.	Дата		
R1	03.08.2026	Выпущено для рассмотрения	
Рев.	Дата	Назначение ревизии	Проверил / Утвердил

ЗАКАЗЧИК: ГЕНЕРАЛЬНЫЙ ПОДРЯДЧИК: ПОДРЯДЧИК: ГЕНЕРАЛЬНЫЙ ПРОЕКТИРОВЩИК:

EWE0426-MGL1-ELE-054-DRW-801505-R1

«СТРОИТЕЛЬСТВО НОВЫХ НИТОК (УЧАСТКОВ) ГАЗОПРОВОДОВ «ГАЗЛИ - САРИМОЙ» И «АКЧАЛОК - ГАЗЛИ - НУКУС» ОБЩЕЙ ПРОТЯЖЕННОСТЬЮ НЕ МЕНЕЕ 275 КМ».

Изм.	Кол. уч.	Лист.	№док.	Подп.	Дата
ГИП		Скабицкий А.			08.2026
Нач.отд.		Гимранов Т.			08.2026
Исполн.		Пац В.			08.2026
Н. контр.		Скабицкий А.			08.2026

ГАЗОПРОВОД «ГАЗЛИ-САРИМОЙ» (54 КМ)
Площадка УЗРГ.
Внутриплощадочные коммуникации

Стадия	Лист	Листов
РП	1	1

Наружное освещение. План. Спецификация

ООО "EAST-WEST Engineering"
г. Ташкент 2026г.

Взам. инв. №

Подп. и дата

Инв. № подл.

Формат А1