
План (1:500)

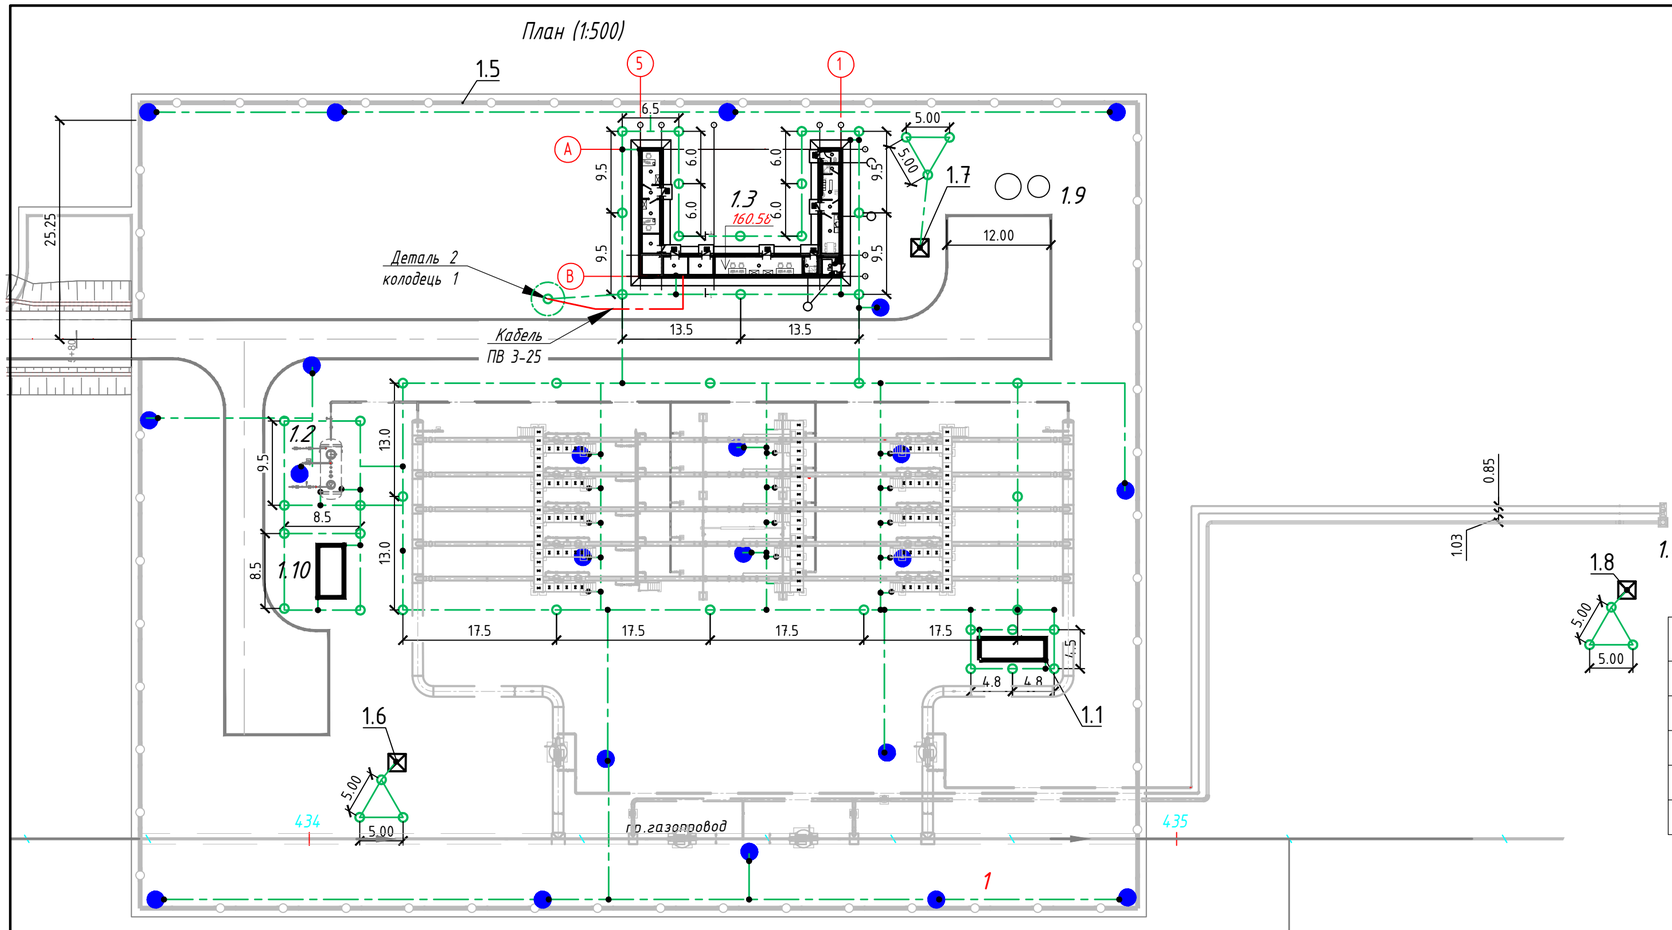

Экспликация зданий и сооружений

Номер на плане	Наименование	Примечание
	Площадка УЗРГ	
1.1	Блок качества газа	
1.2	Площадка дренажной емкости V=25м3	
1.3	Операторная	
1.4	Продувочные свечи	
1.5	Сетчатое ограждение с воротами шир.4.5 м	
1.6	Прожекторная мачта ПМЖ-22.8	
1.7	Прожекторная мачта ПМЖ-22.8	
1.8	Молниеотвод МЖ-24.3	
1.9	Выгреб	
1.10	ГПЭС	


СПЕЦИФИКАЦИЯ ОБОРУДОВАНИЯ И МАТЕРИАЛОВ

Поз.	Обозначение (код)	Наименование	Кол.	Масса ед., кг	Примечание
1	ГОСТ 103-2006/3 СП ГОСТ 535-2005	Полоса стальная 4 х 40	1050	1,26	м
2	ГОСТ 2590-88/09 Г 2 Д ГОСТ 535-2005	Круг стальной Ф16, L=3 м	49	1,60	м
3	ГОСТ 6323-79*	ПВ 3 х 6 - Провод сечением 6 мм² желто-зеленого цвета	10	0,07	м
4	ГОСТ 15836-79	Мастика изоляционная битумно-резиновая, марки МБР-90	1		кг
5	ТУ 102-340-83	Грунтовка ГТ-760 ИН	1		кг


Примечания

1. Вертикальные заземлители выполнить из круглой стали d=16 мм, L=3 м и заглубить до отм. -0,4 м (верх электрода).
2. Горизонтальные заземлители из полосовой стали проложить в траншее на отм. -0,7 м, при пересечении трассы заземления с фундаментами трубопроводов или технологического оборудования так же силовыми кабелями обойти фундамент на расстоянии 0,9 м.
3. Сопротивление контура заземления СТП должно быть не более 4 Ом. При невозможности достичь нормируемого сопротивления контура количеством вертикальных заземлителей указаных на чертеже, необходимо увеличить количество и длину вертикальных заземлителей.
4. Горизонтальную полосу заземления соединить сваркой с вертикальными заземлителями и покрыть в месте сварки слоем мастики изоляционной битумно-резиновой, марки МБР-90, ГОСТ 15836-79, по слою грунтовки ГТ-760 ИН.
5. Заземлить наземные фланцевые соединения трубопроводов см. узел 1.
6. Все приборы, коробки, шкафы КИПиА и металлические части оборудования, подлежащие защитному заземлению, присоединить к системе защитного заземления объекта в соответствии с требованиями ПУЭ, ТУ и действующих нормативных документов.
7. В соответствии с требованиями Технического задания для шкафа САУ, шкафа с вычислителями и блока аналитики предусмотрено отдельную шину функционального заземления (FE) для подключения экранов контрольных и информационных кабелей. Сопротивление шины функционального заземления должно быть не более 1 Ом.
8. Для стоек с оборудованием видеонаблюдения для защиты от поражения электрическим током при косвенном прикосновении предусмотрено автоматическое отключение питания. Уравнивание потенциалов выполнить путем присоединения к клемме PE в шкафу видеонаблюдения, проводником желто-зеленого цвета сечением не менее 6 мм2, пластины заземления на стойке. Также обеспечить надежную металлическую связь стойки с металлическим корпусом камеры.
9. Контур инструментального заземления соединить с контурами заземления. Подвод к шине функционального (инструментального) заземления линию от наружного заземляющего устройства функционального (инструментального) заземления, выполненного в соответствие требованиям ГОСТ Р 50571.5.54-2013, ПУЭ РУз. Сопротивление заземляющего устройства функционального (инструментального) заземления должно быть не более 1 Ом.

Узел 1
Установка перемычки заземления

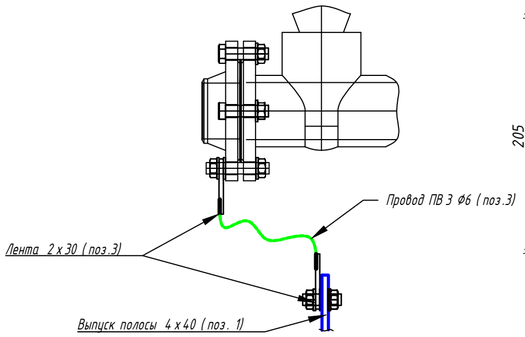

Деталь 2
Подключение кабелей инструментального заземления к наружному контуру заземления

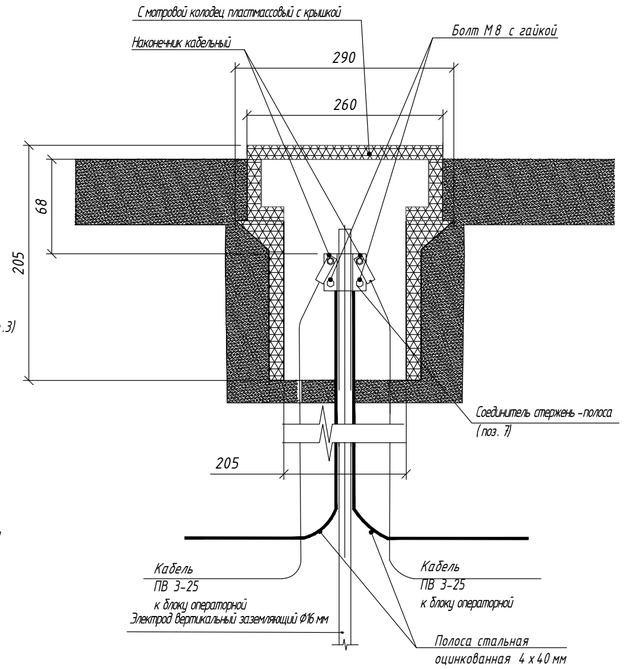

Условные обозначения

- Горизонтальный заземлитель - полоса 4 х 40 прокладываемая горизонтально на глубине 0,5 м
- Вертикальный заземлитель - круг 16 длиной 3 м
- Места присоединения полосы заземления при помощи сварки
- Стойка с оборудованием СПГО

Согласовано

Взам. инв. №

Подп. и дата

Инв. № подл.

Рев.	Дата	Назначение ревизии	Проверил	Утвердил
R1	12.08.2026	Выпущено для рассмотрения		

ЗАКАЗЧИК: UTG ГЕНЕРАЛЬНЫЙ ПОДРЯДЧИК: UET ПОДРЯДЧИК: PBG ГЕНЕРАЛЬНЫЙ ПРОЕКТИРОВЩИК: EAST WEST ENGINEERING

EWE0426-MGL1-ELE-054-DRW-801506-R1

«СТРОИТЕЛЬСТВО НОВЫХ НИТОК (УЧАСТКОВ) ГАЗОПРОВОДОВ «ГАЗЛИ - САРИМОЙ» И «АКЧАЛОК - ГАЗЛИ - НУКУС» ОБЩЕЙ ПРОТЯЖЕННОСТЬЮ НЕ МЕНЕЕ 275 КМ».

Изм.	Кол. уч.	Лист.	№док.	Подп.	Дата
ГИП		Схабицкий А.			08.26
Нач.отд.		Гимранов Т.			08.26
Исполн.		Пац В.			08.26
Н. контр.		Схабицкий А.			08.26

ГАЗОПРОВОД «ГАЗЛИ-САРИМОЙ» (54 КМ) Площадка УЗРГ. Внутриплощадочные коммуникации

Стадия	Лист	Листов
РП	1	1

Заземление. План. Спецификация

ООО "EAST-WEST Engineering" г. Ташкент 2026г.

Формат А2