ЗАКАЗЧИК: UTG UZTRANSGAZ «TRANSGAZINJINIRING» ГЕНЕРАЛЬНЫЙ ПОДРЯДЧИК UET UZBEKENERGOTAMIR ПОДРЯДЧИК PBG Pro Build Generation ГЕНЕРАЛЬНЫЙ ПРОЕКТИРОВЩИК EAST WEST ENGINEERING

ОБЪЕКТ: «СТРОИТЕЛЬСТВО НОВЫХ НИТОК (УЧАСТКОВ) ГАЗОПРОВОДОВ «ГАЗЛИ - САРИМОЙ» И «АКЧАЛОК - ГАЗЛИ - НУКУС» ОБЩЕЙ ПРОТЯЖЕННОСТЬЮ НЕ МЕНЕЕ 275 КМ»
ГАЗОПРОВОД «ГАЗЛИ-САРИМОЙ» (54 КМ)

КОНТРАКТ №: EWEUZ-DW-26/04 от 16.04.2026г..

Ревизия документа: R1

Дата: 12.08.2026г.

ООО “EAST-WEST ENGINEERING”

ОПРОСНЫЙ ЛИСТ

Щит наружного освещения ЩНО. Опросный лист

EWE0426-MGL1-ELE-054-DSH-801511-R1

Согласовано

Взам. инв. №

Подпись и дата

Инв.№подл.

Изм.	Кол.уч	Лист	№док.	Подпись	Дата
ГИП		Схабицкий А.			08.2026
Нач. отд.		Гимранов Т.			08.2026
Исполн.		Пац В.			08.2026
Н. котр.		Схабицкий А.			08.2026

EWE0426-MGL1-ELE-054-DSH-801511-R1

ГАЗОПРОВОД «ГАЗЛИ-САРИМОЙ» (54 КМ)
Площадка УЗРГ.
Внутриплощадочные коммуникации
Щит наружного освещения ЩНО.
Опросный лист

Стадия	Лист	Листов
РП	1	6

EAST WEST ENGINEERING
ООО "EAST-WEST Engineering"
г. Ташкент 2026г

Лист регистрации изменений

Ревизия	Дата	Цель ревизии	Разработал	Проверил	Утвердил
R1	12.08.2026	Выпуск для проверки	Пац В.	Гимранов Т.	Схабицкий А.

Оглавление

1. **ССЫЛОЧНЫЕ ДОКУМЕНТЫ** **4**
2. **ОБЩИЕ ХАРАКТЕРИСТИКИ** **4**
3. **КОНСТРУКТОРСКАЯ ДОКУМЕНТАЦИЯКОНСТРКТОРСКАЯ ДОКУМЕНТАЦИЯ** **4**

1. ССЫЛОЧНЫЕ ДОКУМЕНТЫ

Документ	Название
КМК 2.01.01-94	Климатические и физико-геологические данные для проектирования
КМК 2.01.03-96	Строительство в сейсмических районах
ПУЭ РУз	Правила устройства электроустановок

2. ОБЩИЕ ХАРАКТЕРИСТИКИ


1.	Номинальное рабочее напряжение	400 В
2.	Номинальная частота	50 Гц
3.	Система заземления нейтрали	TN-S
4.	Номинальное напряжение цепей управления и сигнализации	~ 230 В
5.	Номинальное напряжение изоляции	660 В
6.	Конструктив	Навесной, металлический, двери непрозрачные с замком
7.	Степень защиты	IP 44
8.	Комплектующие	Schneider Electric, Siemens, ABB (или аналог)
9.	Ввод кабелей (питающие /отходящие линии)	Сверху/Снизу
10.	Состав шкафа	В соответствии с однолинейной схемой лист 5 и 6
11.	Обозначение шкафа (табличка на двери)	**ЩНО**

Выполнить таблички возле выключателей в соответствии с графой „Наименование механизма по плану” (чертёж, листы 5).

3. КОНСТРУКТОРСКАЯ ДОКУМЕНТАЦИЯ

Конструкторская документация, предоставляемая поставщиком, должна включать:

- Техническое описание системы
- Однолинейную электрическую схему
- Чертеж общего вида, габаритные, установочные и присоединительные размеры;
- Массу;
- Климатические условия применения;
- Сертификат соответствия сейсмическим условиям площадки;
- Критические требования поставщика;
- Значение максимальной рассеиваемой тепловой мощности;
- Схему подключения внешних цепей, с указанием наименований сигналов по каждой цепи;
- Вид системы заземления нейтрали

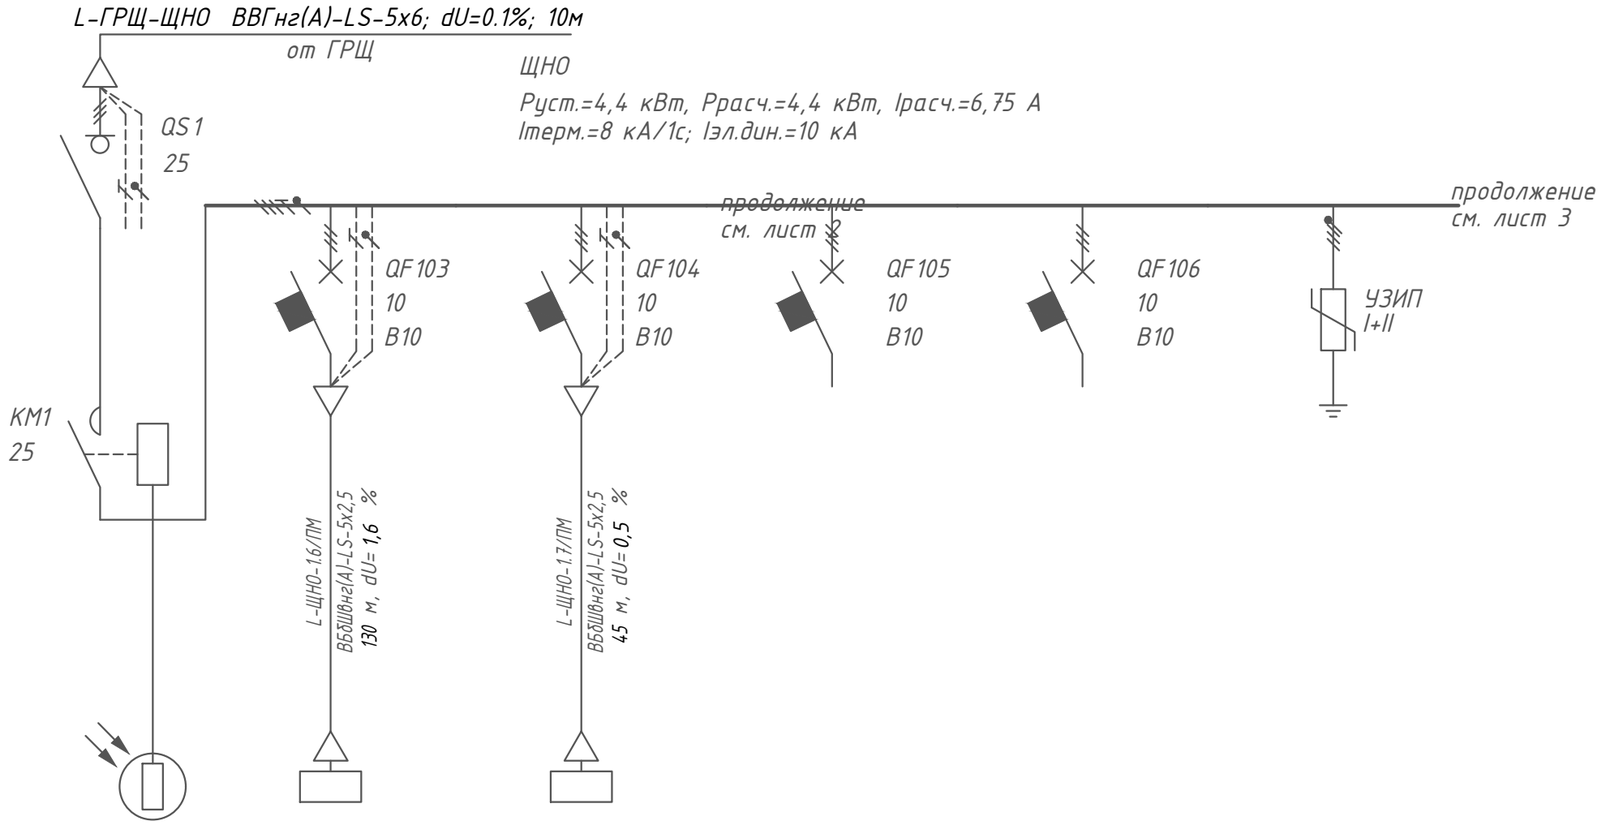

Данные питающей сети						
Шинопровод, распределительное устройство	Обозначение, тип, Iном,А расцепитель или плавкая вставка, А					
	Тип, напряжение, сечение (шинопровод), расчетный ток, А устан. мощность, кВт					
Аппарат отход. линии	Обозначение, тип, Iном., А расцепитель или плавкая вставка, А					
Пусковой аппарат	Тип, Iном., А, нагрев. элемент теплового реле уставка, А					
Кабельная линия						
Электроприемник	Условное обозначение по плану					
	Номер по плану		1.6/ПМ	1.7/ПМ		
	Тип		–	–		
	Руст, кВт		2,4	2,0		
	Ррасч, кВт		2,4	2,0		
	Iном, А		3,38	3,07		
	Iпуск, А		3,38	3,07		
	Наименование механизма по плану	Вводной выключатель / пускатель, управляемый от фотодатчика или вручную	Прожекторная мачта №1	Прожекторная мачта №2	Освещение навеса	Резерв	УЗИП
	Номер по технологическому плану		ПМ1.6	ПМ 1.7			

- номер коммутационного аппарата
- тип коммутационного аппарата и номинальный ток
- уставка расцепителя защиты от перегрузки
- время-токовая характеристика защитного аппарата
- уставка расцепителя защиты от токов утечки (если устанавливается)


Взам. инв. №

Подп. и дата

Инв. № подл.

Изм.	Кол. уч	Лист	№ док	Подп.	Дата	EWE0426-MGL1-ELE-054-DSH-801511-R1	Лист 5

Формат А3

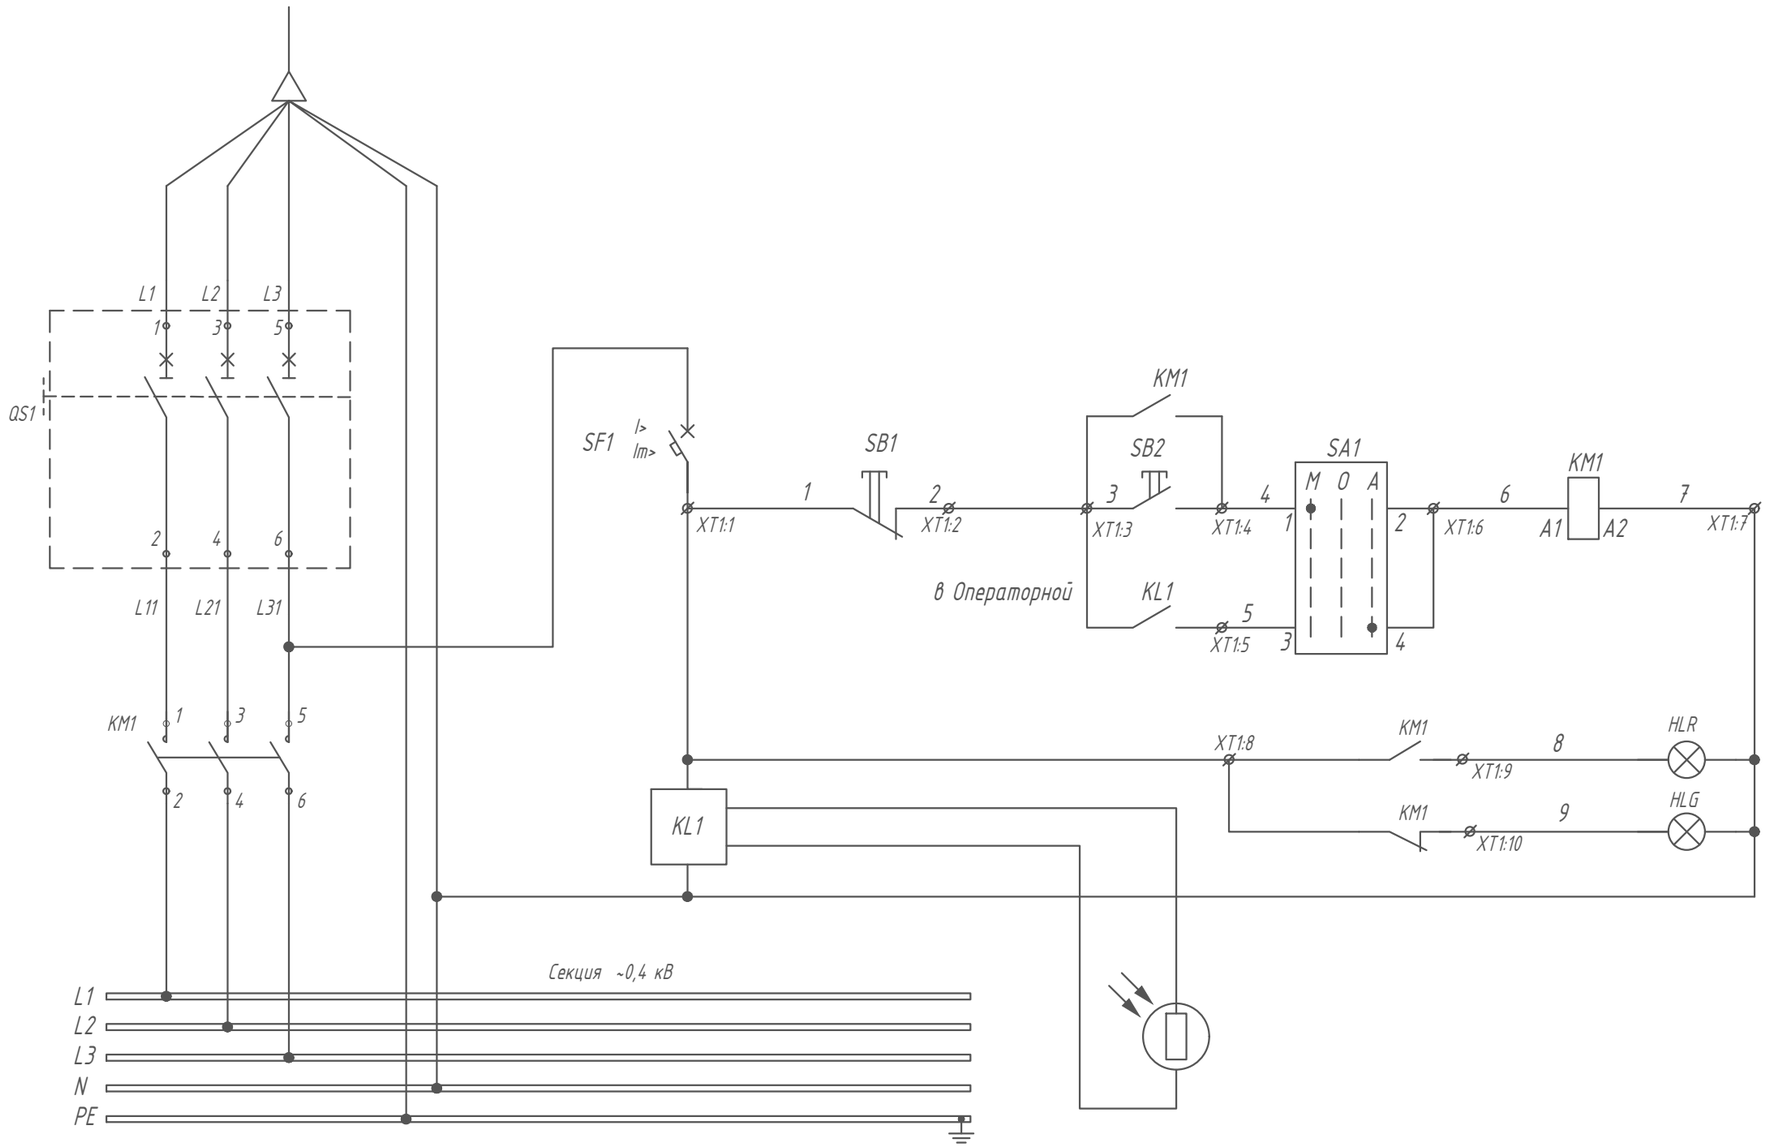

Ручное управление	Ключ выбора вариантов управления
Автомати – ческое управление	
"Включено"	Сигнализация на фасаде щита
"Отключено"	

Взам. инв. №	Подп. и дата	Инв. № подл.

Изм.	Кол. уч	Лист	№ док	Подп.	Дата	EWE0426-MGL1-ELE-054-DSH-801511-R1	Лист 6

Формат А3