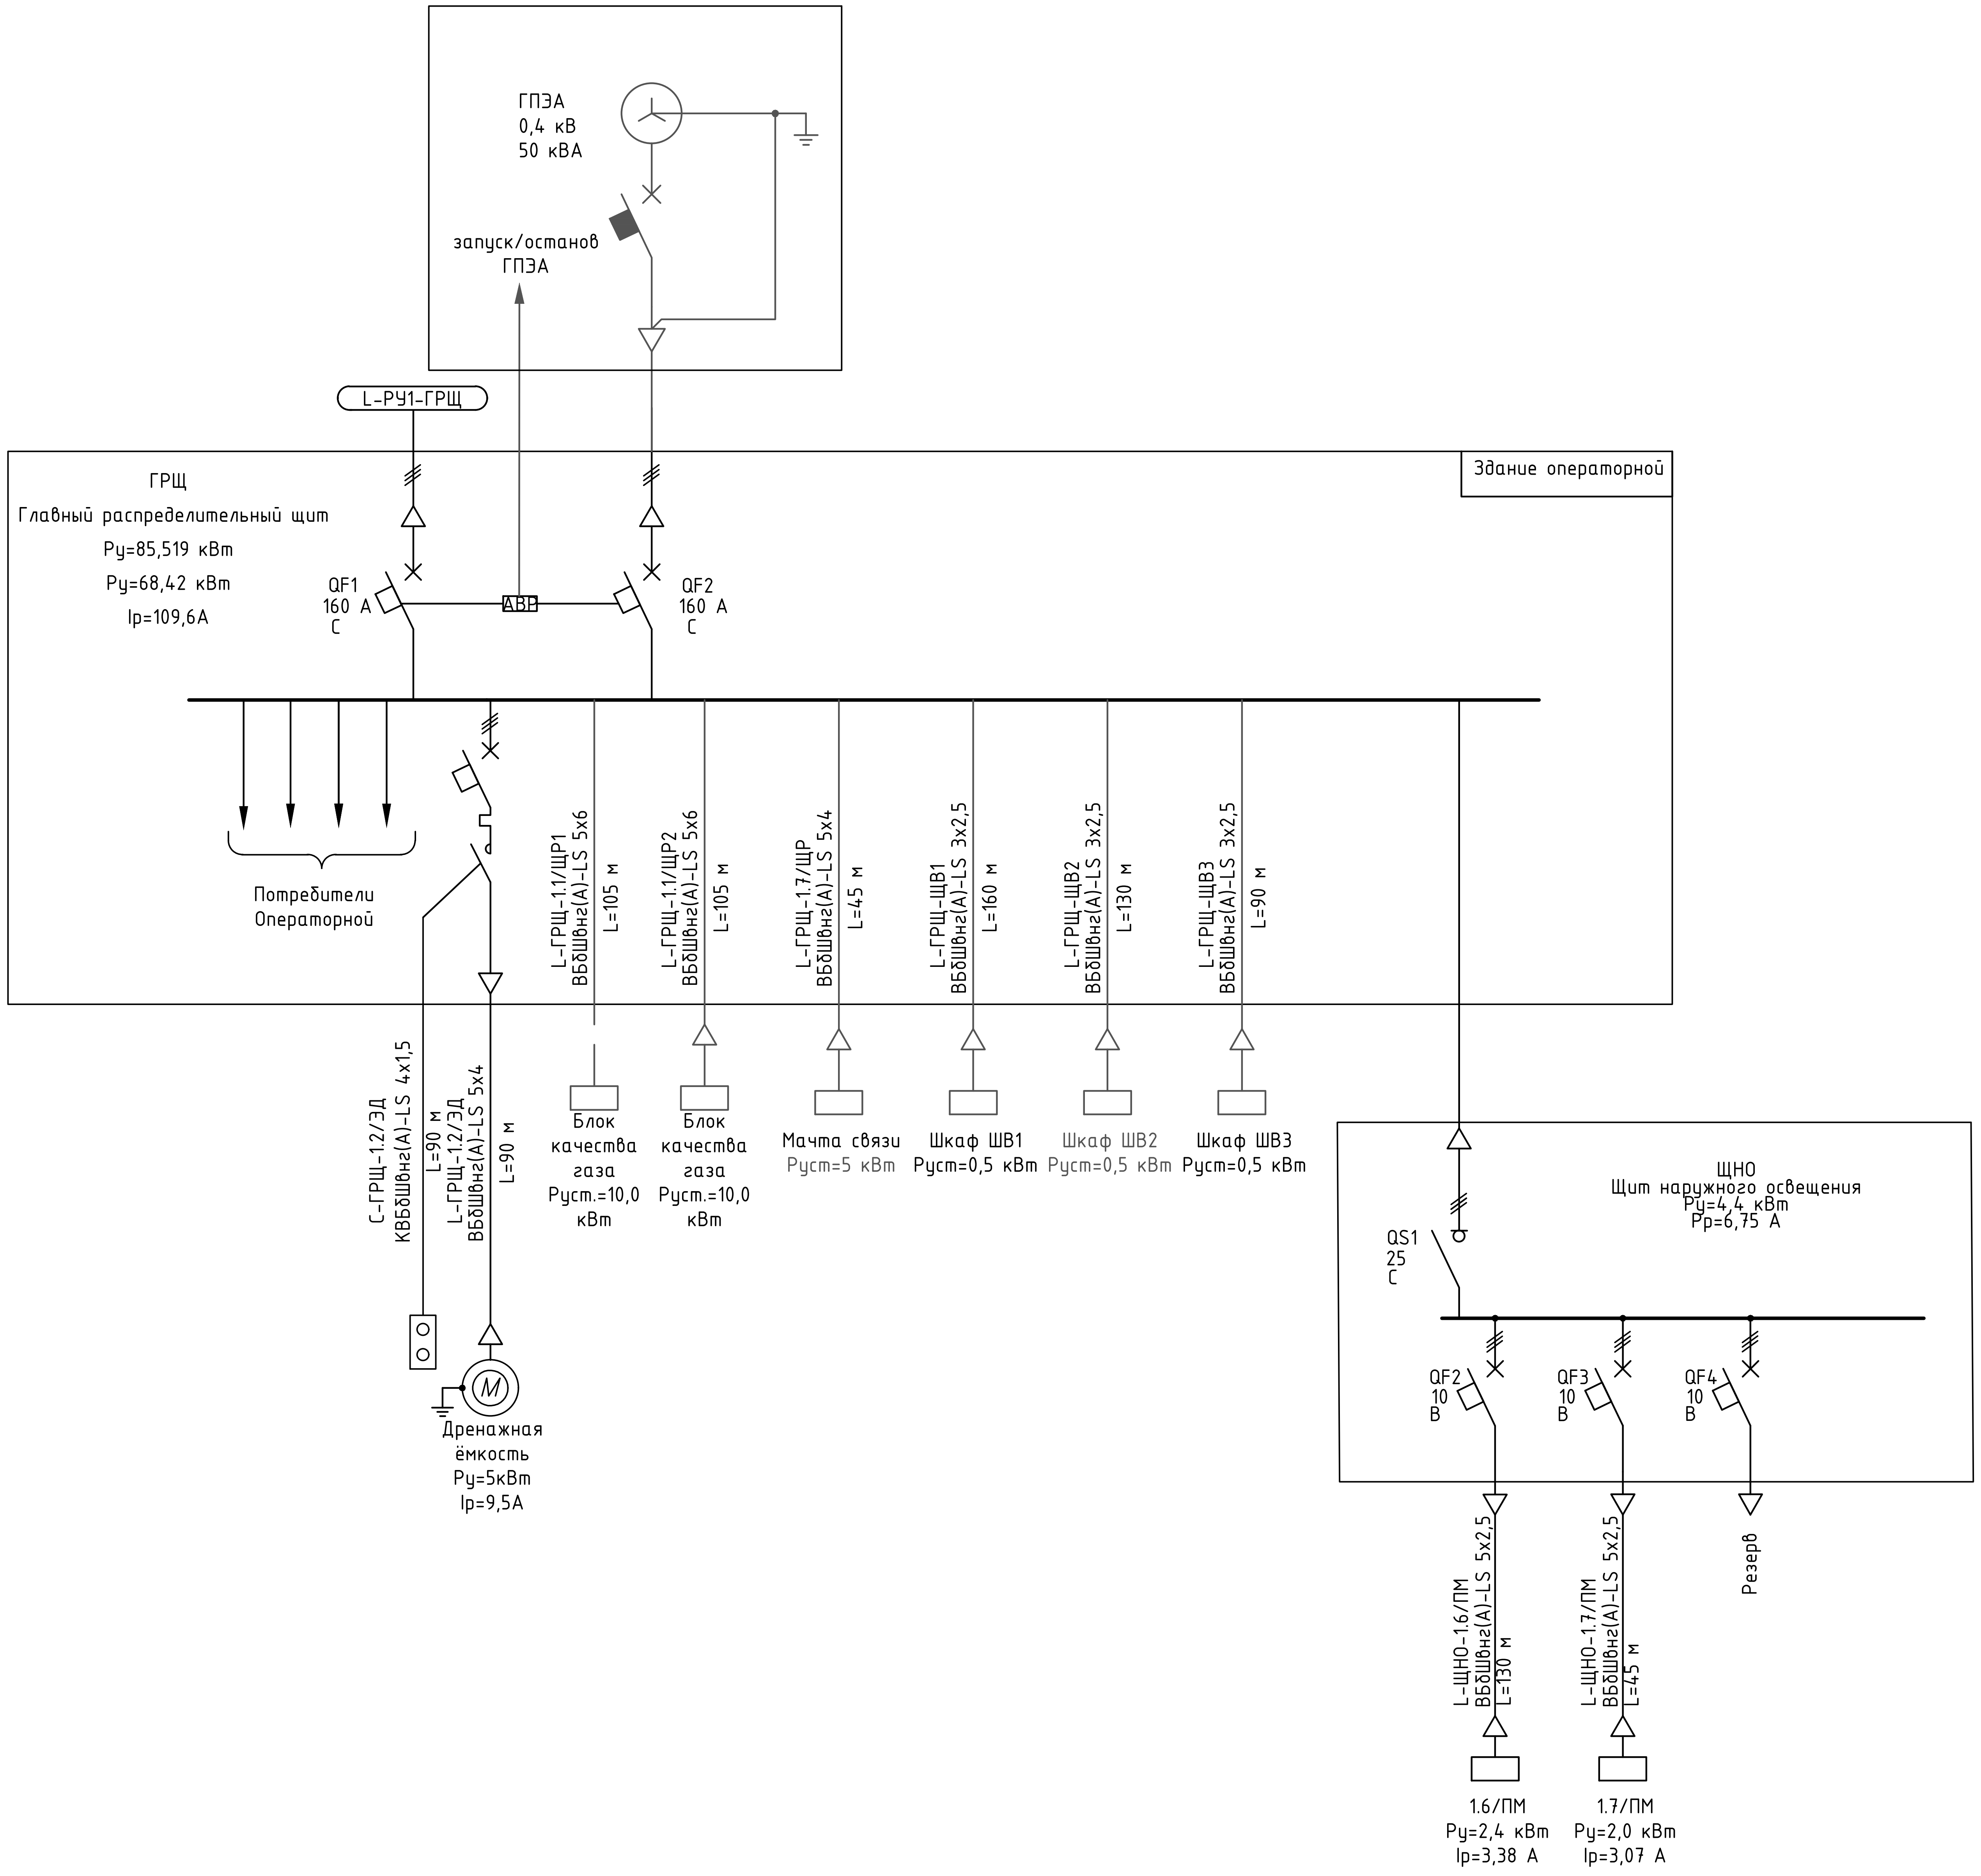

Примечания:

1. Главный распределительный щит (ГРЩ) операторной предусматривается с электроснабжением от ближайшей столбовой трансформаторной подстанции (ТП), от резервной секции РУ-0,4 кВ.
2. Основным источником электроснабжения ГРЩ является сеть 0,4 кВ от указанной ТП. При исчезновении или недопустимом снижении напряжения на основном вводе предусматривается автоматическое отключение основного ввода с последующим формированием сигнала на автоматический запуск газопоршневого электроагрегата (ГПЭА).
3. После выхода ГПЭА на номинальные параметры и при наличии устойчивого напряжения предусматривается автоматическое переключение нагрузки ГРЩ на резервный источник электроснабжения — ГПЭА.
4. Переключение источников электроснабжения должно выполняться с обеспечением электрической и механической блокировки вводных аппаратов, исключающей одновременное подключение основного и резервного источников и возможность подачи встречного напряжения в сеть ТП.
5. После восстановления напряжения на основном вводе и при выполнении заданных условий по времени выдержки предусматривается автоматическое обратное переключение нагрузки ГРЩ на основной источник с последующим отключением ГПЭА и его работой в режиме охлаждения перед остановом.
6. Система автоматического ввода резерва (АВР), управления и запуска ГПЭА должна обеспечивать приоритет основного источника, контроль наличия и качества напряжения на вводах, последовательность переключений, необходимые выдержки времени, а также передачу сигналов аварии и состояния оборудования в систему диспетчеризации/автоматизации объекта.
7. Параметры уставок реле контроля напряжения, выдержки времени отключения основного ввода, запуска ГПЭА, переключения нагрузки и обратного ввода принимаются согласно проектной документации, техническим условиям на подключение и требованиям изготовителя ГПЭА и оборудования АВР.

Процедура нумерации кабелей

L-16/ РУ 1-3.2/ НКУ -1(А,В)

L	-	16/ РУ 1	-	3.2/ НКУ	-	1	(А,В)
ТИП КАБЕЛЯ: Н - выше 1 кВ; L - ниже 1 кВ; С - контрольный; DC - кабель постоянного тока		ТАГОВЫЙ НОМЕР НАЧАЛА КАБЕЛЯ (ИСТОЧНИК): здание 16 по экспликации / ЩИТ РУНН секция 1		ТАГОВЫЙ НОМЕР КОНЦА КАБЕЛЯ (ПОТРЕБИТЕЛЬ): с ооружение 3.2 по экспликации / Потребители ГПА. Щит распределительный		ПОРЯДКОВЫЙ НОМЕР ВВОДА (или питающей секции)	КОЛИЧЕСТВО ПАРАЛЕЛЬНЫХ КАБЕЛЕЙ (если больше 1 го кабеля): А,В - 2 паралеьных кабеля

Рев.	Дата	Назначение ревизии	Проверил	Утвердил
R1	12.08.2026	Выпущено для рассмотрения		

ЗАКАЗЧИК: UTG UZTRANSGAZ
ГЕНЕРАЛЬНЫЙ ПОДРЯДЧИК: UET UZBEKENERGOTAMIR
ПОДРЯДЧИК: PBG Pro Build Generation
ГЕНЕРАЛЬНЫЙ ПРОЕКТИРОВЩИК: EAST WEST ENGINEERING

EWE0426-MGL1-ELE-054-SCM-801502-R1

«СТРОИТЕЛЬСТВО НОВЫХ НИТОК (УЧАСТКОВ) ГАЗОПРОВОДОВ «ГАЗЛИ - САРИМОЙ» И «АКЧАЛОК - ГАЗЛИ - НУКУС» ОБЩЕЙ ПРОТЯЖЕННОСТЬЮ НЕ МЕНЕЕ 275 КМ».

Изм.	Кол. уч.	Лист.	№док.	Подп.	Дата
ГИП		Схабицкий А.			08.2026
Нач.отд.		Гимранов Т.			08.2026
Исполн.		Пац В.			08.2026
Н. контр.		Схабицкий А.			08.2026

ГАЗОПРОВОД «ГАЗЛИ-САРИМОЙ» (54 КМ)
Площадка УЗРГ.
Внутриплощадочные коммуникации

Стадия	Лист	Листов
РП	1	1

Схема электроснабжения

ООО "EAST-WEST Engineering"
г. Ташкент 2026г.

Формат А2

Взам. инв. №
Подпись и дата
Инв.№ подл.