
Данные питающей сети		
Шинопровод, распределительное устройство	Обозначение, тип, Iном,А расцепитель или плавкая вставка, А	
	Тип, напряжение, сечение (шинопровод), расчетный ток, А устан. мощность, кВт	
Аппарат отход. линии	Обозначение, тип, Iном., А расцепитель или плавкая вставка, А	
Пусковой аппарат	Тип, Iном., А, нагрев. элемент теплового реле уставка, А	
Кабельная линия		
Электроприемник	Условное обозначение по плану	
	Номер по плану	
	Тип	
	Руст, кВт	
	Ррасч, кВт	
	Iном, А	
	Iпуск, А	
	Наименование механизма по плану	
	Номер по технологическому плану	

	1.6/ПМ	1.7/ПМ
	–	–
	2,4	2,0
	2,4	2,0
	3,38	3,07
	3,38	3,07
Вводной выключатель / пускатель, управляемый от фотодатчика или вручную	Прожекторная мачта №1	Прожекторная мачта №2
	ПМ1.6	ПМ 1.7

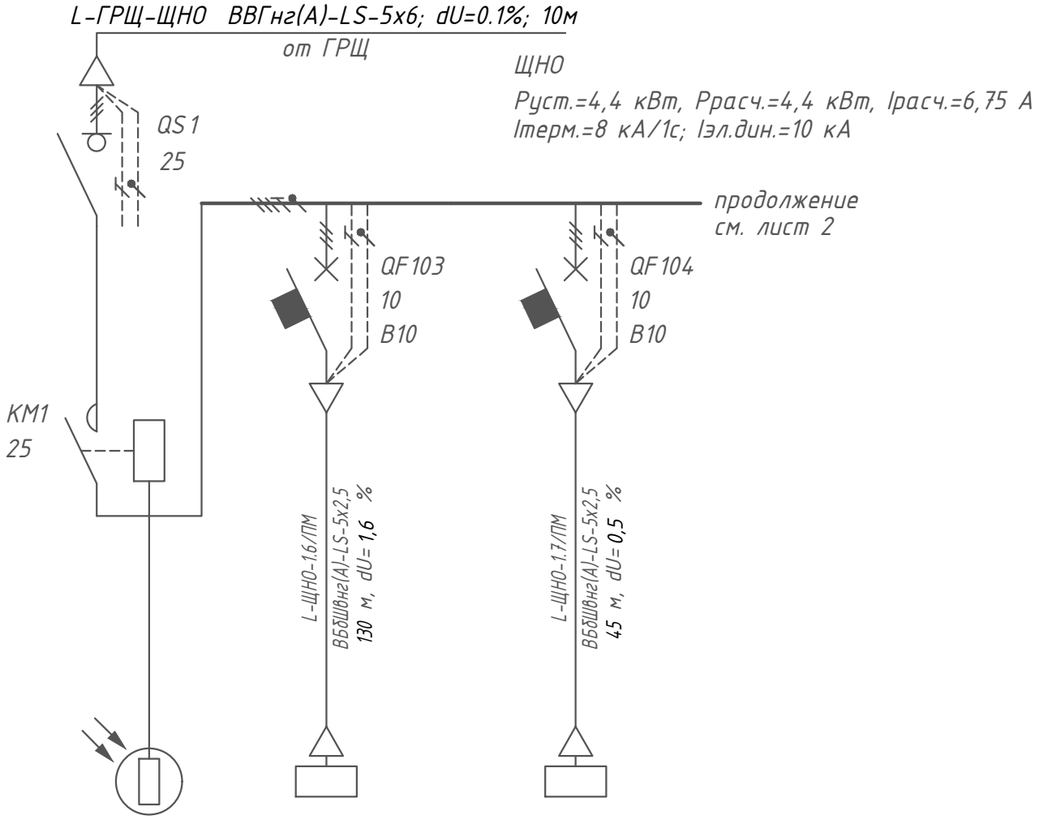

- номер коммутационного аппарата
- тип коммутационного аппарата и номинальный ток
- уставка расцепителя защиты от перегрузки
- время-токовая характеристика защитного аппарата
- уставка расцепителя защиты от токов утечки (если устанавливается)

Рев.	Дата	Назначение ревизии	Проверил	Утвердил
R1	12.08.2026	Выпущено для рассмотрения		

ЗАКАЗЧИК: UTG UZBEKNEFTEGAZ | ГЕНЕРАЛЬНЫЙ ПОДРЯДЧИК: UET UZBEKENERGOTAMIR | ПОДРЯДЧИК: PBG Pro Build Generation | ГЕНЕРАЛЬНЫЙ ПРОЕКТИРОВЩИК: EAST WEST ENGINEERING

Изм.	Кол. уч.	Лист.	№док.	Подп.	Дата
ГИП		Схабицкий А.			08.2026
Нач.отд.		Гимранов Т.			08.2026
Исполн.		Пац В.			08.2026
Н. контр.		Схабицкий А.			08.2026

EWE0426-MGL1-ELE-054-SCM-801507-R1

«СТРОИТЕЛЬСТВО НОВЫХ НИТОК (УЧАСТКОВ) ГАЗОПРОВОДОВ «ГАЗЛИ – САРИМОЙ» И «АКЧАЛОК – ГАЗЛИ – НУКУС» ОБЩЕЙ ПРОТЯЖЕННОСТЬЮ НЕ МЕНЕЕ 275 КМ».

ГАЗОПРОВОД «ГАЗЛИ-САРИМОЙ» (54 КМ)
Площадка УЗРГ.
Внутриплощадочные коммуникации

Стадия	Лист	Листов
РП	1	3


Щит наружного освещения. Схема электрическая однолинейная

ООО "EAST-WEST Engineering"
г. Ташкент 2026г.

Взам. инв. № | Подпись и дата | Инв.№ подл.

Формат А3

Данные питающей сети				
Шинопровод, распределительное устройство	Обозначение, тип, Iном,А расцепитель или плавкая вставка, А			
	Тип, напряжение, сечение (шинопровод), расчетный ток, А устан. мощность, кВт			
Аппарат отход. линии	Обозначение, тип, Iном., А расцепитель или плавкая вставка, А			
Пусковой аппарат	Тип, Iном., А, нагрев. элемент теплового реле уставка, А			
Кабельная линия				
Электроприемник	Условное обозначение по плану			
	Номер по плану			
	Тип			
	Руст, кВт			
	Ррасч, кВт			
	Iном, А			
	Iпуск, А			
	Наименование механизма по плану Номер по технологическому плану	Освещение навеса	Резерв	УЗИП

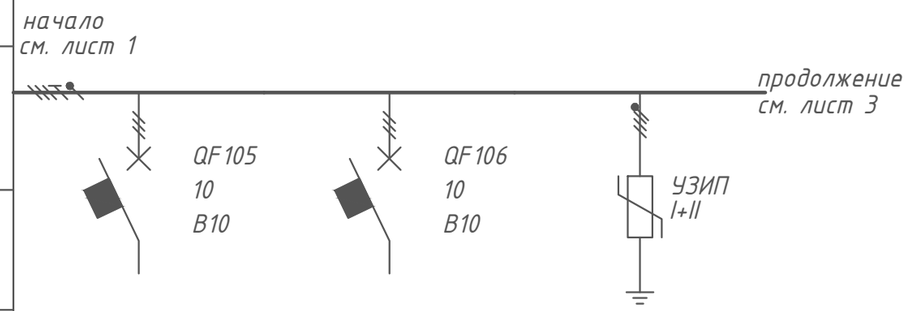


QF4 – номер коммутационного аппарата
iC60L – тип коммутационного аппарата и номинальный ток
63 – уставка расцепителя защиты от перегрузки
хар.C – время-токовая характеристика защитного аппарата
30 мА – уставка расцепителя защиты от токов утечки (если устанавливается)

Взам. инв. №
Подп. и дата
Инв. № подл.

Изм.	Кол. уч	Лист	№ док	Подп.	Дата	EWE0426-MGL1-ELE-054-SCM-801507-R1	Лист 2

Формат А3

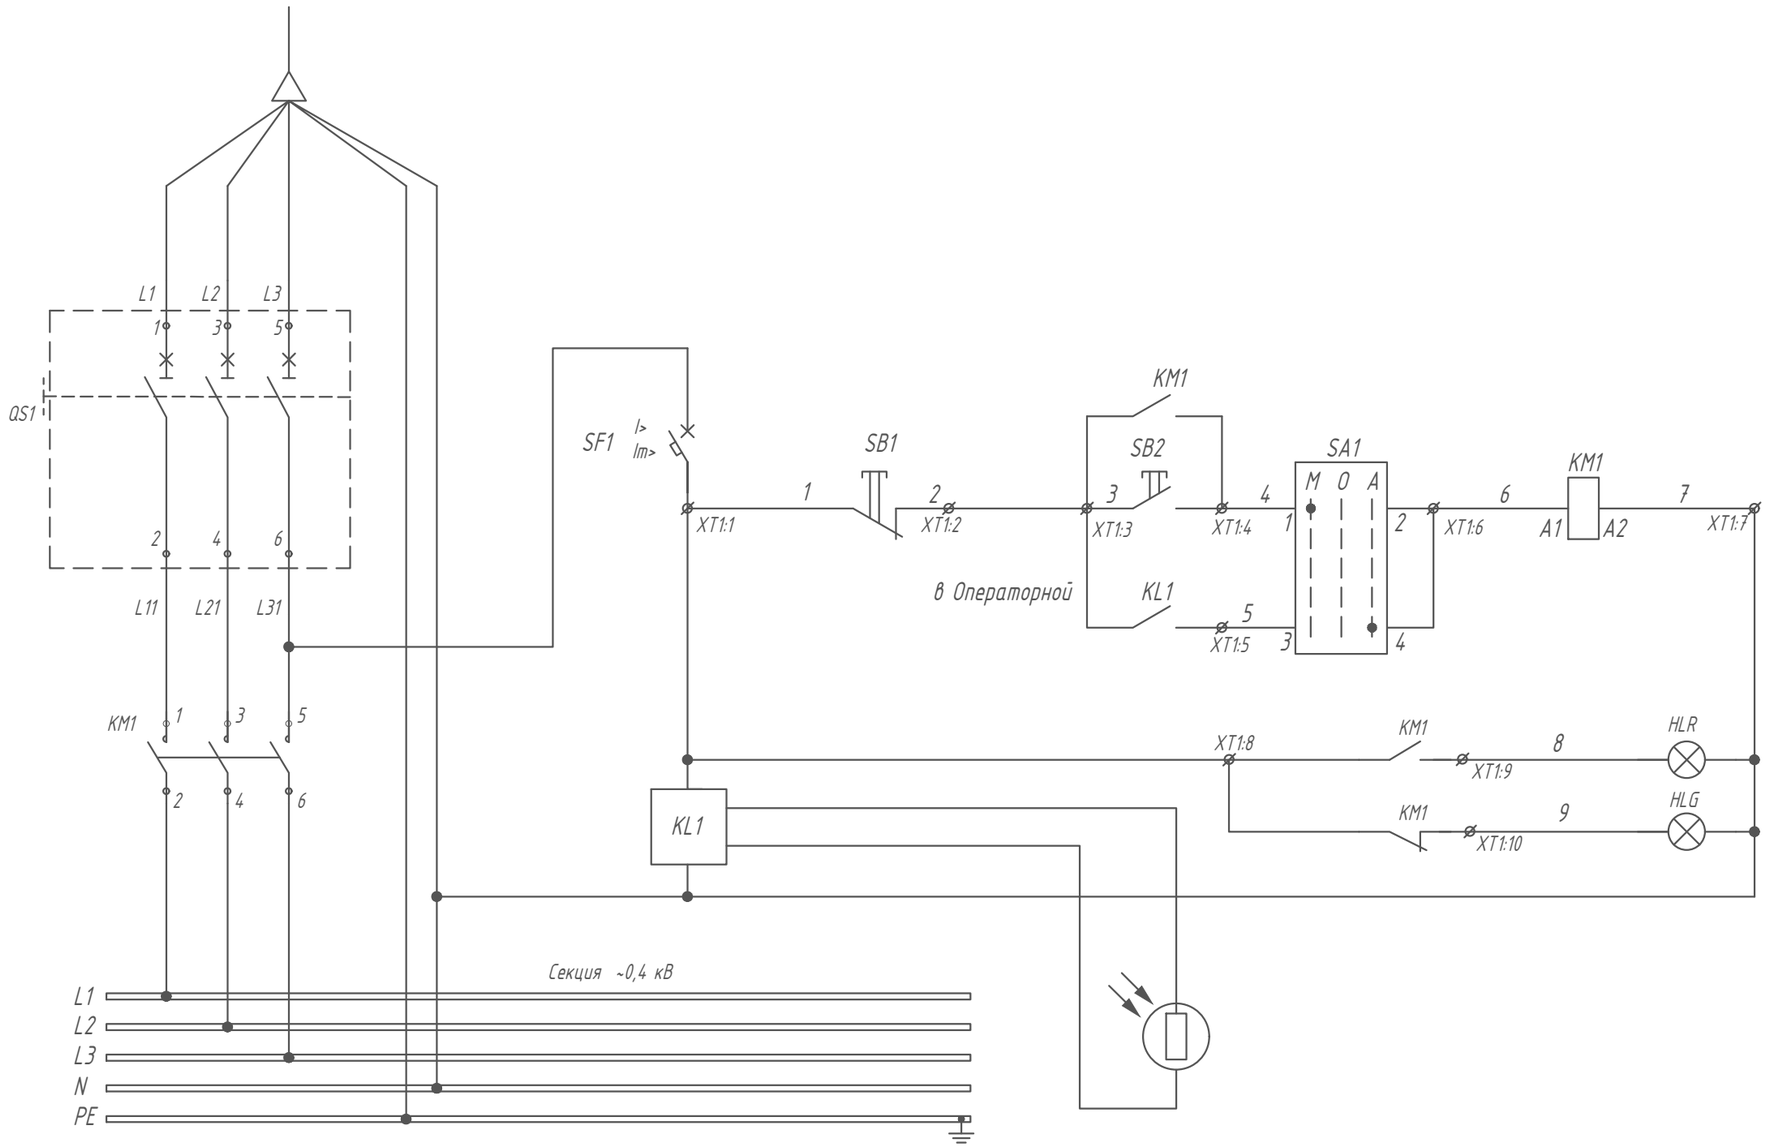

Ручное управление	Ключ выбора вариантов управления
Автомати – ческое управление	
"Включено"	Сигнализация на фасаде щита
"Отключено"	

Изм.	Кол. уч	Лист	№ док	Подп.	Дата	EWE0426-MGL1-ELE-054-SCM-801507-R1	Лист 3

Взам. инв. №

Подп. и дата

Инв. № подл.

Формат А3