План (1:50)

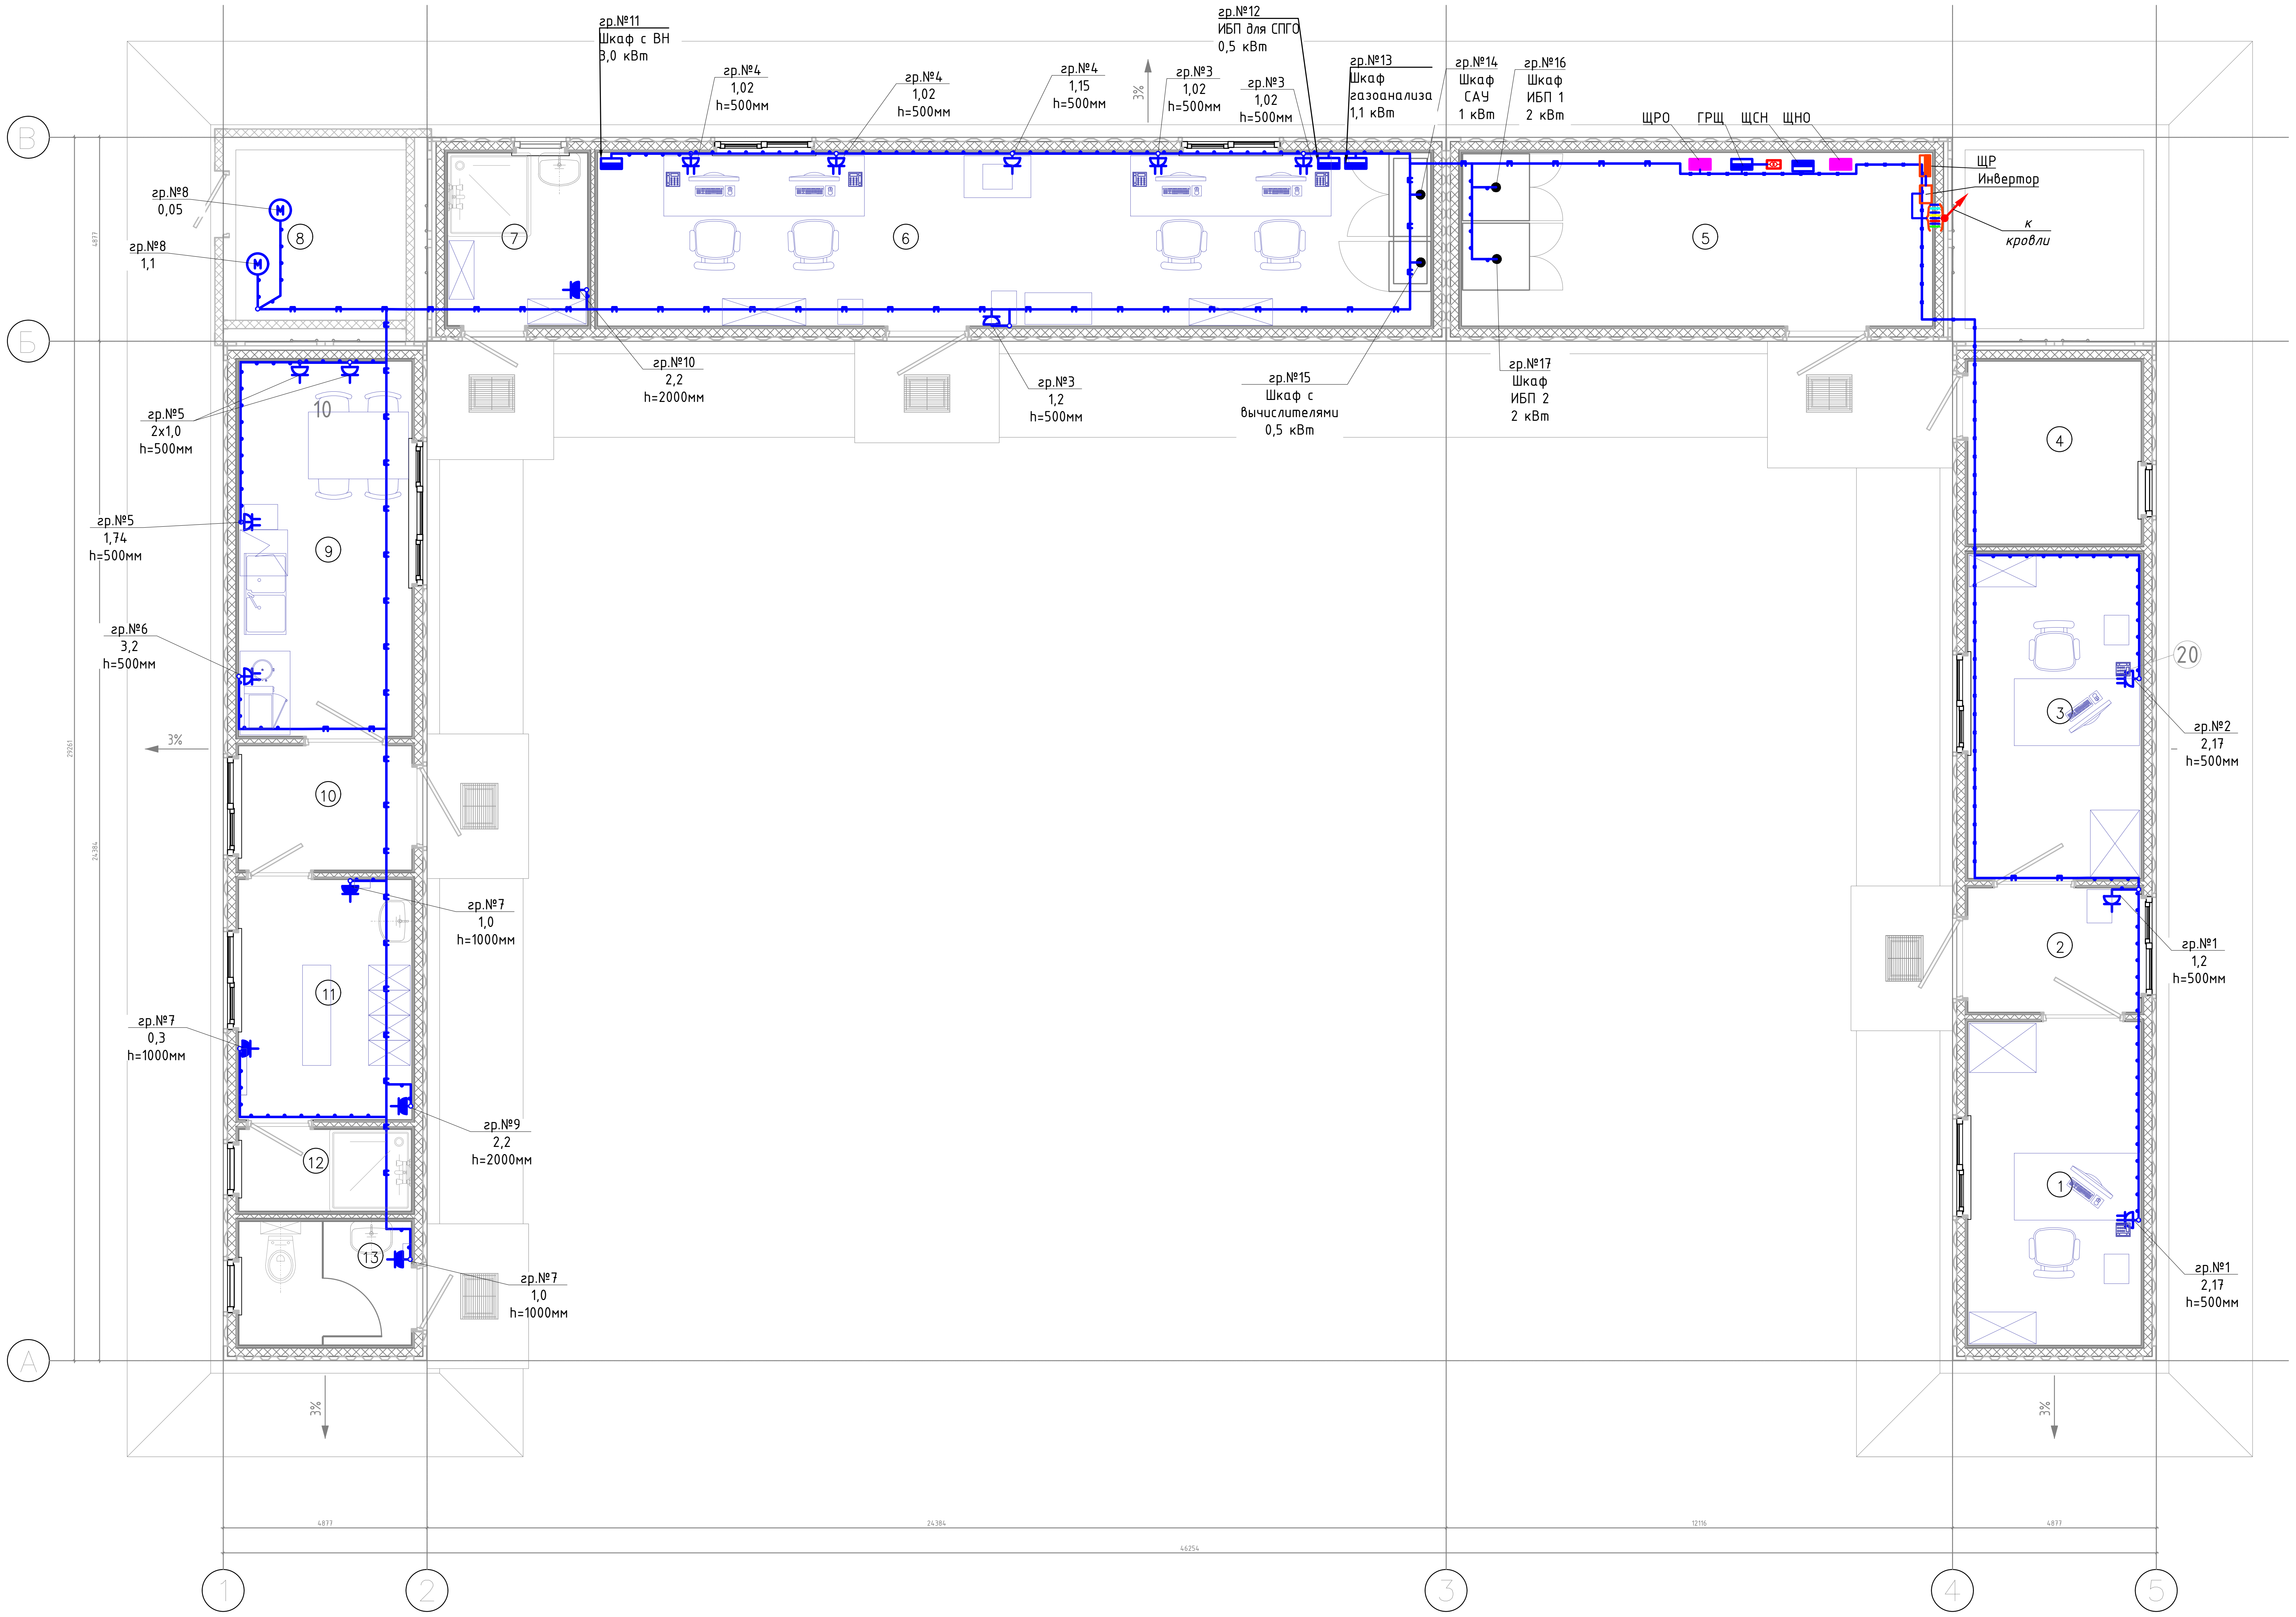

Экспликация помещений

№	Наименование	Площадь, $м^2$	Кат. помещения
1	Кабинет ведущего инженера	8,10	?
2	Тамбур	3,10	?
3	Кабинет инженера химика	8,10	?
4	Кладовая	4,60	?
5	Электрощитовая	11,80	?
6	Кабинет операторов	20,80	?
7	Душ	3,50	—
8	Насосная	4,40	?
9	Комната отдыха и приема пищи	9,40	—
10	Тамбур	3,10	?
11	Гардероб	6,00	?
12	Душ	2,10	—
13	С/У	3,10	—

Поз.	Обозначение	Наименование	Кол.	Масса ед., кг	Примечание
1	Код 53801	Коробка ответвительная пластмассовая наружная с 6-ю кабельными вводами, IP55, 100х100х50, шт.	20	0,22	
2	Код 43212NY	Клеммная колодка на 12 клемм, на ток 24А, шт.	20	0,05	
3		Розетка штепсельная, для открытой установки, одноместная, с заземленным контактом, IP20, шт.	5	0,25	
4		Розетка штепсельная, открытой установки, одноместная, с заземленным контактом с крышкой, IP65, шт.	5	0,25	
5		Розетка штепсельная, для открытой установки, двухместная, с заземленным контактом, IP20, шт.	6	0,35	
6		Розетка штепсельная, для открытой установки, трехместная, с заземленным контактом, IP20, шт.	2	0,35	
7	ГОСТ 31996-2012	Кабель ВВГнг(А)-LS-3х2,5-0,66, м	505	0,18	
8	ГОСТ 31996-2012	Кабель ВВГнг(А)-LS-3х4-0,66, м	375	0,2	
9	ГОСТ 31996-2012	Кабель ВВГнг(А)-LS-3х6-0,66, м	205	0,29	
10	ГОСТ 31996-2012	Кабель ВВГнг(А)-LS-5х6-0,66, м	10	0,45	
11	ГОСТ 31996-2012	Кабель ВВГнг(А)-LS-5х10-0,66, м	20	0,67	
12	ГОСТ 31996-2012	Кабель ВВГнг(А)-LS-5х16-0,66, м	10	1,16	

Примечания:

1. Питающая сеть выполнена кабелем ВВГнг(А)-LS.
2. Прокладку кабелей выполнять:

а) в кабельных коробах 80х40 мм и мини-каналах 50х20, 15х17 мм;

б) места ответвительных коробок указаны условно и требуют уточнения по месту;

в) спуски кабелей к розетками осуществляется открыто в кабель мини-каналах 15х17 мм, закрепленных к стене.

3. Размеры и привязки приведены для справок, нарезку кабеля производить после уточнения трасс.
4. При проходе кабелей через стены кабели защитить отрезками трубы, которую после прокладки кабелей заделать легкопробиваемым негорючим составом.
5. За относительную отметку 0,000 принят уровень чистого пола.

Условные обозначения:

━┷━	– Кабель в кабельном коробе;
⏚	– Штепсельная двухполюсная одноместная розетка открытой установки, с защитными контактами, IP20;
⏚	– Штепсельная двухполюсная одноместная розетка открытой установки, с защитными контактами, IP65;
⏚	– Штепсельная двухполюсная двухместная розетка открытой установки, с защитными контактами, IP20;
⏚	– Штепсельная двухполюсная трехместная розетка открытой установки, с защитными контактами, IP20;
○	– Коробка ответвительная для открытой установки.

Расшифровка обозначения на плане:

Номер группы
гр.№4
Мощность оборудования, кВт
1,5
h-500
Высота установки

Рев.	Дата	Назначение ревизии	Проверил	Утвердил
R1	12.08.2026	Выпущено для рассмотрения		

ЗАКАЗЧИК:
ГЕНЕРАЛЬНЫЙ ПОДРЯДЧИК:
ПОДРЯДЧИК:
ГЕНЕРАЛЬНЫЙ ПРОЕКТИРОВЩИК:

EWE0426-MGL1-ELE-054-DRW-800402-R1

«СТРОИТЕЛЬСТВО НОВЫХ НИТОК (УЧАСТКОВ) ГАЗОПРОВОДОВ «ГАЗЛИ – САРИМОЙ» И «АКЧАЛОК – ГАЗЛИ – НУКУС» ОБЩЕЙ ПРОТЯЖЕННОСТЬЮ НЕ МЕНЕЕ 275 КМ».

Изм.	Кол. уч.	Лист.	№док.	Подп.	Дата
ГИП		Схабицкий А.			08.2026
Нач.отд.		Гимранов Т.			08.2026
Исполн.		Пац В.			08.2026
Н. контр.		Схабицкий А.			08.2026

ГАЗОПРОВОД «ГАЗЛИ-САРИМОЙ» (54 КМ)
ОПЕРАТОРНАЯ

Стадия	Лист	Листов
РП	1	1

План питающей сети,
сети электроснабжения технологического
оборудования и розеточной сети

ООО "EAST-WEST Engineering"
г. Ташкент 2026г.

Формат А1

Взам. инв. №
Подпись и дата
Инв.№ подл.