
План (1:50)

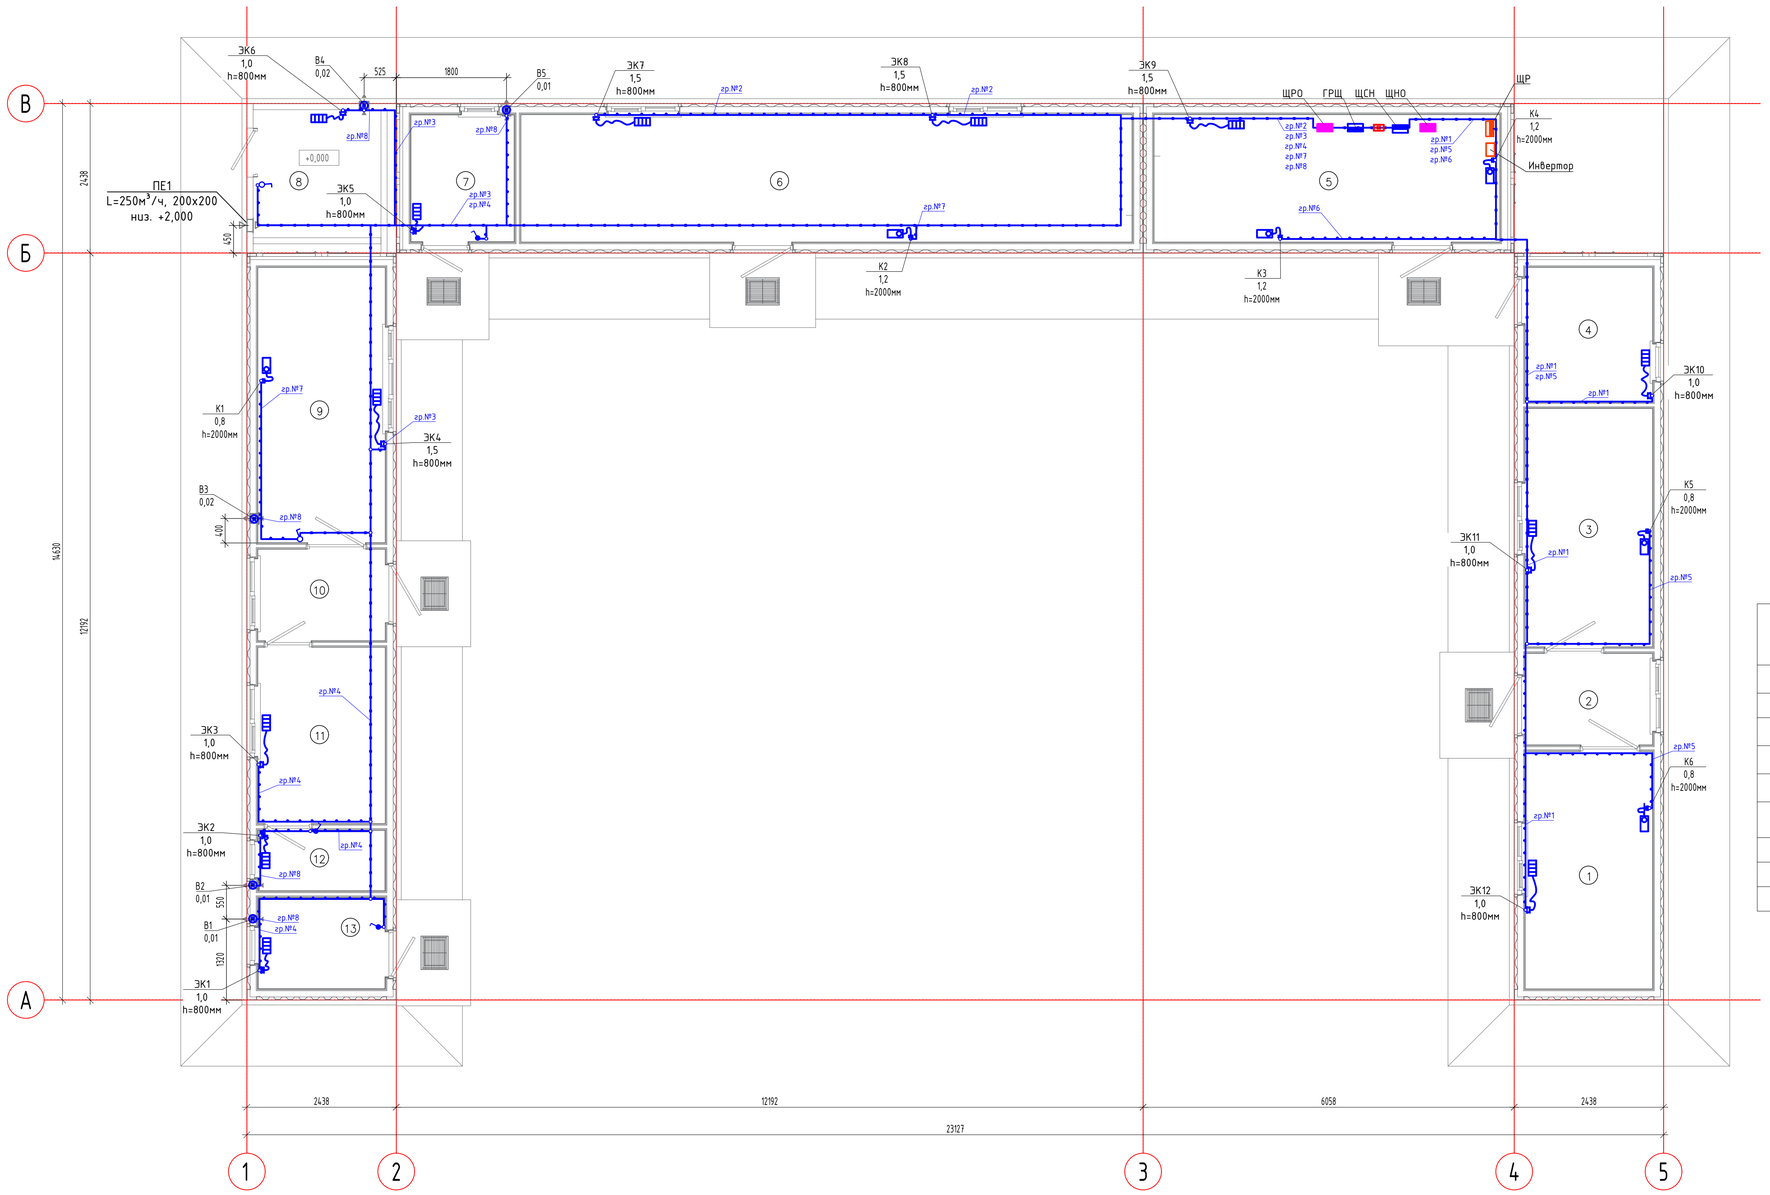

Экспликация помещений


№	Наименование	Площадь, м²	Кат. помещения
1	Кабинет ведущего инженера	8,10	?
2	Тамбур	3,10	?
3	Кабинет инженера химика	8,10	?
4	Кладовая	4,60	?
5	Электрощитовая	11,80	?
6	Кабинет операторов	20,80	?
7	Душ	3,50	–
8	Насосная	4,40	?
9	Комната отдыха и приема пищи	9,40	–
10	Тамбур	3,10	?
11	Гардероб	6,00	?
12	Душ	2,10	–
13	С/У	3,10	–

Поз.	Обозначение	Наименование	Кол.	Масса ед., кг	Приме-чание
1	Код 53801	Коробка ответвительная пластмассовая наружная с 6-ю кабельными вводами, IP55, 100х100х50, шт.	4,0	0,22	
2	Код 43212NY	Клеммная колодка на 12 клемм, на ток 24А, шт.	4,0	0,05	
3		Выключатель одноклавишный открытой установки 16А, IP20, шт.	2	0,1	
4		Выключатель одноклавишный открытой установки 16А, IP65, шт.	3	0,1	
5		Розетка штепсельная, для открытой установки, одноместная, с заземленным контактом, IP20, шт.	15	0,25	
6		Розетка штепсельная, открытой установки, одноместная, с заземленным контактом с крышкой, IP65, шт.	3	0,25	
7	ГОСТ 31996-2012	Кабель ВВГнг(А)-LS-3х4-0,66	225		
8	ГОСТ 31996-2012	Кабель ВВГнг(А)-LS-3х6-0,66	165		
9	ГОСТ 31996-2012	Кабель ВВГнг(А)-LS-3х2,5-0,66	120		

Примечания:
1. Питающая сеть выполнена кабелем ВВГнг(А)-LS.
2. Щит ЩСН установить на отм. +1,500 от пола.
3. Прокладку кабелей выполнять:
а) в кабельных коробах 200х80 мм;
б) места ответвительных коробок указаны условно и требуют уточнения по месту;
в) спуски кабелей к розеткам осуществляется открыто в кабель мини-каналах 15х17 мм, закрепленных к стене.
4. Размеры и привязки приведены для справок, нарезку кабеля производить после уточнения трасс.
5. Управление канальным вентилятором осуществляется индивидуальным выключателем.
6. При проходе кабелей через стены кабели защитить отрезками трубы, которую после прокладки кабелей заделать легкопробиваемым негорючим составом.
7. За относительную отметку 0,000 принят уровень чистого пола.

Условные обозначения:
- Кабель проложенный в кабельном лотке;
- Кабель проложенный в металлорукаве;
- Штепсельная двухполюсная розетка открытой установки, с защитными контактами, IP20;
- Штепсельная двухполюсная розетка открытой установки, с защитными контактами, IP65;
- Электроконвектор;
- Сплит-система, внутренний блок;
- Канальный вентилятор, вытяжной мобильный вентилятор разо-бытового назначения;
- Выключатель одноклавишный открытой установки, IP20;
- Коробка ответвительная для открытой установки.

Расшифровка обозначения на плане:

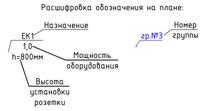

R1	12.08.2026	Выпущено для рассмотрения			
Рев.	Дата	Назначение ревизии		Проверил	Утвердил

ЗАКАЗЧИК: ГЕНЕРАЛЬНЫЙ ПОДРЯДЧИК: ПОДРЯДЧИК: ГЕНЕРАЛЬНЫЙ ПРОЕКТИРОВЩИК:

EWE0426-MGL1-ELE-054-DRW-800404-R1

«СТРОИТЕЛЬСТВО НОВЫХ НИТОК (УЧАСТКОВ) ГАЗОПРОВОДОВ «ГАЗЛИ – САРИМОЙ» И «АКЧАЛОК – ГАЗЛИ – НУКУС» ОБЩЕЙ ПРОТЯЖЕННОСТЬЮ НЕ МЕНЕЕ 275 КМ».

Изм.	Кол. уч.	Лист.	№док.	Подп.	Дата
ГИП		Схабицкий А.			08.2026
Нач.отд.		Гимранов Т.			08.2026
Исполн.		Пац В.			08.2026
Н. контр.		Схабицкий А.			08.2026

ГАЗОПРОВОД «ГАЗЛИ-САРИМОЙ» (54 КМ) ОПЕРАТОРНАЯ

Стадия	Лист	Листов
РП	1	1

План систем вентиляции и кондиционирования

ООО "EAST-WEST Engineering" г. Ташкент 2026г.

Взам. инв. № | Подпись и дата | Инв.№ подл.

Формат А1