

План на отм. 0,000

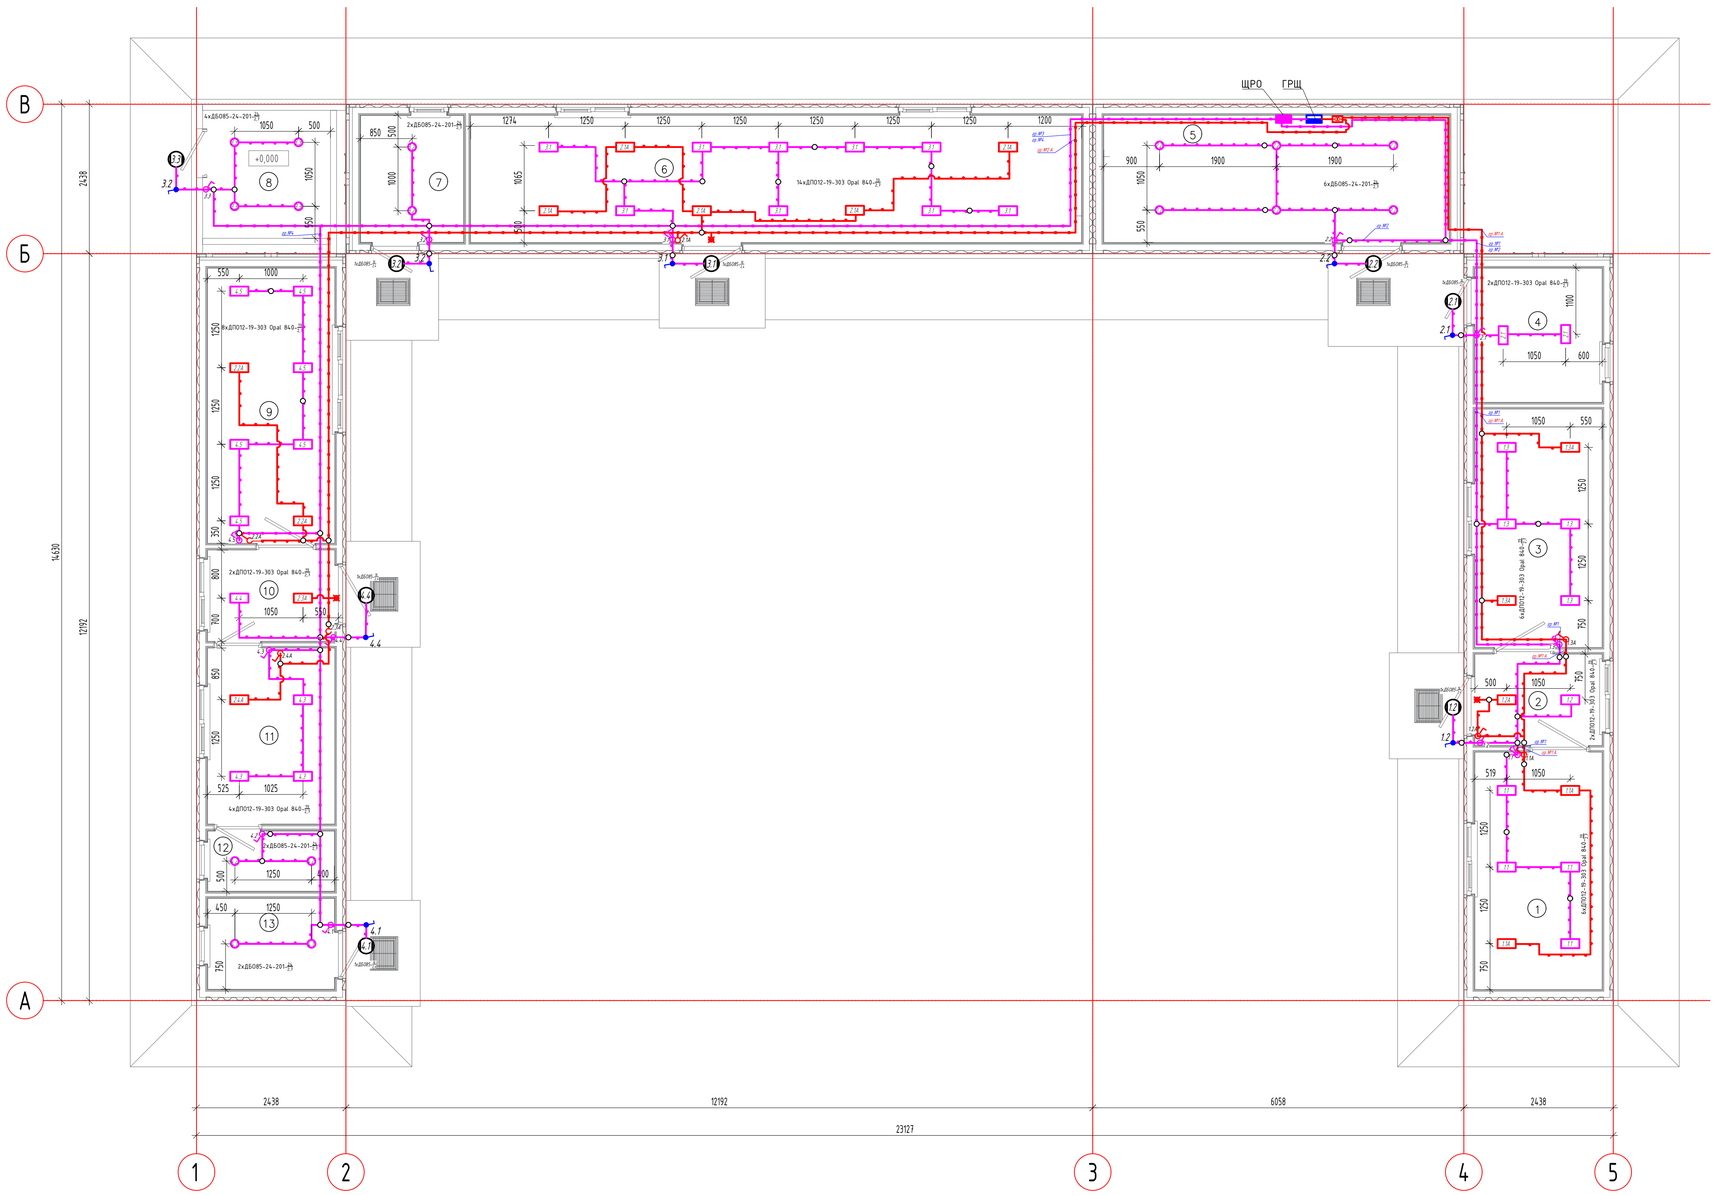


Условные обозначения:

- Кабель рабочего/аварийного освещения, проложенный в кабельном лотке;
- Кабель рабочего/аварийного освещения, проложенный в металлорукаве;
- Светильник светодиодный для установки на поверхность;
- Световые указатели "ВЫХОД";
- Выключатель одноклавишный открытой установки, IP20;
- Выключатель двухклавишный открытой установки, IP20;
- Ящик с безопасным разделительным трансформатором напряжением 220/36 В, мощностью 250 ВА, IP54, ЯТПР-0,25-220/36
- Щиток рабочего освещения;
- Главный распределительный щит;
- Коробка ответвительная для открытой установки.

Расшифровка обозначения на плане:

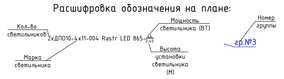


Экспликация помещений

| № | Наименование | Площадь, м² | Кат. помещения |
|---|---|---|---|
| 1 | Кабинет ведущего инженера | 8,10 | ? |
| 2 | Тамбур | 3,10 | ? |
| 3 | Кабинет инженера химика | 8,10 | ? |
| 4 | Кладовая | 4,60 | ? |
| 5 | Электрощитовая | 11,80 | ? |
| 6 | Кабинет операторов | 20,80 | ? |
| 7 | Душ | 3,50 | — |
| 8 | Насосная | 4,40 | ? |
| 9 | Комната отдыха и приема пищи | 9,40 | — |
| 10 | Тамбур | 3,10 | ? |
| 11 | Гардероб | 6,00 | ? |
| 12 | Душ | 2,10 | — |
| 13 | С/У | 3,10 | — |

| Поз. | Обозначение | Наименование | Кол. | Масса ед., кг | Приме-чание |
|---|---|---|---|---|---|
| 1 | ДП012-19-303 Opal 840 | Светодиодный светильник для монтажа на поверхность светодиодный УХЛ4, IP40, шт. | 44 | 2,5 | |
| 2 | ДБ085-24-201 | Светодиодный светильник для монтажа на поверхность светодиодный У1, IP65, шт. | 16 | 1,92 | |
| 3 | *ДБО 85-16* | Светодиодный светильник для монтажа на поверхность светодиодный У1, IP65, шт. | 8 | 1,92 | |
| 4 | ДП078-3-113 Neptun | Указатель выхода-светильник УХЛ4, IP65 с табличкой "ВЫХОД", шт. | 3 | 1,25 | |
| 5 | Код 53801 | Коробка ответвительная пластмассовая наружная с 6-ю кабельными вводами, IP55, 100х100х50, шт. | 60 | 0,22 | |
| 6 | Код 43212NY | Клеммная колодка на 12 клемм, на ток 24А, шт. | 60 | 0,05 | |
| 7 | | Выключатель одноклавишный открытой установки 16А, IP20, шт. | 16 | 0,1 | |
| 8 | | Выключатель одноклавишный открытой установки 16А, IP65, шт. | 8 | 0,1 | |
| 9 | | Выключатель одвухклавишный открытой установки 16А, IP20, шт. | 4 | 0,1 | |
| 10 | ГОСТ 31996-2012 | Кабель ВВГнг(А)-LS-3х2,5-0,66, м | 405 | 0,148 | |
| 11 | ГОСТ 31996-2012 | Кабель ВВГнг(А)-FRLS-3х1,5-0,66, м | 200 | 0,331 | |
| 12 | | Металлорукав МРПИ-15 В ПВХ-оболочке | 230 | 0,217 | |
| 13 | | Короб 200х80 В комплекте с крышкой системы «In-line» длиной 2м | 170 | | |
| 14 | | Ответвитель Т-образный с крышкой для короба 200х80 мм | 4 | | |
| 15 | | Угол 90° для короба с крышкой 200х80 мм | 6 | | |
| 16 | | Крепёжный комплект для кабельного короба 200х80 мм | 375 | | |
| 17 | | Саморез по металлу с шестигранной головкой, оцинкованный, 4,8х19 мм | 750 | | |
| 18 | | Шайба увеличенная оцинкованная | 750 | | |
| 19 | | Монтажная перфорированная полоса/лента оцинкованная, ширина 20–25 мм | 190 | | |
| 20 | | Скоба металлическая однолапковая для металлорукава МР-15 | 286 | | |
| 21 | | Дюбель-гвоздь 6х40 мм | 286 | | |
| 22 | | Саморез по металлу 4,2х16 мм (при креплении к металлическим конструкциям) | 286 | | |
| 23 | ЯТПР-0,25-220/36 | Ящик с безопасным разделительным трансформатором в комплекте с розеткой 36 Вт, 0,25 кВА, 220/36 В, IP20, УХЛ4, компл. | 1 | 9 | |

Примечания:

1. Предусмотрены следующие виды электроосвещения:
а) рабочее ~230В;
б) аварийного (эвакуационное) ~230В.
2. Сеть рабочего освещения, распределительная выполнена кабелем ВВГнг(А)-LS, а эвакуационное ВВГнг(А)-FRLS.
3. Прокладку сети рабочего освещения выполнить:
а) в металлорукаве;
б) опуски к выключателям – в металлорукаве;
б) места ответвительных коробок указаны условно и требуют уточнения по месту.
4. Прокладку сети аварийного освещения выполнить аналогично прокладке сети рабочего освещения, но по разным трассам с рабочим освещением.
5. Размеры и привязки приведены.
6. Пластиковые короба крепить к строительным конструкциям при помощи саморезов.
7. Управление рабочим и аварийным освещением осуществляется индивидуальными выключателями.
8. Питание аварийного (эвакуационного) освещения и ЯТП осуществляется со щита ГРЩ.
9. При проходе кабелей через стены кабели защитить отрезками трубы, которую после прокладки кабелей заделать легкопробиваемым негорючим составом.
10. Выключатели установить на высоте 0,8 м от уровня чистого пола.
11. Все металлические нетоковедущие части осветительной арматуры, нормально не находящиеся под напряжением, заземлить присоединением к специальной жиле (PE) питающего кабеля.
12. Питающая и распределительная сеть выполнена кабелем марки ВВГнг(А)-LS.
13. Способ крепления светильников – потолочный.

| Рев. | Дата | Назначение ревизии | Проверил | Утвердил |
|---|---|---|---|---|
| R1 | 12.08.2026 | Выпущено для рассмотрения | | |

ЗАКАЗЧИК: ГЕНЕРАЛЬНЫЙ ПОДРЯДЧИК: ПОДРЯДЧИК: ГЕНЕРАЛЬНЫЙ ПРОЕКТИРОВЩИК:

EWE0426-MGL1-ELE-054-DRW-800405-R1

«СТРОИТЕЛЬСТВО НОВЫХ НИТОК (УЧАСТКОВ) ГАЗОПРОВОДОВ «ГАЗЛИ – САРИМОЙ» И «АКЧАЛОК – ГАЗЛИ – НУКУС» ОБЩЕЙ ПРОТЯЖЕННОСТЬЮ НЕ МЕНЕЕ 275 КМ».

| Изм. | Кол. уч. | Лист. | №док. | Подп. | Дата |
|---|---|---|---|---|---|
| ГИП | | Схабицкий А. | | | 08.2026 |
| Нач.отд. | | Гимранов Т. | | | 08.2026 |
| Исполн. | | Пац В. | | | 08.2026 |
| Н. контр. | | Схабицкий А. | | | 08.2026 |

ГАЗОПРОВОД «ГАЗЛИ-САРИМОЙ» (54 КМ) ОПЕРАТОРНАЯ

| Стадия | Лист | Листов |
|---|---|---|
| РП | 1 | 1 |

План сети освещения

ООО "EAST-WEST Engineering" г. Ташкент 2026г.

Взам. инв. № | Подпись и дата | Инв.№ подл.

Формат А1