
План кровли М 1:100

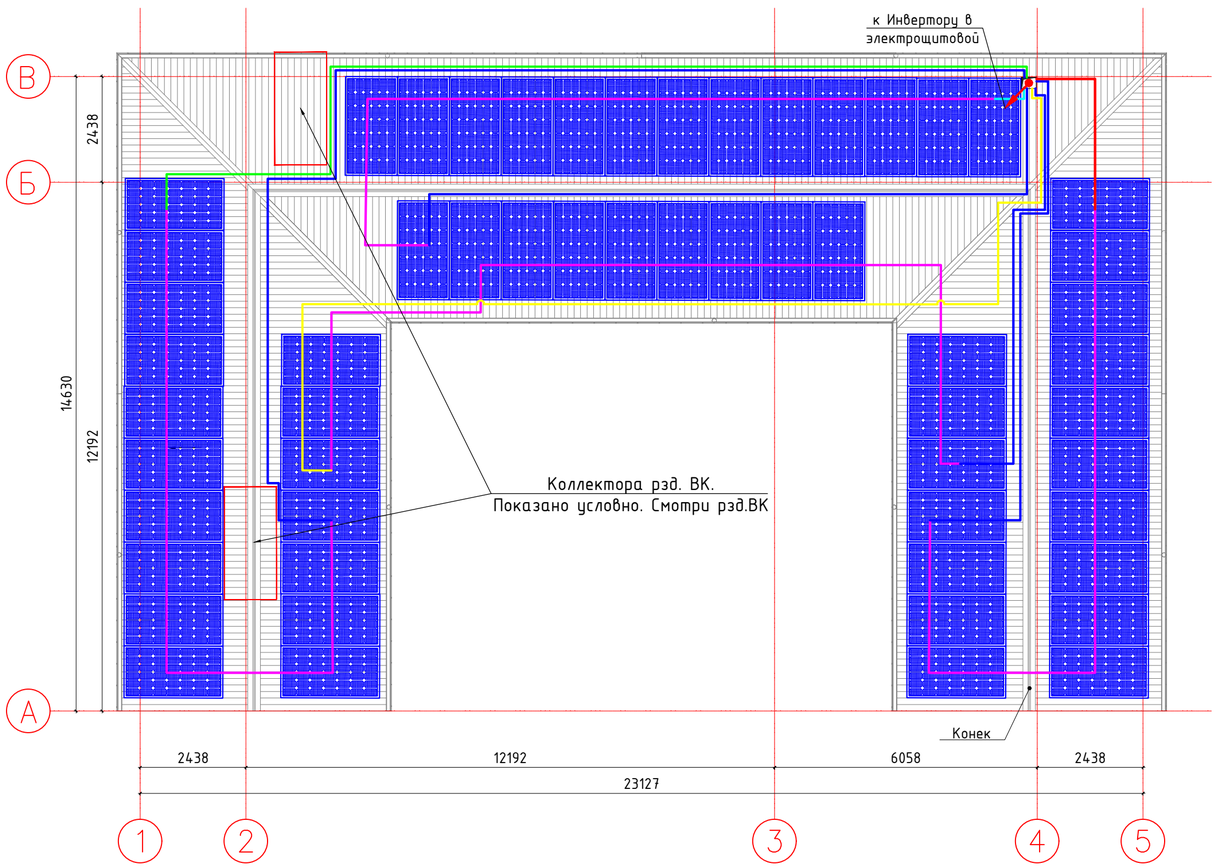

Примечание:

Проект ФЭС выполнен в ознокомительных целях, для определения места, количества и мощности ФЭС. Для расчета использовано оборудование SOLAR. При монтаже, данное оборудование может быть заменено на другие марки оборудования с аналогичными параметрами, прошедшими обязательную сертификацию "Узгосстандартом" в порядке, установленном законодательством Республики Узбекистан.

Схема интеграции оборудования ФЭС (щита управления, инвертор, панели) с ВРУ в зависимости от модели, разрабатывается поставщиком данного оборудования и согласовывается с заказчиком и проектной организацией. Способ установки панелей см. раздел АР.

R1	12.08.2026	Выпущено для рассмотрения		
Рев.	Дата	Назначение ревизии	Проверил	Утвердил

ЗАКАЗЧИК: UTG ГЕНЕРАЛЬНЫЙ ПОДРЯДЧИК: UET ПОДРЯДЧИК: PBG ГЕНЕРАЛЬНЫЙ ПРОЕКТИРОВЩИК: EAST WEST ENGINEERING

Изм.	Кол. уч.	Лист.	№док.	Подп.	Дата
ГИП		Схабицкий А.			08.2026
Нач.отд.		Гимранов Т.			08.2026
Исполн.		Пац В.			08.2026
Н. контр.		Схабицкий А.			08.2026

EWE0426-MGL1-ELE-054-DRW-800410-R1

«СТРОИТЕЛЬСТВО НОВЫХ НИТОК (УЧАСТКОВ) ГАЗОПРОВОДОВ «ГАЗЛИ – САРИМОЙ» И «АКЧАЛОК – ГАЗЛИ – НУКУС» ОБЩЕЙ ПРОТЯЖЕННОСТЬЮ НЕ МЕНЕЕ 275 КМ».

ГАЗОПРОВОД «ГАЗЛИ-САРИМОЙ» (54 КМ)

Стадия	Лист	Листов
РП	1	1

Место расположение солнечных панелей. План кровли

ООО "EAST-WEST Engineering" г. Ташкент 2026г.

Взам. инв. №

Подпись и дата

Инв.№ подл.

Формат А2