ЗАКАЗЧИК: **ГЕНЕРАЛЬНЫЙ ПОДРЯДЧИК** **ПОДРЯДЧИК** **ГЕНЕРАЛЬНЫЙ ПРОЕКТИРОВЩИК**

ОБЪЕКТ: «СТРОИТЕЛЬСТВО НОВЫХ НИТОК (УЧАСТКОВ) ГАЗОПРОВОДОВ «ГАЗЛИ - САРИМОЙ» И «АКЧАЛОК - ГАЗЛИ - НУКУС» ОБЩЕЙ ПРОТЯЖЕННОСТЬЮ НЕ МЕНЕЕ 275 КМ»
ГАЗОПРОВОД «ГАЗЛИ-САРИМОЙ» (54 КМ)

КОНТРАКТ №: EWEUZ-DW-26/04 от 16.04.2026г..

Ревизия документа: R1

Дата: 12.08.2026г.

ООО “EAST-WEST ENGINEERING”

ОПРОСНЫЙ ЛИСТ

Щит питания вентиляции и кондиционирования ЩСН. Опросный лист

EWE0426-MGL1-ELE-054-DSH-800414-R1

Согласовано

Взам. инв. №

Подпись и дата

Инв.№подл.

Изм.	Кол.уч	Лист	№док.	Подпись	Дата
ГИП		Схабицкий А.			08.2026
Нач. отд.		Гимранов Т.			08.2026
Исполн.		Пац В.			08.2026
Н. котр.		Схабицкий А.			08.2026

EWE0426-MGL1-ELE-054-DSH-800414-R1

ГАЗОПРОВОД «ГАЗЛИ-САРИМОЙ» (54 КМ)
ОПЕРАТОРНАЯ
Щит питания вентиляции и кондиционирования ЩСН. Опросный лист

Стадия	Лист	Листов
РП	1	5

ООО “EAST-WEST Engineering”
г. Ташкент 2026г

Лист регистрации изменений

Ревизия	Дата	Цель ревизии	Разработал	Проверил	Утвердил
R1	12.08.2026	Выпуск для проверки	Пац В.	Гимранов Т.	Схабицкий А.

Оглавление

1. **ССЫЛОЧНЫЕ ДОКУМЕНТЫ** **4**
2. **ОБЩИЕ ХАРАКТЕРИСТИКИ** **4**
3. **КОНСТРУКТОРСКАЯ ДОКУМЕНТАЦИЯКОНСТРКТОРСКАЯ ДОКУМЕНТАЦИЯ** **4**

1. ССЫЛОЧНЫЕ ДОКУМЕНТЫ

Документ	Название
КМК 2.01.01-94	Климатические и физико-геологические данные для проектирования
КМК 2.01.03-96	Строительство в сейсмических районах
ПУЭ РУз	Правила устройства электроустановок

2. ОБЩИЕ ХАРАКТЕРИСТИКИ


1.	Номинальное рабочее напряжение	400 В
2.	Номинальная частота	50 Гц
3.	Система заземления нейтрали	TN-S
4.	Номинальное напряжение цепей управления и сигнализации	~ 230 В
5.	Номинальное напряжение изоляции	660 В
6.	Конструктив	Навесной, металлический, двери непрозрачные с замком
7.	Степень защиты	IP 44
8.	Комплектующие	Schneider Electric, Siemens, ABB (или аналог)
9.	Ввод кабелей (питающие /отходящие линии)	Снизу/Сверху
10.	Состав шкафа	В соответствии с однолинейной схемой лист 5
11.	Обозначение шкафа (табличка на двери)	**ЩСН**

Выполнить таблички возле выключателей в соответствии с графой „Наименование механизма по плану” (чертёж, листы 5).

3. КОНСТРУКТОРСКАЯ ДОКУМЕНТАЦИЯ

Конструкторская документация, предоставляемая поставщиком, должна включать:

- Техническое описание системы
- Однолинейную электрическую схему
- Чертеж общего вида, габаритные, установочные и присоединительные размеры;
- Массу;
- Климатические условия применения;
- Сертификат соответствия сейсмическим условиям площадки;
- Критические требования поставщика;
- Значение максимальной рассеиваемой тепловой мощности;
- Схему подключения внешних цепей, с указанием наименований сигналов по каждой цепи;
- Вид системы заземления нейтрали

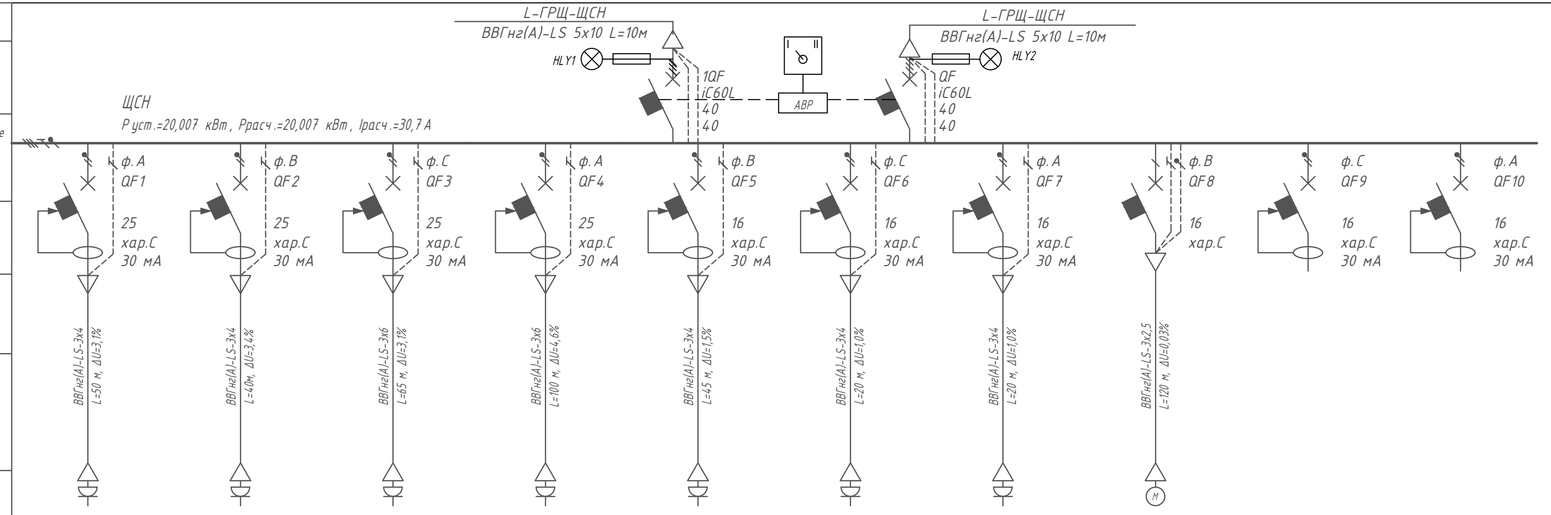

Данные питающей сети										
Шинопровод, распределительное устройство	Обозначение, тип, Iном.А расцепитель или плавкая вставка, А									
	Тип, напряжение, сечение (шинопровод), расчетный ток, А устан. мощность, кВт									
Аппарат отход. линии	Обозначение, тип, Iном., А расцепитель или плавкая вставка, А									
Пусковой аппарат	Тип, Iном., А, нагрев. элемент теплового реле уставка, А									
Кабельная линия										
Электроприемник	Условное обозначение по плану									
	Номер группы	№1	№2	№3	№4	№5	№6	№7	№8		
	Маркировка кабеля	L-ЩСН-ЭК10-12	L-ЩСН-ЭК7-9	L-ЩСН-ЭК4-6	L-ЩСН-ЭК1-3	L-1/ЩСН-К5-К6	L-1/ЩСН-К3-К4	L-1/ЩСН-К1-К2	L-1/ЩСН-В1-В5		
	Руст., кВт	3,0	4,5	3,5	3,0	1,6	2,4	2,0	0,07		
	Ррасч., кВт	3,0	4,5	3,5	3,0	1,6	2,4	2,0	0,07		
	Iном, А	13,77	20,7	20,66	13,77	7,35	11,02	9,2	0,30		
	Iпуск, А	13,77	20,7	20,66	13,77	7,35	11,02	9,2	0,30		
	Номер помещения	Помещение №1, 3, 4	Помещение №5, 6	Помещение №7, 8, 9	Помещение №11, 12, 13	Помещение №1, 3	Помещение №5	Помещение №6, 9	Помещение №7, 8, 9, 12, 13		
	Назначение	Конвектор ЭК 12, ЭК 11, ЭК 10,	Конвектор ЭК 7, ЭК 8, ЭК 9	Конвектор ЭК 4, ЭК 5, ЭК 6	Конвектор ЭК 1, ЭК 2, ЭК 3	Сплит-система К 5, К 6	Сплит-система К 3, К 4	Сплит-система К 1, К 2	Канальный вентилятор В 1, В 2, В 3, В 4, В 5	РЕЗЕРВ	РЕЗЕРВ

ф.А – распределение потребителей по фазам
QF4 – номер коммутационного аппарата
16 – номинальный ток или уставка расцепителя защиты от перегрузки
хар.С – защитная характеристика автоматического выключателя
30 мА – уставка расцепителя защиты от токов утечки (если устанавливается)

Взам. инв. №
Подпись и дата
Инв.№ подл.

Изм.	Кол. уч.	Лист	№ док.	Подп.	Дата	EWE0426-MGL1-ELE-054-DSH-800414-R1	Лист 5

Формат А4х3