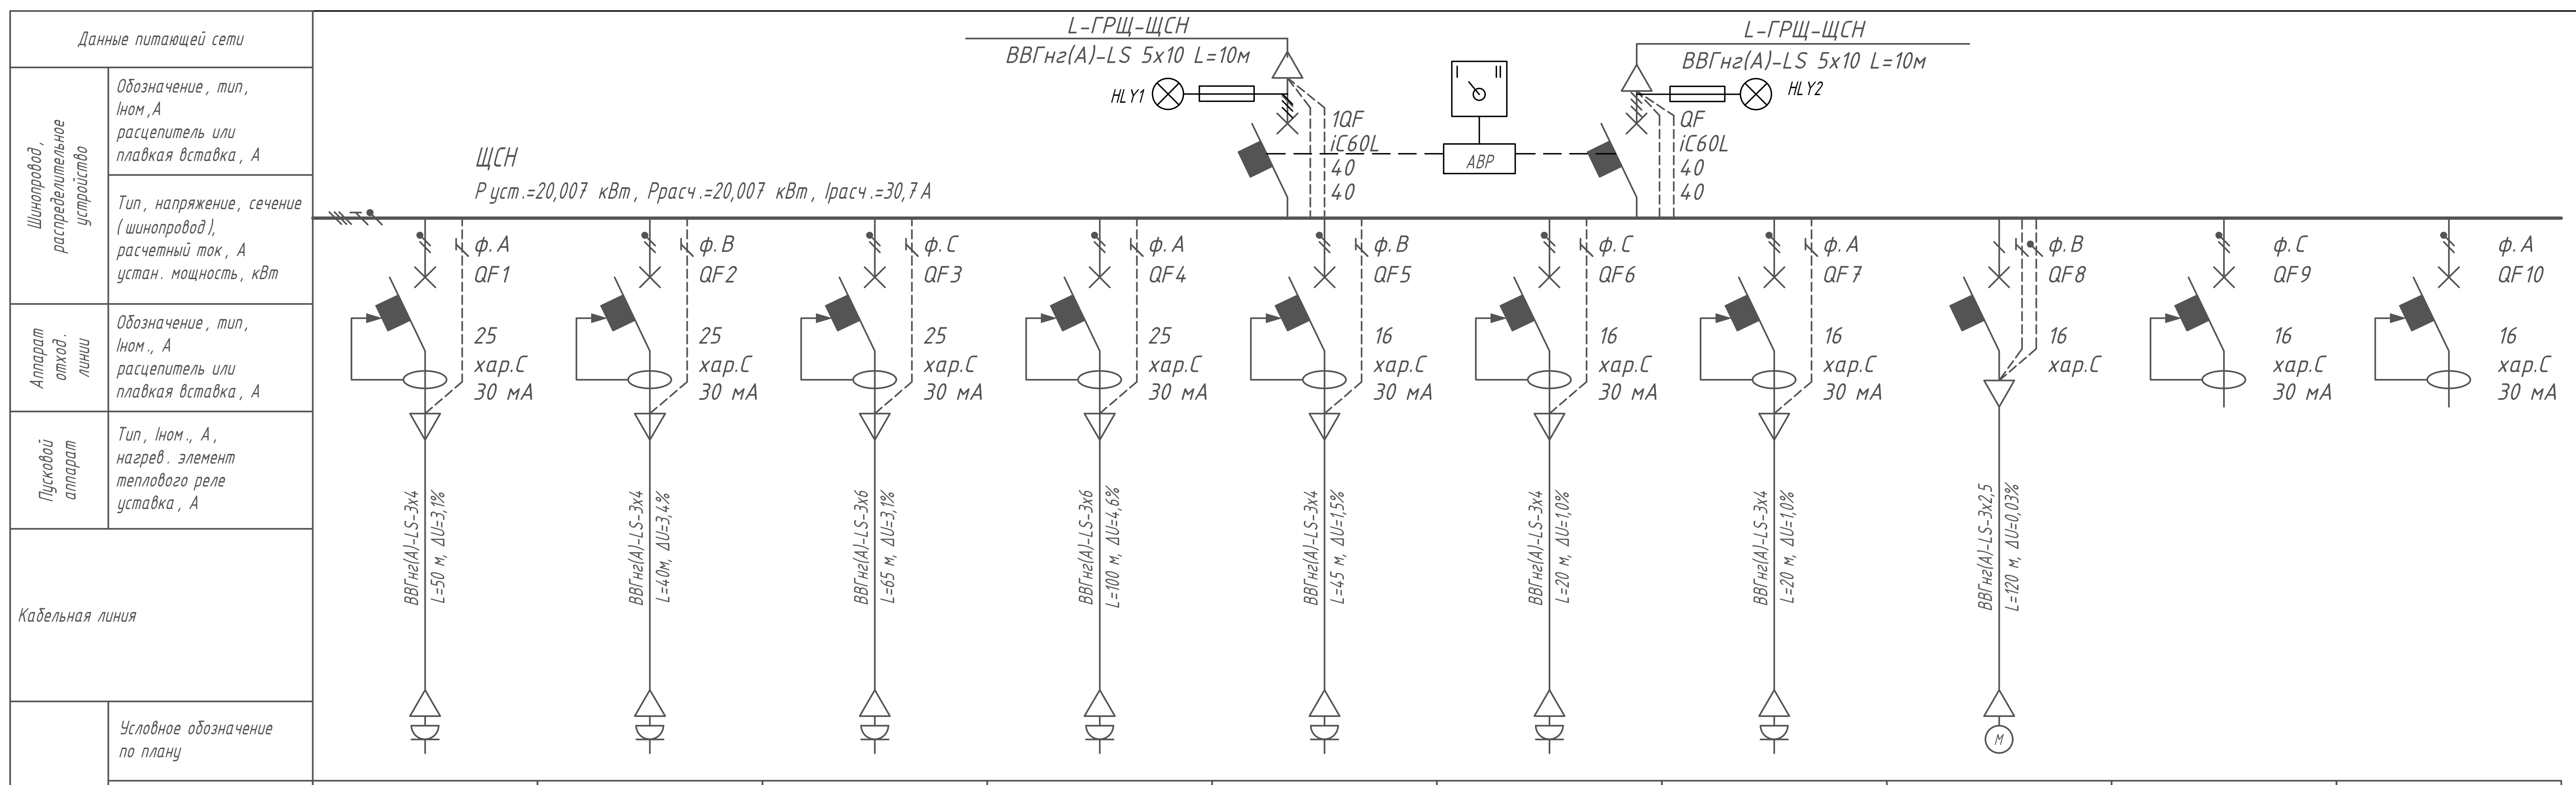

Электроприемник	Номер группы	№1	№2	№3	№4	№5	№6	№7	№8		
	Маркировка кабеля	L-ЩСН-ЭК10-12	L-ЩСН-ЭК7-9	L-ЩСН-ЭК4-6	L-ЩСН-ЭК1-3	L-1/ЩСН-К5-К6	L-1/ЩСН-К3-К4	L-1/ЩСН-К1-К2	L-1/ЩСН-В1-В5		
	Руст, кВт	3,0	4,5	3,5	3,0	1,6	2,4	2,0	0,07		
	Ррасч, кВт	3,0	4,5	3,5	3,0	1,6	2,4	2,0	0,07		
	Iном, А	13,77	20,7	20,66	13,77	7,35	11,02	9,2	0,30		
	Iпуск, А	13,77	20,7	20,66	13,77	7,35	11,02	9,2	0,30		
	Номер помещения	Помещение №1, 3, 4	Помещение №5, 6	Помещение №7, 8, 9	Помещение №11, 12, 13	Помещение №1, 3	Помещение №5	Помещение №6, 9	Помещение №7, 8, 9, 12, 13		
	Назначение	Конвектор ЭК 12, ЭК 11, ЭК 10,	Конвектор ЭК 7, ЭК 8, ЭК 9	Конвектор ЭК 4, ЭК 5, ЭК 6	Конвектор ЭК 1, ЭК 2, ЭК 3	Сплит-система К 5, К 6	Сплит-система К 3, К 4	Сплит-система К 1, К 2	Канальный вентилятор В 1, В 2, В 3, В 4, В 5	РЕЗЕРВ	РЕЗЕРВ

ф.А – распределение потребителей по фазам
QF4 – номер коммутационного аппарата
16 – номинальный ток или уставка расцепителя защиты от перегрузки
хар.С – защитная характеристика автоматического выключателя
30 мА – уставка расцепителя защиты от токов утечки (если устанавливается)

Взам. инв. №
Подпись и дата
Инв.№ подл.

Рев.	Дата	Назначение ревизии	Проверил	Утвердил
R1	12.08.2026	Выпущено для рассмотрения		

ЗАКАЗЧИК: UTG UZTRANSGAZ
ГЕНЕРАЛЬНЫЙ ПОДРЯДЧИК: UET UZBEKENERGOTAMIR
ПОДРЯДЧИК: PBG Pro Build Generation
ГЕНЕРАЛЬНЫЙ ПРОЕКТИРОВЩИК: EAST WEST ENGINEERING

EWE0426-MGL1-ELE-054-SCM-800407-R1

«СТРОИТЕЛЬСТВО НОВЫХ НИТОК (УЧАСТКОВ) ГАЗОПРОВОДОВ «ГАЗЛИ - САРИМОЙ» И «АКЧАЛОК - ГАЗЛИ - НУКУС» ОБЩЕЙ ПРОТЯЖЕННОСТЬЮ НЕ МЕНЕЕ 275 КМ».

ГАЗОПРОВОД «ГАЗЛИ-САРИМОЙ» (54 КМ)
ОПЕРАТОРНАЯ

Изм.	Кол. уч.	Лист.	№док.	Подп.	Дата
ГИП		Схабицкий А.			08.2026
Нач.отд.		Гимранов Т.			08.2026
Исполн.		Пац В.			08.2026
Н. контр.		Схабицкий А.			08.2026

Стадия	Лист	Листов
РП	1	1

Щит питания вентиляции и кондиционирования ЩСН. Схема электрическая однолинейная

ООО "EAST-WEST Engineering"
г. Ташкент 2026г.

Формат А4x4