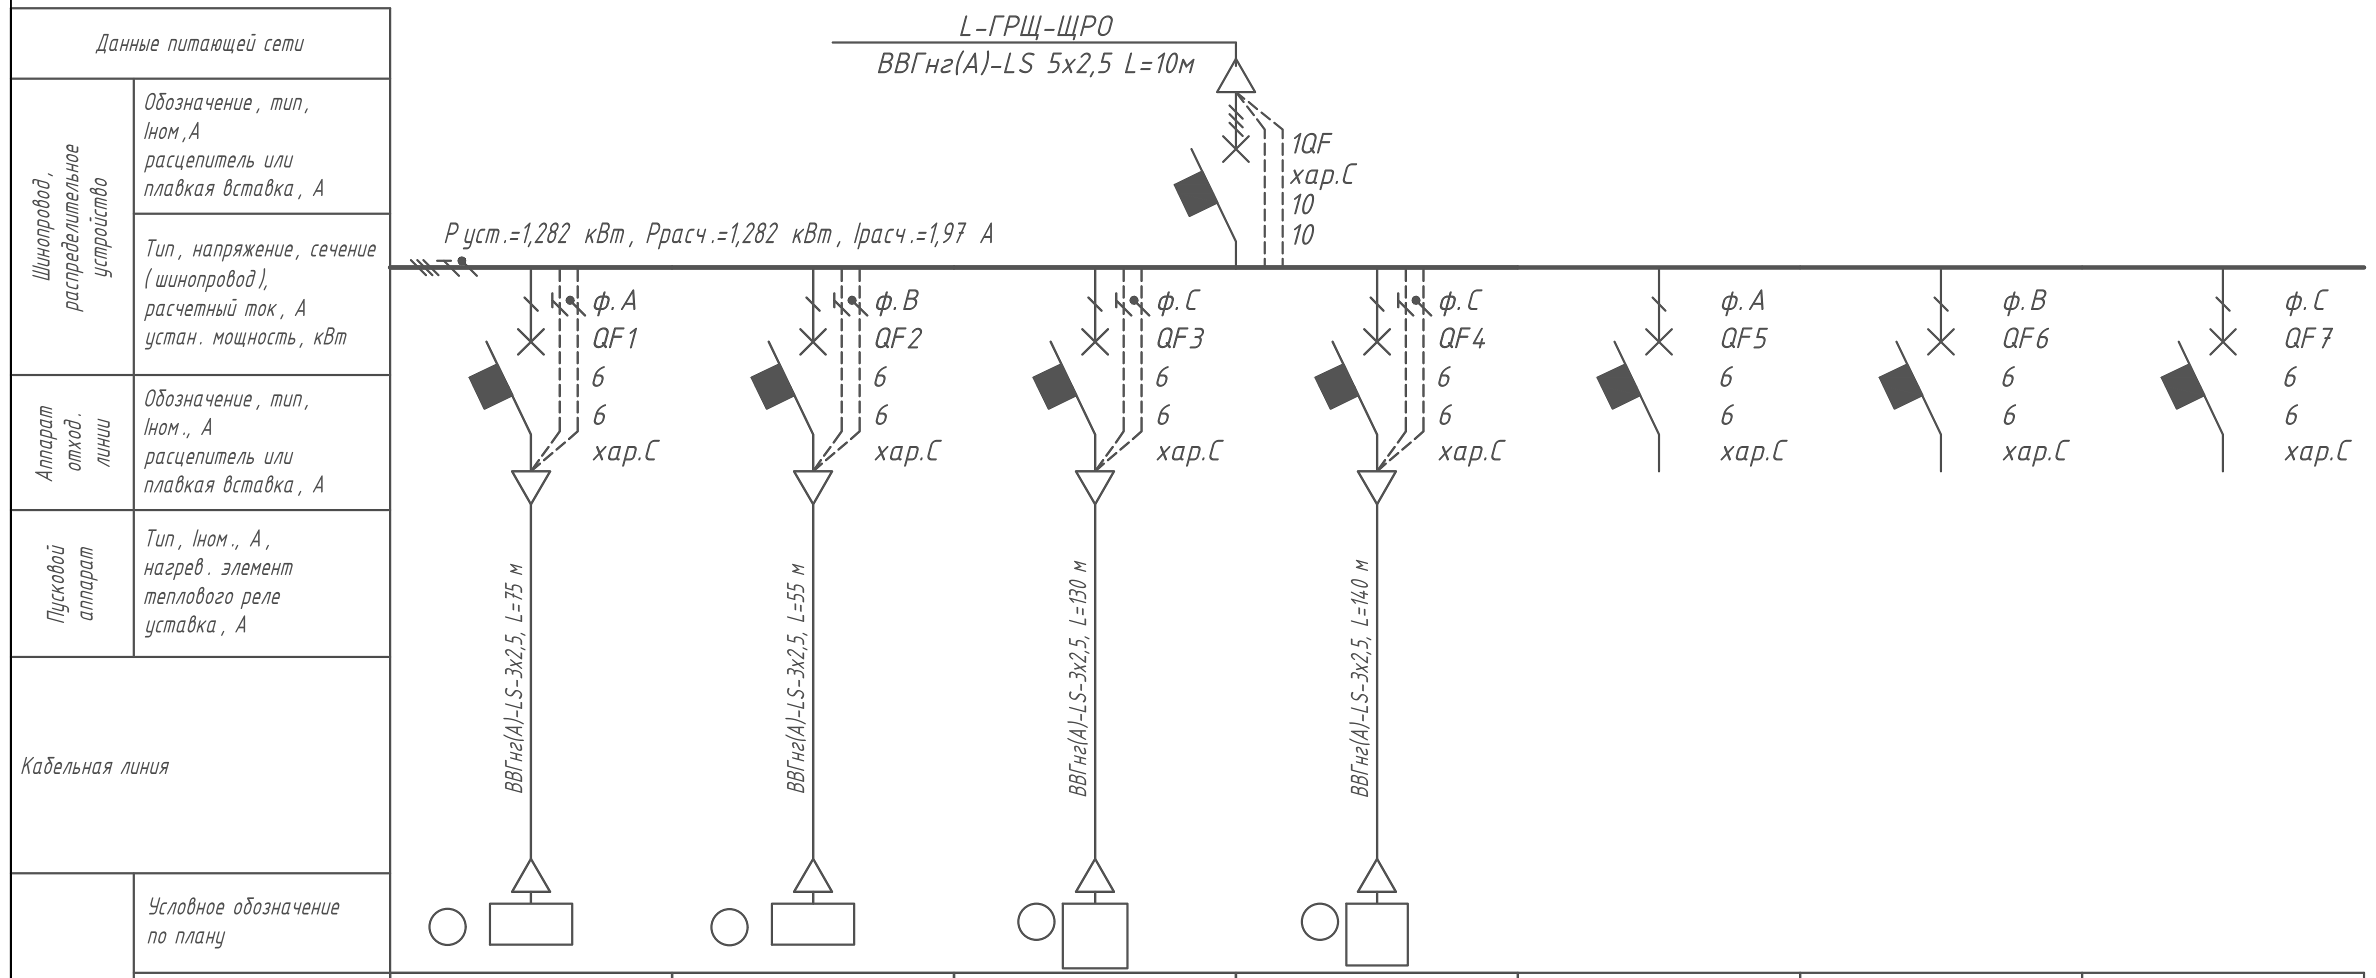
Данные питающей сети
Шинопровод, распределительное устройство
Обозначение, тип, Iном,А расцепитель или плавкая вставка, А
Тип, напряжение, сечение (шинопровод), расчетный ток, А устан. мощность, кВт
Аппарат отход. линии
Обозначение, тип, Iном., А расцепитель или плавкая вставка, А
Пусковой аппарат
Тип, Iном., А, нагрев. элемент теплового реле уставка, А
Кабельная линия
Условное обозначение по плану
L-ГРЩ-ЩРО
ВВГнг(А)-LS 5x2,5 L=10м
1QF
хар.С
10
10
Р уст.=1,282 кВт, Ррасч.=1,282 кВт, Iрасч.=1,97 А
ф.А
QF1
6
6
хар.С
ф.В
QF2
6
6
хар.С
ф.С
QF3
6
6
хар.С
ф.С
QF4
6
6
хар.С
ф.А
QF5
6
6
хар.С
ф.В
QF6
6
6
хар.С
ф.С
QF7
6
6
хар.С
ВВГнг(А)-LS-3x2,5, L=75 м
ВВГнг(А)-LS-3x2,5, L=55 м
ВВГнг(А)-LS-3x2,5, L=130 м
ВВГнг(А)-LS-3x2,5, L=140 м

Электроприемник							
Номер группы	гр.№1	гр.№2	гр.№3	гр.№4			
Маркировка кабеля	ЩРО-ГР1	ЩРО-ГР2	ЩРО-ГР3	ЩРО-ГР4			
Руст, кВт	0,187	0,214	0,563	0,318			
Ррасч, кВт	0,187	0,214	0,563	0,318			
Iном, А	0,9	1,0	2,6	1,5			
Iпуск, А	0,9	1,0	2,6	1,5			
Номер помещения	Помещения №1,2,3	Помещения №4,5	Помещения №6,7,8	Помещения №9,10,11,12,13			
Назначение	Рабочее осещение	Рабочее осещение	Рабочее осещение	Рабочее осещение	РЕЗЕРВ	РЕЗЕРВ	РЕЗЕРВ

ф.А – распределение потребителей по фазам
QF4 – номер коммутационного аппарата
16 – номинальный ток или уставка расцепителя защиты от перегрузки
хар.С – защитная характеристика автоматического выключателя
30 мА – уставка расцепителя защиты от токов утечки (если устанавливается)

Взам. инв. №
Подпись и дата
Инв.№ подл.

Рев.	Дата	Назначение ревизии	Проверил	Утвердил
R1	12.08.2026	Выпущено для рассмотрения		

ЗАКАЗЧИК: UTG UZTRANSGAZ
ГЕНЕРАЛЬНЫЙ ПОДРЯДЧИК: UET UZBEKENERGOTAMIR
ПОДРЯДЧИК: PBG Pro Build Generation
ГЕНЕРАЛЬНЫЙ ПРОЕКТИРОВЩИК: EAST WEST ENGINEERING

EWE0426-MGL1-ELE-054-SCM-800408-R1

«СТРОИТЕЛЬСТВО НОВЫХ НИТОК (УЧАСТКОВ) ГАЗОПРОВОДОВ «ГАЗЛИ – САРИМОЙ» И «АКЧАЛОК – ГАЗЛИ – НУКУС» ОБЩЕЙ ПРОТЯЖЕННОСТЬЮ НЕ МЕНЕЕ 275 КМ».

Изм.	Кол. уч.	Лист.	№док.	Подп.	Дата
ГИП		Схабицкий А.			08.2026
Нач.отд.		Гимранов Т.			08.2026
Исполн.		Пац В.			08.2026
Н. контр.		Схабицкий А.			08.2026

ГАЗОПРОВОД «ГАЗЛИ-САРИМОЙ» (54 КМ)
ОПЕРАТОРНАЯ

Стадия	Лист	Листов
РП	1	1

Щит рабочего освещения ЩРО. Схема электрическая однолинейная

EAST WEST ENGINEERING
ООО "EAST-WEST Engineering"
г. Ташкент 2026г.

Формат А4x3