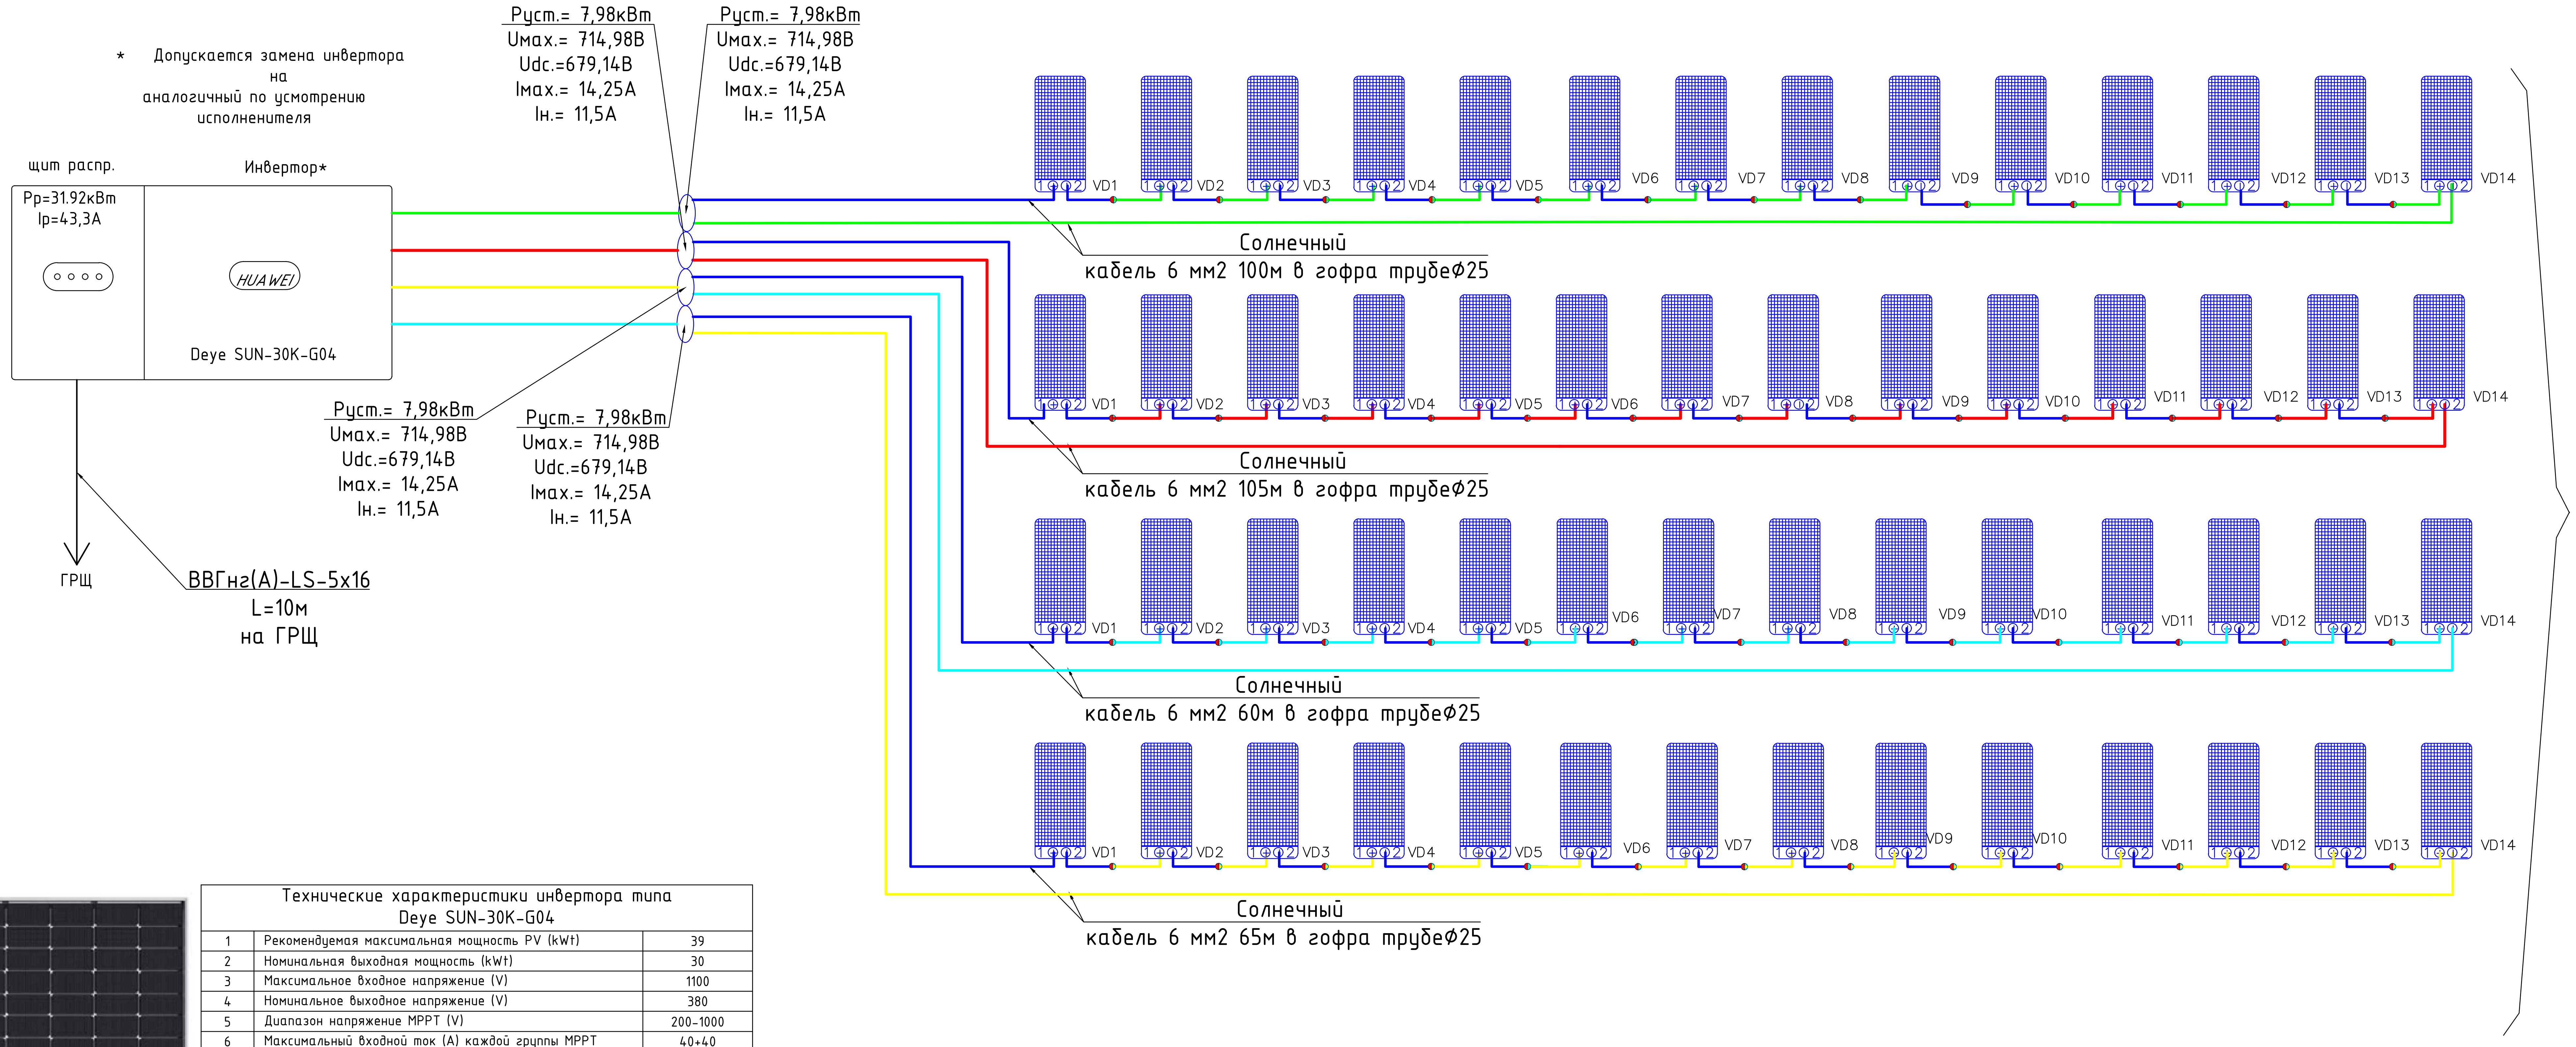
* Допускается замена инвертора на аналогичный по усмотрению исполнителя
щит распр.
Pp=31.92кВт
Ip=43,3А
Инвертор*
HUAWEI
Deye SUN-30K-G04
ГРЩ
ВВГнг(А)-LS-5х16
L=10м
на ГРЩ
Pуст.= 7,98кВт
Umax.= 714,98В
Udc.=679,14В
Imax.= 14,25А
Iн.= 11,5А
Pуст.= 7,98кВт
Umax.= 714,98В
Udc.=679,14В
Imax.= 14,25А
Iн.= 11,5А
Pуст.= 7,98кВт
Umax.= 714,98В
Udc.=679,14В
Imax.= 14,25А
Iн.= 11,5А
Pуст.= 7,98кВт
Umax.= 714,98В
Udc.=679,14В
Imax.= 14,25А
Iн.= 11,5А
VD1 VD2 VD3 VD4 VD5 VD6 VD7 VD8 VD9 VD10 VD11 VD12 VD13 VD14
Солнечный кабель 6 мм2 100м в гофра трубеФ25
Солнечный кабель 6 мм2 105м в гофра трубеФ25
Солнечный кабель 6 мм2 60м в гофра трубеФ25
Солнечный кабель 6 мм2 65м в гофра трубеФ25
Допускается замена панелей на аналогичный по усмотрению исполнителя

Технические характеристики инвертора типа Deye SUN-30K-G04		
1	Рекомендуемая максимальная мощность PV (kWt)	39
2	Номинальная выходная мощность (kWt)	30
3	Максимальное входное напряжение (V)	1100
4	Номинальное выходное напряжение (V)	380
5	Диапазон напряжение MPPT (V)	200-1000
6	Максимальный входной ток (A) каждой группы MPPT	40+40
7	Максимальный выходной ток (A)	53/50.72
8	Рабочее температура инвертора в пределе ^{0}C	от -25 до +60
9	Тип установки инвертора	Навесное

Общие параметры ПАНЕЛИ	
Наименование	JINKO_Tiger Neo N-type
модель	JKM570N-72HL4-BDV
Тип ячейки	182*91мм монокристалл
Количество ячеек	144 (6*24)
Размер компонента	2278*1134*30мм
Вес компонента	32,0 кг

Технические характеристики панели		
	STC	NOCT
Максимальное напряжение питания (Вмп)	42,29	39,65
Максимальный ток мощности (имп)	13,48	10,81
Напряжение разомкнутой цепи (Voc)	51,07	48,51
Ток короткого замыкания (Isc)	14.25	11.50
Пиковая мощность (Pmax)	570 Вт	

Технические данные: Солнечный кабель 6 мм^2

Тип кабеля: H1Z2Z2-K
Внешний Ø: прибл. 6,50 мм
Вес CU кг/100 м: 5,76 кг
Материал проводника: медь, луженая
Класс проводника: Класс 5
Материал изоляции проводника: сшитый полиолефиновый сополимер в соответствии с EN 50618.
Материал внешней оболочки: сшитый полиолефиновый сополимер EN 50618
Цвет оболочки: черный и красный
Номинальное напряжение [В] AC: Uo/U 1/1 кВ, макс. 1,2/1,2 кВ; постоянный ток: 1,5 кВ, макс. 1,8/1,8 кВ
Испытательное напряжение [В]: переменный ток: 6,5 кВ, постоянный ток: 15 кВ (5 мин).
Сопротивление изоляции: > 750 МОм х км при 20°C
наименьший фиксированный радиус изгиба [xd]: 5 x d
наименьший радиус изгиба в движении [xd]: 15 x d
рабочая темп. фиксированный мин./макс. [C]: от -40 °C до +90 °C
температура на проводнике: макс. 125°C
поведение при возгорании: IEC EN 60332-1-2
Стандарты EN 50618 / CPR EN13501-6

Диаграмма деталей струны

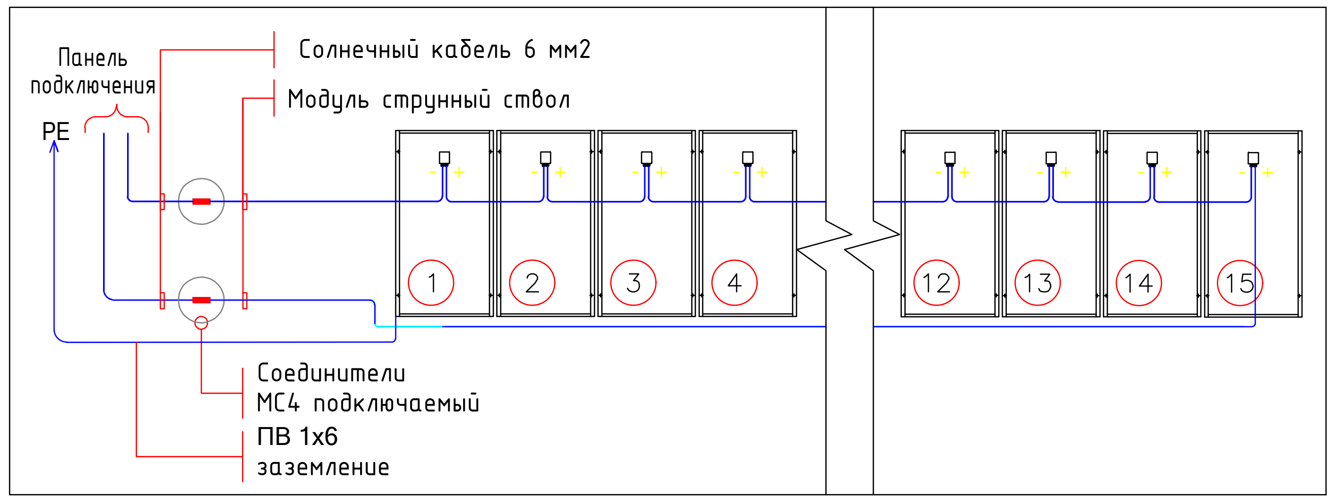

Примечание:

Проект ФЭС выполнен в ознокомительных целях, для определения места, количества и мощности ФЭС. Для расчета использовано оборудование SOLAR. При монтаже, данное оборудование может быть заменено на другие марки оборудования с аналогичными параметрами, прошедшими обязательную сертификацию "Узгосстандартом" в порядке, установленном законодательством Республики Узбекистан.

Схема интеграции оборудования ФЭС (щита управления, инвертор, панели) с ГРЩ в зависимости от модели, разрабатывается поставщиком данного оборудования и согласовывается с заказчиком и проектной организацией.

Рев.	Дата	Назначение ревизии	Проверил	Утвердил
R1	12.08.2026	Выпущено для рассмотрения		

ЗАКАЗЧИК: UTG UZTRANSGAZ
ГЕНЕРАЛЬНЫЙ ПОДРЯДЧИК: UET UZBEKENERGOTAMIR
ПОДРЯДЧИК: PBG Pro Build Generation
ГЕНЕРАЛЬНЫЙ ПРОЕКТИРОВЩИК: EAST WEST ENGINEERING

EWE0426-MGL1-ELE-054-SCM-800409-R1

«СТРОИТЕЛЬСТВО НОВЫХ НИТОК (УЧАСТКОВ) ГАЗОПРОВОДОВ «ГАЗЛИ - САРИМОЙ» И «АКЧАЛОК - ГАЗЛИ - НУКУС» ОБЩЕЙ ПРОТЯЖЕННОСТЬЮ НЕ МЕНЕЕ 275 КМ».

Изм.	Кол. уч.	Лист.	№док.	Подп.	Дата
ГИП		Схабицкий А.			08.2026
Нач.отд.		Гимранов Т.			08.2026
Исполн.		Пац В.			08.2026
Н. контр.		Схабицкий А.			08.2026

ГАЗОПРОВОД «ГАЗЛИ-САРИМОЙ» (54 КМ)

Стадия	Лист	Листов
РП	1	1

Принципиальная схема соединенной с сетью ФЭС. Технические характеристики оборудования ФЭС

ООО "EAST-WEST Engineering"
г. Ташкент 2026г.

Формат А2

Взам. инв. №
Подпись и дата
Инв.№ подл.