Ведомость рабочих чертежей основного комплекта

№ п.п.	Наименование	Примечание
1	Общие данные EWE0426-MGL1-GLT-054-COM-800101	R1
2	Разбивочный план. М1:500 EWE0426-MGL1-GLT-054-DRW-800102	R1
3	План организации рельефа. М1:500 EWE0426-MGL1-GLT-054-DRW-800103	R1
4	План земляных масс. М1:500 EWE0426-MGL1-GLT-054-DRW-800104	R1
5	Сводный план сетей инженерно-технического обеспечения. М1:500 EWE0426-MGL1-GLT-054-DRW-800105	R1
6	План благоустройства территории. М1:500. EWE0426-MGL1-GLT-054-DRW-800106	R1
7	План подъездной автодороги ПК0+00.00-ПК5+86.32. М1:1000 EWE0426-MGL1-GLT-054-DRW-800107	R1
8	Продольный профиль ПК0+00.00-ПК5+86.32 EWE0426-MGL1-GLT-054-DRW-800108	R1
9	Рабочие поперечные профили ПК0+50.00-ПК5+50.00 EWE0426-MGL1-GLT-054-DRW-800109	R1
10	Типовые поперечные профили EWE0426-MGL1-GLT-054-DRW-800110	R1
11	Конструкция дорожной одежды EWE0426-MGL1-GLT-054-DRW-800111	R1
12	Металлическая водопропускная труба отверстием 0.53 м EWE0426-MGL1-GLT-054-DRW-800112	R1

Ведомость основных комплектов рабочих чертежей

Обозначение	Наименование	Примечание
EWE0426-MGL1-GLT	Генеральный план	
EWE0426-MGL1-SAR	Архитектурные решения	
EWE0426-MGL1-STR	Строительные конструкции	
EWE0426-MGL1-PRE	Технология производства	
EWE0426-MGL1-PIL	Линейная часть	
EWE0426-MGL1-SYS	Автоматизация технологии производства - КИП	
EWE0426-MGL1-ELE	Электротехническая часть	

Ведомость ссылочных и прилагаемых документов

Обозначение	Наименование	Примечание
	Ссылочные документы	
ГОСТ 10704-91	Трубы стальные электросварные прямошовные	
ГОСТ 6665-2023	Камни бетонные и железобетонные бортовые	
ГОСТ 8267-93	Щебень и гравий из плотных горных пород для строительных работ	
ГОСТ 25607-2009	Смеси щебеночно-гравийно-песчаные для покрытий и оснований автомобильных дорог и аэродромов	
ГОСТ 26633-2015	Бетоны тяжелые и мелкозернистые	
ГОСТ 23558-94	Смеси щебеночно-гравийно-песчаные и грунты, обработанные неорганическими вяжущими материалами, для дорожного и аэродромного строительства	
Серия 3.501.1-156, Выпуск 1	Укрепление русел конусов и откосов насыпи у малых и средних мостов и водопропускных труб	
	Прилагаемые документы	
EWE0426-MGL1-GLT-054-SCH-800113	Ведомость объемов строительных и монтажных работ	R1
EWE0426-MGL1-GLT-054-SCH-800114	Попикетная ведомость объемов земляных работ	R1

Технико-экономические показатели по генплану


№	Наименование показателей	Ед.изм.	Количество
1	Общая площадь территории в ограждении	га	1.0678
2	Площадь застройки	$м^2$	154.5
3	Площадь покрытия автодорог, тротуаров и площадок	$м^2$	10832.5
4	Площадь озеленения	$м^2$	-
5	Коэффициент использования территории	1	1
6	Длина подъездной автодороги	км	0.58


Общие указания:

Генеральный план объекта "Строительство узла замера газа на 114 км МГ "Газли-Саримай" Ду-1220 мм УП "Ургенчтрансгаз", разработан на основании технического задания, на материалах инженерно-геодезических изысканий, выполненных "CENTRAL GEO SURVEY ENGINEERING" MCHJ , в соответствии с технологической схемой производства с учётом подключения инженерных сетей, розы ветров, а также с соблюдением санитарных и противопожарных норм согласно требованиям, действующих в Республике Узбекистан.

- КМК 2.09.17-2021 Генеральные планы промышленных предприятий;
- ШНК 2.05.02-23 Автомобильные дороги;
- СНиП 2.05.07-91* Промышленный транспорт;
- ГОСТ 21.508-2020 Правила выполнения рабочей документации генеральных планов предприятий, сооружений и жилищно-гражданских объектов.

2. Вертикальная планировка разработана в соответствии с требованиями технологической и строительной частей проекта, а также в увязке с существующим рельефом.
3. Система высот-Балтийская.
4. Система координат - местная.
5. Проектируемая подъездная автомобильная дорога в соответствии с законом Республики Узбекистан № ЗРУ-117 "Об автомобильных дорогах" относится к подъездным автомобильным дорогам IV-в категории.

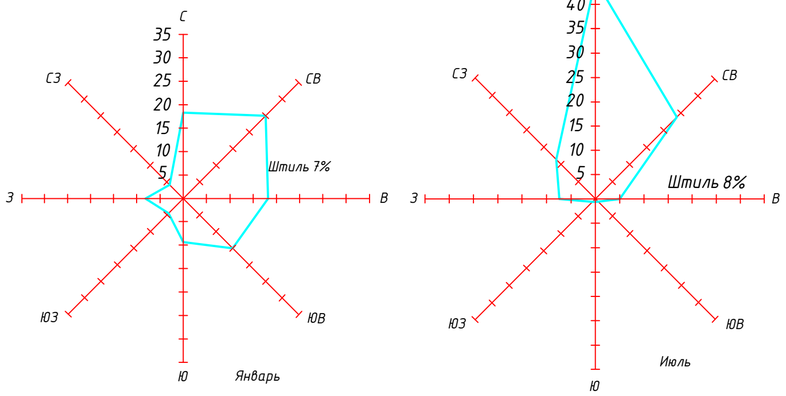

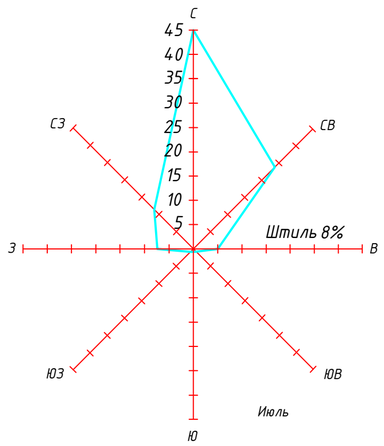

мет.ст.Джангелды

Месяц	С	СВ	В	ЮВ	Ю	ЮЗ	З	СЗ	Штиль
Январь	18	25	18	15	9	4	7	4	10
Июль	45	28	5	1	1	1	7	12	4

Рев.	Дата	Назначение ревизии	Проверил	Утвердил
R1	10.08.2026	Выпущено для рассмотрения		

ЗАКАЗЧИК: UTG VIETNAMGAS | ГЕНЕРАЛЬНЫЙ ПОДРЯДЧИК: UET UZBEKENERGOTAMIR | ПОДРЯДЧИК: PBG Pro Build Generation | ГЕНЕРАЛЬНЫЙ ПРОЕКТИРОВЩИК: EAST WEST ENGINEERING

EWE0426-MGL1-GLT-054-COM-800101-R1

«СТРОИТЕЛЬСТВО НОВЫХ НИТОК (УЧАСТКОВ) ГАЗОПРОВОДОВ «ГАЗЛИ – САРИМОЙ» И «АКЧАЛОК - ГАЗЛИ – НУКУС» ОБЩЕЙ ПРОТЯЖЕННОСТЬЮ НЕ МЕНЕЕ 275 КМ»

Изм.	Кол. уч.	Лист.	№док.	Подп.	Дата
ГИП		Схабицкий А.			08.2026
Нач.отд.		Нигманова Н.			08.2026
Исполн.		Горлова О.			08.2026
Н. контр.		Схабицкий А.			08.2026

ГАЗОПРОВОД «ГАЗЛИ-САРИМОЙ» (54 КМ)
Площадка УЗРГ.
Генеральный план и транспорт

Стадия	Лист	Листов
РД	1	14

Общие данные

ООО "EAST-WEST Engineering"
г. Ташкент 2026г.

Взам. инв. №

Подпись и дата

Инв.№ подл.

Формат А2