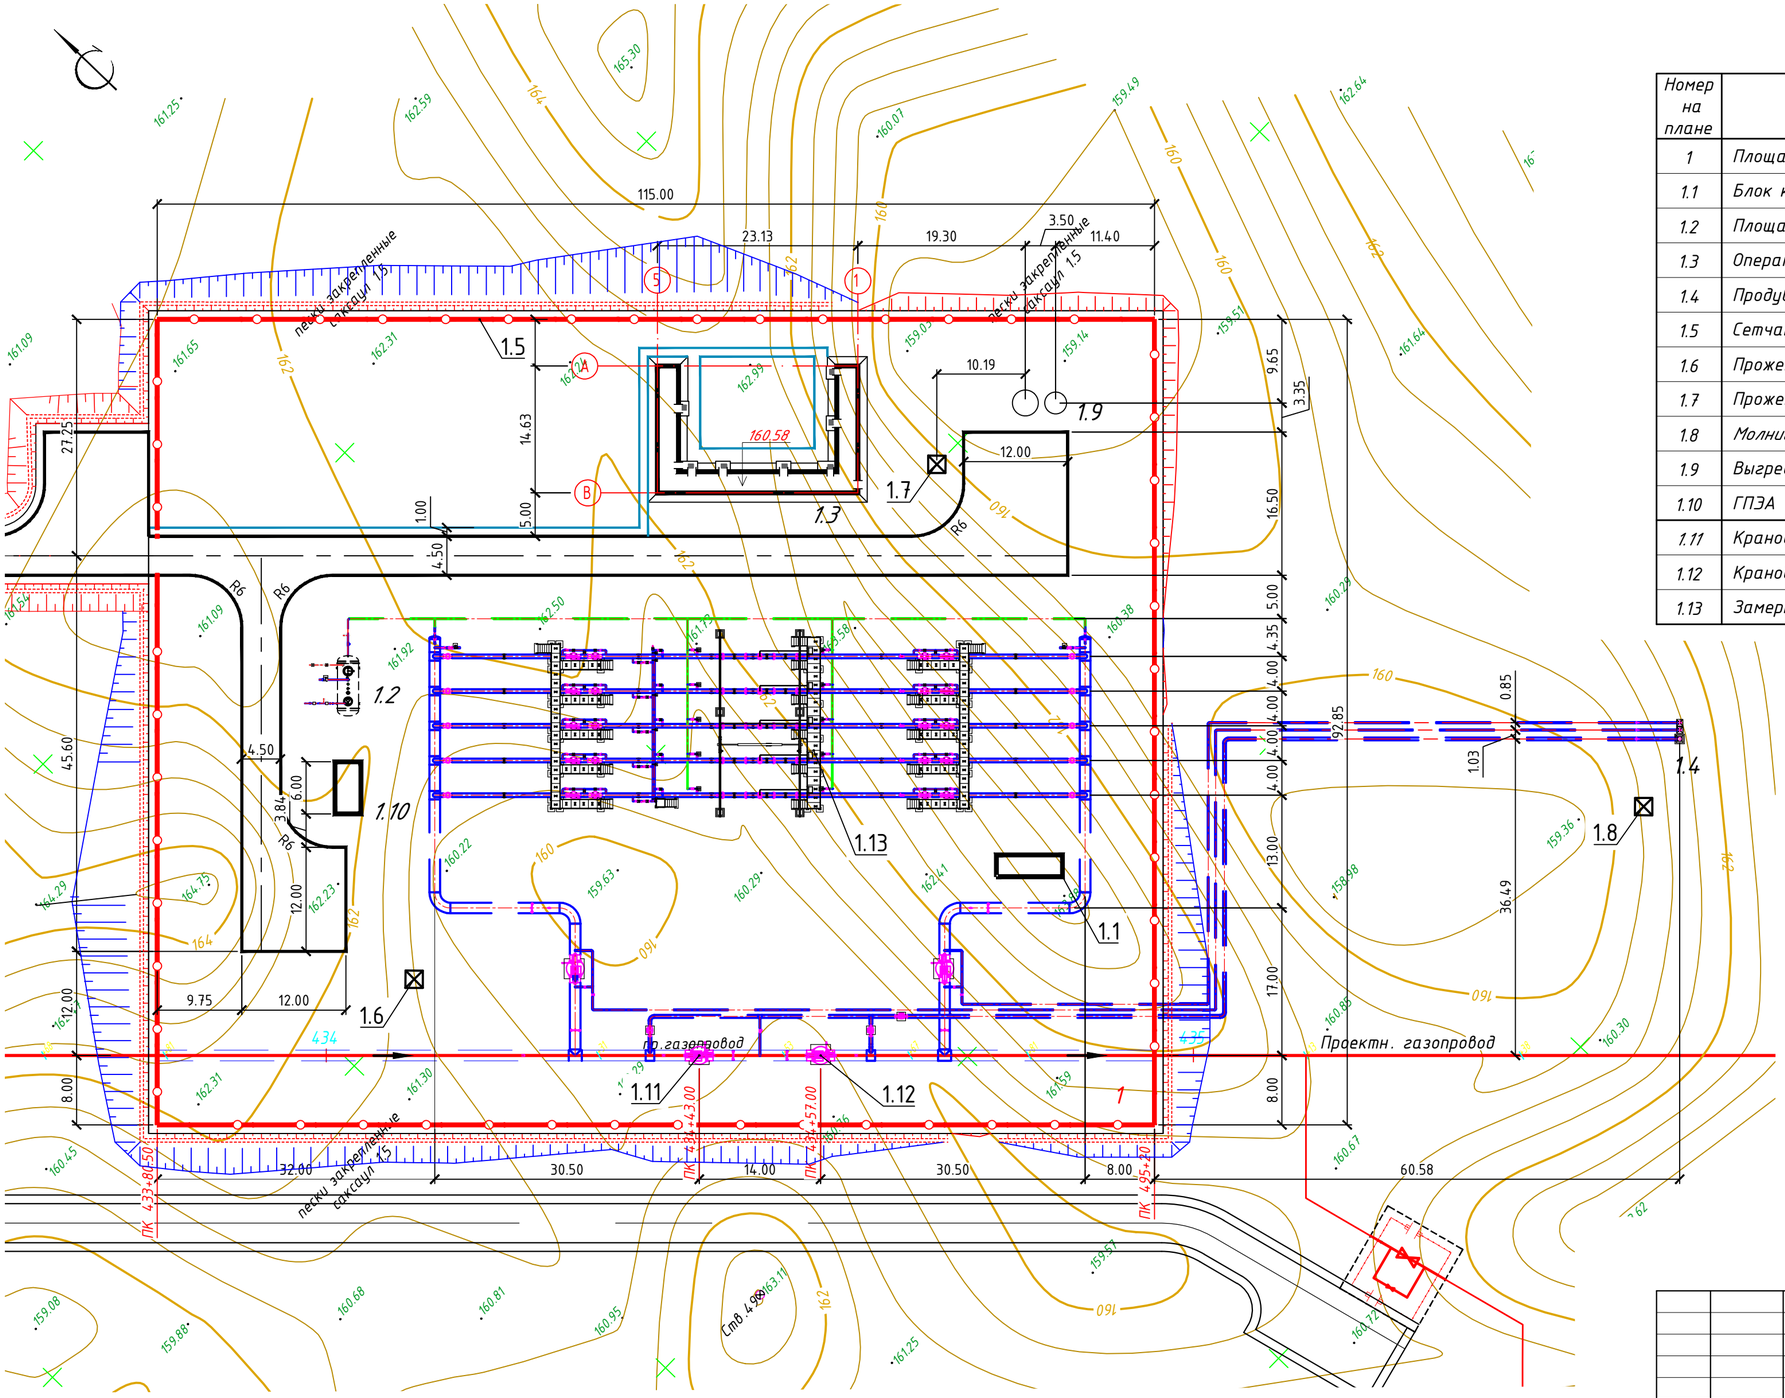


Экспликация зданий и сооружений

Номер на плане	Наименование	Примечание
1	Площадка УЗРГ	
1.1	Блок качества газа	
1.2	Площадка дренажной емкости V=25м3	
1.3	Операторная	
1.4	Продувочные свечи	
1.5	Сетчатое ограждение с воротами шир.4.5 м	
1.6	Прожекторная мачта ПМЖ-22.8	
1.7	Прожекторная мачта ПМЖ-22.8	
1.8	Молниеотвод МЖ-24.3	
1.9	Выгреб	
1.10	ГПЗА	
1.11	Крановый узел XV-D12-001	
1.12	Крановый узел XV-D12-002	
1.13	Замерный узел	

Условные обозначения

- Здания и сооружения
- Автодороги, подъезды
- Тротуар
- Ограждение
- Ворота
- 160.58 Отметка нуля
- Водоотводная канава
- Откосы насыпи
- Откосы выемки

Примечание:

1. Данный чертеж разработан на материалах инженерно-геодезических изысканий, выполненных "CENTRAL GEO SURVEY ENGINEERING" MCHJ.
2. Система координат - местная.
3. Система высот - Балтийская.
4. Площадка УЗРГ привязана линейно к пикетажу крановых узлов проектируемого МГ.
5. Размеры даны в метрах.

Рев.	Дата	Назначение ревизии	Проверил	Утвердил
R1	10.08.2026	Выпущено для рассмотрения		

ЗАКАЗЧИК: UTG | ГЕНЕРАЛЬНЫЙ ПОДРЯДЧИК: ЦЕТ | ПОДРЯДЧИК: PBG | ГЕНЕРАЛЬНЫЙ ПРОЕКТИРОВЩИК: EAST WEST ENGINEERING

EWE0426-MGL1-GLT-054-DRW-800102-R1

«СТРОИТЕЛЬСТВО НОВЫХ НИТОК (УЧАСТКОВ) ГАЗОПРОВОДОВ «ГАЗЛИ – САРИМОЙ» И «АКЧАЛОК – ГАЗЛИ – НУКУС» ОБЩЕЙ ПРОТЯЖЕННОСТЬЮ НЕ МЕНЕЕ 275 КМ»

Изм.	Кол. уч.	Лист.	№док.	Подп.	Дата
ГИП		Схабицкий А.			08.2026
Нач.отд.		Нигманова Н.			08.2026
Исполн.		Горлова О.			08.2026
Н. контр.		Схабицкий А.			08.2026

ГАЗОПРОВОД «ГАЗЛИ-САРИМОЙ» (54 КМ)
Площадка УЗРГ.
Генеральный план и транспорт.

Стадия	Лист	Листов
РД	1	1

Разбивочный план. М 1:500

ООО "EAST-WEST Engineering"
г. Ташкент 2026г.

Взам. инв. №
Подпись и дата
Инв.№ подл.

Формат А2