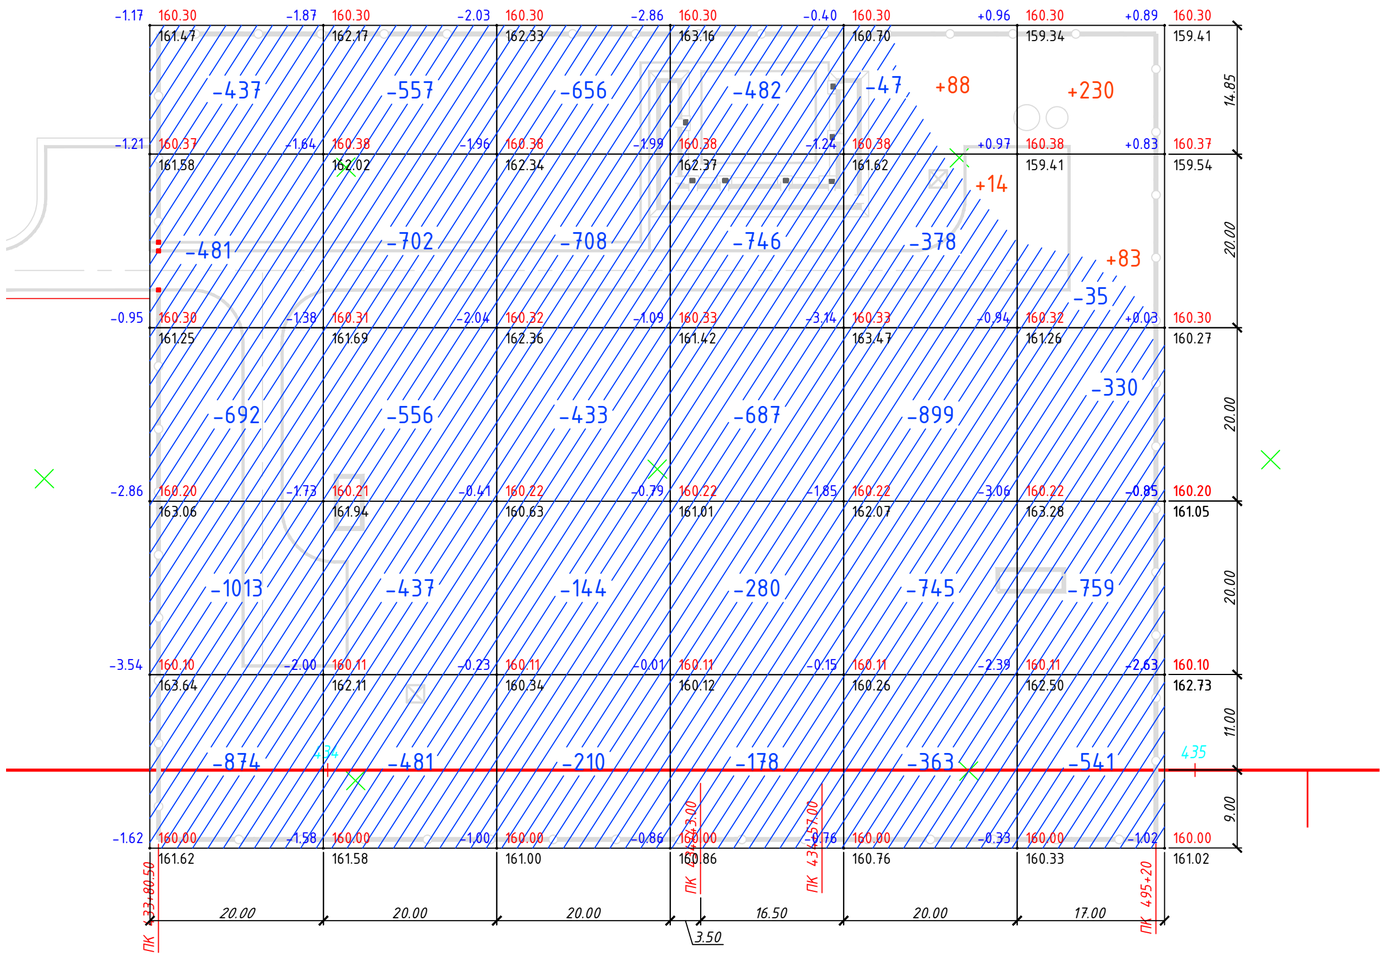


Итого,м3								
	Насыпь (+)	--	--	--	--	+102	+313	+415
	Выемка (-)	-3497	-2733	-2151	-2373	-2432	-1665	-14851

Общая площадь насыпи = 707 м2
Общая площадь выемки = 10391 м2
Общая площадь 0-области = 0 м2
Общая площадь картограммы = 11097 м2

Примечание:

1. Сетка картограммы привязана линейно к пикетажному положению кранов площадки.
2. Сетка квадратов объема земляных масс разбита на ячейки размерами 20х20 м.
3. Производство земляных работ вести в соответствии с строительным регламентом КР 02.01-23.
4. Данная картограмма рассчитана без учёта объёмов вытесненного грунта из под зданий, сооружений и подземных инженерных сетей.

Ведомость объемов земляных масс

Наименование грунта Ground specification	Количество, м³ Quantity, м³		Примечание Remark
	Насыпь (+) Embankment(+)	Выемка (-) Excavation(-)	
1. Грунт планировки территории	415	14851*	
2. Вытесненный грунт, в т.ч. при устройстве:		3765	
а) автодорожных покрытий		(2797.5)	
б) тротуаров		(34.5)	
в) щебеночного покрытия площадки		(933)	
3. Замена плодородного слоя грунта на участках насыпи	212		
4. Поправка на уплотнение (k=1.1)	63		
Всего пригодного грунта	690	18616	
5. Избыток пригодного грунта	17926		
6. Плодородный грунт, всего, в т.ч.:		2820	
а) используемый для озеленения территории			
б) избыток плодородного грунта	2820		
7. Итого перерабатываемого грунта	21436	21436	

* С учетом плодородного грунта.

Условные обозначения:

8,93 | 770,01 / 761,08 — рабочая отм. | проектная отм. / отм.сущ.рельефа

+294.00 — объем насыпи в м³

-874.00 — объем выемки в м³

Ограждение

Ворота

Проектируемые здания

Линия нулевых работ

Область выемки

Рев.	Дата	Назначение ревизии	Проверил	Утвердил
R1	10.08.2026	Выпущено для рассмотрения		

ЗАКАЗЧИК: UTG ЦЕНТРАЛЬНАЯ АЗИЯ | ГЕНЕРАЛЬНЫЙ ПОДРЯДЧИК: UET | ПОДРЯДЧИК: PBG Pro Build Generation | ГЕНЕРАЛЬНЫЙ ПРОЕКТИРОВЩИК: EAST WEST ENGINEERING

EWE0426-MGL1-GLT-054-DRW-800104-R1

«СТРОИТЕЛЬСТВО НОВЫХ НИТОК (УЧАСТКОВ) ГАЗОПРОВОДОВ «ГАЗЛИ – САРИМОЙ» И «АКЧАЛОК – ГАЗЛИ – НУКУС» ОБЩЕЙ ПРОТЯЖЕННОСТЬЮ НЕ МЕНЕЕ 275 КМ»

Изм.	Кол. уч.	Лист.	№док.	Подп.	Дата				
ГИП		Схабицкий А.			08.2026	ГАЗОПРОВОД «ГАЗЛИ-САРИМОЙ» (54 КМ) Площадка УЗРГ. Генеральный план и транспорт.	Стадия	Лист	Листов
Нач.отд.		Нигманова Н.			08.2026		РД	1	1
Исполн.		Горлова О.			08.2026				
Н. контр.		Схабицкий А.			08.2026	План земляных масс. М 1:500	ООО "EAST-WEST Engineering" г. Ташкент 2026г.		

Взам. инв. № | Подпись и дата | Инв.№ подл.

Формат А2