Взам. инв. №

Подпись и дата

Инв.№ подл.

Номер ИГЭ	Группа по разработке	Наименование грунта
ПРС		Почвы
1		Песок мелкий
4	1	Алевролиты
2	30б	Песчаники

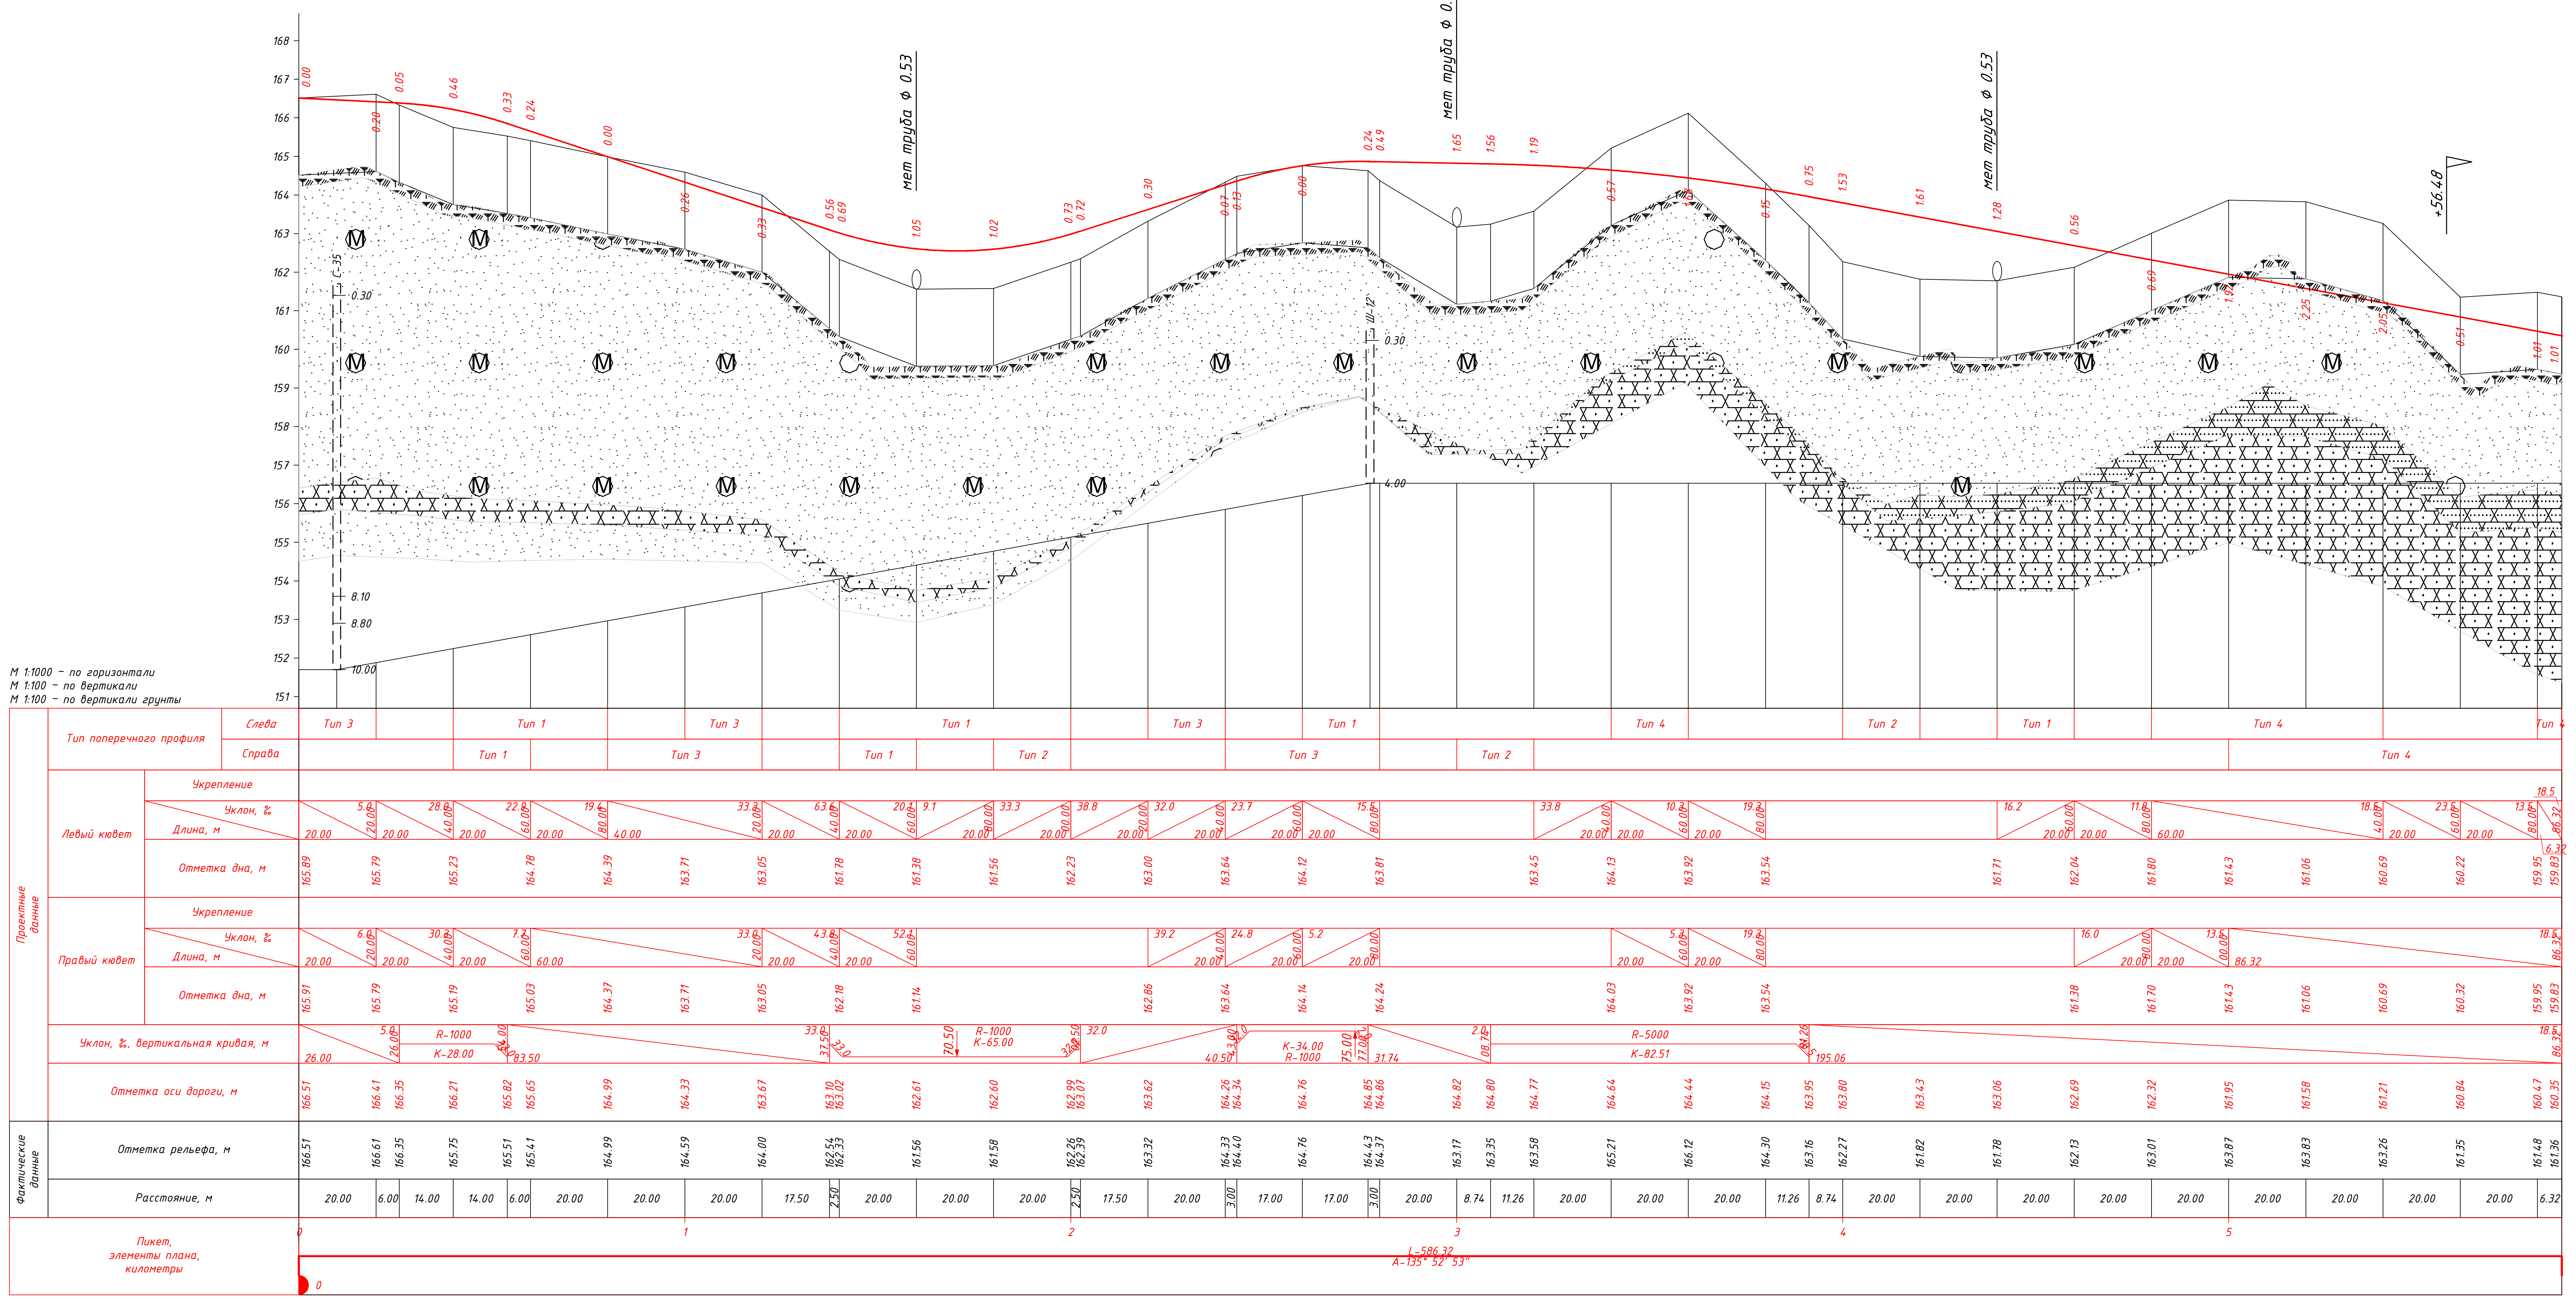

М 1:1000 – по горизонтали
М 1:100 – по вертикали
М 1:100 – по вертикали грунты

Условные обозначения:

- Линия поверхности дороги
- Линия поверхности земли
- 0,22 0,35 — Насыпи высотой 0,22м и 0,35м
- 80 / 56,4 — Участок дороги с уклоном 80‰ на протяжении 56,4 м
- 22,2 K-7,1T-3,5 R-30.0 У-13°29'11" 29,3 — Поворот дороги влево и характеристики угла поворота (длина кривой, тангенс, радиус, угол)
- 80,9 K-6,4 T-3,2 R-30.0 У-12°15'57" 87,3 — Поворот дороги вправо и характеристики угла поворота (длина кривой, тангенс, радиус, угол)
- +60 5 6 — Съезд с дороги влево и вправо в м после пикета +60
- 7 1 2 — Километры (7) и пикеты (1 и 2)
- ▨ П — Почвенно-растительный слой
- ▨ 1 — Песок мелкий с прослойками суглинка мощностью до 0,8 т. (ИГЭ-1)
- ▨ 2 — Песчаник низкой и средней прочности (ИГЭ-2)
- ▨ 4 — Алевролит низкой прочности (ИГЭ-4)
- ① — Номер инженерно-геологического элемента (ИГЭ)

Примечание:

1. Данный чертеж рассматривать совместно с чертежами "План подъездной автолдороги", "Поперечные профили", "Типовые поперечные профили", "Конструкция дорожной одежды".
2. Размеры даны в метрах.

Рев.	Дата	Назначение ревизии	Проверил	Утвердил
R1	10.08.2026	Выпущено для рассмотрения		

ЗАКАЗЧИК: UTG UZTRANSGAZ
ГЕНЕРАЛЬНЫЙ ПОДРЯДЧИК: UET UZBEKENERGOTAMIR
ПОДРЯДЧИК: PBG Pro Build Generation
ГЕНЕРАЛЬНЫЙ ПРОЕКТИРОВЩИК: EAST WEST ENGINEERING

EWE0426-MGL1-GLT-054-DRW-800108-R1

«СТРОИТЕЛЬСТВО НОВЫХ НИТОК (УЧАСТКОВ) ГАЗОПРОВОДОВ «ГАЗЛИ – САРИМОЙ» И «АКЧАЛОК – ГАЗЛИ – НУКУС» ОБЩЕЙ ПРОТЯЖЕННОСТЬЮ НЕ МЕНЕЕ 275 КМ»

Изм.	Кол. уч.	Лист.	№док.	Подп.	Дата
ГИП		Схабицкий А.			08.2026
Нач.отд.		Нигманова Н.			08.2026
Исполн.		Горлова О.			08.2026
Н. контр.		Схабицкий А.			08.2026

ГАЗОПРОВОД «ГАЗЛИ-САРИМОЙ» (54 КМ)
Площадка УЗРГ.
Генеральный план и транспорт.

Стадия	Лист	Листов
РД	1	1

Продольный профиль
ПК0+00.00-ПК5+86.32

EAST WEST ENGINEERING
ООО "EAST-WEST Engineering"
г. Ташкент 2026г.

Формат А3х4