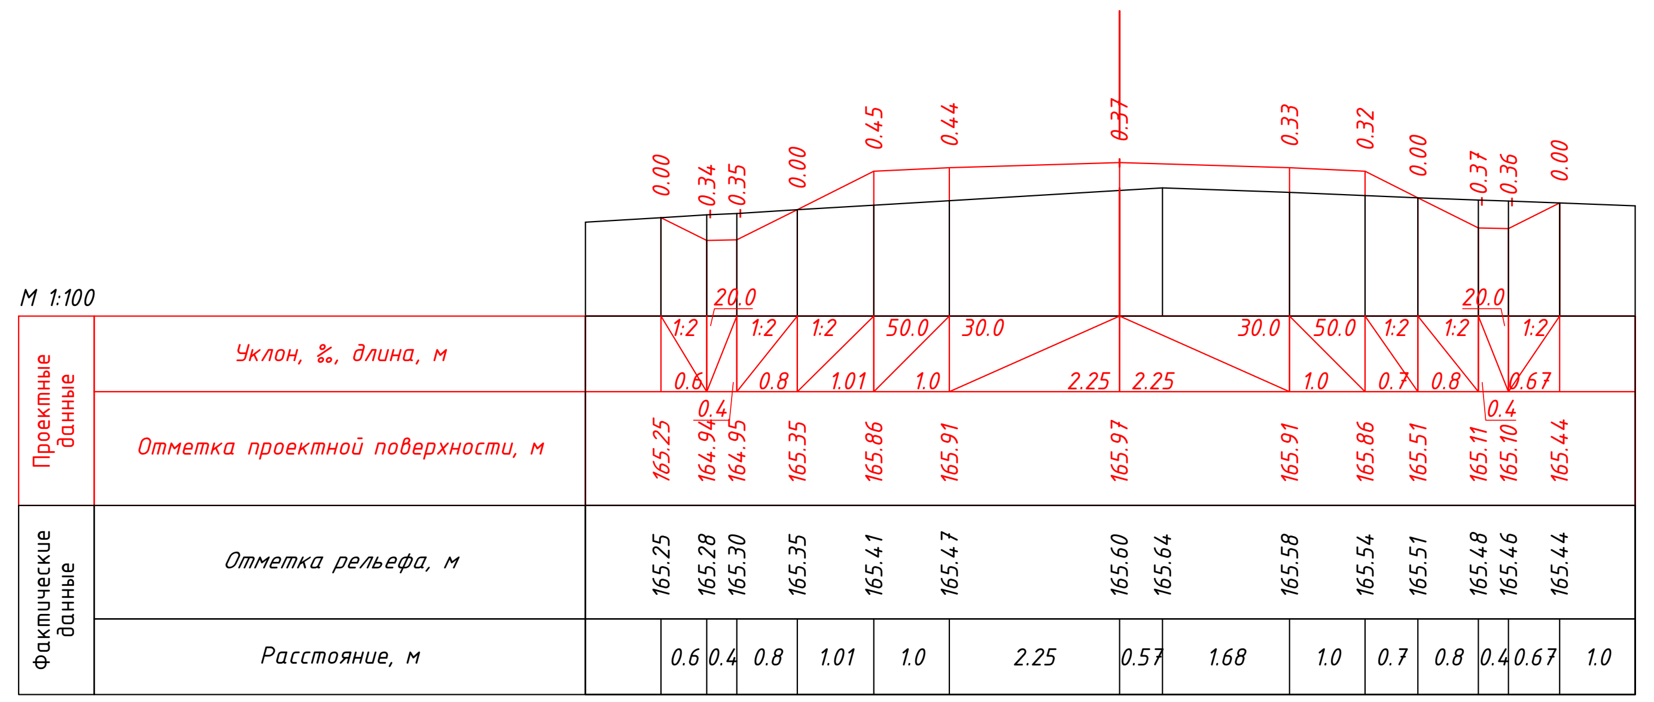

ПК 0+50.00

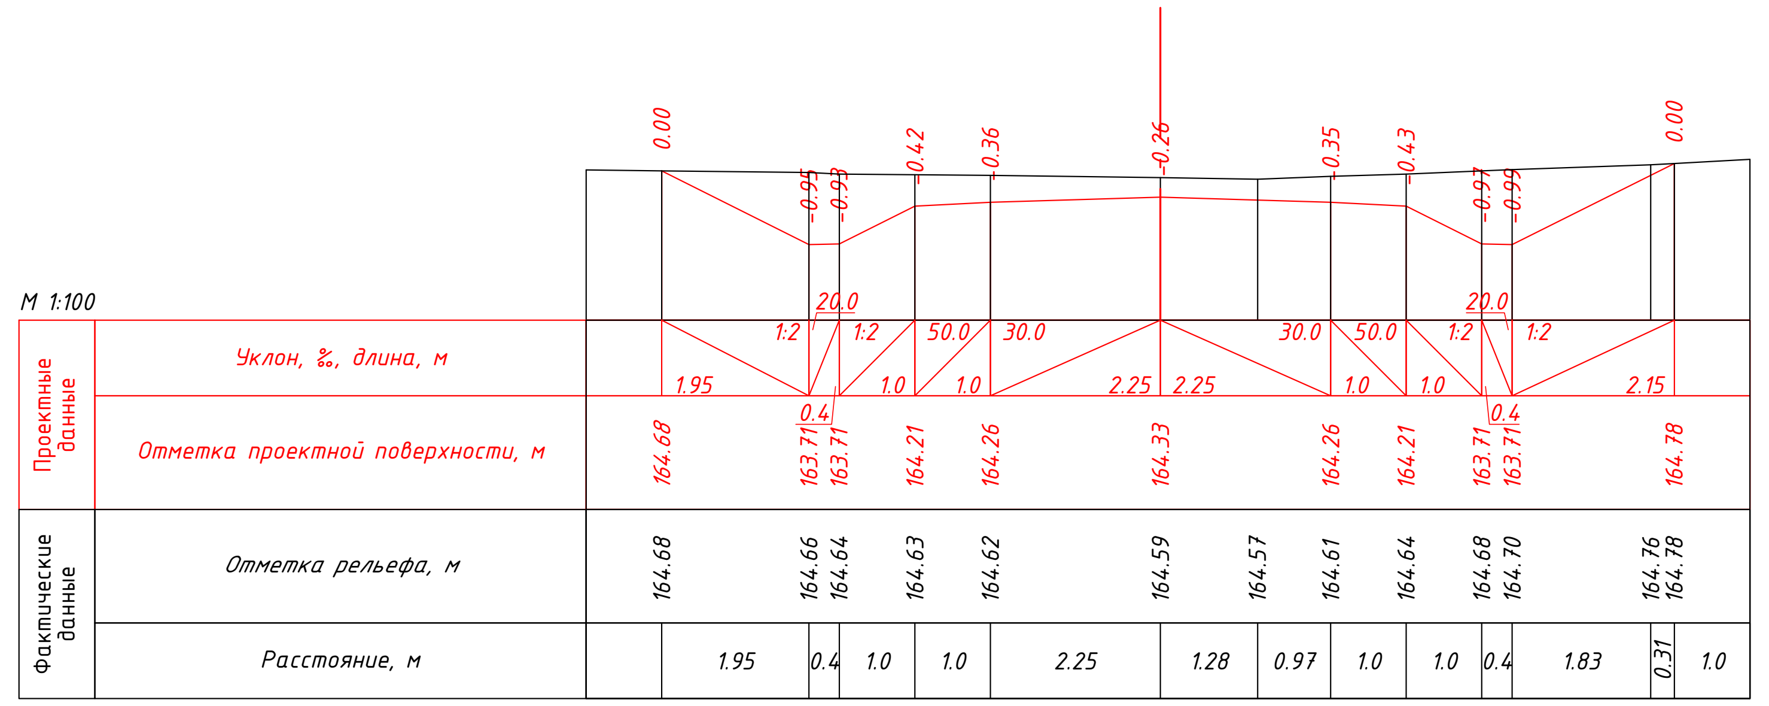

ПК 1+00.00

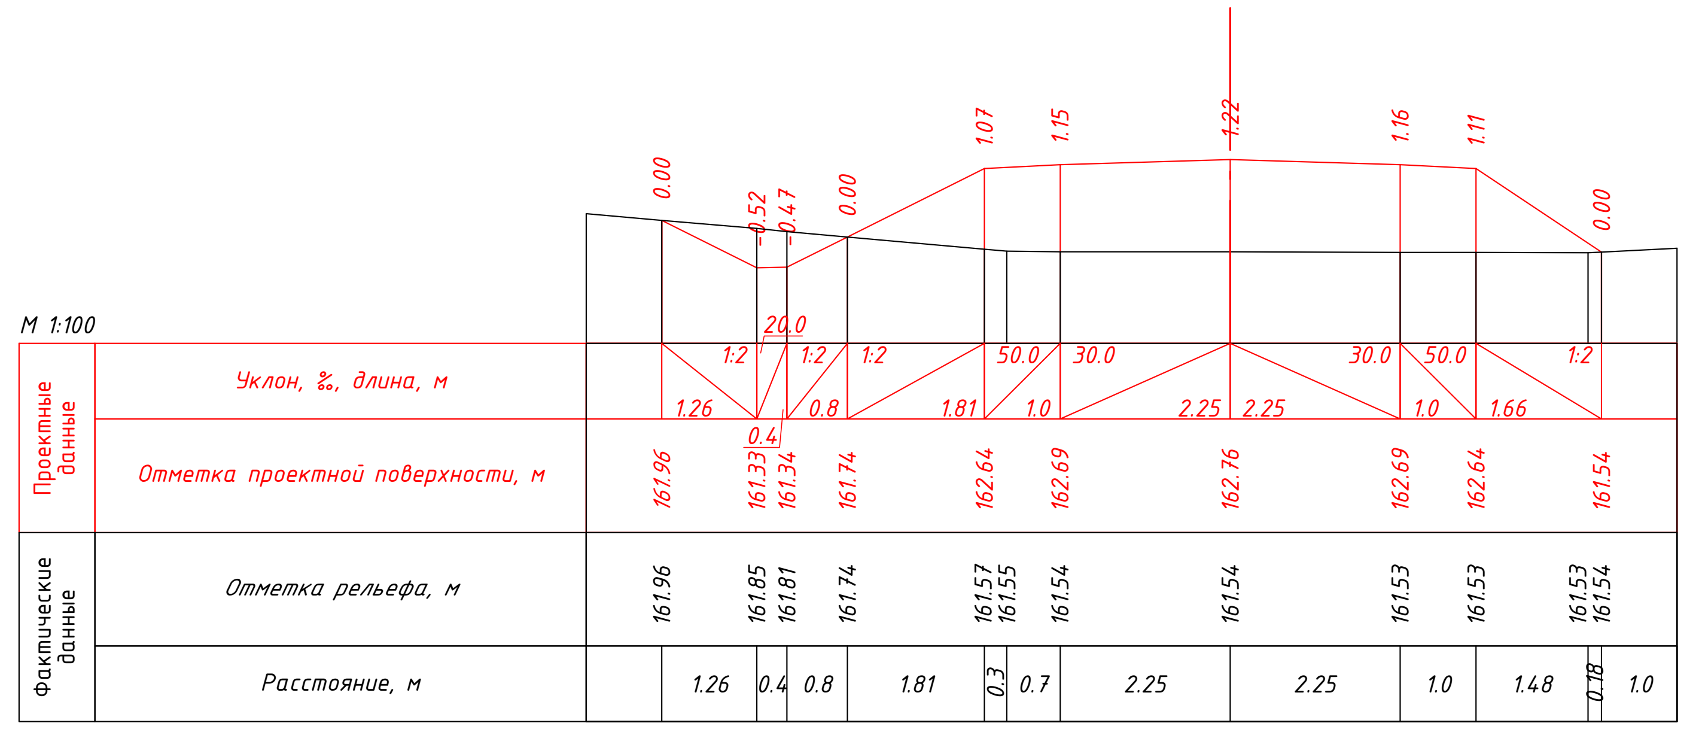

ПК 1+50.00

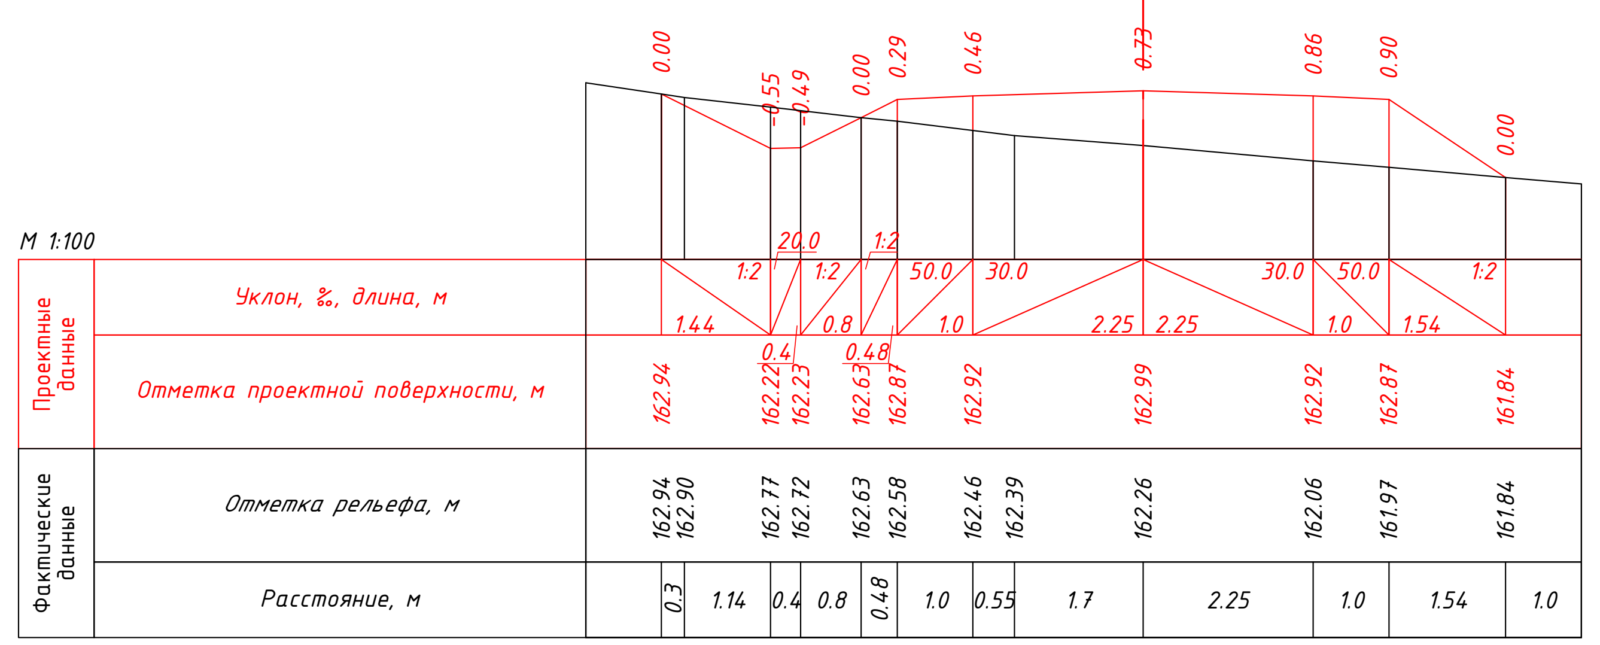

ПК 2+00.00

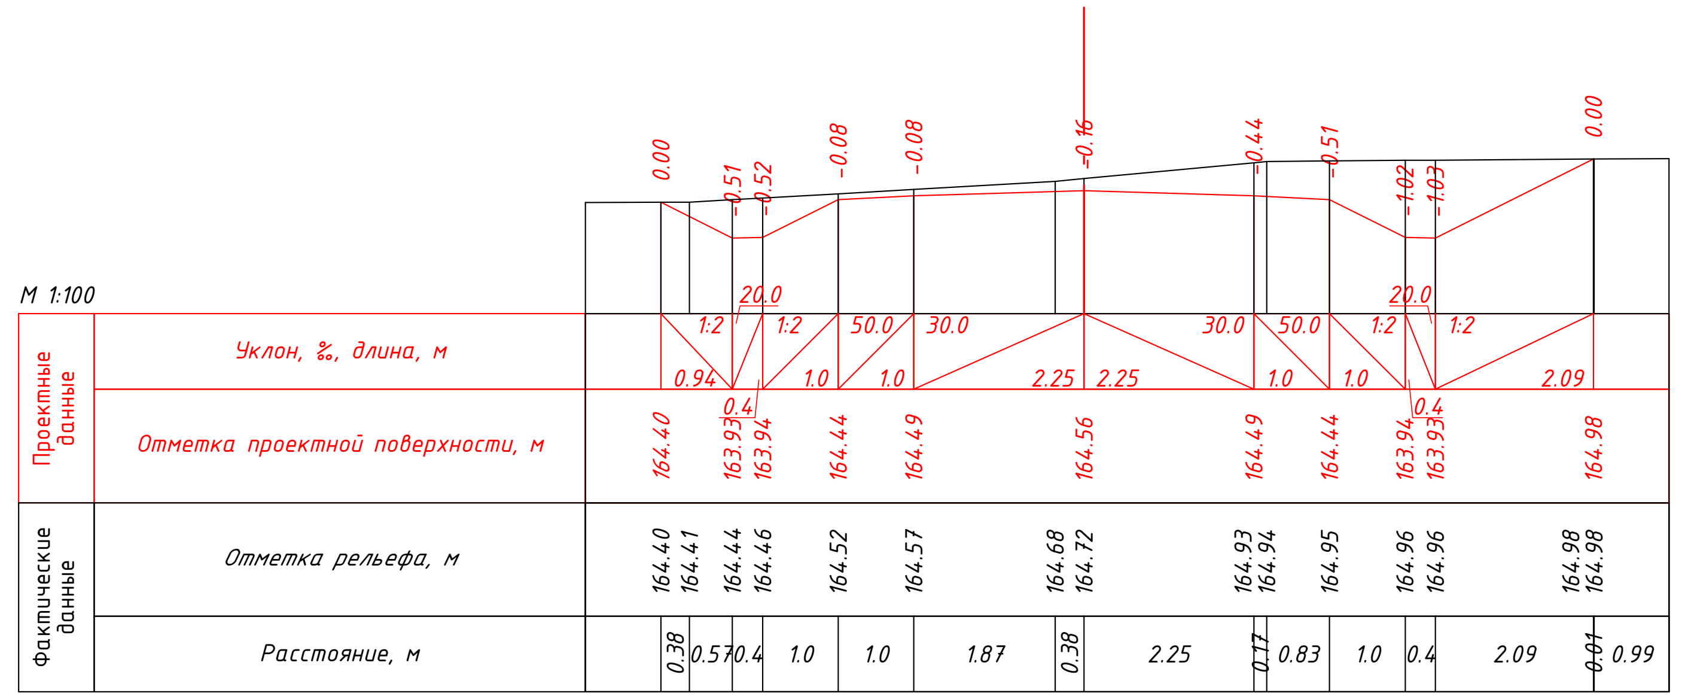

ПК 2+50.00

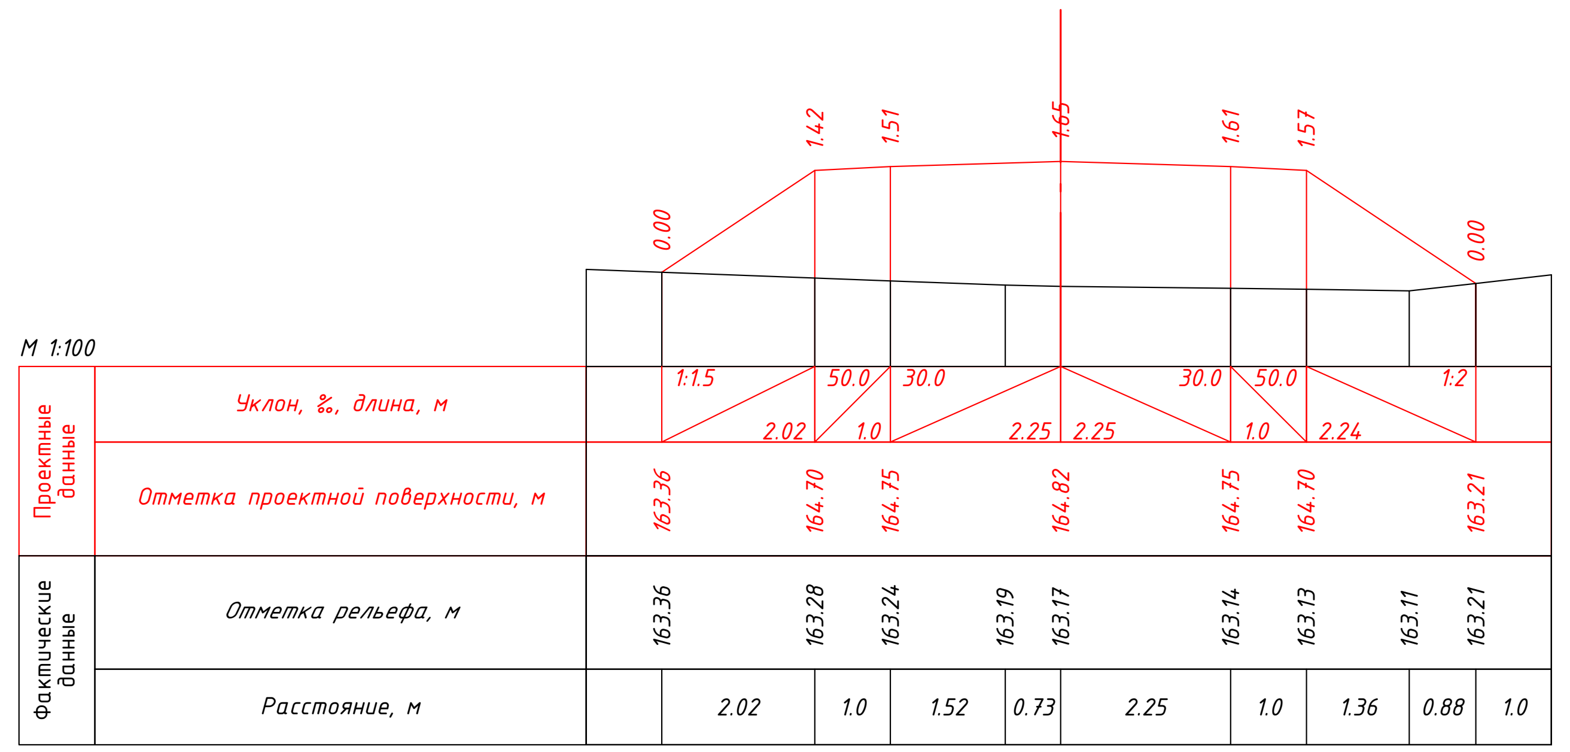

ПК 3+00.00

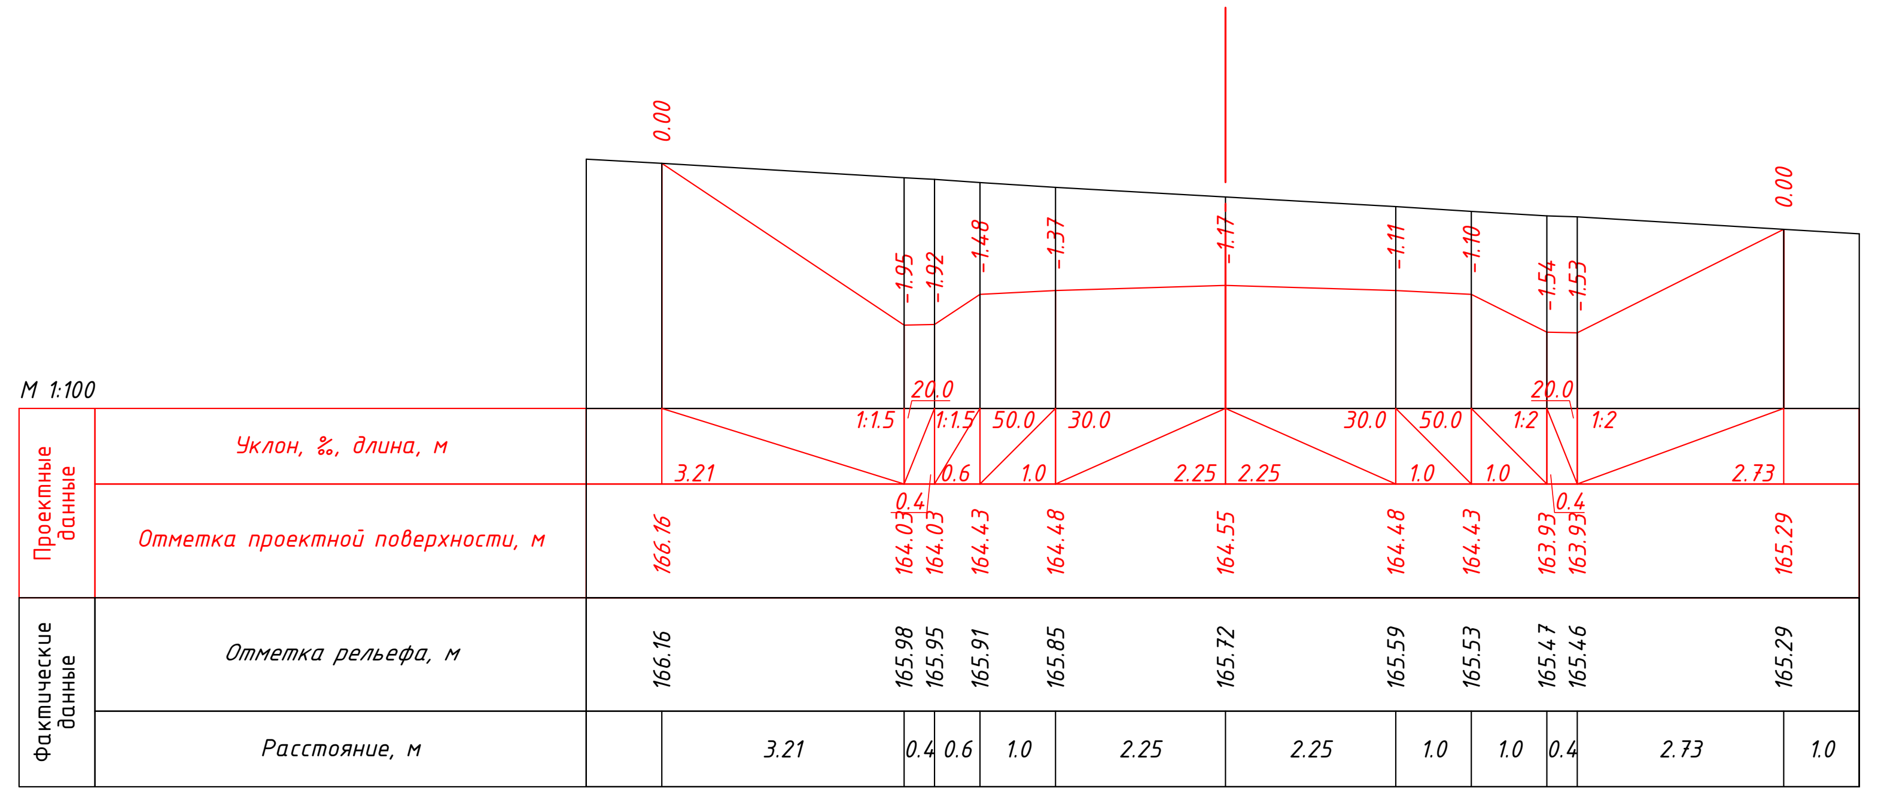

ПК 3+50.00

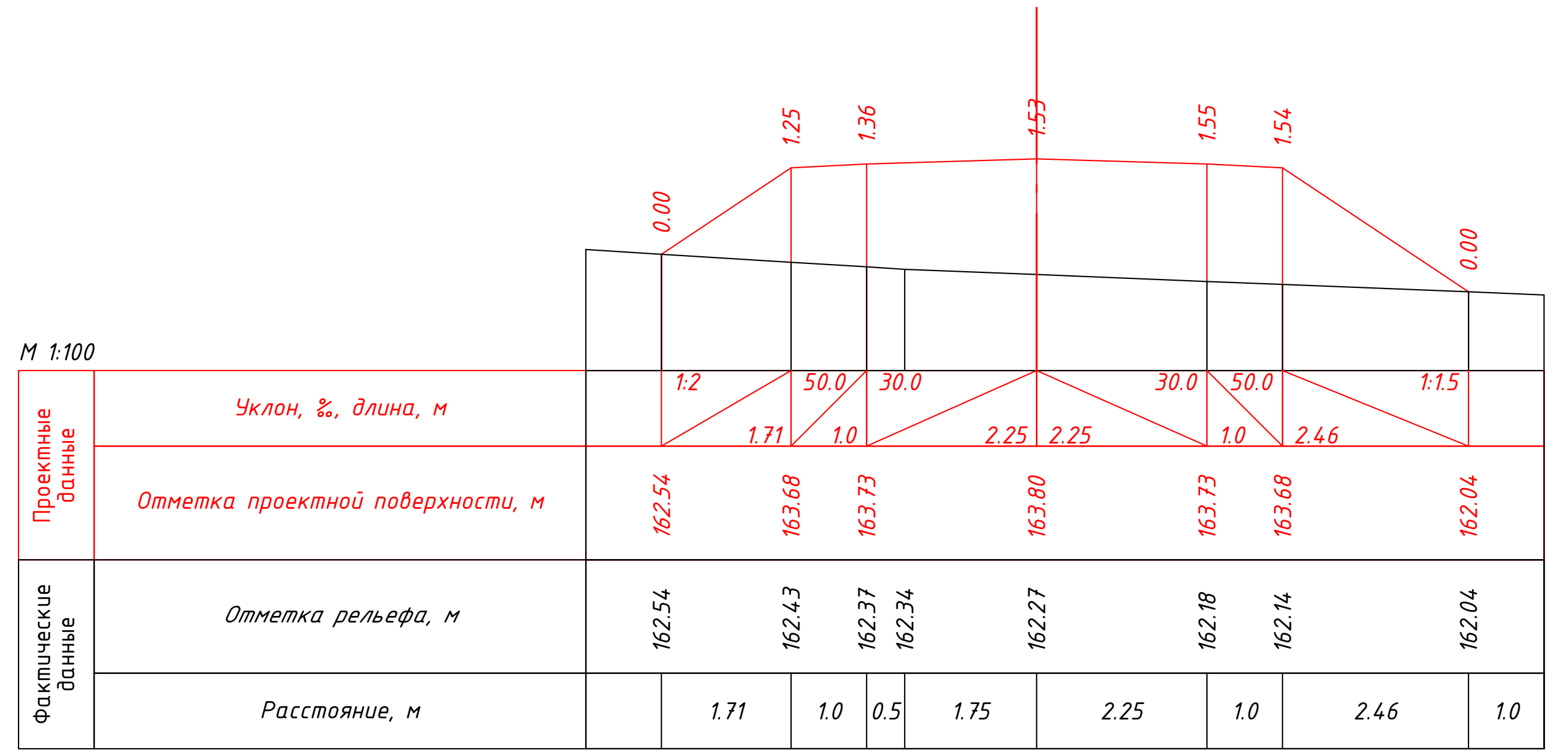

ПК 4+00.00

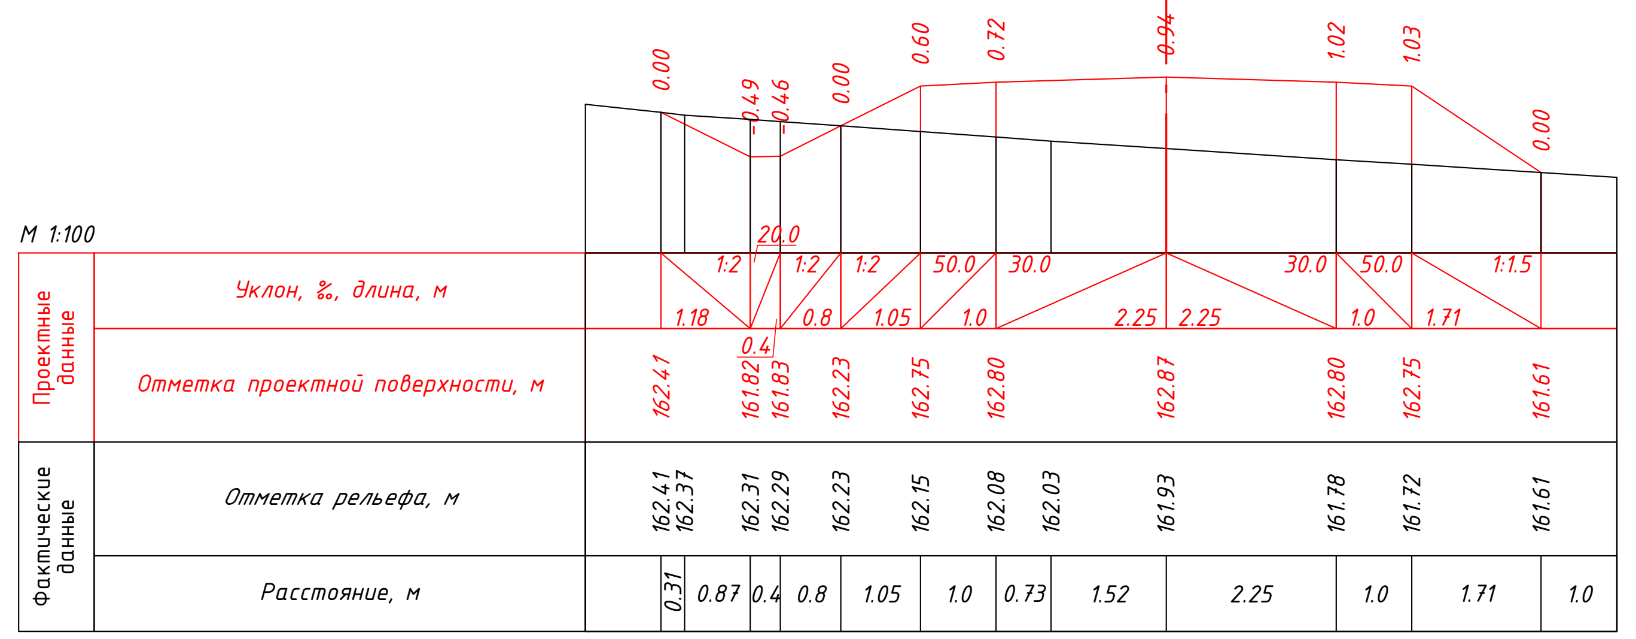

ПК 4+50.00

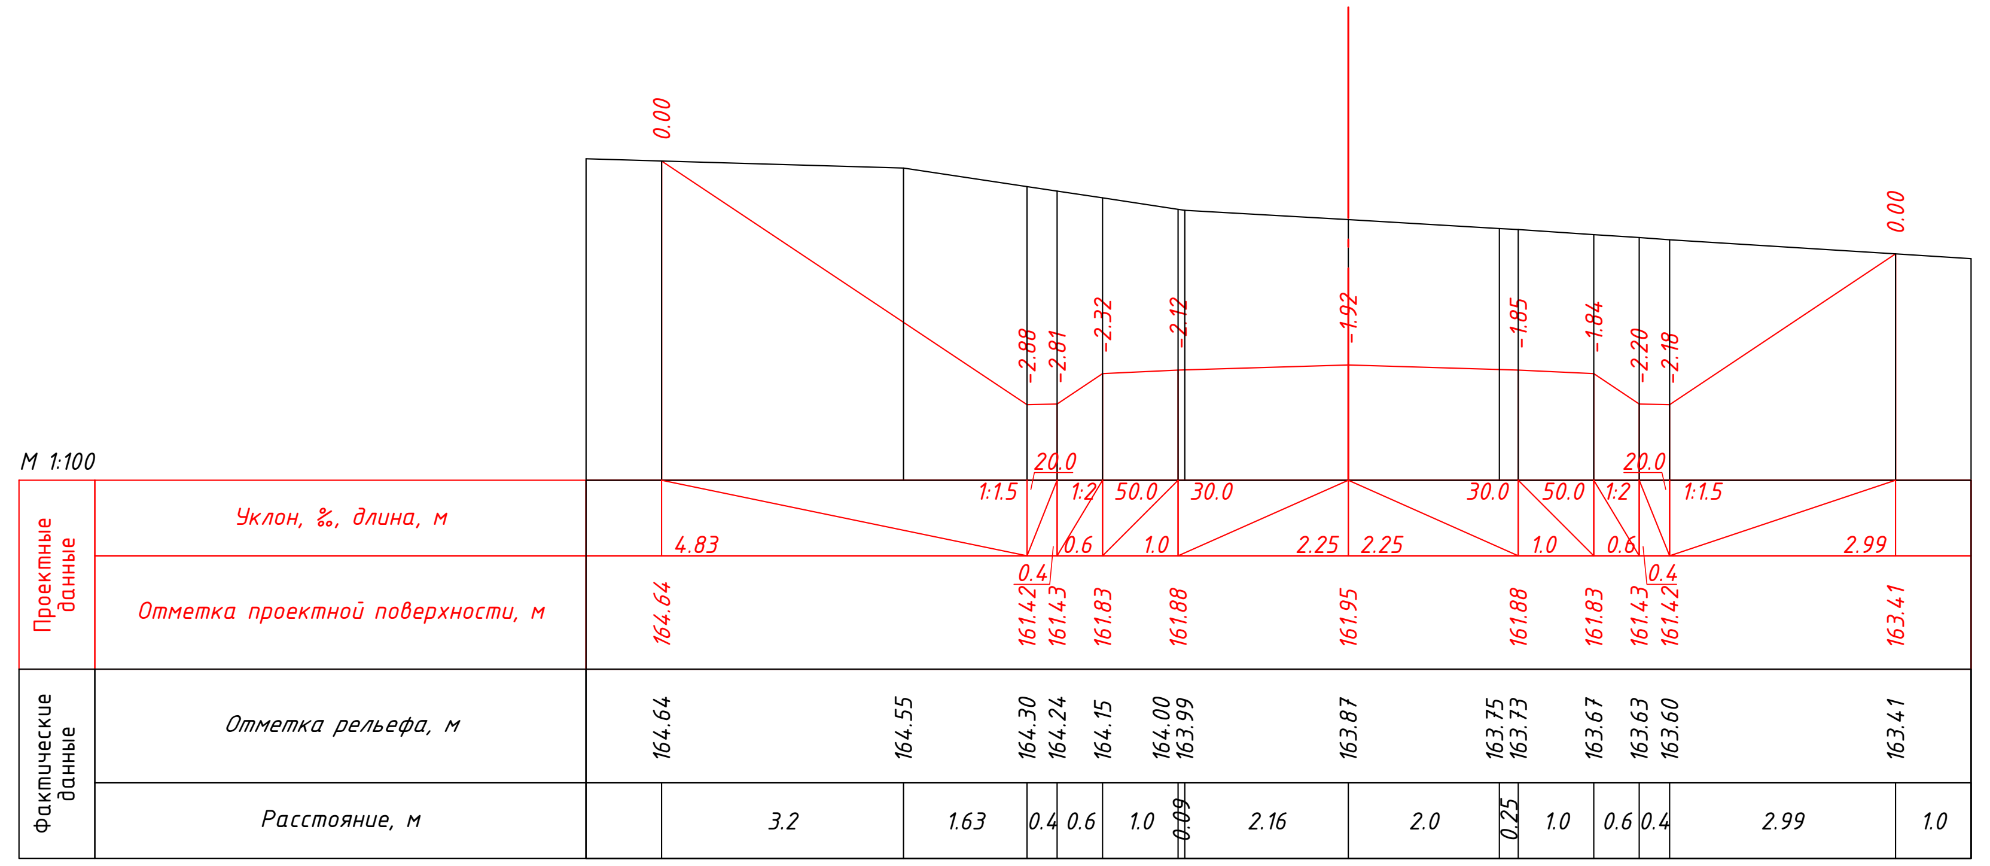

ПК 5+00.00

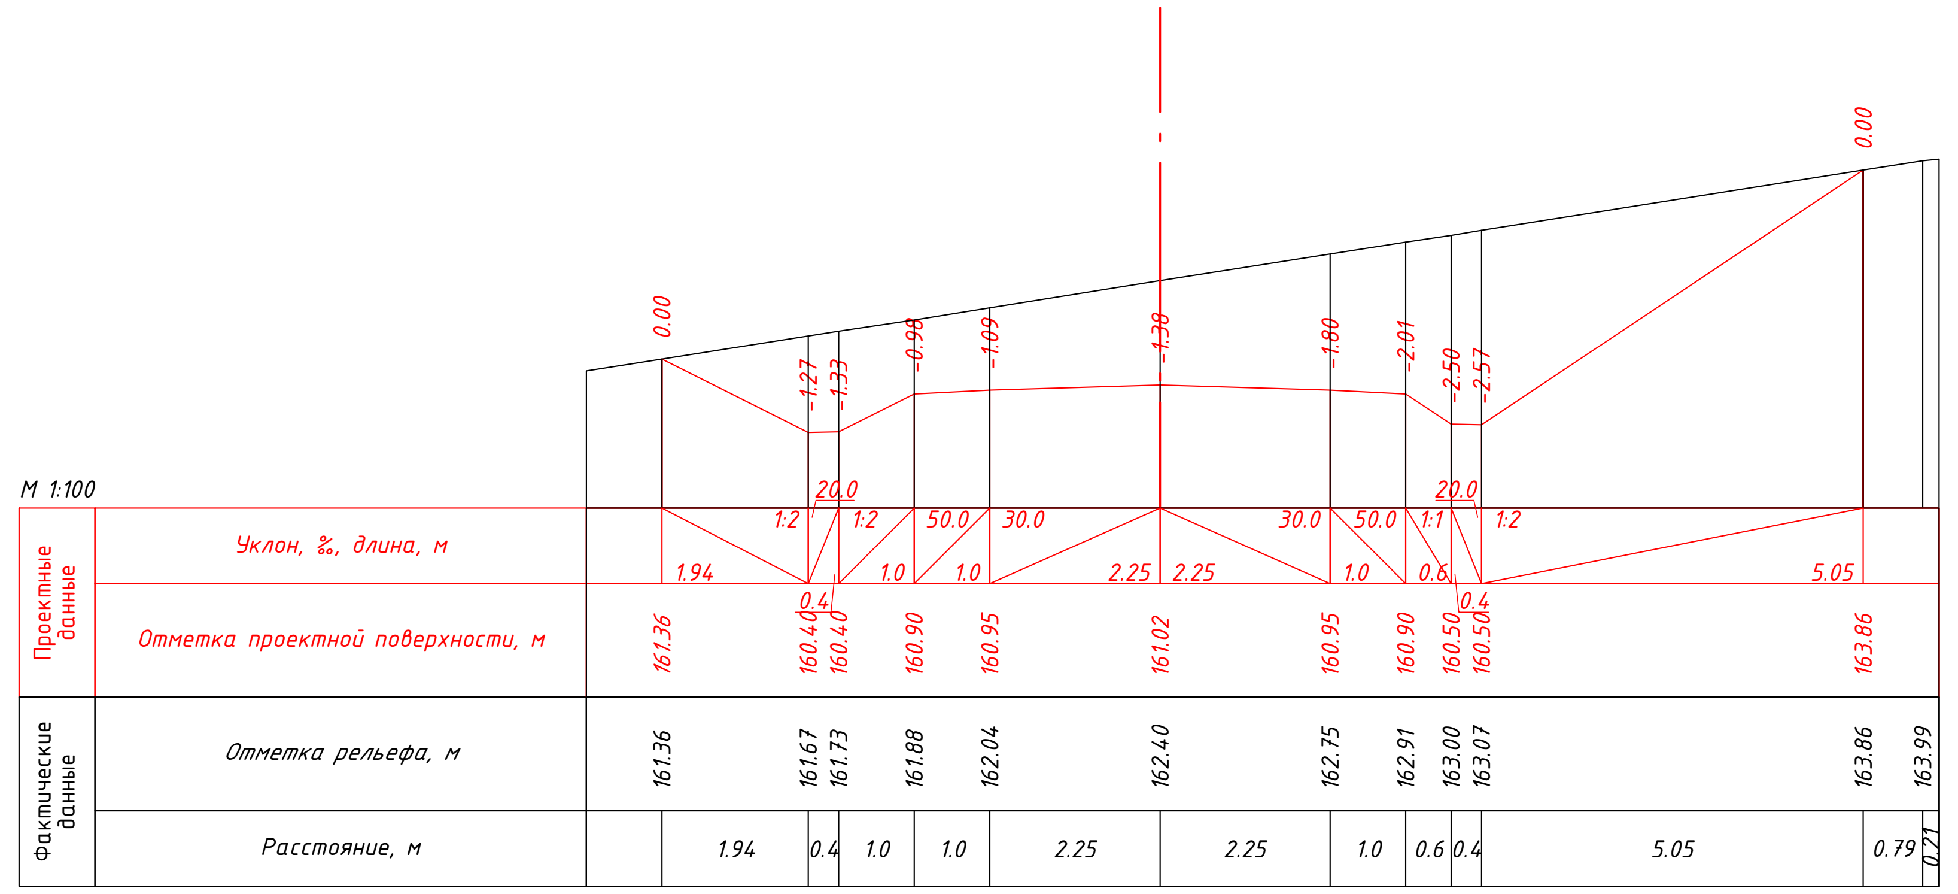

ПК 5+50.00

Примечание:

1. Данный чертеж рассматривать совместно с чертежами "План подъездной автодороги", "Продольный профиль", "Типовые поперечные профили", "Конструкция дорожной одежды".
2. Размеры даны в метрах.

Рев.	Дата	Назначение ревизии	Проверил	Утвердил
R1	10.08.2026	Выпущено для рассмотрения		

ЗАКАЗЧИК: UTG UZTRANSGAZ
ГЕНЕРАЛЬНЫЙ ПОДРЯДЧИК: UET UZBEKENERGOTAMIR
ПОДРЯДЧИК: PBG Pro Build Generation
ГЕНЕРАЛЬНЫЙ ПРОЕКТИРОВЩИК: EAST WEST ENGINEERING

EWE0426-MGL1-GLT-054-DRW-800109-R1

«СТРОИТЕЛЬСТВО НОВЫХ НИТОК (УЧАСТКОВ) ГАЗОПРОВОДОВ «ГАЗЛИ – САРИМОЙ» И «АКЧАЛОК – ГАЗЛИ – НУКУС» ОБЩЕЙ ПРОТЯЖЕННОСТЬЮ НЕ МЕНЕЕ 275 КМ»

Изм.	Кол. уч.	Лист.	№док.	Подп.	Дата
ГИП		Схабицкий А.			08.2026
Нач.отд.		Нигманова Н.			08.2026
Исполн.		Горлова О.			08.2026
Н. контр.		Схабицкий А.			08.2026

ГАЗОПРОВОД «ГАЗЛИ-САРИМОЙ» (54 КМ)
Площадка УЗРГ.
Генеральный план и транспорт.

Стадия	Лист	Листов
РД	1	1

Рабочие поперечные профили
ПК0+50.00-ПК5+50.00

EAST WEST ENGINEERING
ООО "EAST-WEST Engineering"
г. Ташкент 2026г.

Формат А3х4

Взам. инв. №
Подпись и дата
Инв.№ подл.