Тип 1. Типовой поперечный профиль земляного полотна автодороги. Насыпь в песках от пылеватого до средней крупности высотой до 1,0 м

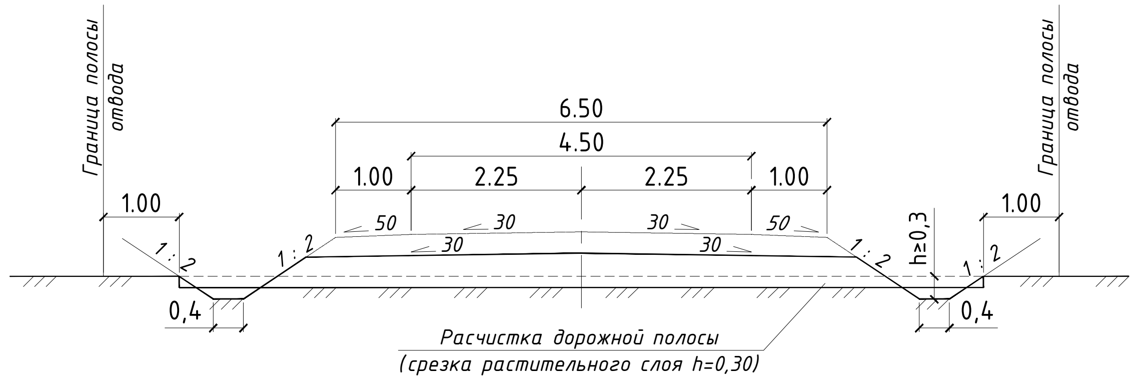

Тип 2. Типовой поперечный профиль земляного полотна автодороги. Насыпь в песках от пылеватого до средней крупности высотой более 1,0м

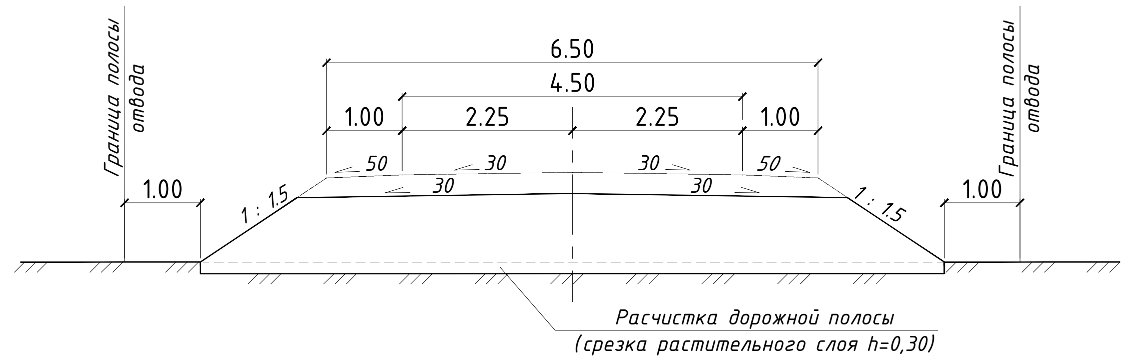

Тип 3. Типовой поперечный профиль земляного полотна автодороги. Выемка в песках от пылеватого до средней крупности глубиной до 1,0м

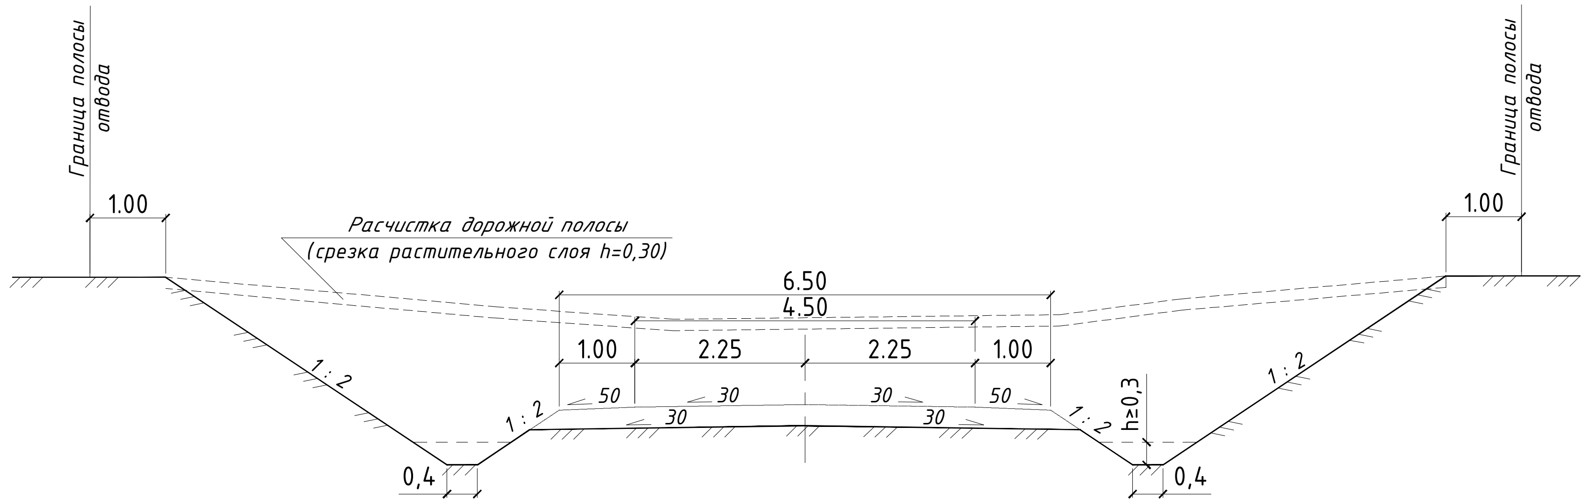

Тип 4. Типовой поперечный профиль земляного полотна автодороги. Выемка в песках от пылеватого до средней крупности глубиной более 1,0м

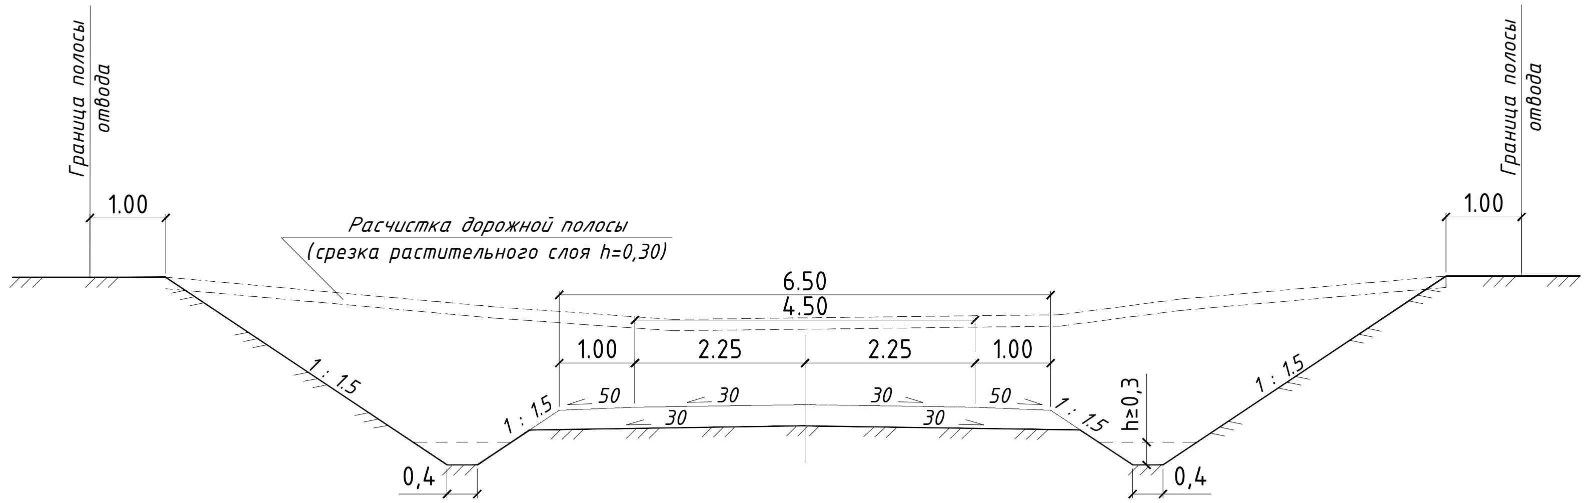

Примечания:

1. Типовые поперечные конструкции земляного полотна разработаны в соответствии с требованиями норм ШНК 2.05.02-23 "Автомобильные дороги", СНиП 2.05.07-91* "Промышленный транспорт", типового альбома "Земляное полотно автомобильных дорог общего пользования "Серия 503-0-48.87.
2. Все размеры приведены в метрах.

Рев.	Дата	Назначение ревизии	Проверил	Утвердил
R1	10.08.2026	Выпущено для рассмотрения		

ЗАКАЗЧИК: UTG UZTRANSGAZ

ГЕНЕРАЛЬНЫЙ ПОДРЯДЧИК: UET UZBEKENERGOTAMIR

ПОДРЯДЧИК: PBG Pro Build Generation

ГЕНЕРАЛЬНЫЙ ПРОЕКТИРОВЩИК: EAST WEST ENGINEERING

EWE0426-MGL1-GLT-054-DRW-800110-R1

«СТРОИТЕЛЬСТВО НОВЫХ НИТОК (УЧАСТКОВ) ГАЗОПРОВОДОВ «ГАЗЛИ – САРИМОЙ» И «АКЧАЛОК - ГАЗЛИ – НУКУС» ОБЩЕЙ ПРОТЯЖЕННОСТЬЮ НЕ МЕНЕЕ 275 КМ»

Изм.	Кол. уч.	Лист.	№док.	Подп.	Дата
ГИП		Схабицкий А.			08.2026
Нач.отд.		Нигманова Н.			08.2026
Исполн.		Горлова О.			08.2026
Н. контр.		Схабицкий А.			08.2026

ГАЗОПРОВОД «ГАЗЛИ-САРИМОЙ» (54 КМ)
Площадка УЗРГ.
Генеральный план и транспорт.

Стадия	Лист	Листов
РД	1	1

Типовые поперечные профили

ООО "EAST-WEST Engineering"
г. Ташкент 2026г.

Формат А4х3

Взам. инв. №

Подпись и дата

Инв.№ подл.