

Конструкция дорожной одежды подъездной автодороги. Тип 1

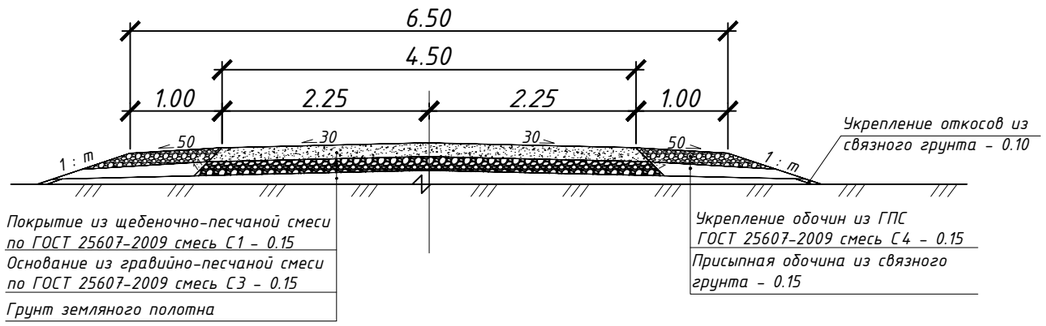

Конструкция дорожной одежды тротуара. Тип 3

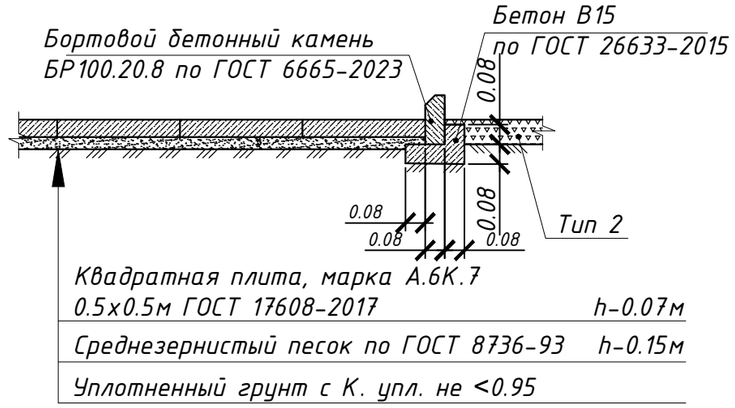


Конструкция щебеночного покрытия площадки УЗРГ. Тип 2 (1:20)



Конструкция дорожной одежды Внутриплощадочного проезда. Тип 1 (1:20)



Узел сопряжения проезда и площадки

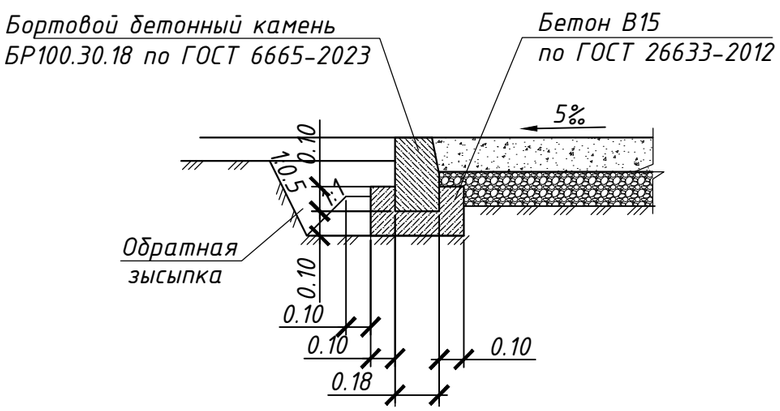

Рев.	Дата	Назначение ревизии	Проверил	Утвердил
R1	10.08.2026	Выпущено для рассмотрения		

ЗАКАЗЧИК: UTG UZTRANSGAZ

ГЕНЕРАЛЬНЫЙ ПОДРЯДЧИК: UET UZBEKENERGOTAMIR

ПОДРЯДЧИК: PBG Pro Build Generation

ГЕНЕРАЛЬНЫЙ ПРОЕКТИРОВЩИК: EAST WEST ENGINEERING

Изм.	Кол. уч.	Лист.	№док.	Подп.	Дата
ГИП		Схабицкий А.			08.2026
Нач.отд.		Нигманова Н.			08.2026
Исполн.		Горлова О.			08.2026
Н. контр.		Схабицкий А.			08.2026

EWE0426-MGL1-GLT-054-DRW-800111-R1

«СТРОИТЕЛЬСТВО НОВЫХ НИТОК (УЧАСТКОВ) ГАЗОПРОВОДОВ «ГАЗЛИ – САРИМОЙ» И «АКЧАЛОК - ГАЗЛИ – НУКУС» ОБЩЕЙ ПРОТЯЖЕННОСТЬЮ НЕ МЕНЕЕ 275 КМ»

ГАЗОПРОВОД «ГАЗЛИ-САРИМОЙ» (54 КМ)
Площадка УЗРГ.
Генеральный план и транспорт

Стадия	Лист	Листов
РД	1	1

Конструкция дорожной одежды

ООО "EAST-WEST Engineering"
г. Ташкент 2026г.

Взам. инв. №

Подпись и дата

Инв.№ подл.

Формат А3