


РАЗРЕЗ ПО ОСИ ТРУБЫ

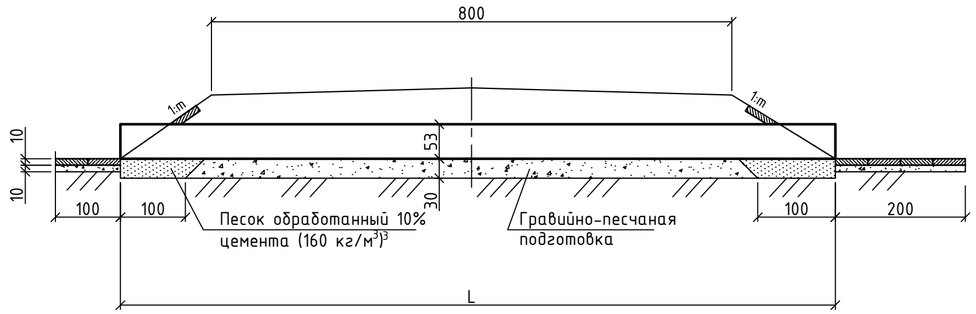


РАЗРЕЗ

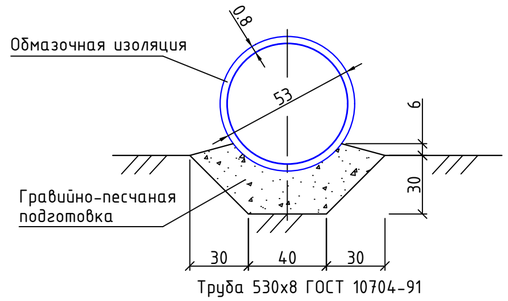


Ф А С А Д

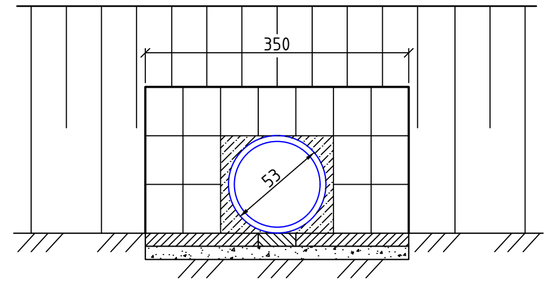

ПЛАН (НАСЫПЬ НЕ ПОКАЗАНА)

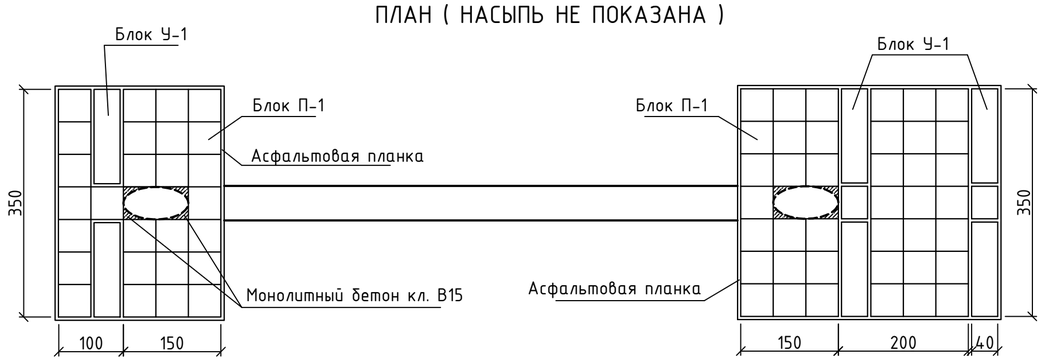

ОМОНОЛИЧИВАНИЕ ПЛИТ

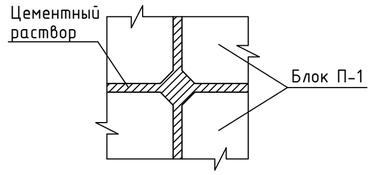

Примечание:

1. Материал трубы – стальные трубы Dн – 530 мм, толщина стенки трубы – 8 мм по ГОСТ 10704-91.
2. Гидроизоляция трубы – два слоя полимерной липкой ленты на битумной или клеевой грунтовке. Поверхность металлической трубы перед устройством изоляции должна быть тщательно очищена от ржавчины.
3. Обсыпка труб производится мягким грунтом на высоту не менее 0.5 м от верха трубы. Грунт отсыпается с обеих сторон одновременно на всю ширину насыпи слоями не более 20 см с уплотнением каждого слоя. Особо тщательно уплотняется грунт в нижней части насыпи.
4. Укрепление русла и откосов принято из сборных бетонных плит П-1 по серии 3-501.1-156.
5. Все работы по строительству трубы выполняются в соответствии со ШНК 2.05.03-22 "Мосты и трубы".
6. Размеры на чертеже даны сантиметрах.
7. Настоящий чертеж рассматривать совместно с чертежем "План подъездной автодороги"

ОБЪЕМЫ РАБОТ НА 1 П.М. ТРУБЫ

№	Наименование	Ед.изм.	Количество
1	Разработка грунта вручную под укрепление	$м^3$	0.2
2	Гравийно-песчаная подготовка	$м^3$	0.16
3	Мет труба d-0.53м толщина стенки 8мм	кг	103.0
4	Гидроизоляция	$м^2$	2.0

СПЕЦИФИКАЦИЯ БЛОКОВ УКРЕПЛЕНИЯ

№№блоков	Габаритные размеры, см	Материал	Объем блока,$м^3$	Количество блоков на трубу,шт.	Вес блока, т	Общий объем,$м^3$
У-1	40x50x150	бетон кл.В15	0.30	6.0	0.72	1.80
П-1	49x49x10	бетон кл.В15	0.022	69.0	0.053	1.52

УКРЕПЛЕНИЕ

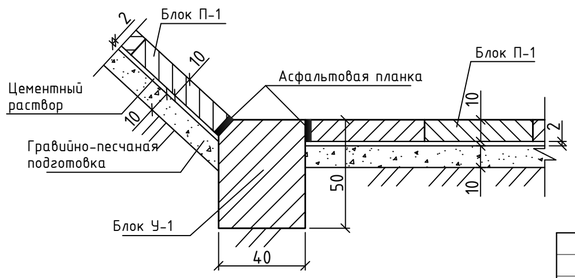


ТАБЛИЦА ПРИВЯЗКИ СООРУЖЕНИЙ И ОБЪЕМОВ РАБОТ

№№ п/п	Местоположение сооружения	Высота насыпи	Отметки			Уклон сооружения	Длина трубы	Объемы работ на трубы					Укрепительные работы							
			Бровка земполотна	Трубы у входа	Трубы у выхода			Разработка грунта в ручную под основание	Гравийно-песчаная подготовка	Песок обработанный 10% цемента(160кг/м³)	Мет труба d-0.53м толщина стенки 8мм	Гидроизоляция	Укрепление блоками П-1	Укрепление блоками У-1	Разработка грунта вручную под укрепление	Гравийно-песчаная подготовка	Бетон кл.В15 укладываемый на месте	Асфальтовые пленки	Металл монтажных петель	Цементный раствор
	ПК +	м	м	м	м	‰	м	$м^3$	$м^3$	$м^3$	m	$м^2$	шт/$м^3$	шт/$м^3$	$м^3$	$м^3$	$м^3$	$м^3$	кг	$м^3$
1	1+60.00	1.23	162.61	161.38	161.14	24	10.0	2.0	1.28	0.32	1.03	20.0	69.0 / 1.52	6.00 / 1.80	6.00	2.30	0.20	0.30	10.0	0.40
1	3+00.00	1.68	164.83(6x) 164.81	163.15	163.10	4	13.0	2.6	1.76	0.32	1.34	26.0	69.0 / 1.52	6.00 / 1.80	6.00	2.30	0.20	0.30	10.0	0.40
1	4+40.00	1.41	163.16(6x) 162.96	162.00	161.65	27	13.0	2.6	1.76	0.32	1.34	26.0	69.0 / 1.52	6.00 / 1.80	6.00	2.30	0.20	0.30	10.0	0.40

Рев.	Дата	Назначение ревизии	Проверил	Утвердил
R1	10.08.2026	Выпущено для рассмотрения		

ЗАКАЗЧИК: UTG ГЕНЕРАЛЬНЫЙ ПОДРЯДЧИК: UET ПОДРЯДЧИК: PBG ГЕНЕРАЛЬНЫЙ ПРОЕКТИРОВЩИК: EAST WEST ENGINEERING

EWE0426-MGL1-GLT-054-DRW-800112-R1

«СТРОИТЕЛЬСТВО НОВЫХ НИТОК (УЧАСТКОВ) ГАЗОПРОВОДОВ «ГАЗЛИ – САРИМОЙ» И «АКЧАЛОК – ГАЗЛИ – НУКУС» ОБЩЕЙ ПРОТЯЖЕННОСТЬЮ НЕ МЕНЕЕ 275 КМ»

Изм.	Кол. уч.	Лист.	№док.	Подп.	Дата			
ГИП		Схабицкий А.			08.2026	ГАЗОПРОВОД «ГАЗЛИ-САРИМОЙ» (54 КМ) Площадка УЗРГ. Генеральный план и транспорт.	Стадия	Лист	Листов
Нач.отд.		Нигманова Н.			08.2026		РД	1	1
Исполн.		Горлова О.			08.2026				
Н. контр.		Схабицкий А.			08.2026	Металлическая водопропускная труба отверстием 0.53 м	EAST WEST ENGINEERING	ООО "EAST-WEST Engineering" г. Ташкент 2026г.	

Взам. инв. № | Подпись и дата | Инв.№ подл.

Формат А2