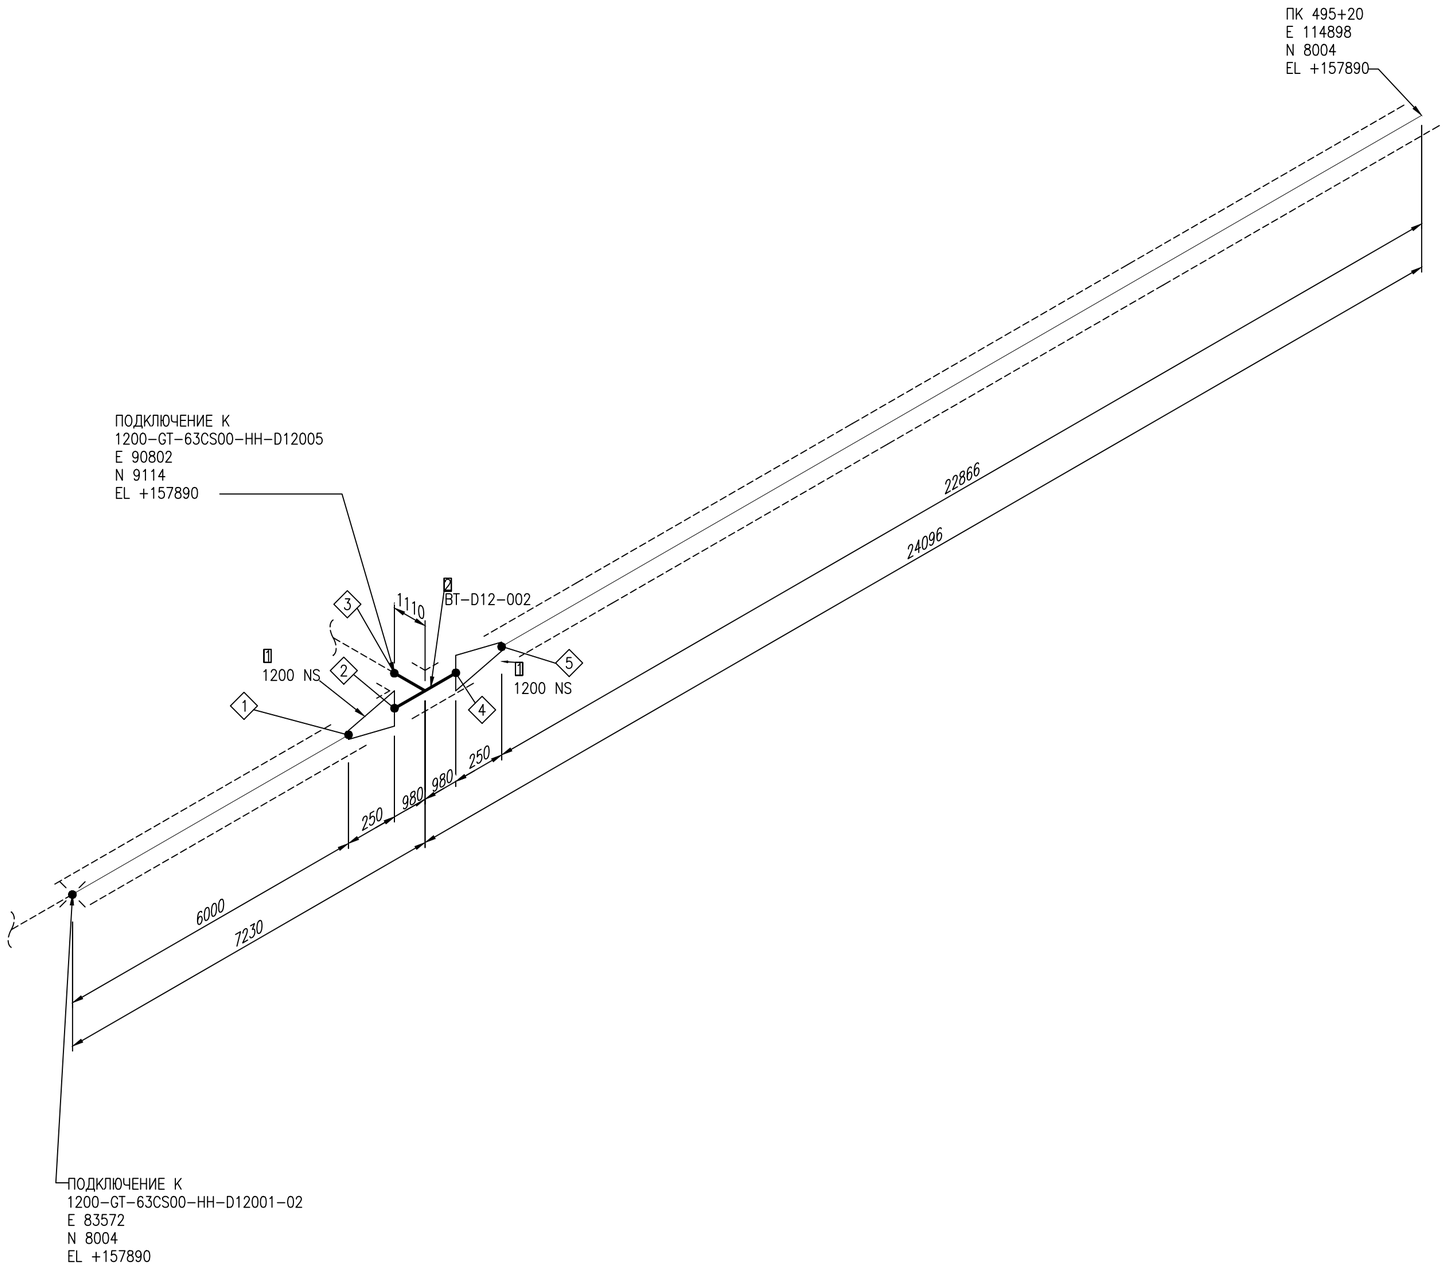


СПЕЦИФИКАЦИЯ ИЗДЕЛИЙ И МАТЕРИАЛОВ

ПОЗ.	НАИМЕНОВАНИЕ	СТАНДАРТ	КОЛ.	ПРИМЕЧАНИЕ
	ФИТИНГИ			
1	Кольцо КП I 1220(17K60×12K60)-5,5(8,25)-B-30, сталь K60	ТУ 1469-017-38948552-2015	2	
2	Тройник ТР I 1220(17K60)-5,5(8,25)-0,6-30, сталь K60	ТУ 1469-017-38948552-2015	1	

Трубопровод	ДАННЫЕ ПО ТРУБОПРОВОДУ		
1200-GT-63CS00-HH-D12001	Расчетные параметры	Температура	-26,9...+85 °C
		Давление	6,3 MPa
	Рабочие параметры	Температура	-20...+60 °C
		Давление	5,5 MPa
	Параметры испытания	Тип	Гидравлическое
Ссылочные чертежи No		Давление	8.25 MPa
EWE0426-MGL1-PRE-054-SCM-610120	Изоляция	Тип	HH
		Толщина	5 mm
	Катодная защита	Да или Нет	Да

Рев.	Дата	Назначение ревизии	Проверил	Утвердил
R1	25.08.2026	Выпущено для рассмотрения		

ЗАКАЗЧИК: UTG ГЕНЕРАЛЬНЫЙ ПОДРЯДЧИК: UET ПОДРЯДЧИК: PBG ГЕНЕРАЛЬНЫЙ ПРОЕКТИРОВЩИК: EAST WEST ENGINEERING

ПЕРЕЧЕНЬ СВАРНЫХ ШВОВ

№	DN	ТИП
1	1200	BUTTWELD
2	1200	BUTTWELD
3	1200	BUTTWELD
4	1200	BUTTWELD
5	1200	BUTTWELD

Изм.	Кол.уч.	Лист	№док.	Подпись	Дата
ГИП		Схабицкий А.			08.2026
Нач.отд.		Рябинин А.			08.2026
Исполн.		Халилов Ж.			08.2026
Н.контр		Схабицкий А.			08.2026

EWE0426-MGL1-PRE-054-ISO-800702-R1

«СТРОИТЕЛЬСТВО НОВЫХ НИТОК (УЧАСТКОВ) ГАЗОПРОВОДОВ «ГАЗЛИ - САРИМОЙ» И «АКЧАЛОК - ГАЗЛИ - НУКУС» ОБЩЕЙ ПРОТЯЖЕННОСТЬЮ НЕ МЕНЕЕ 275 КМ».

ГАЗОПРОВОД «ГАЗЛИ-САРИМОЙ» (54 КМ)
Узел замера расхода газа УЗРГ-D12-001


Стадия	Лист	Листов
РД	1	4

Изометрический чертеж трубопровода
1200-GT-63CS00-HH-D12001

ООО "EAST-WEST Engineering"
г. Ташкент 2026г.

Взам. инв. №
Подпись и дата
Инв.№ подл.

Формат А2 594x420

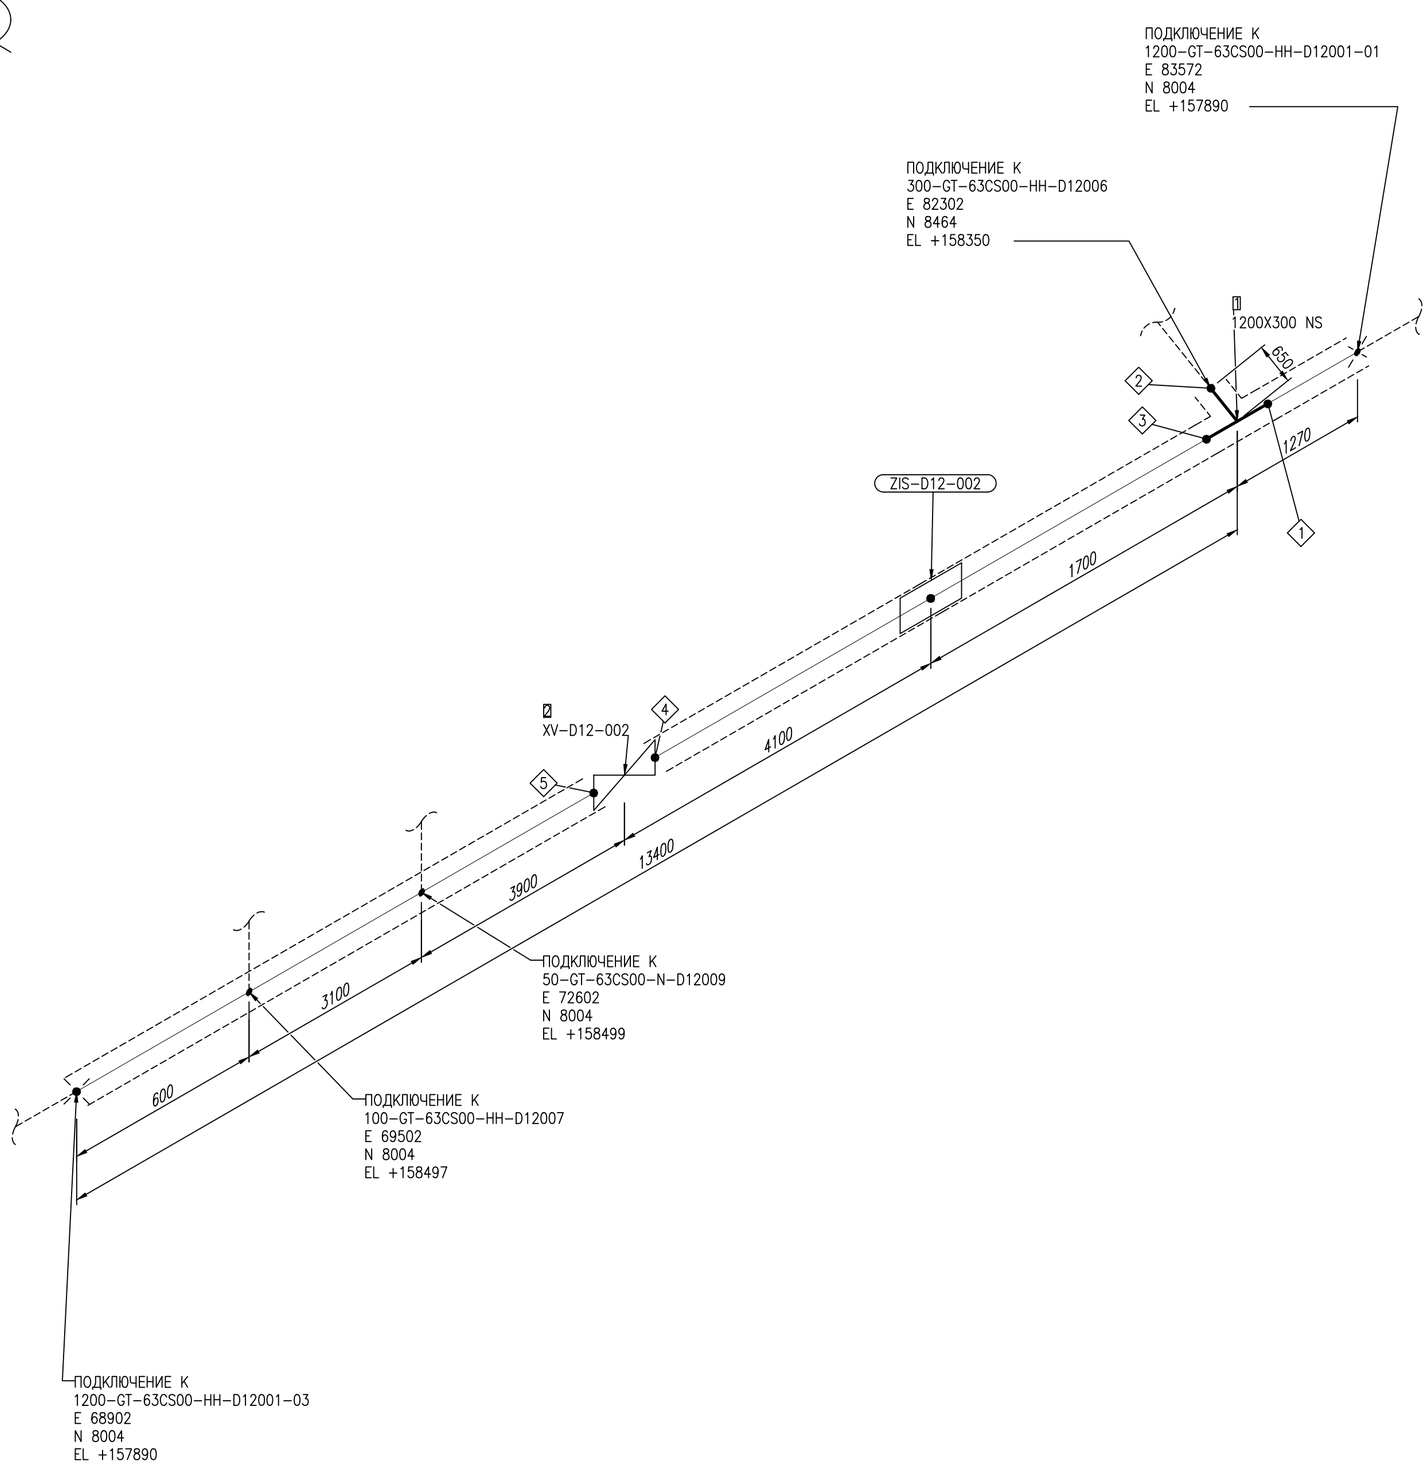

СПЕЦИФИКАЦИЯ ИЗДЕЛИЙ И МАТЕРИАЛОВ

ПОЗ.	НАИМЕНОВАНИЕ	СТАНДАРТ	КОЛ.	ПРИМЕЧАНИЕ
	ФИТИНГИ			
1	Тройник T I 1220(13К60)-325(10К48)-5,5(8,25)-0,75-655-30, сталь К60	ТУ 1469-017-38948552-2015	1	
	АРМАТУРА			
2	Кран шаровой DN1200 PN-6,3 МПа с пневмогидроприводом, приварной, подземный	EWE0426-MGL1-PRE-054-DSH-610134	1	

Трубопровод	ДАННЫЕ ПО ТРУБОПРОВОДУ		
1200-GT-63CS00-HH-D12001	Расчетные параметры	Температура	-26,9...+85 °C
		Давление	6,3 MPa
	Рабочие параметры	Температура	-20...+60 °C
		Давление	5,5 MPa
Ссылочные чертежи No	Параметры испытания	Тип	Гидравлическое
		Давление	8.25 MPa
EWE0426-MGL1-PRE-054-SCM-610120	Изоляция	Тип	HH
		Толщина	5 mm
	Катодная защита	Да или Нет	Да

Рев.	Дата	Назначение ревизии	Проверил	Утвердил
R1	25.08.2026	Выпущено для рассмотрения		

ЗАКАЗЧИК: ГЕНЕРАЛЬНЫЙ ПОДРЯДЧИК: ПОДРЯДЧИК: ГЕНЕРАЛЬНЫЙ ПРОЕКТИРОВЩИК:

ПЕРЕЧЕНЬ СВАРНЫХ ШВОВ

№	DN	ТИП
1	1200	BUTTWELD
2	1200	BUTTWELD
3	1200	BUTTWELD
4	1200	BUTTWELD
5	1200	BUTTWELD

Изм.	Кол.уч.	Лист	№док.	Подпись	Дата
ГИП		Схабицкий А.			08.2026
Нач.отд.		Рябинин А.			08.2026
Исполн.		Халилов Ж.			08.2026
Н.контр		Схабицкий А.			08.2026

EWE0426-MGL1-PRE-054-ISO-800702-R1

«СТРОИТЕЛЬСТВО НОВЫХ НИТОК (УЧАСТКОВ) ГАЗОПРОВОДОВ «ГАЗЛИ - САРИМОЙ» И «АКЧАЛОК - ГАЗЛИ - НУКУС» ОБЩЕЙ ПРОТЯЖЕННОСТЬЮ НЕ МЕНЕЕ 275 КМ».

ГАЗОПРОВОД «ГАЗЛИ-САРИМОЙ» (54 КМ)
Узел замера расхода газа УЗРГ-D12-001


Стадия	Лист	Листов
РД	2	4

Изометрический чертеж трубопровода
1200-GT-63CS00-HH-D12001

ООО "EAST-WEST Engineering"
г. Ташкент 2026г.

Взам. инв. №
Подпись и дата
Инв.№ подл.

Формат А2 594x420

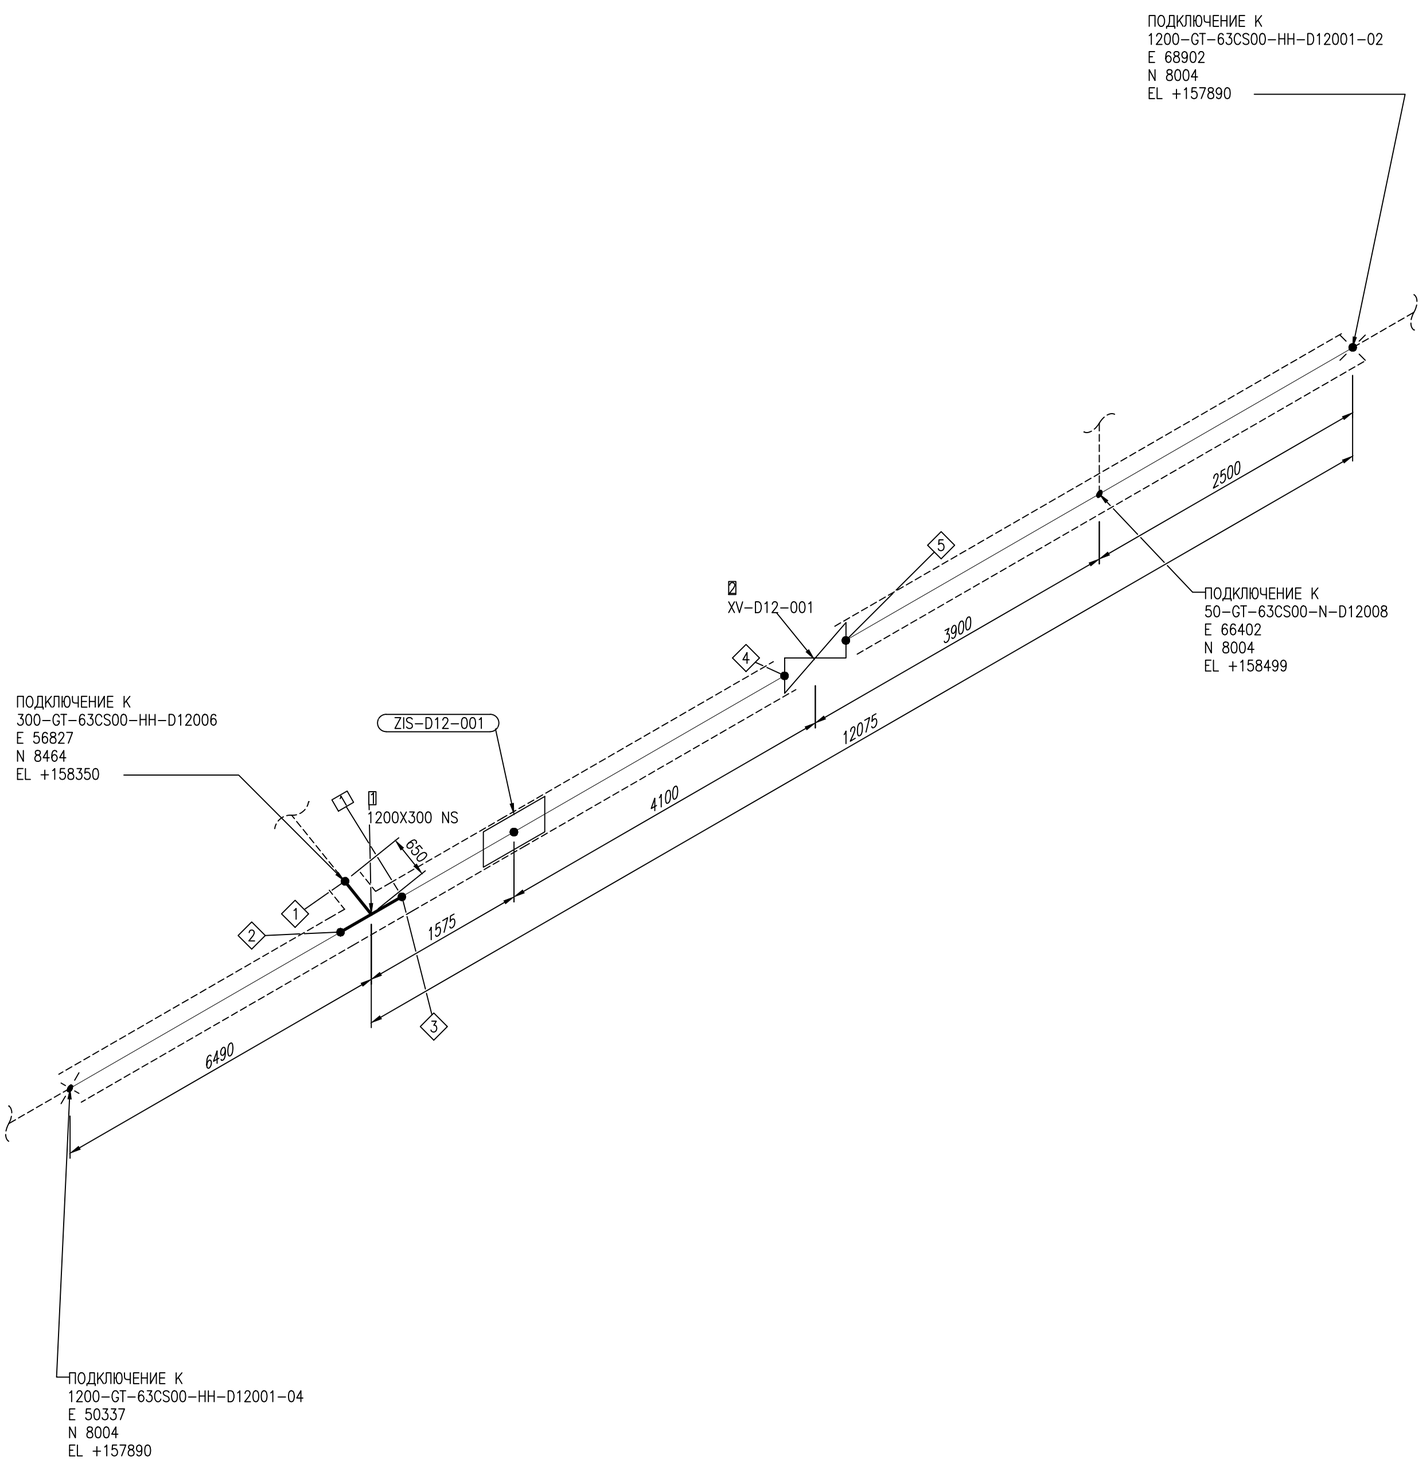

СПЕЦИФИКАЦИЯ ИЗДЕЛИЙ И МАТЕРИАЛОВ				
ПОЗ.	НАИМЕНОВАНИЕ	СТАНДАРТ	КОЛ.	ПРИМЕЧАНИЕ
	ФИТИНГИ			
1	Тройник T I 1220(13К60)-325(10К48)-5,5(8,25)-0,75-655-30, сталь К60	ТУ 1469-017-38948552-2015	1	
	АРМАТУРА			
2	Кран шаровой DN1200 PN-6,3 МПа с пневмогидроприводом, приварной, подземный	EWE0426-MGL1-PRE-054-DSH-610134	1	

ПЕРЕЧЕНЬ СВАРНЫХ ШВОВ		
№	DN	ТИП
1	300	BUTTWELD
2	1200	BUTTWELD
3	1200	BUTTWELD
4	1200	BUTTWELD
5	1200	BUTTWELD

Трубопровод	ДАННЫЕ ПО ТРУБОПРОВОДУ		
1200-GT-63CS00-HH-D12001	Расчетные параметры	Температура	-26,9...+85 °C
		Давление	6,3 MPa
	Рабочие параметры	Температура	-20...+60 °C
		Давление	5,5 MPa
Ссылочные чертежи No	Параметры испытания	Тип	Гидравлическое
EWE0426-MGL1-PRE-054-SCM-610120		Давление	8.25 MPa
	Изоляция	Тип	HH
		Толщина	5 mm
	Катодная защита	Да или Нет	Да

Рев.	Дата	Назначение ревизии	Проверил	Утвердил
R1	25.08.2026	Выпущено для рассмотрения		

ЗАКАЗЧИК: UTG ЦЕНТРАЛЬНАЯ АЗИЯ

ГЕНЕРАЛЬНЫЙ ПОДРЯДЧИК: UET

ПОДРЯДЧИК: PBG Pre Build Generation

ГЕНЕРАЛЬНЫЙ ПРОЕКТИРОВЩИК: EAST WEST ENGINEERING

Изм.	Кол.уч.	Лист	№док.	Подпись	Дата
ГИП		Схабицкий А.			08.2026
Нач.отд.		Рябинин А.			08.2026
Исполн.		Халилов Ж.			08.2026
Н.контр		Схабицкий А.			08.2026

EWE0426-MGL1-PRE-054-ISO-800702-R1

«СТРОИТЕЛЬСТВО НОВЫХ НИТОК (УЧАСТКОВ) ГАЗОПРОВОДОВ «ГАЗЛИ - САРИМОЙ» И «АКЧАЛОК - ГАЗЛИ - НУКУС» ОБЩЕЙ ПРОТЯЖЕННОСТЬЮ НЕ МЕНЕЕ 275 КМ».

ГАЗОПРОВОД «ГАЗЛИ-САРИМОЙ» (54 КМ)
Узел замера расхода газа УЗРГ-D12-001

Стадия	Лист	Листов
РД	3	4

Изометрический чертеж трубопровода
1200-GT-63CS00-HH-D12001

EAST WEST ENGINEERING


ООО "EAST-WEST Engineering"
г. Ташкент 2026г.

Взам. инв. №

Подпись и дата

Инв.№ подл.

Формат А2 594x420

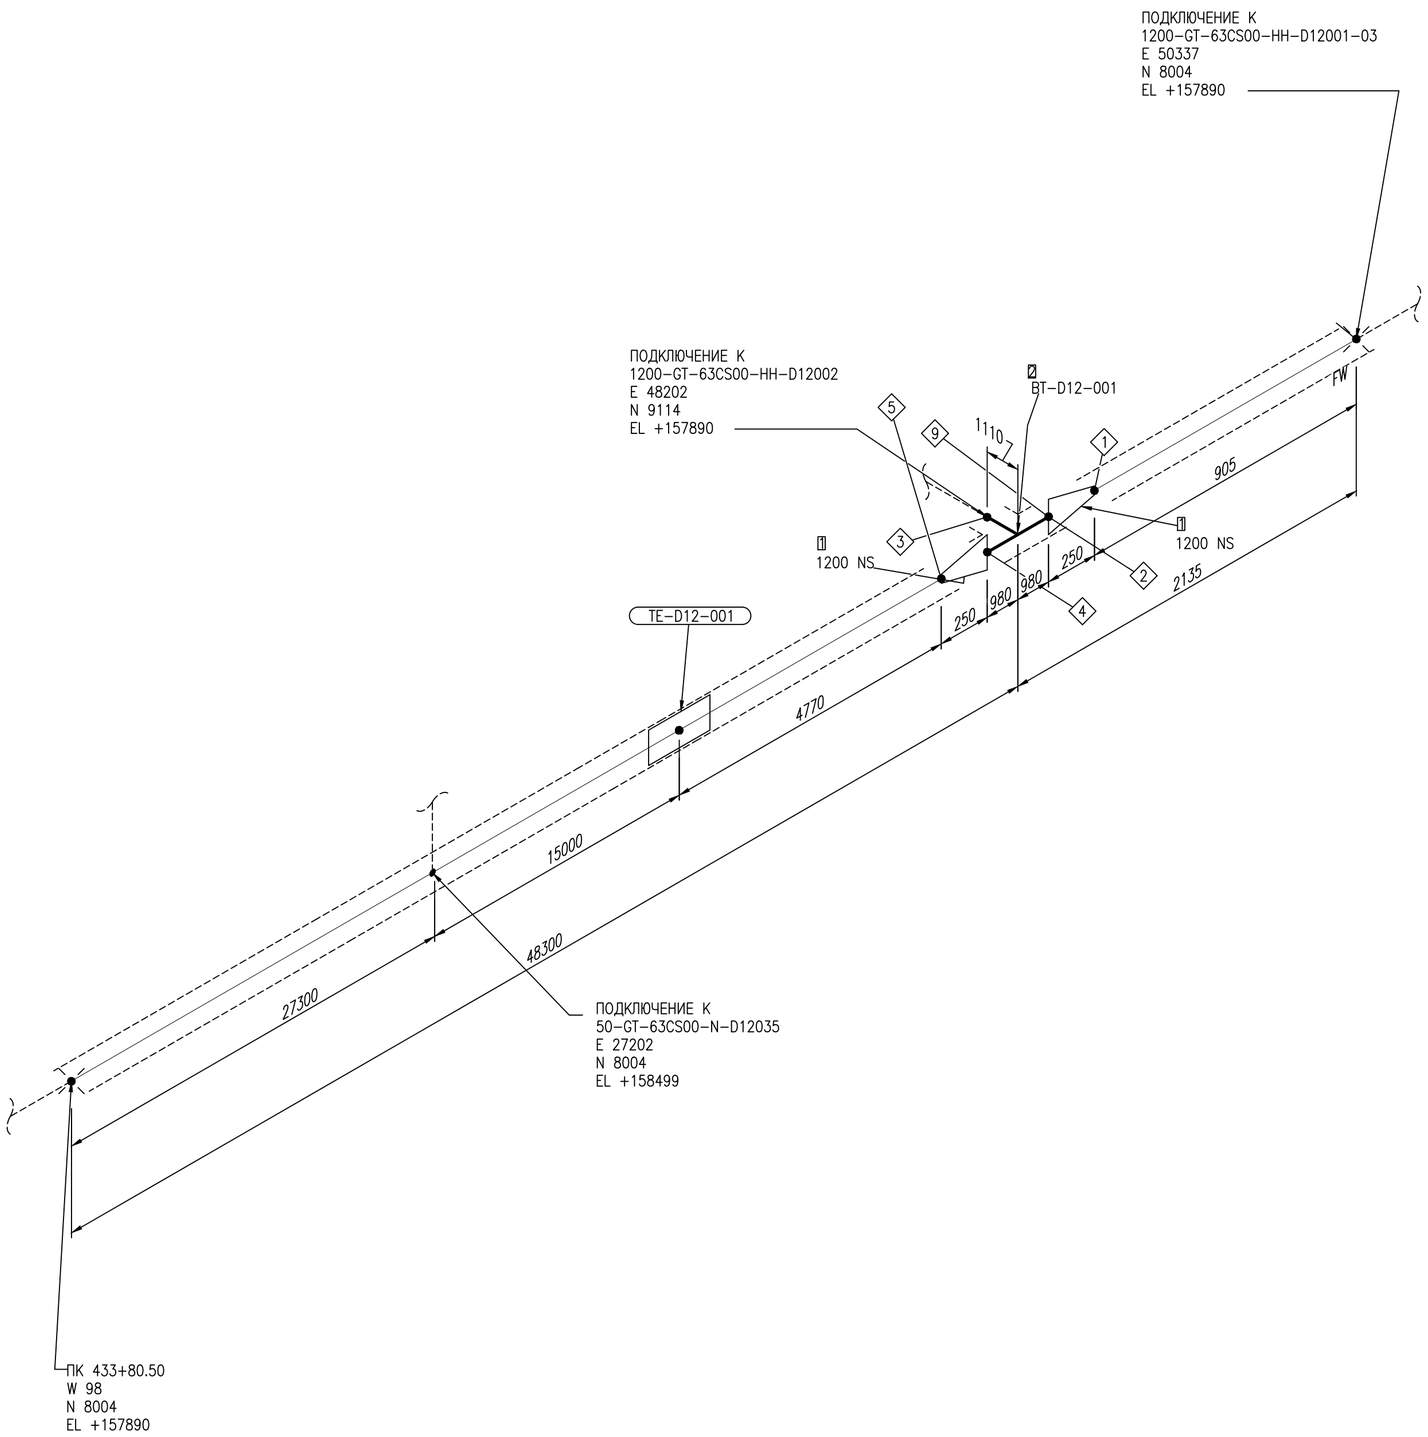

СПЕЦИФИКАЦИЯ ИЗДЕЛИЙ И МАТЕРИАЛОВ				
ПОЗ.	НАИМЕНОВАНИЕ	СТАНДАРТ	КОЛ.	ПРИМЕЧАНИЕ
	ФИТИНГИ			
1	Кольцо КП I 1220(17K60×12K60)-5,5(8,25)-B-30, сталь K60	ТУ 1469-017-38948552-2015	2	
2	Тройник ТР I 1220(17K60)-5,5(8,25)-0,6-30, сталь K60	ТУ 1469-017-38948552-2015	1	

Трубопровод	ДАННЫЕ ПО ТРУБОПРОВОДУ		
1200-GT-63CS00-HH-D12001	Расчетные параметры	Температура	-26,9...+85 °C
		Давление	6,3 MPa
	Рабочие параметры	Температура	-20...+60 °C
		Давление	5,5 MPa
	Параметры испытания	Тип	Гидравлическое
Ссылочные чертежи No		Давление	8.25 MPa
EWE0426-MGL1-PRE-054-SCM-610120	Изоляция	Тип	HH
		Толщина	5 mm
	Катодная защита	Да или Нет	Да

Рев.	Дата	Назначение ревизии	Проверил	Утвердил
R1	25.08.2026	Выпущено для рассмотрения		

ПЕРЕЧЕНЬ СВАРНЫХ ШВОВ		
№	DN	ТИП
1	1200	BUTTWELD
2	1200	BUTTWELD
3	1200	BUTTWELD
4	1200	BUTTWELD
5	1200	BUTTWELD

ЗАКАЗЧИК: UTG ГЕНЕРАЛЬНЫЙ ПОДРЯДЧИК: UET ПОДРЯДЧИК: PBG ГЕНЕРАЛЬНЫЙ ПРОЕКТИРОВЩИК: EAST WEST ENGINEERING

Изм.	Кол.уч.	Лист	№док.	Подпись	Дата	
ГИП		Схабицкий А.			08.2026	EWE0426-MGL1-PRE-054-ISO-800702-R1
Нач.отд.		Рябинин А.			08.2026	«СТРОИТЕЛЬСТВО НОВЫХ НИТОК (УЧАСТКОВ) ГАЗОПРОВОДОВ «ГАЗЛИ - САРИМОЙ» И «АКЧАЛОК - ГАЗЛИ - НУКУС» ОБЩЕЙ ПРОТЯЖЕННОСТЬЮ НЕ МЕНЕЕ 275 КМ».
Исполн.		Халилов Ж.			08.2026	ГАЗОПРОВОД «ГАЗЛИ-САРИМОЙ» (54 КМ) Узел замера расхода газа УЗРГ-D12-001
						Стадия: РД; Лист: 4; Листов: 4
Н.контр		Схабицкий А.			08.2026	Изометрический чертеж трубопровода 1200-GT-63CS00-HH-D12001
						ООО "EAST-WEST Engineering" г. Ташкент 2026г.

Взам. инв. № | Подпись и дата | Инв.№ подл.