N СЕВЕР

СПЕЦИФИКАЦИЯ ИЗДЕЛИЙ И МАТЕРИАЛОВ

ПОЗ.	НАИМЕНОВАНИЕ	СТАНДАРТ	КОЛ.	ПРИМЕЧАНИЕ
	ТРУБЫ			
1	Труба 3–1220x16–K60	ГОСТ 31447–2012	34.3М	
	ФИТИНГИ			
2	Отвод ОК I 90–1220(17K60)–5,5(8,25)–0,6–1,5Dн–30, сталь K60	ТУ 1469–017–38948552–2015	2	
	АРМАТУРА			
3	Кран шаровой DN1200 PN–6,3 МПа с пневмогидроприводом, приварной, подземный	EWE0426–MGL1–PRE–054–DSH–610134	1	

ПЕРЕЧЕНЬ СВАРНЫХ ШВОВ

№	DN	ТИП
1	1200	FIELDWELD
2	1200	BUTTWELD
3	1200	BUTTWELD
4	1200	FIELDWELD
5	1200	FIELDWELD
6	1200	BUTTWELD
7	1200	BUTTWELD
8	1200	BUTTWELD
9	1200	BUTTWELD
10	1200	FIELDWELD
11	50	TAPWELD

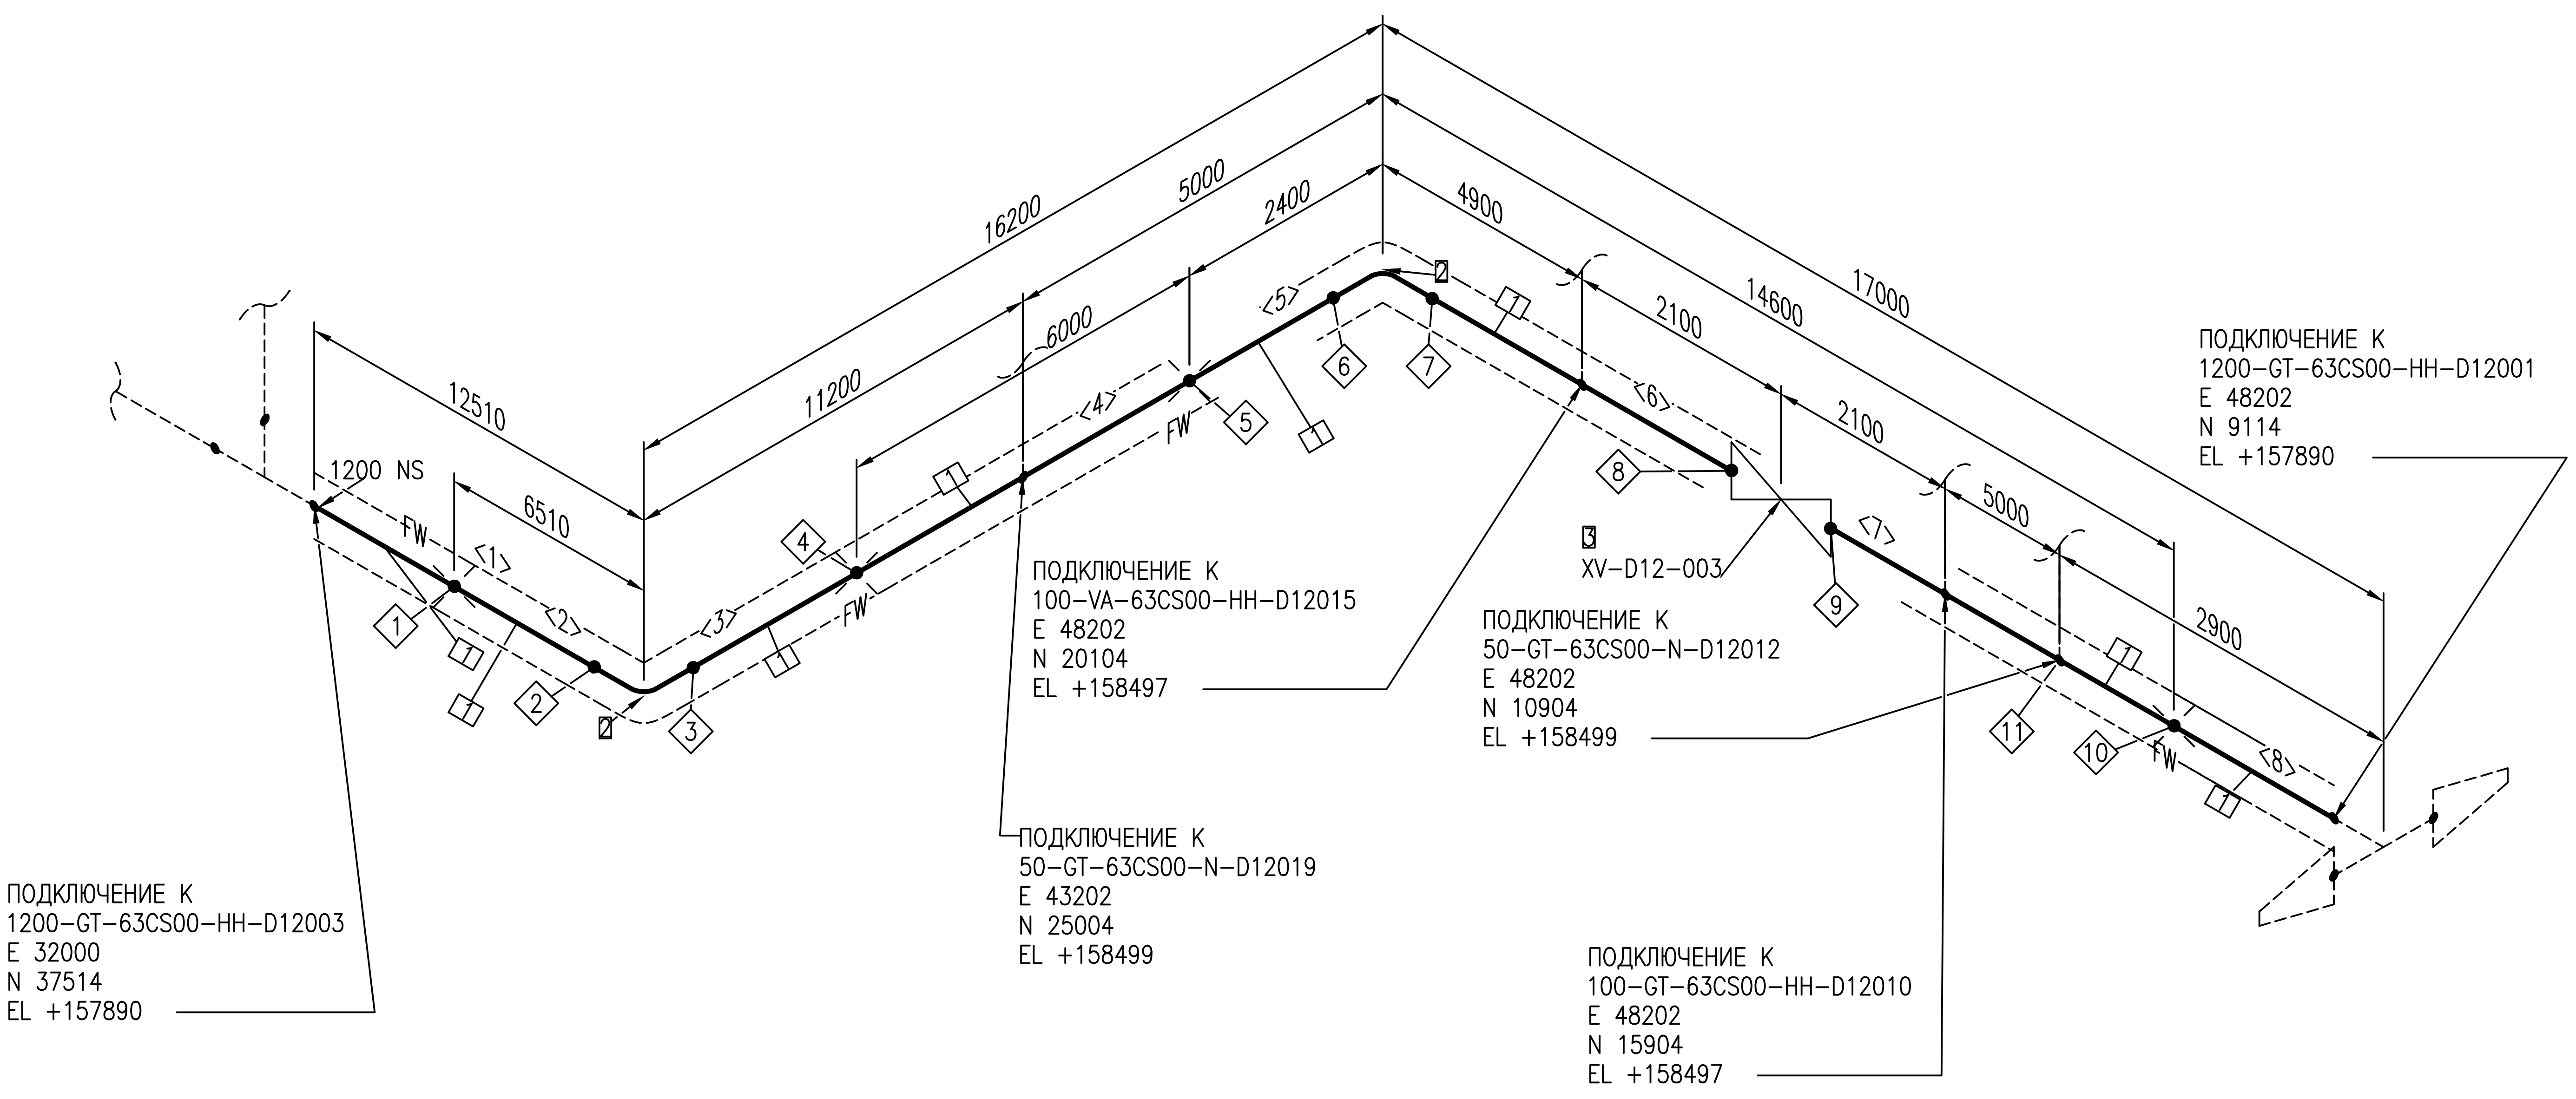

ПЕРЕЧЕНЬ ТРУБНЫХ КАТУШЕК

№	DN	ДЛИНА
1	1200	6000ММ
2	1200	4711ММ
3	1200	6000ММ
4	1200	6000ММ
5	1200	601ММ
6	1200	3601ММ
7	1200	6000ММ
8	1200	1291ММ

Трубопровод	ДАННЫЕ ПО ТРУБОПРОВОДУ		
1200–GT–63CS00–HH–D12002	Расчетные параметры	Температура	–26,9…+85 °C
		Давление	6,3 MPa
	Рабочие параметры	Температура	–20…+60 °C
		Давление	5,5 MPa
	Параметры испытания	Тип	Гидравличское
Ссылочные чертежи No		Давление	8.25 MPa
EWE0426–MGL1–PRE–054–SCM–610120	Изоляция	Тип	HH
		Толщина	5 mm
	Катодная защита	Да или Нет	Да

Рев.	Дата	Назначение ревизии	Проверил	Утвердил
R1	25.08.2026	Выпущено для рассмотрения		

ЗАКАЗЧИК: UTG UZTRANSGAZ
ГЕНЕРАЛЬНЫЙ ПОДРЯДЧИК: UET UZBEKENERGOTAMIR
ПОДРЯДЧИК: PBG Pro Build Generation
ГЕНЕРАЛЬНЫЙ ПРОЕКТИРОВЩИК: EAST WEST ENGINEERING

EWE0426–MGL1–PRE–054–ISO–800703–R1

«СТРОИТЕЛЬСТВО НОВЫХ НИТОК (УЧАСТКОВ) ГАЗОПРОВОДОВ «ГАЗЛИ – САРИМОЙ» И «АКЧАЛОК – ГАЗЛИ – НУКУС» ОБЩЕЙ ПРОТЯЖЕННОСТЬЮ НЕ МЕНЕЕ 275 КМ».

Изм.	Кол.уч.	Лист	№док.	Подпись	Дата
ГИП		Схабицкий А.			08.2026
Нач.отд.		Рябинин А.			08.2026
Исполн.		Халилов Ж.			08.2026
Н.контр		Схабицкий А.			08.2026

ГАЗОПРОВОД «ГАЗЛИ–САРИМОЙ» (54 КМ)
Узел замера расхода газа УЗРГ–D12–001

Стадия	Лист	Листов
РД	1	1

Изометрический чертеж трубопровода
1200–GT–63CS00–HH–D12002

ООО "EAST–WEST Engineering"
г. Ташкент 2026г.

Взам. инв. №
Подпись и дата
Инв.№ подл.

Формат А2 594x420